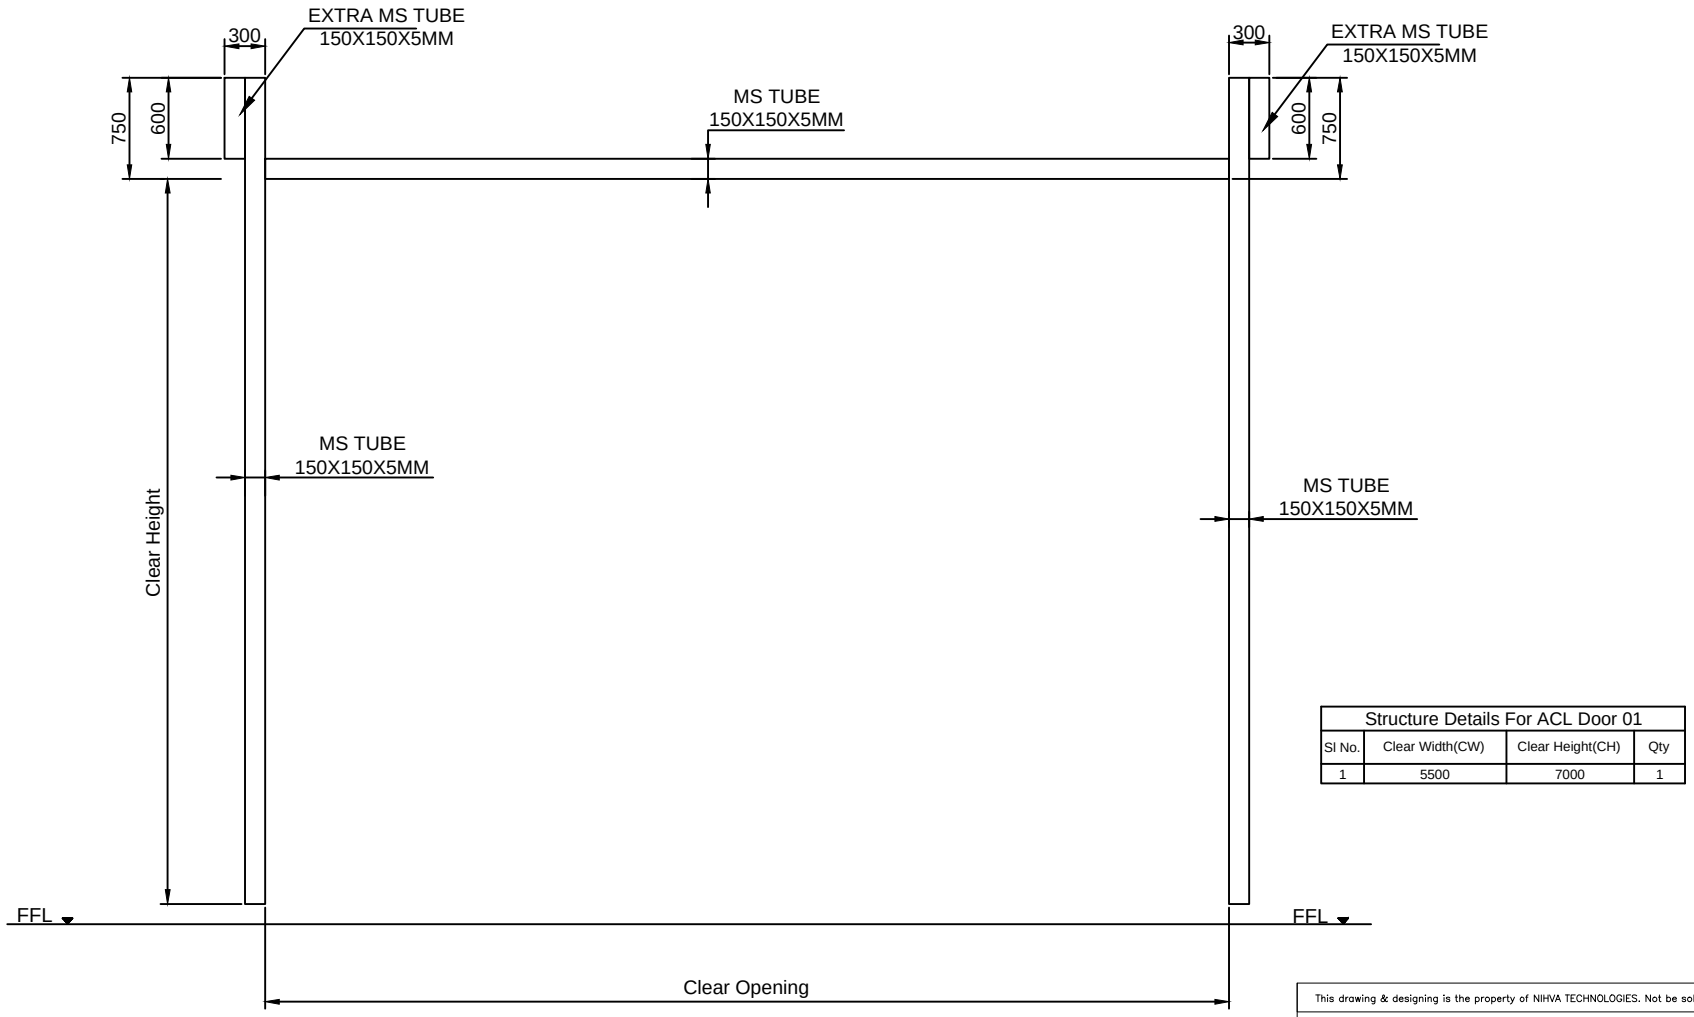

Structure Details For ACL Door 01			
Sl No.	Clear Width(CW)	Clear Height(CH)	Qty
1	5500	7000	1

Note:-

1.All dimensions are in MM

2.All Civil work and required MS Structure support will be in client scope

Rev.No	Revision	Date	Revised By

This drawing & designing is the property of NIHVA TECHNOLOGIES. Not be sold or copy to any other concern.

NIHVA TECHNOLOGIES PVT. LTD.

NIHVA TECHNOLOGY PVT. LTD. PUNE
Tel : 020 66304033
Email:- info@nihva.com
Website:- www.nihva.com

ROLLING SHUTTER STRUCTURE

	NAME	DATE
DRAWN.BY	KISHAN	10/08/2022
CHECK.BY	M.SUTAR	10/08/2022
APPRD.BY	A.KURHADE	10/08/2022

CLIENT - RONAK BUIDWELL PVT. LTD.

PROJECT - ROLLING SHUTTER STRUCTURE

SITE -

DWG. NO. - NIHVA/22-23/CLT/0106 | REV.01

SCALE: 01 | WT: | SHEET: 01 OF 01

If any queries contact : design@nihva.com