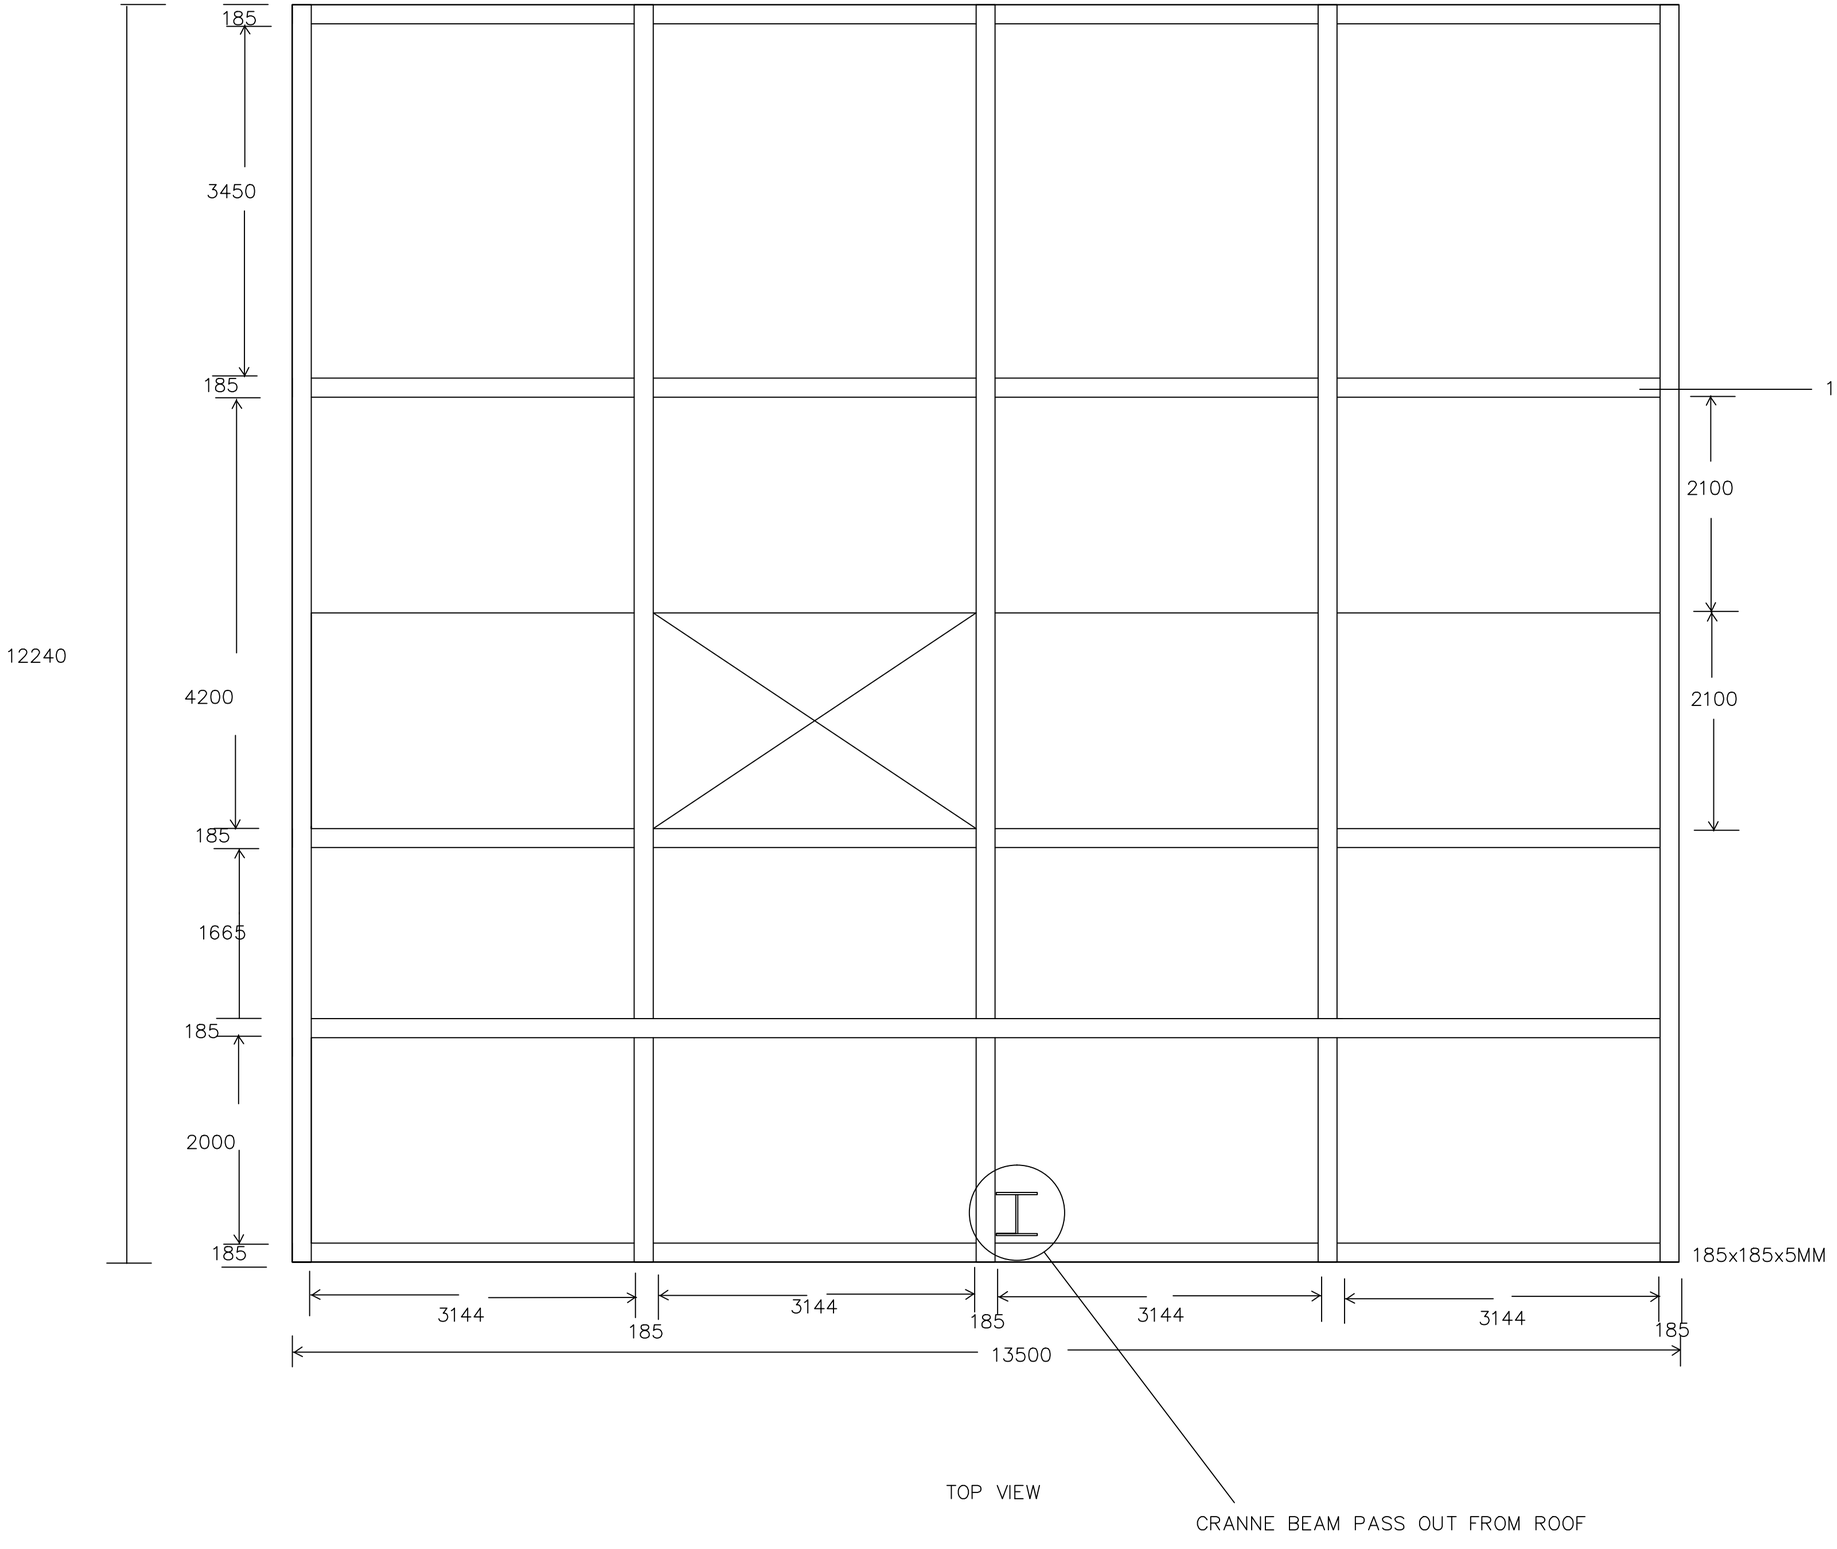
185
3450
185
4200
185
1665
185
2000
185
12240
185MM
2100
2100
T. ANGALE
100x100x8MM
185x185x5MM
3144
185
3144
185
3144
3144
185
13500
TOP VIEW
CRANNE BEAM PASS OUT FROM ROOF