


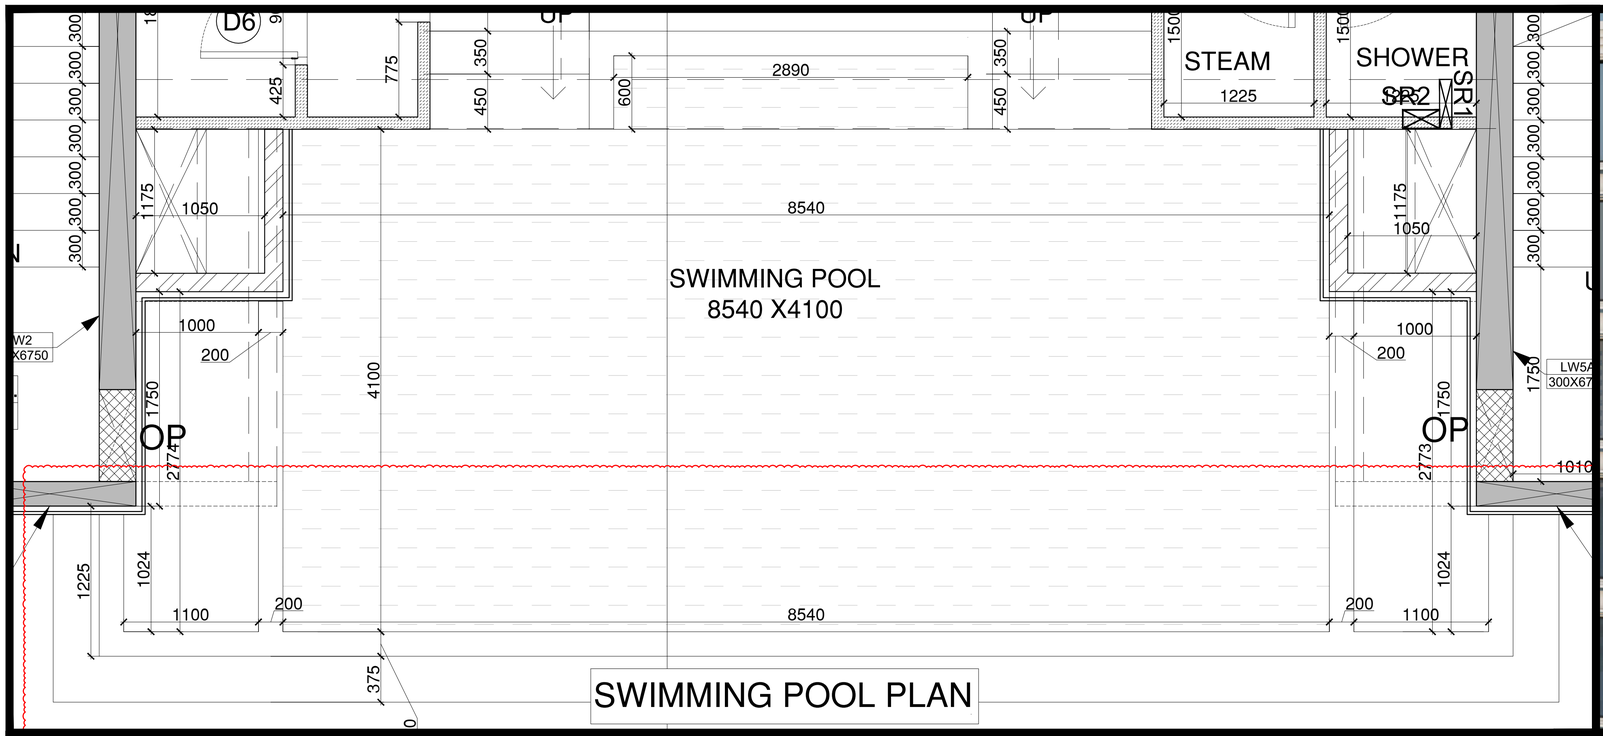


NOTE:

. Use of this drawing for construction shall explicitly confirm acceptance of following conditions :

1. All General Notes as per sheet G01(General Information & Index Sheet) are applicable to this drawing sheet.
2. Do not Scale Drawings. Dimensions govern.
3. All dimensions are in millimeters unless noted otherwise.
4. All dimensions are from unfinished to unfinished levels unless otherwise specified.
5. In case of discrepancies larger scale detailed drawings shall supersede smaller scale drawings.
6. Any discrepancy in between Plan, Elevation, Section shall be immediately brought to Architects notice prior to construction on site.
7. Any discrepancy between Architecture, Structure, MEPF, Facade,other drawings shall be immediately brought to Architects notice prior to construction on site.
8. Any irregularities in construction which occurs as a result discrepancy between Architecture, Structure, MEP, others drawings which have not been brought to the Architects notice prior to execution shall become the responsibility of the Contractor.
9. All services (MEPF) drawings are to be referred only for technical content , only coordinated working drawings to be followed for all work at site.
10. All structural sizes and details to be referred from drawings schedules given by structural consultants. However profile coordinates to be strictly as per architectural drawings.
11. All Floor Levels are Unfinished floor level (SSL) unless otherwise specified.
12. Supervision if specifically asked would be provided but responsibility regarding correct & sound construction shall solely rest with contractor/builder.
13. All relevant samples to be approved by architect prior to procurement.
14. No Shell plan/Shop drawings/Formwork drawing/s issued by any agency is valid for construction unless stamped and signed by architect along with comments if any.
15. All open spaces between proposed Built Structures to site / plot boundaries OR Open spaces between built structures shall be cross-verified with the municipal approved drawing at site prior to commencement of construction.
16. Any discrepancy between the VFC drawings and the municipal approved drawings must be immediately brought to notice of the Architect prior to execution.

KEY PLAN SCALE:- 1:750

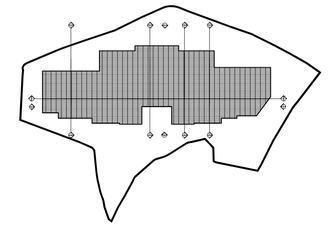


PROJECT NAME


PROPOSED RESIDENTIAL BUILDING ON PLOT BEARING CTS.NO.1395,1396 & 1397 , N. D. ROAD, PALI HILL , AT VILLAGE - BANDRA (W)

RIVISION


DATE:	REMARK:
30/09/2023	R0 (AGFC)

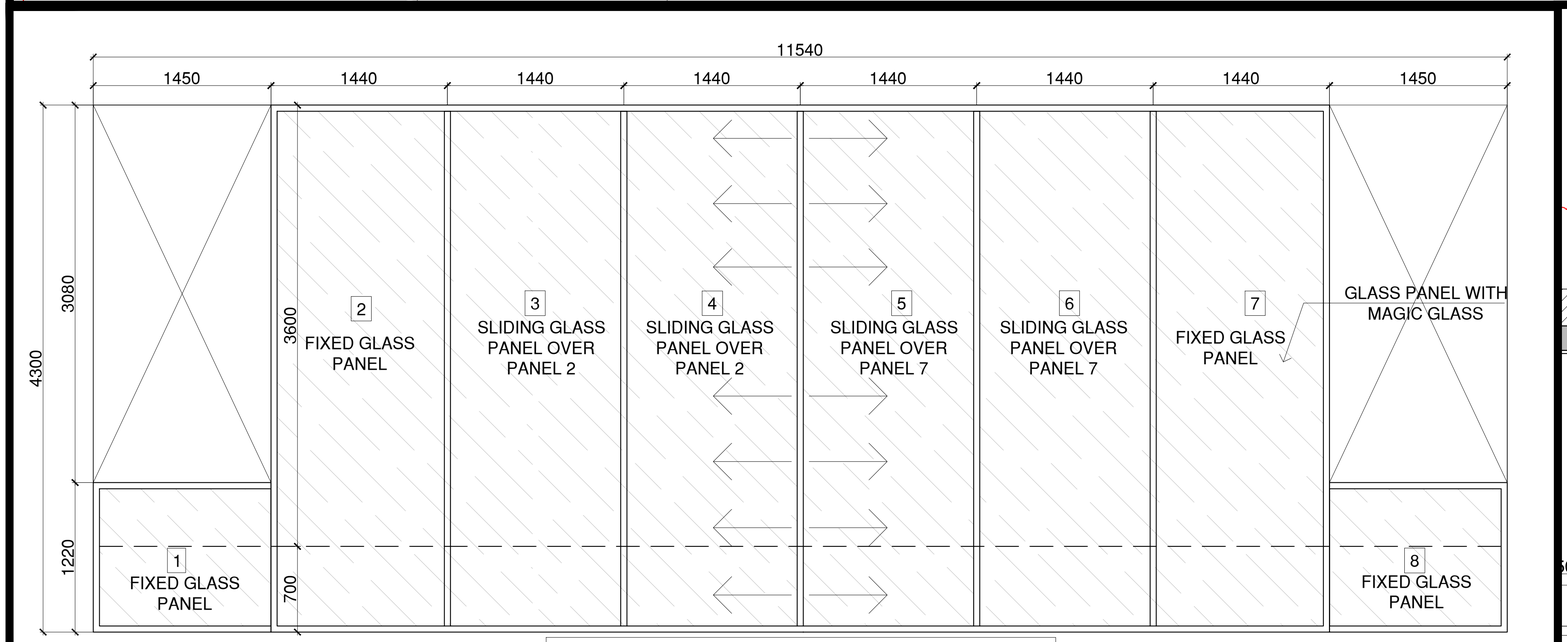

RETRACTABLE ROOF PLAN

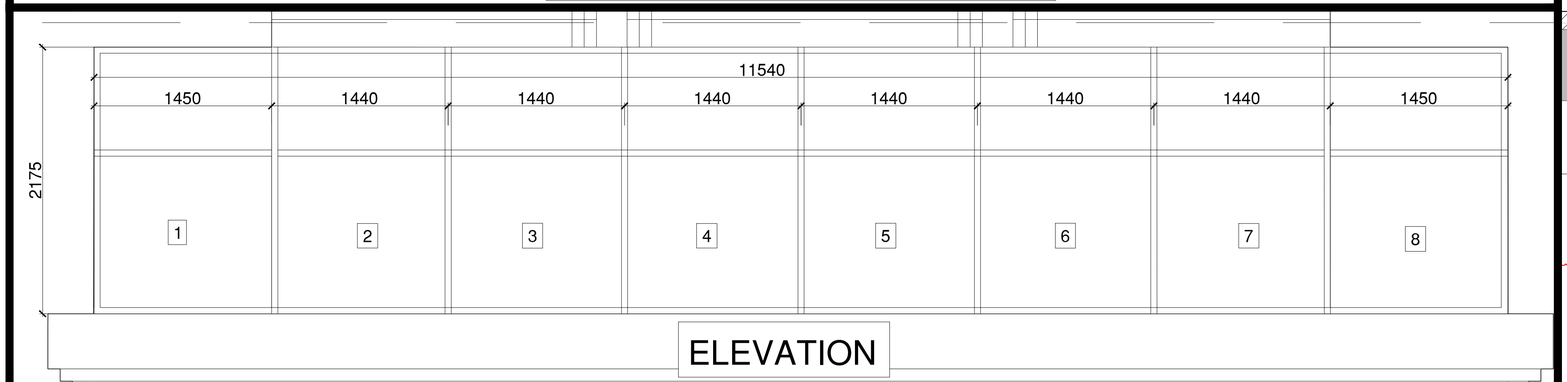

ELEVATION

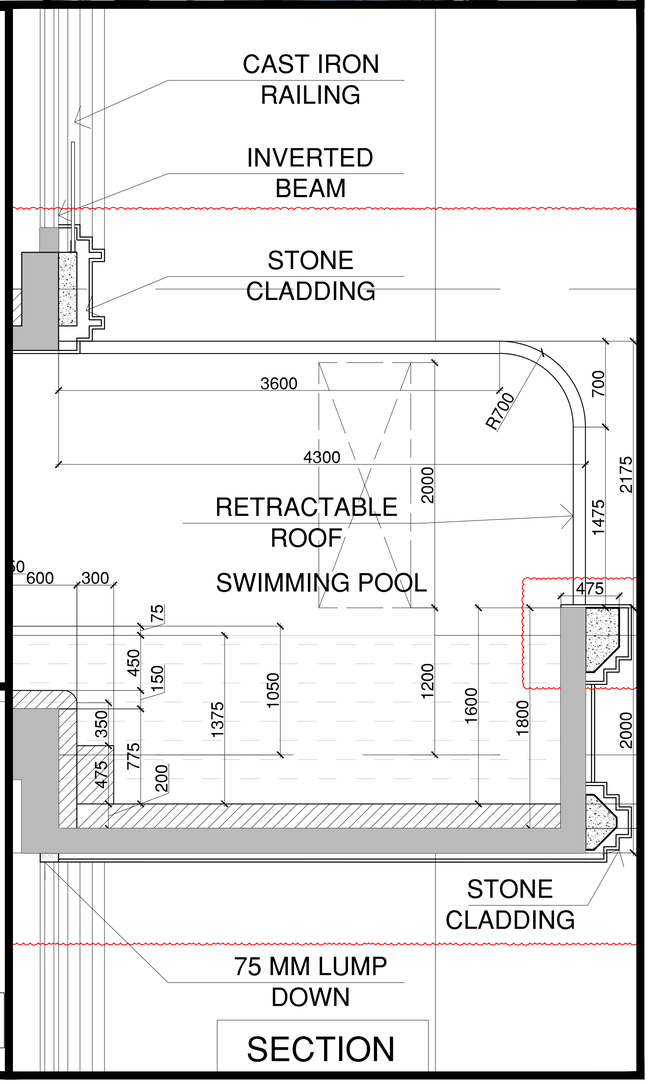

SECTION

CLIENT

ASHAR PROMISES DELIVERED

Ashar IT Park Jayshri Baug, Road No.16 Z Wagle Estate B Wing 11th Floor, Thane(West) -4000604

PRINCIPAL ARCHITECT

ATELIER Design Consultants Pvt Ltd

C2, 705, Skyline Wealth Spaces, 7th Floor, Premier Road, Ghatkopar (W), Mumbai - 400086.
Email : kmadesigns99@gmail.com

STRUCTURAL CONSULTANT

JW CONSULTANTS LLP

Sai Radhe, Office No 201 , 2nd Floor Behind Hotel Sheraton Grand 100-101 Kennedy Road Pune, Maharashtra - 411001 India.

MEP CONSULTANT ENGINEERS

301, Sangam S V Road , Santacruz West, Mumbai - 400054

DRAWING TITLE:-	NORTH:-
RETRACTABLE ROOF OVER SWIMMING POOL	
STATUS:- AGFC	
DRAWING NO.:- A-DK-404	REVISION:- R0
SHEET SIZE:- A1	SCALE :- 1:25

DRAWN BY :	CHECKED :	DATE :
Ar. Ruhcir J	Ar. Piyush K	30/09/2023