


DWG.NO: SALT_1729_GA_01_R0

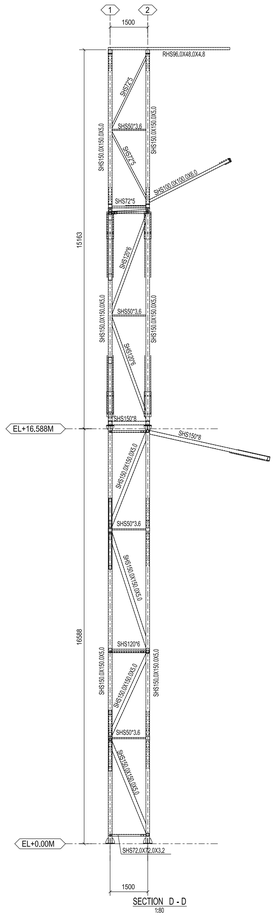


SECTION D - D
1:80

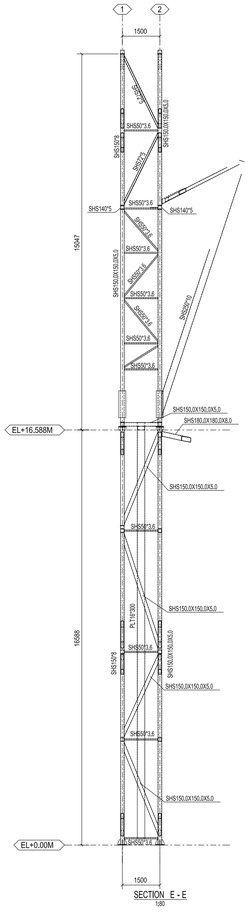


SECTION E - E
1:80

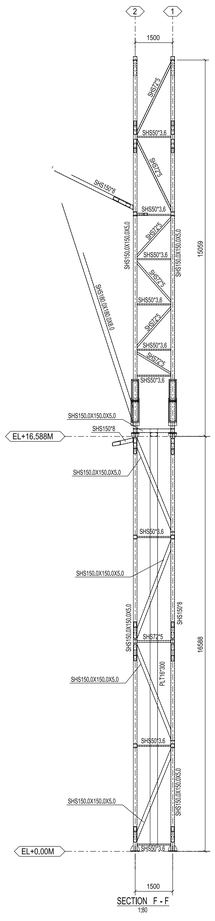


SECTION F - F
1:80

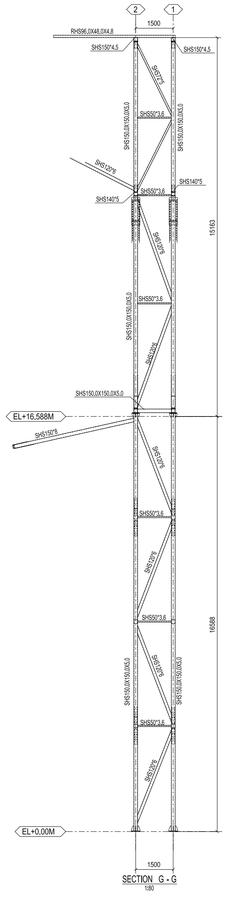


SECTION G - G
1:80

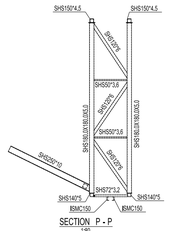


SECTION P - P
1:80

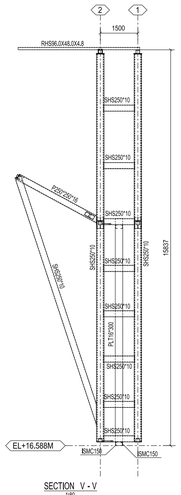


SECTION V - V
1:80

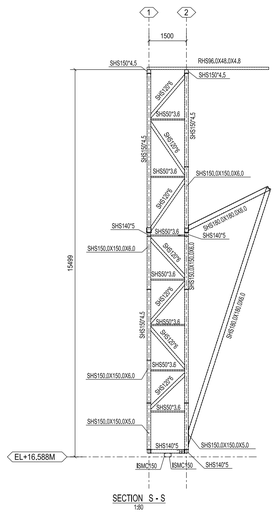


SECTION S - S
1:80

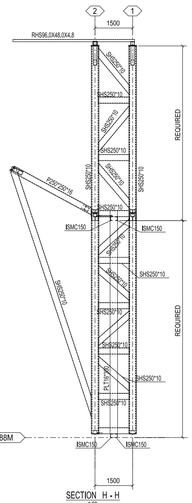


SECTION H - H
1:80

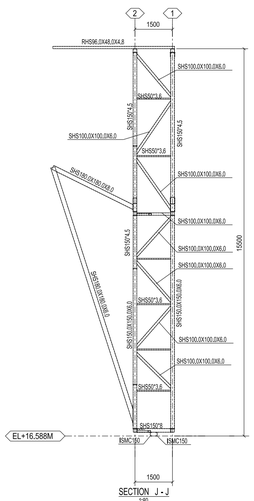


SECTION J - J
1:80

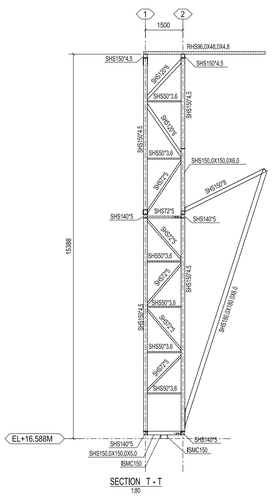


SECTION T - T
1:80

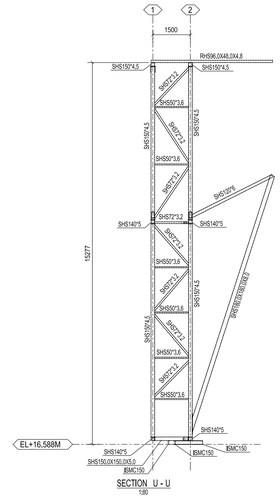


SECTION U - U
1:80

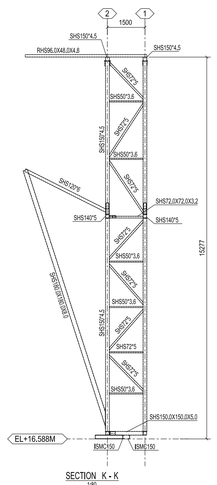


SECTION K - K
1:80

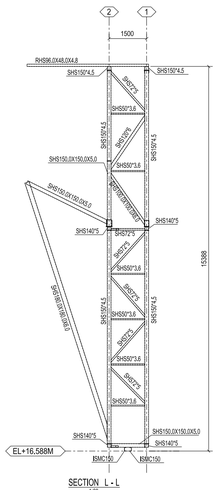


SECTION L - L
1:80

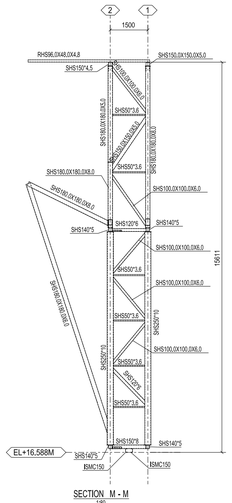


SECTION M - M
1:80

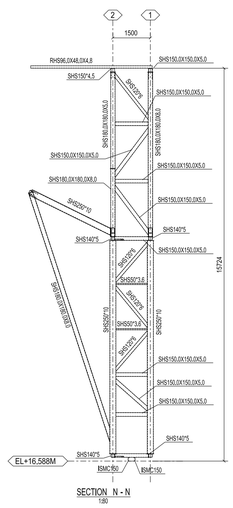

SECTION N - N
1:80

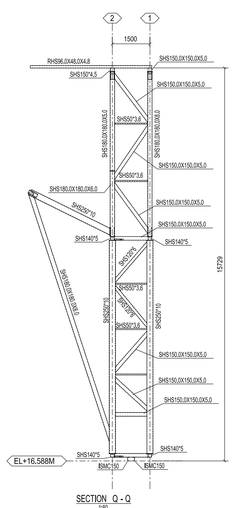

SECTION Q - Q
1:80

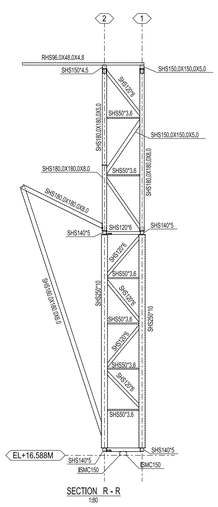

SECTION R - R
1:80

REV.NO.	DESCRIPTION.	REV.DATE	DRAWN.	CHKD.	APPD.
0	GA DRAWING FOR APPROVAL	05.11.22	MEGHA	HAB	HAB

DWG.TITLE :- GA DRAWING FOR DOOR FRAME(84M)

PROJECT	MEGADOOR INSTALLATION AT HYDRABAD AIRPORT
CLIENT	GMR

SALT Design Services
NIHVA TECHNOLOGIES PVT LTD

SALT DESIGN SERVICES

NIHVA TECHNOLOGIES PVT. LTD. PUNE
Tel : 020 66304033
Email:- info@nihva.com
Website:- www.nihva.com

DRAWN :RRK	CHECKED : HAB	SCALE: 1:100
APPROVED : HAB	JOB CODE. : 1729	DATE: 05.11.2022
DWG.NO: SALT_1729_GA_01_R0	(SH-2OF3)	REV. - R0 SIZE. - A0

A1 [841 x 594]