MATERIAL:-G.I

DOOR HANDLING:

SINGLE DOOR ???? HAND ACTIVE

INFILL: HONEY COMB

RAL NO FRAME:-

RAL NO LEAF:-

PANIC BAR :
MODEL NO.- LOCKWOOD MAKE
PE RM501P
PHT LOCK :
MODEL NO. LOCKWOOD MAKE
PE ACC004

DOOR CLOSER : STD ARM - MODEL NO-YADC 6003 -YALE MAKE

ACCESSORIES:-

1.SS BALL BEARING HINGES
3S2BB403030-CE-M =YALE MAKE


2.SMOKE SEAL-S88BL-PEMKO MAKE

FRAME SHEET THIK.1.2mm


LEAF SHEET THIK.0.8 mm

POWDER COATED METAL CAP WITH RAL


2 HRS FIRE RATED

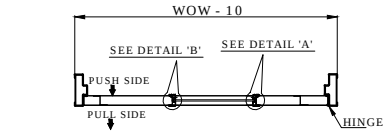

TOP VIEW

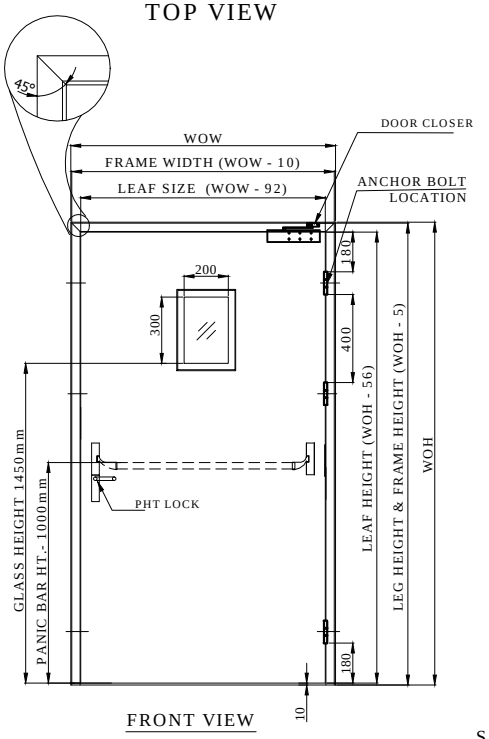


FRONT VIEW

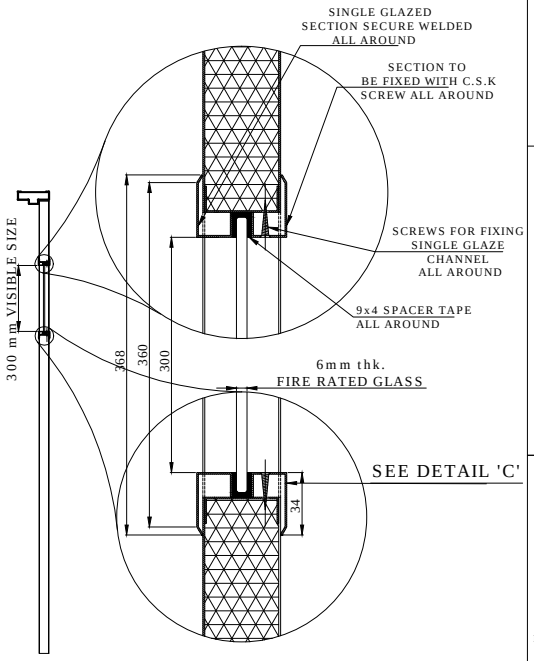


SIDE VIEW
SECTION A-A'

SINGLE GLAZE FIXING DETAIL

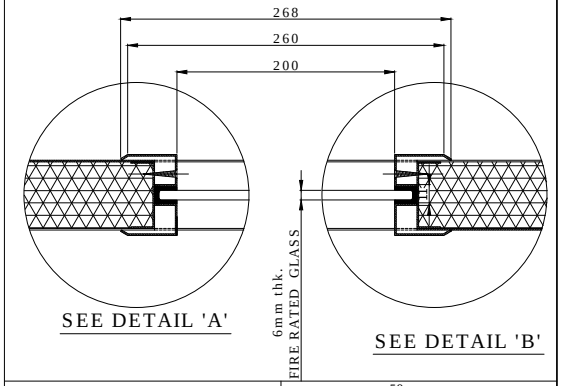



SEE DETAIL 'A'

SEE DETAIL 'B'

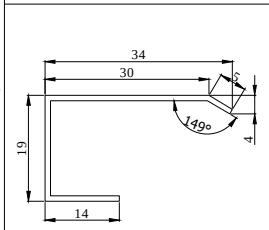


SEE DETAIL 'C'

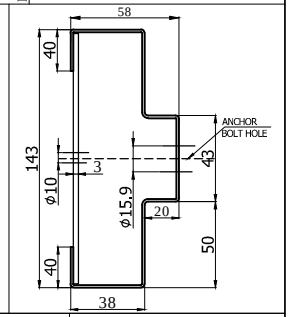

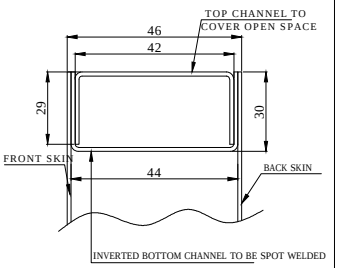

DOOR TOP SECTION DETAIL

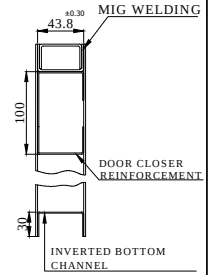

DOOR BOTTOM & TOP DETAIL

SR. NO	WALL OPENING WIDTH	WALL OPENING HEIGHT	QTY	RAL	LOCATION	HARDWARE
08	900	1800	02	3020	Admin Building (IH) - Fire Shaft	Single leaf Metal door with vision panel
07	900	2375	01	9002	Block G - Security cabin - white colour	Single leaf metal door with Vision Panel, Hinges , Door closer , Single point panic bar, with external trim
06	900	2380	01	9002	Block G - Security cabin - white colour	Single leaf metal door with Vision Panel, Hinges , Door closer , Single point panic bar, with external trim
05	1200	2400	01	3020	Block B - First floor	Single leaf metal door with vision panel, Hinges , Door closer , Single point panic bar with external trim
04	1200	2100	01	9002	Block B - Metering Kiosk (GD6B)	Hinges , Door closer , Single point panic bar , Non-Fire rated Glass 300X300mm
03	1200	2100	01	9002	Block D - Metering Kiosk (GD6B)	Hinges , Door closer , Single point panic bar , Non-Fire rated Glass 300X300mm
02	1200	2100	01	9002	Block C - Metering Kiosk (GD6B)	Hinges , Door closer , Single point panic bar , Non-Fire rated Glass 300X300mm
01	1200	2100	01	9002	RMU 2 (GD6B)	Hinges , Door closer , Single point panic bar , Non-Fire rated Glass 300X300mm

TOLERANCE - ±05mm

REV. NO	DATE	DRAWN	REMARK
R01	18.03.19	P.V.A	1.SPECIFICATION CHANGE

This drawing & design is the property of NIHVA TECHNOLOGIES. Not to be sold or copied to any other concern.

TITLE: FIRE RATED SINGLE LEAF STEEL DOOR

NIHVA TECHNOLOGIES PVT. LTD.

NIHVA TECHNOLOGIES PVT. LTD. PUNE
Tel : 020 66304033
Email:- info@nihva.com
Website:- www.nihva.com

	NAME	SIGN	DATE
DRAWN	P.V.A		16.03.2019
CHECK	V.M.T		16.03.2019
APPRD.			

If any queries contact : design@nihva.com

ALL DIMENSION ARE IN mm

CLIENT - SYNERGY

PROJECT - EMBASSY

SITE LOCATION - CHAKAN, PUNE.

DWG. NO. : NIHVA/18-19/0291/R01 | REV- R01

SCALE: NTS | WT: | SHEET: 01 OF 01