
BSW

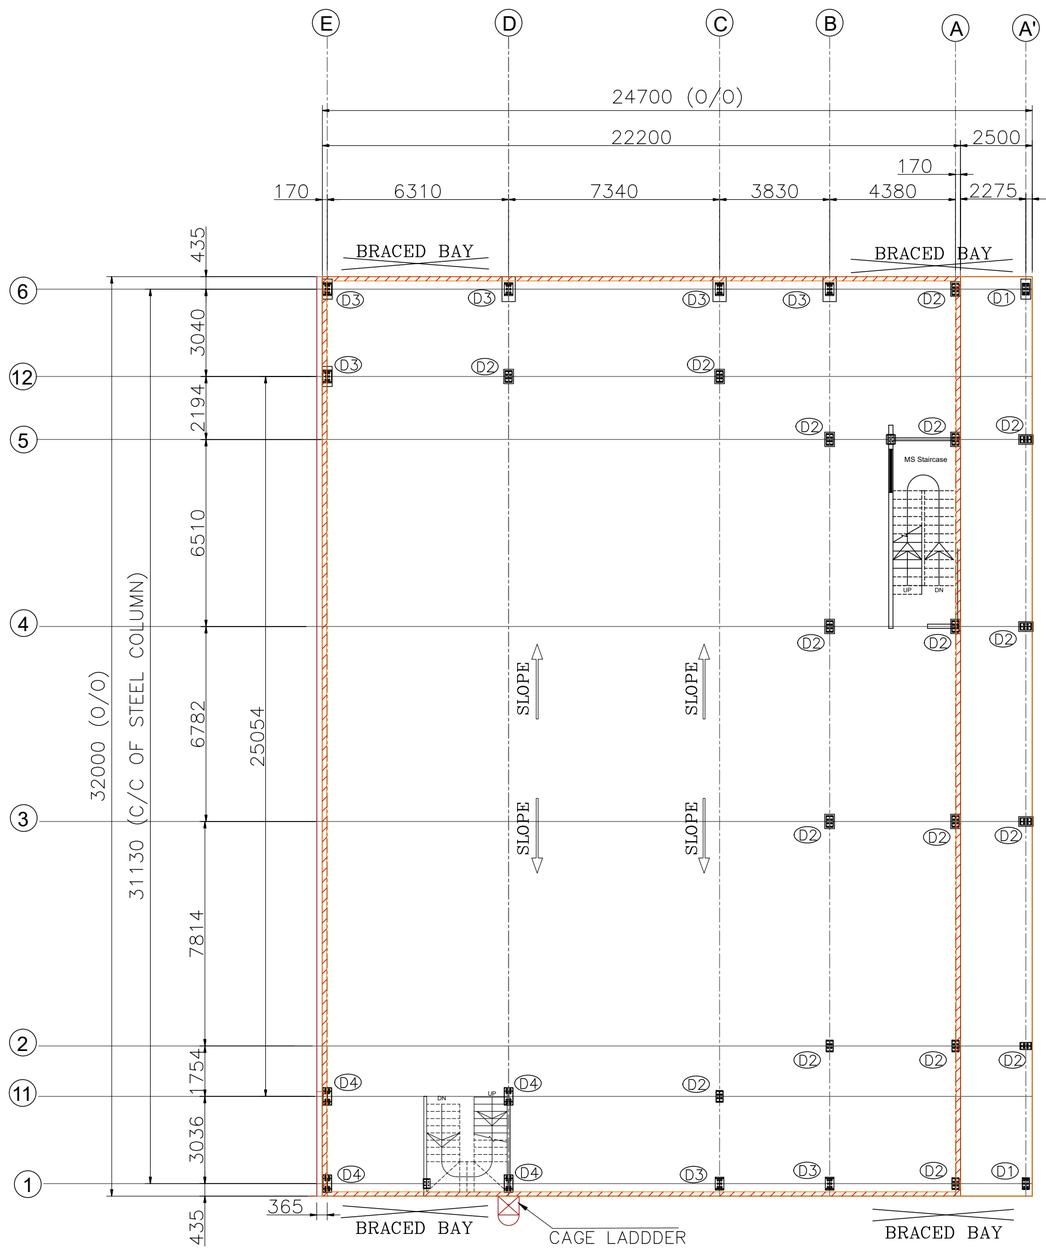

LEW

REW

FSW

ANCHOR BOLT PLAN

FFL ±0.000M

NOTES:-

1. ALL DIMENSIONS ARE IN MILLIMETERS AND LEVELS ARE IN METERS UNLESS NOTED OTHERWISE.
2. NO DIMENSION SHALL BE SCALED OFF, ONLY WRITTEN DIMENSION SHALL BE FOLLOWED.
3. ALL DIMENSIONS SHALL HAVE TO BE VERIFIED AT SITE PRIOR TO FABRICATION.
4. ALL STRUCTURAL STEEL MEMBER EXCEPT PURLIN AND SIDE RUNNER SHALL CONFORM TO YS 345 OF IS:2062.
5. GRADE OF PURLIN SHALL CONFORM TO YS245
6. ALL WELDING ELECTRODE SHALL CONFORM TO AWS.
7. ALL FILLET & INTERMITTENT WELDS SHALL BE FOLLOWED AS MENTIONED CONFORMING TO AWS.
8. DETAIL OF BOLTS & BOLT HOLES SHALL BE FOLLOWED AS PER ASTM A 325
9. HOLDING DOWN BOLTS SHALL BE OF PROPERTY CLASS 4.6 (GRADE-B) CONFORMING TO IS:1367 P-3 & SHALL BE IN ACCORDANCE WITH IS:1367.
10. WELDING WORK SHALL BE CHECKED FROM TIME TO TIME.
11. FABRICATION WORK SHALL BE AS PER BEST ENGINEERING PRACTICE UNLESS SPECIFIED OTHERWISE.
12. WELDED SURFACE SHALL BE SMOOTH GROUND FOR PROPER CONTACT WITH OTHER MEMEBER/UNITS.

LEGEND:


FSW = FRONT SIDE WALL
BSW = BACK SIDE WALL
LEW = LEFT END WALL
REW = RIGHT END WALL

SWARAJYA STEEL BUILDING
WE BUILD BEST ...


ALL UNITS ARE IN MM & KGS.
DO NOT SCALE THE DRAWING.

REV.	DATE	DESCRIPTION	DSN	DRN	CKD
		ISSUED FOR APPROVAL	AP	PW	AP
00	18-06-2026	ISSUED FOR APPROVAL	AP	PW	AP


PROJECT No.	: SSB-J-2603
ASP JOB No.	: J-285
PROJECT NAME	: JHUNJHUNU AIRPORT
CLIENT NAME	: M/S VS INFRA VENTURES
COMPANY NAME	: AIR GLOBE AVIATION SCHOOL
JOB SITE LOCATION	: MIRA ROAD
ANCHOR BOLT PLAN	DWG. No. AB-01

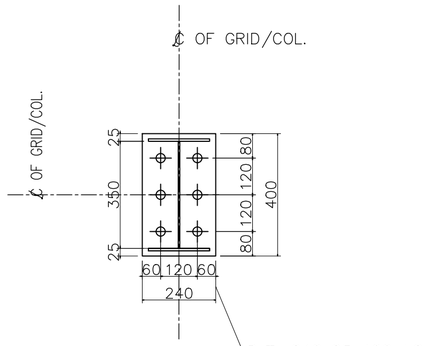


DETAIL D1 (2 No. REQD.) GA-01 (AS DRAWN)

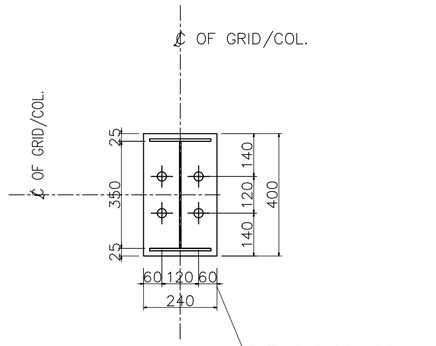


DETAIL D2 (17 No. REQD.) GA-01 (AS DRAWN)

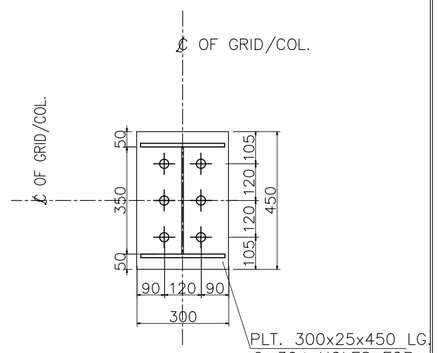


DETAIL D3 (7 No. REQD.) GA-01 (AS DRAWN)

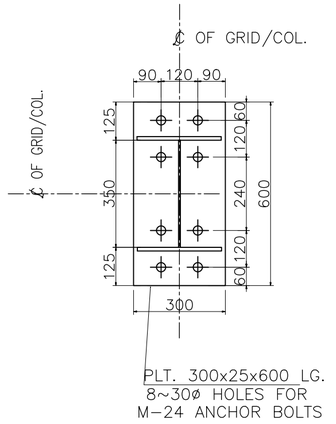


DETAIL D4 (4 No. REQD.) GA-01 (AS DRAWN)

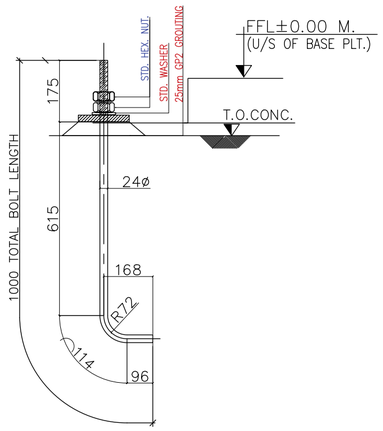


M-24 ANCHOR BOLT DETAIL
(154 Nos. REQD.)

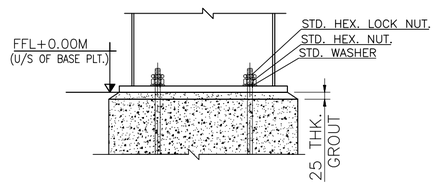

TYPICAL COLUMN BASE DETAIL (U.N.O.)
(DETAIL D2)

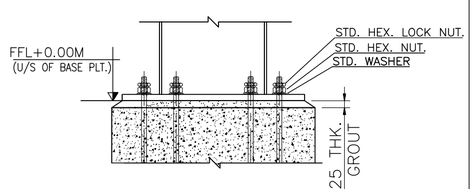

TYPICAL COLUMN BASE DETAIL (U.N.O.)
(DETAIL D4)

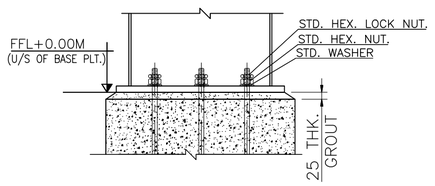

TYPICAL COLUMN BASE DETAIL (U.N.O.)
(DETAIL D1/D3)

PART MARK	QTY.	DISC.	LENGTH	WIDTH	THK.
M 24 AB	154	-	1000	-	-

SWARAJYA STEEL BUILDING
WE BUILD BEST ...


ALL UNITS ARE IN MM & KGS.
DO NOT SCALE THE DRAWING.

REV	DATE	DESCRIPTION			
		ISSUED FOR APPROVAL	AP	PW	AP
00	18-06-2026	ISSUED FOR APPROVAL	AP	PW	AP
REV	DATE	DESCRIPTION	DSN	DRN	CKD

PROJECT No.	: SSB-J-2603
ASP JOB No.	: J-285
PROJECT NAME	: JHUNJHUNU AIRPORT
CLIENT NAME	: M/S VS INFRA VENTURES
COMPANY NAME	: AIR GLOBE AVIATION SCHOOL
JOB SITE LOCATION	: MIRA ROAD
ANCHOR BOLT DETAIL PLAN	DWG. No. AB-02


ANCHOR BOLT DETAIL PLAN

BSW

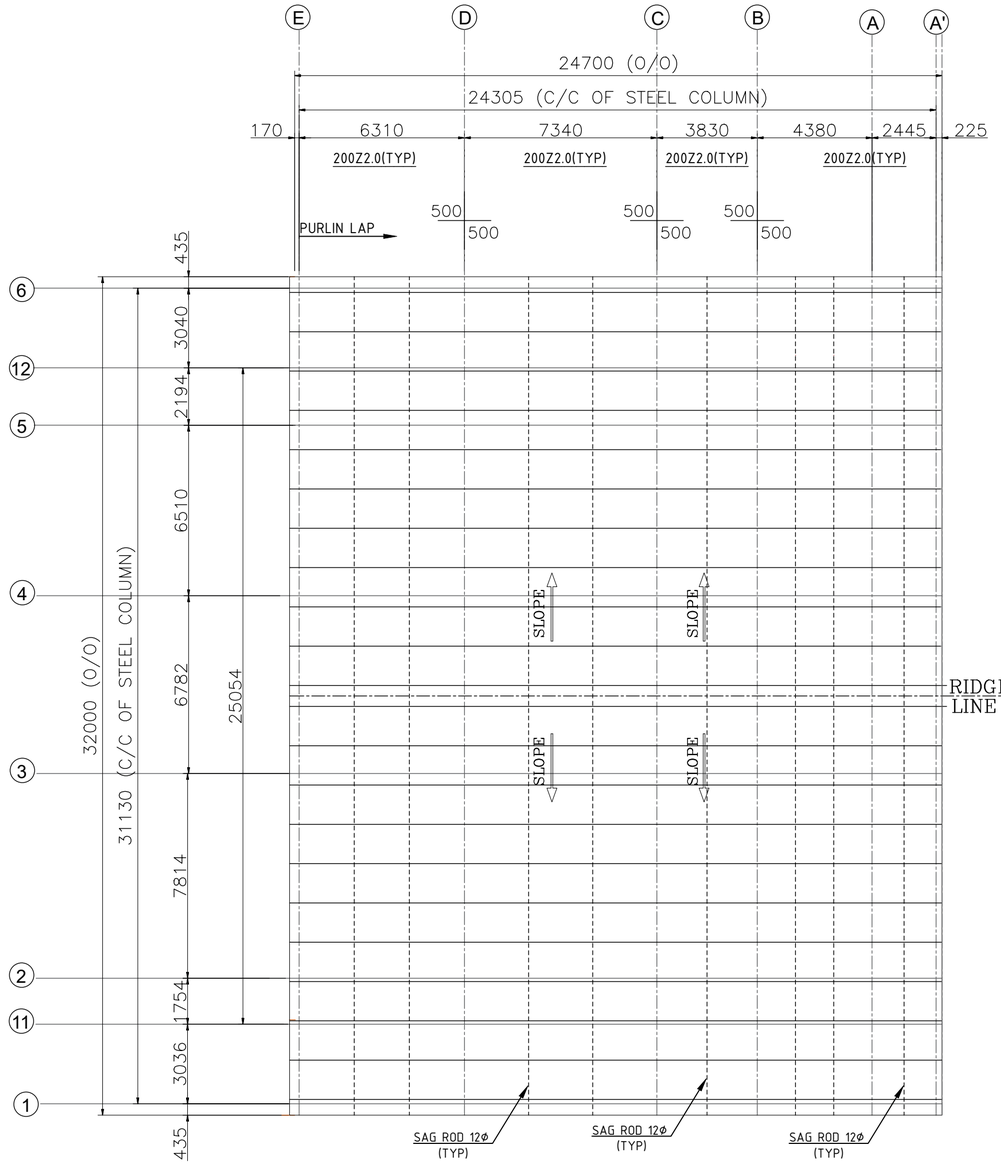



FSW

PURLIN ARRANGEMENT @ ROOF

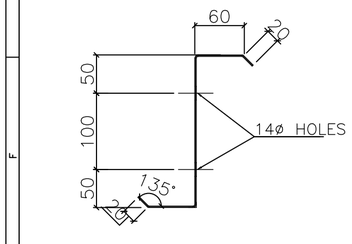


TYPICAL PURLIN DETAIL

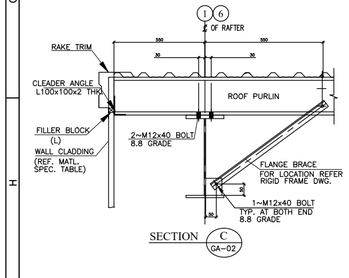


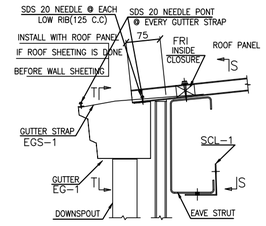


TYP. DETAIL AT EAVE
VIEW: A-A

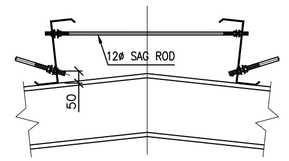

SAG ROD DETAIL AT ROOF PEAK

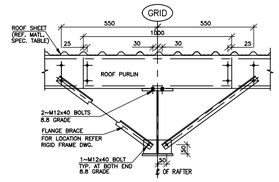

TYPICAL PURLIN LAP DETAIL (SHORT LAP)

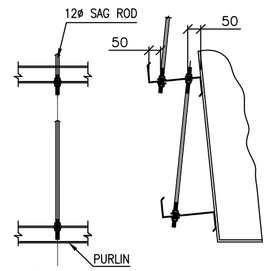

TYPICAL SAG ROD DETAIL

LEGEND:

FSW = FRONT SIDE WALL
BSW = BACK SIDE WALL
LEW = LEFT END WALL
REW = RIGHT END WALL


SWARAJYA STEEL BUILDING
WE BUILD BEST ...

ALL UNITS ARE IN MM & KGS.
DO NOT SCALE THE DRAWING.

REV.	DATE	DESCRIPTION	DSN	DRN	CKD
		ISSUED FOR APPROVAL	AP	PW	AP
00	18-06-2026	ISSUED FOR APPROVAL	AP	PW	AP

PROJECT No.	: SSB-J-2603
ASP JOB No.	: J-285
PROJECT NAME	: JHUNJHUNU AIRPORT
CLIENT NAME	: M/S VS INFRA VENTURES
COMPANY NAME	: AIR GLOBE AVIATION SCHOOL
JOB SITE LOCATION	: MIRA ROAD
ROOF FRAMING PLAN	DWG. No. GA-01


BSW

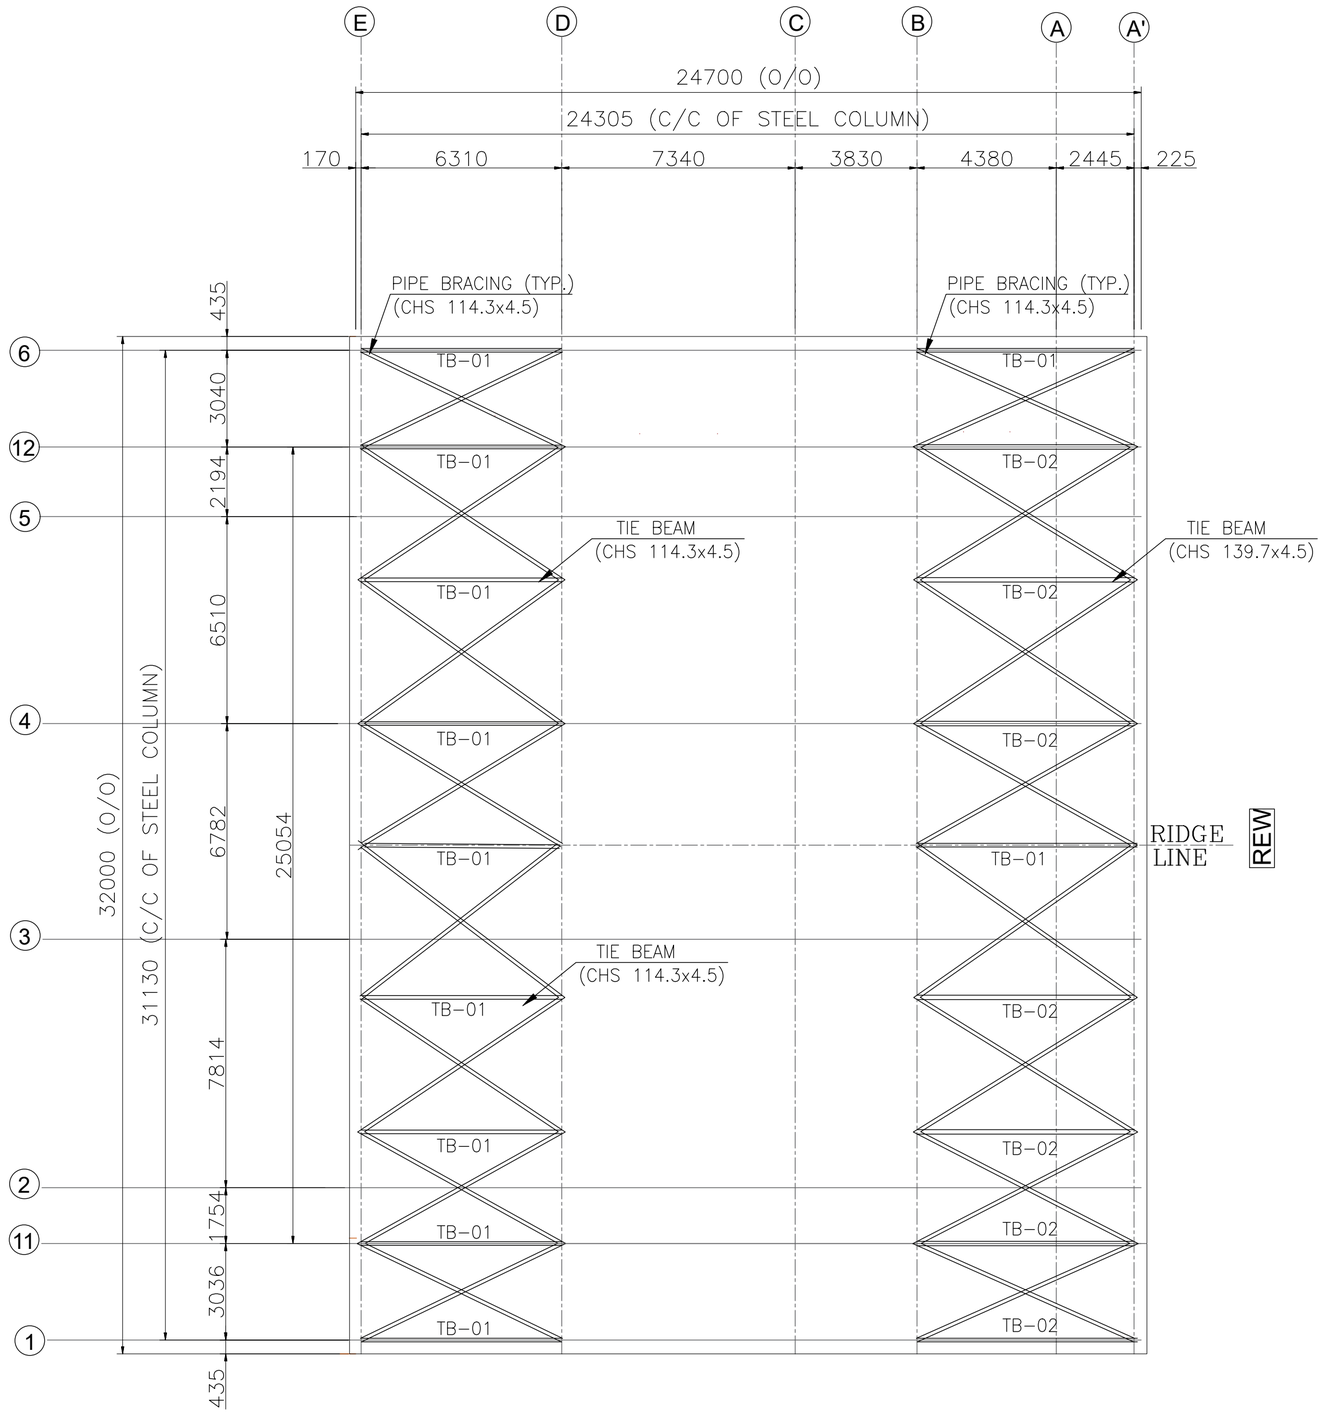


FSW

BRACING ARRANGEMENT @ ROOF

MATERIAL	SPECIFICATION
PIPE BRACING	(CHS 114.3x4.5)
TIE BEAM (TB-01)	(CHS 114.3x4.5)
TIE BEAM (TB-02)	(CHS 139.7x4.5)

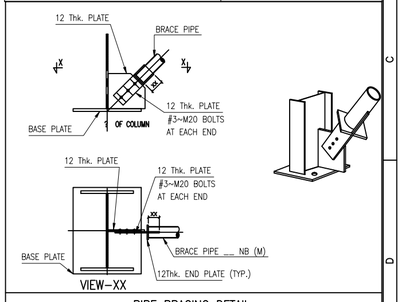

PIPE BRACING DETAIL
(@COLUMN BASE)

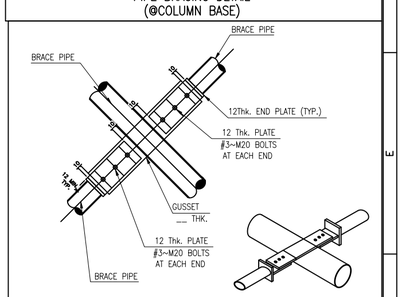

PIPE BRACING DETAIL
(@ INTERSECTION LOCATION)

LEGEND:

FSW = FRONT SIDE WALL
BSW = BACK SIDE WALL
LEW = LEFT END WALL
REW = RIGHT END WALL


SWARAJYA STEEL BUILDING
WE BUILD BEST ...

ALL UNITS ARE IN MM & KGS.
DO NOT SCALE THE DRAWING.

REV.	DATE	DESCRIPTION	DSN	DRN	CKD
		ISSUED FOR APPROVAL	AP	PW	AP
00	18-06-2026	ISSUED FOR APPROVAL	AP	PW	AP

PROJECT No.	: SSB-J-2603
ASP JOB No.	: J-285
PROJECT NAME	: JHUNJHUNU AIRPORT
CLIENT NAME	: M/S VS INFRA VENTURES
COMPANY NAME	: AIR GLOBE AVIATION SCHOOL
JOB SITE LOCATION	: MIRA ROAD
ROOF BRACING PLAN	DWG. No. GA-02

BSW

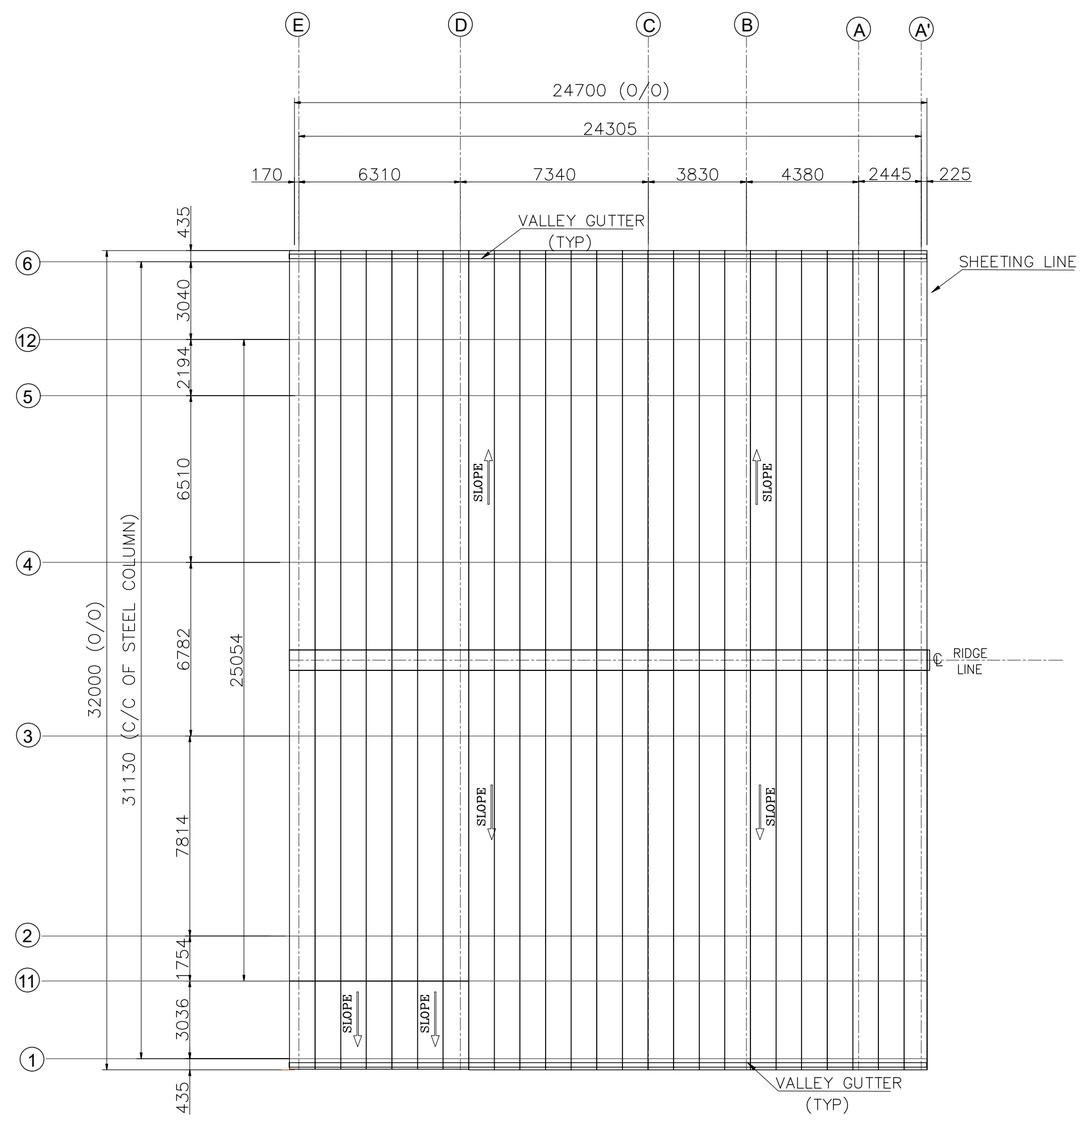


LEW


REW

FSW


ROOF SHEETING PLAN

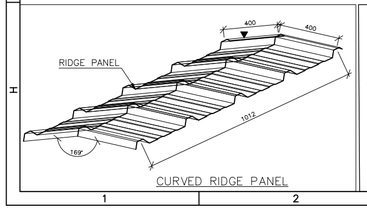


CURVED RIDGE PANEL

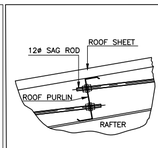

TYPICAL SAG ROD DETAIL

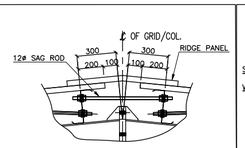

TYP. DETAIL OF RIDGE SAG ROD

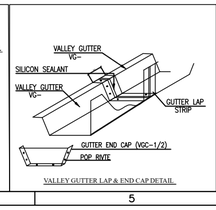

VALLEY GUTTER LAP & END CAP DETAIL

MATERIAL SPECIFICATION		
ITEM	DESCRIPTION	
ROOF SHEET	8MM BUBBLE INSULATION	
ROOF SHEET	MATERIAL = BG 1000MM THICKNESS = 0.5MM COLOUR = TO BE CONFIRM	
WALL CLADDING PANEL	MATERIAL = PPGI 1000MM THICKNESS = 0.5MM COLOUR = TO BE CONFIRM	
VALLEY GUTTER	THICKNESS = 0.5MM MATERIAL = GALVALUME COLOUR = TO BE CONFIRM	
PVC DOWN SPOUT PIPE	TYPE = SQ. 110 BOX COLOUR = TO BE CONFIRM	(AT EVERY GRID)
SKYLIGHT	TYPE = POLYCARBONATE SHEET THICKNESS = 2.0 MM. SIZE =3200MMx1000MM	N/A
TURBO VENTILATOR	SIZE =600MM DIA.	N/A

LEGEND:

FSW = FRONT SIDE WALL
BSW = BACK SIDE WALL
LEW = LEFT END WALL
REW = RIGHT END WALL

SWARAJYA STEEL BUILDING
WE BUILD BEST ...

ALL UNITS ARE IN MM & KGS.
DO NOT SCALE THE DRAWING.


REV	DATE	DESCRIPTION	DSN	DRN	CKD
		ISSUED FOR APPROVAL	AP	PR	AP
00	14-06-2024	ISSUED FOR APPROVAL	AP	PR	AP

PROJECT No.	: SSB-J-2603
ASP JOB No.	: J-285
PROJECT NAME	: JHUNJHUNU AIRPORT
CLIENT NAME	: M/S VS INFRA VENTURES
COMPANY NAME	: AIR GLOBE AVATION SCHOOL
JOB SITE LOCATION	: MIRA ROAD

ROOF SHEETING PLAN

DWG. No. GA-03

BSW

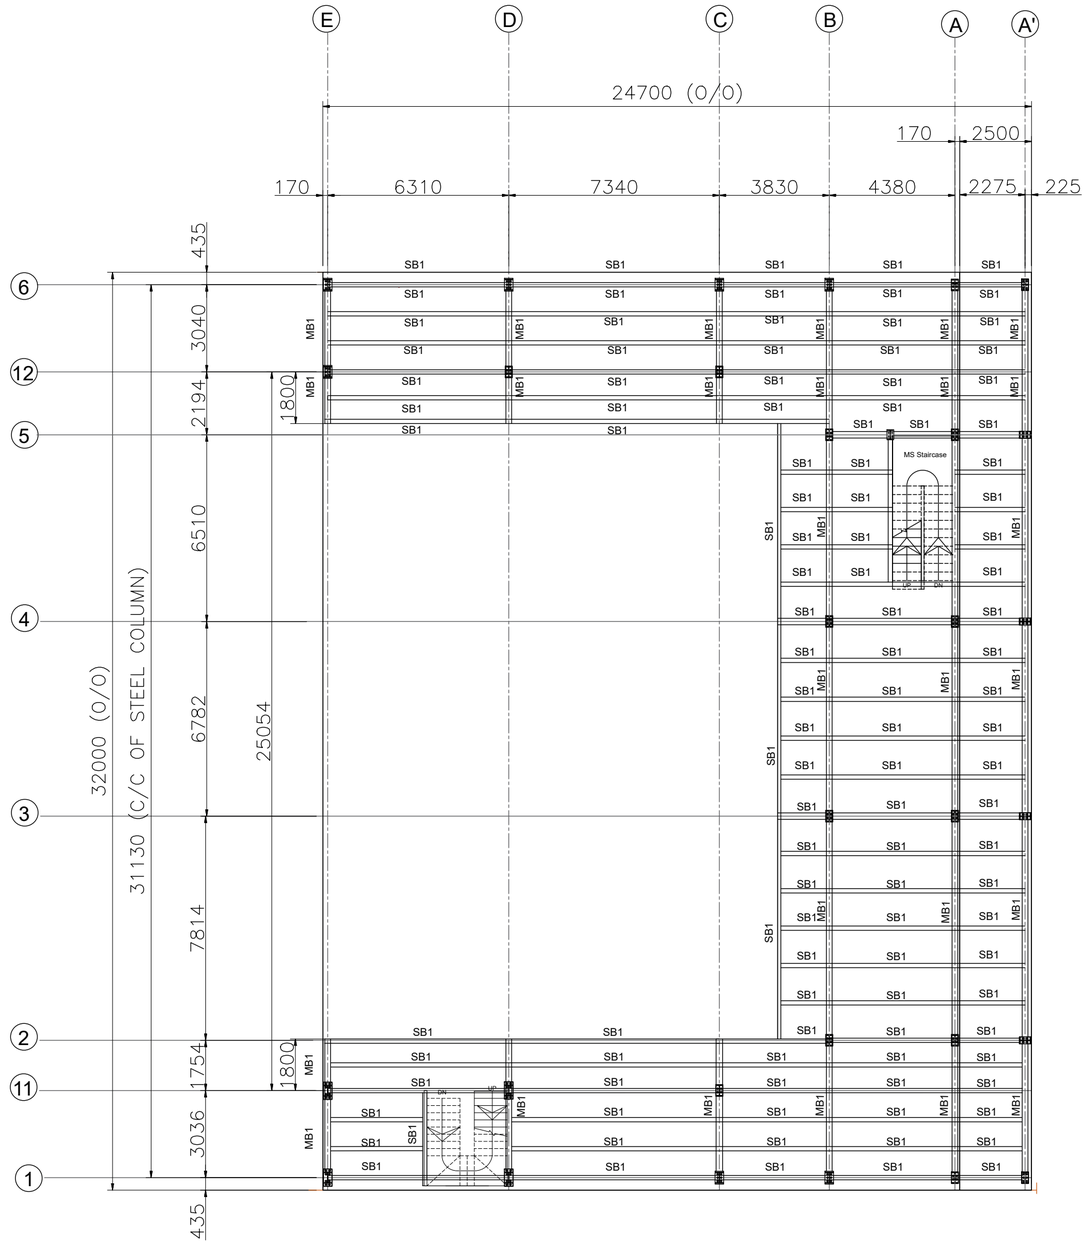


LEW

REW

MEZZANINE BEAM	
MARK	SIZE
MB1	W–450x6 F–200x10
SB1	W–350x5 F–150x6

BEAM–MB1 TYP

JOIST–SB1 TYP

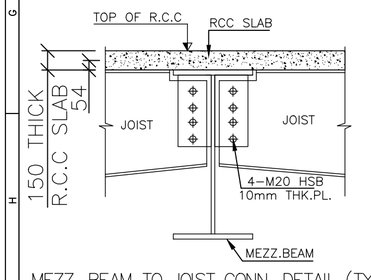

MEZZ. BEAM TO JOIST CONN. DETAIL (TYP).

FSW

MEZZANINE FIRST FLOOR PLAN

LVL– (+3.800M)


SWARAJYA STEEL BUILDING
WE BUILD BEST ...

ALL UNITS ARE IN MM & KGS.
DO NOT SCALE THE DRAWING.

REV.	DATE	DESCRIPTION	DSN	DRN	CKD
		ISSUED FOR APPROVAL	AP	PW	AP
00	18-06-2026	ISSUED FOR APPROVAL	AP	PW	AP

PROJECT No.	: SSB–J–2603
ASP JOB No.	: J–285
PROJECT NAME	: JHUNJHUNU AIRPORT
CLIENT NAME	: M/S VS INFRA VENTURES
COMPANY NAME	: AIR GLOBE AVIATION SCHOOL
JOB SITE LOCATION	: MIRA ROAD
MEZZANINE FIRST FLOOR PLAN	DWG. No. GA–04

BSW

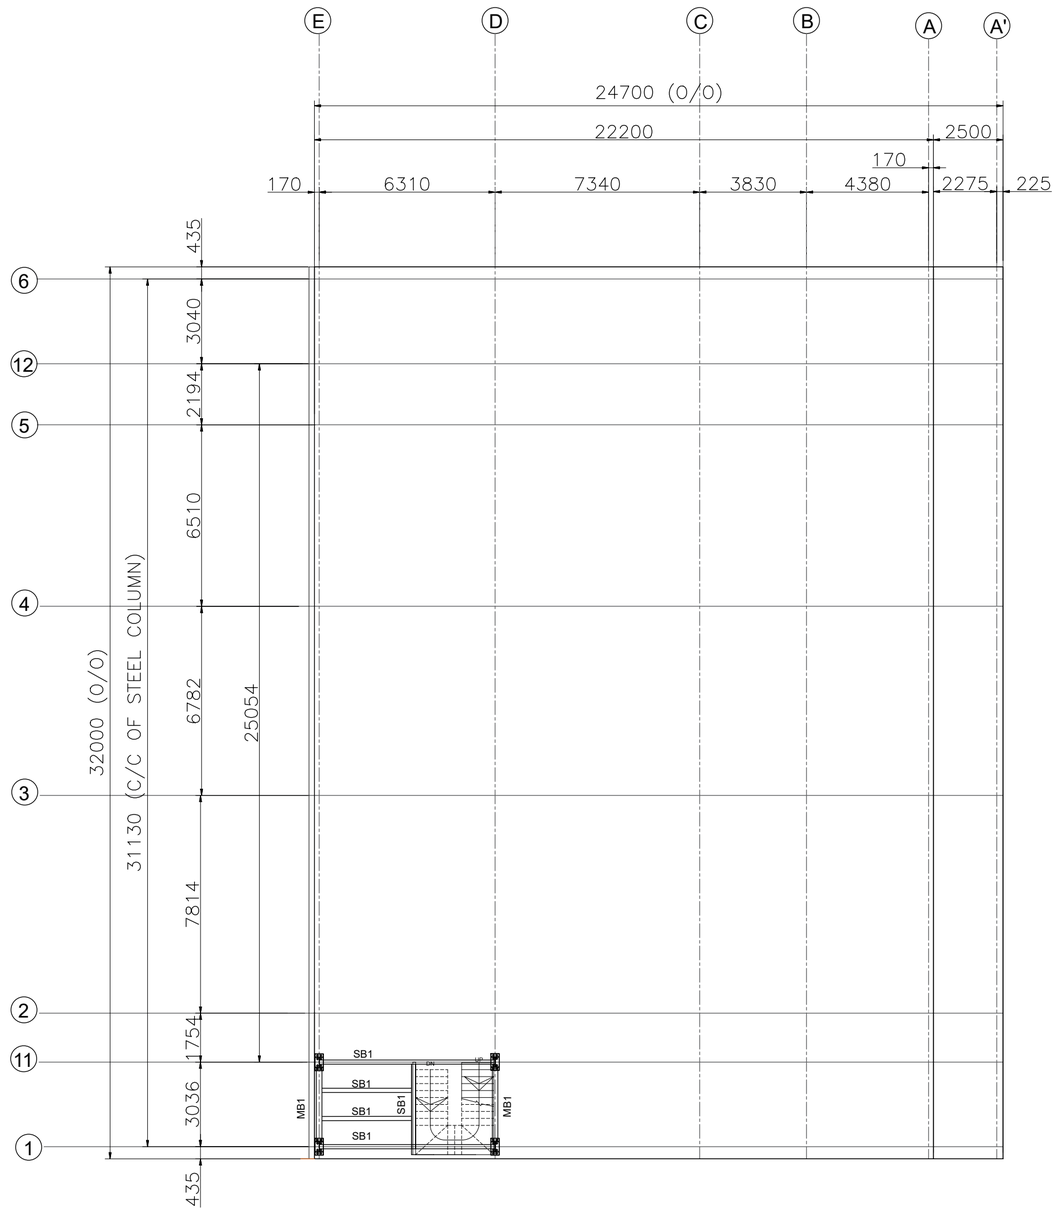

FSW

MEZZANINE SECOND FLOOR PLAN

LVL- (+7.4500M)

MEZZANINE BEAM	
MARK	SIZE
MB1	W-450x6 F-200x10
SB1	W-350x5 F-150x6

SWARAJYA STEEL BUILDING
WE BUILD BEST ...

ALL UNITS ARE IN MM & KGS.
DO NOT SCALE THE DRAWING.


REV.	DATE	DESCRIPTION	DSN	DRN	CKD
		ISSUED FOR APPROVAL	AP	PW	AP
00	18-06-2026	ISSUED FOR APPROVAL	AP	PW	AP

PROJECT No.	: SSB-J-2603
ASP JOB No.	: J-285
PROJECT NAME	: JHUNJHUNU AIRPORT
CLIENT NAME	: M/S VS INFRA VENTURES
COMPANY NAME	: AIR GLOBE AVIATION SCHOOL
JOB SITE LOCATION	: MIRA ROAD

MEZZANINE SECOND FLOOR PLAN	DWG. No.
	GA-05

MEZZANINE BEAM	
MARK	SIZE
MB1	W-450x6 F-200x10
SB1	W-350x5 F-150x6

BSW

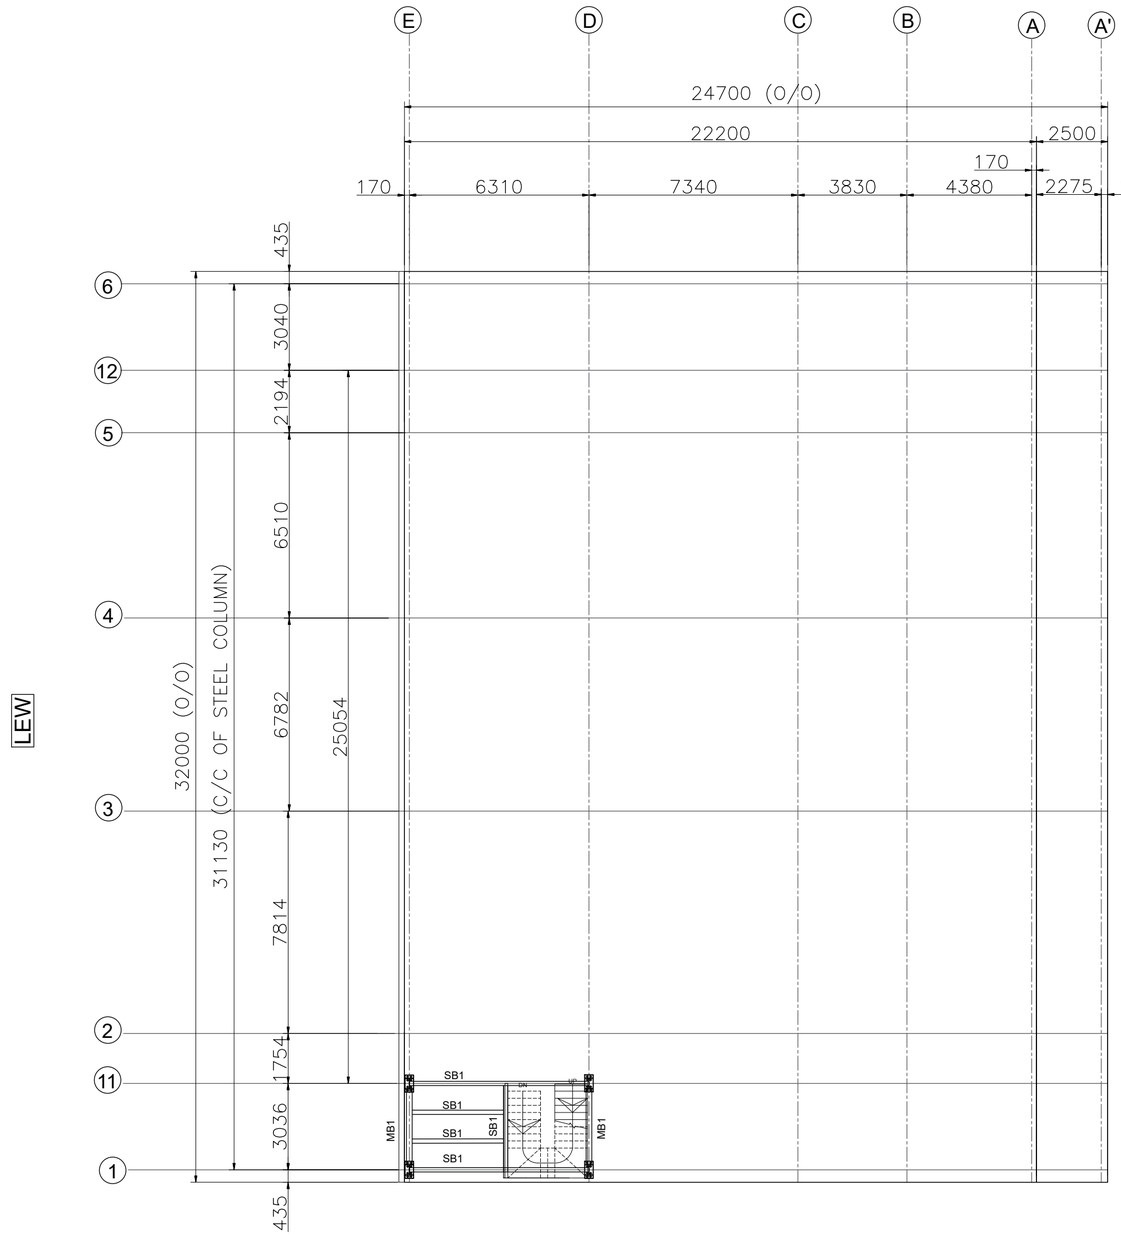

FSW

MEZZANINE THIRD FLOOR PLAN

LVL – (+10.45M)

SWARAJYA STEEL BUILDING
WE BUILD BEST ...


ALL UNITS ARE IN MM & KGS.
DO NOT SCALE THE DRAWING.

REV.	DATE	DESCRIPTION	DSN	DRN	CKD
		ISSUED FOR APPROVAL	AP	PW	AP
00	18-06-2026	ISSUED FOR APPROVAL	AP	PW	AP

PROJECT No.	: SSB-J-2603
ASP JOB No.	: J-285
PROJECT NAME	: JHUNJHUNU AIRPORT
CLIENT NAME	: M/S VS INFRA VENTURES
COMPANY NAME	: AIR GLOBE AVIATION SCHOOL
JOB SITE LOCATION	: MIRA ROAD


MEZZANINE THIRD FLOOR PLAN

DWG. No.
GA-06

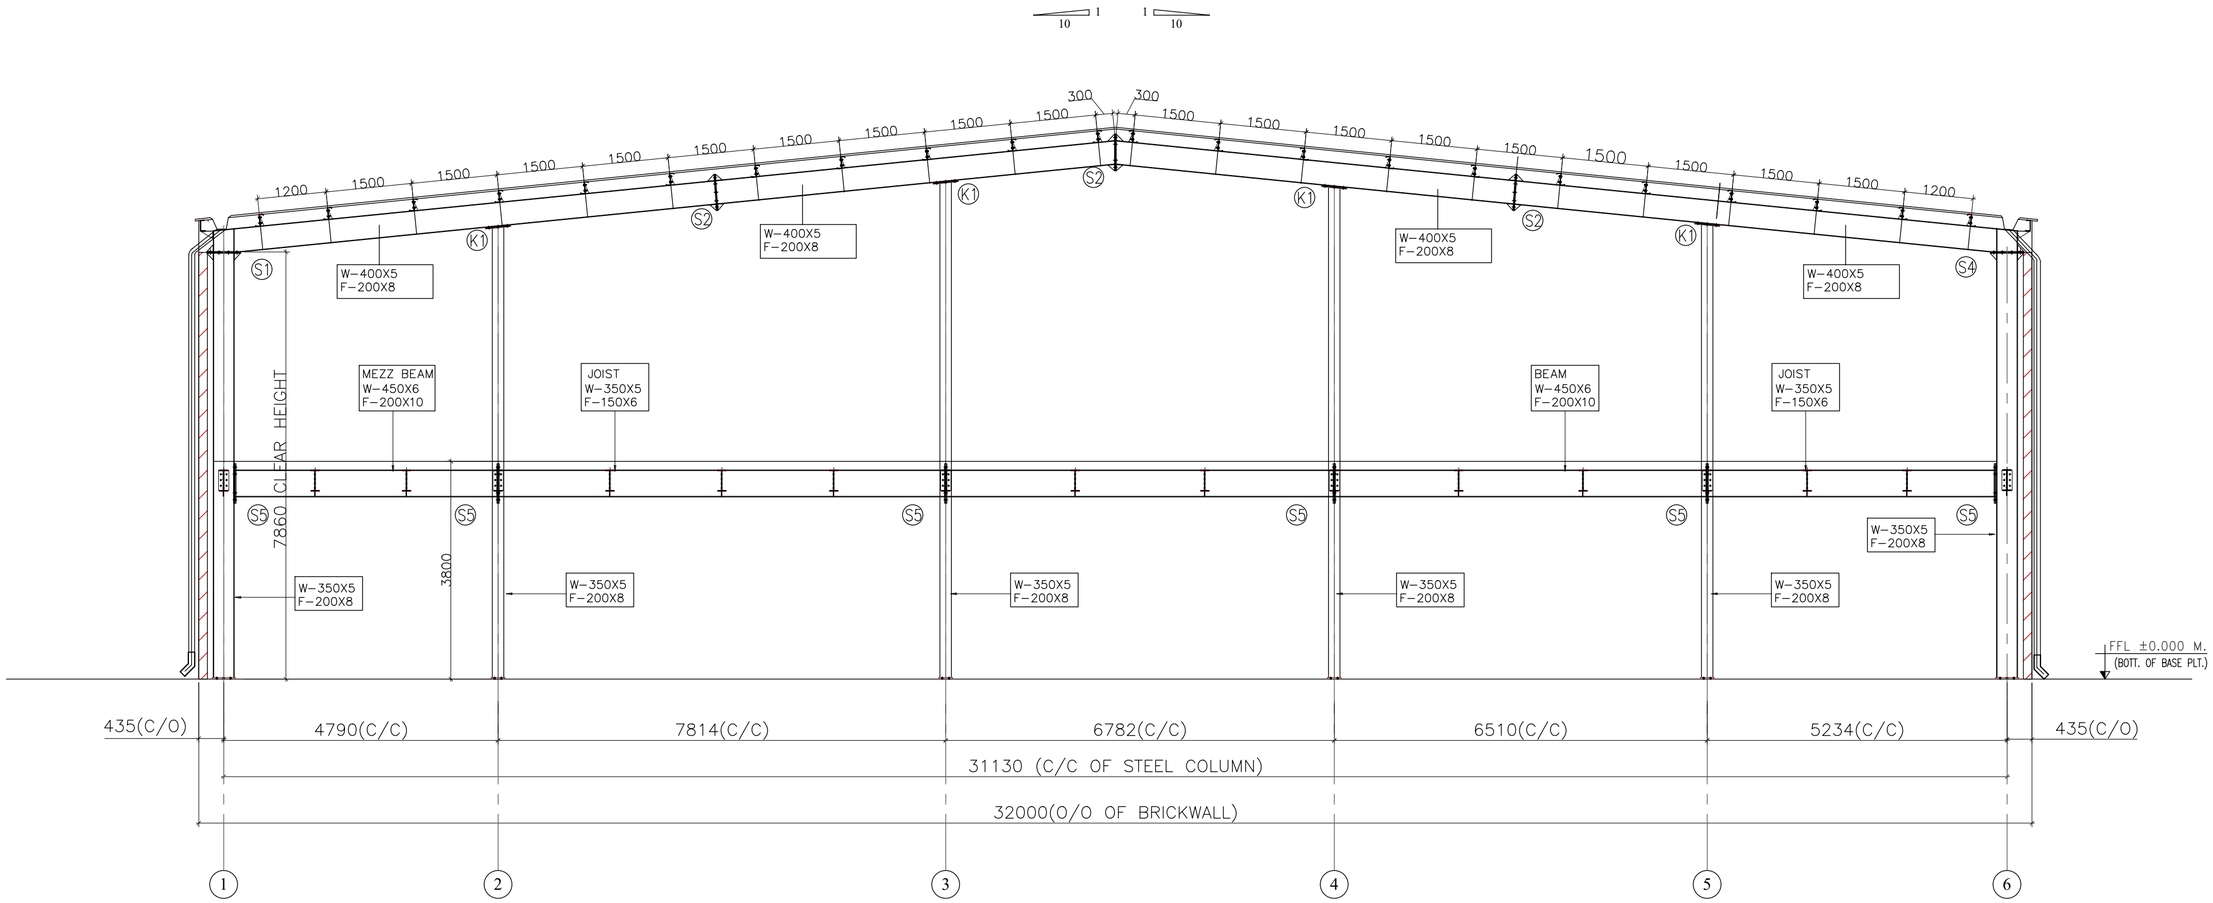

END FRAME CROSS SECTION

(FOR FRAME LINE A')

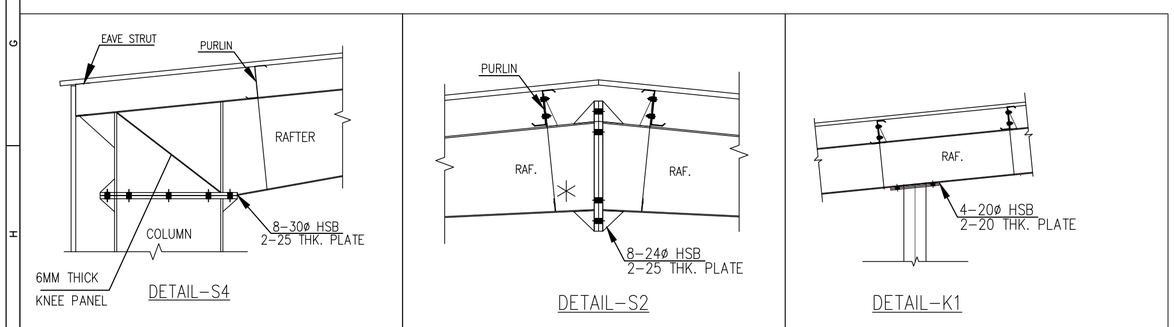

SWARAJYA STEEL BUILDING
WE BUILD BEST ...


ALL UNITS ARE IN MM & KGS.
DO NOT SCALE THE DRAWING.

REV.	DATE	DESCRIPTION	DSN	DRN	CKD
		ISSUED FOR APPROVAL	AP	PW	AP
00	18-06-2026	ISSUED FOR APPROVAL	AP	PW	AP

PROJECT No.	: SSB-J-2603
ASP JOB No.	: J-285
PROJECT NAME	: JHUNJHUNU AIRPORT
CLIENT NAME	: M/S VS INFRA VENTURES
COMPANY NAME	: AIR GLOBE AVIATION SCHOOL
JOB SITE LOCATION	: MIRA ROAD


END FRAME C/S

DWG. No.
GA-07

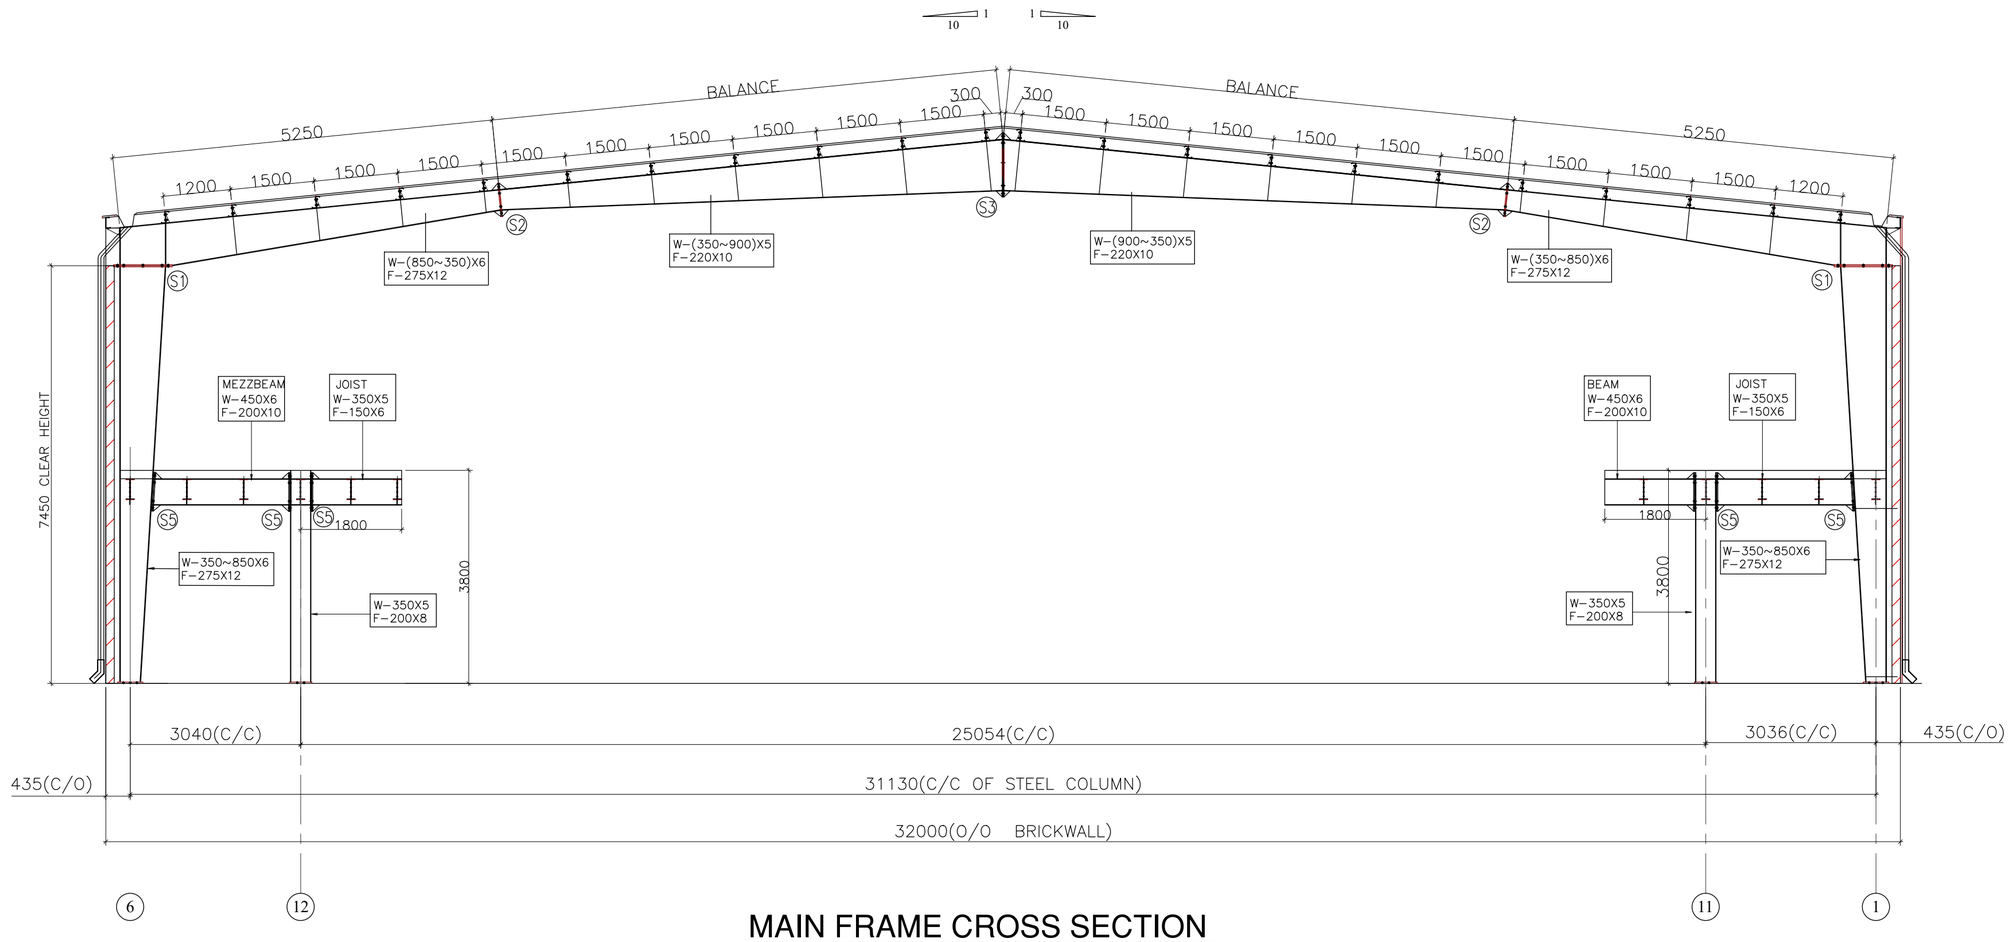


MAIN FRAME CROSS SECTION


(FOR FRAME LINE C)

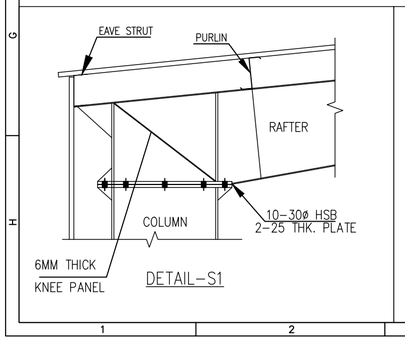


DETAIL-S1

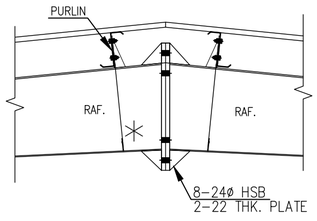


DETAIL-S2

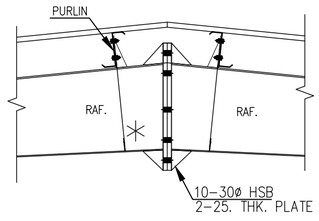

DETAIL-S3

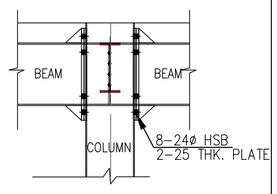

DETAIL-S5

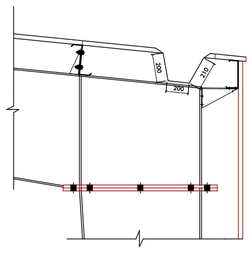


VALLEY GUTTER (TYP)

SWARAJYA STEEL BUILDING
WE BUILD BEST ...

ALL UNITS ARE IN MM & KGS.
DO NOT SCALE THE DRAWING.


REV.	DATE	DESCRIPTION	DSN	DRN	CKD
		ISSUED FOR APPROVAL	AP	PW	AP
00	18-06-2026	ISSUED FOR APPROVAL	AP	PW	AP

PROJECT No.	: SSB-J-2603
ASP JOB No.	: J-285
PROJECT NAME	: JHUNJHUNU AIRPORT
CLIENT NAME	: M/S VS INFRA VENTURES
COMPANY NAME	: AIR GLOBE AVIATION SCHOOL
JOB SITE LOCATION	: MIRA ROAD
MAIN FRAME C/S	DWG. No. GA-09

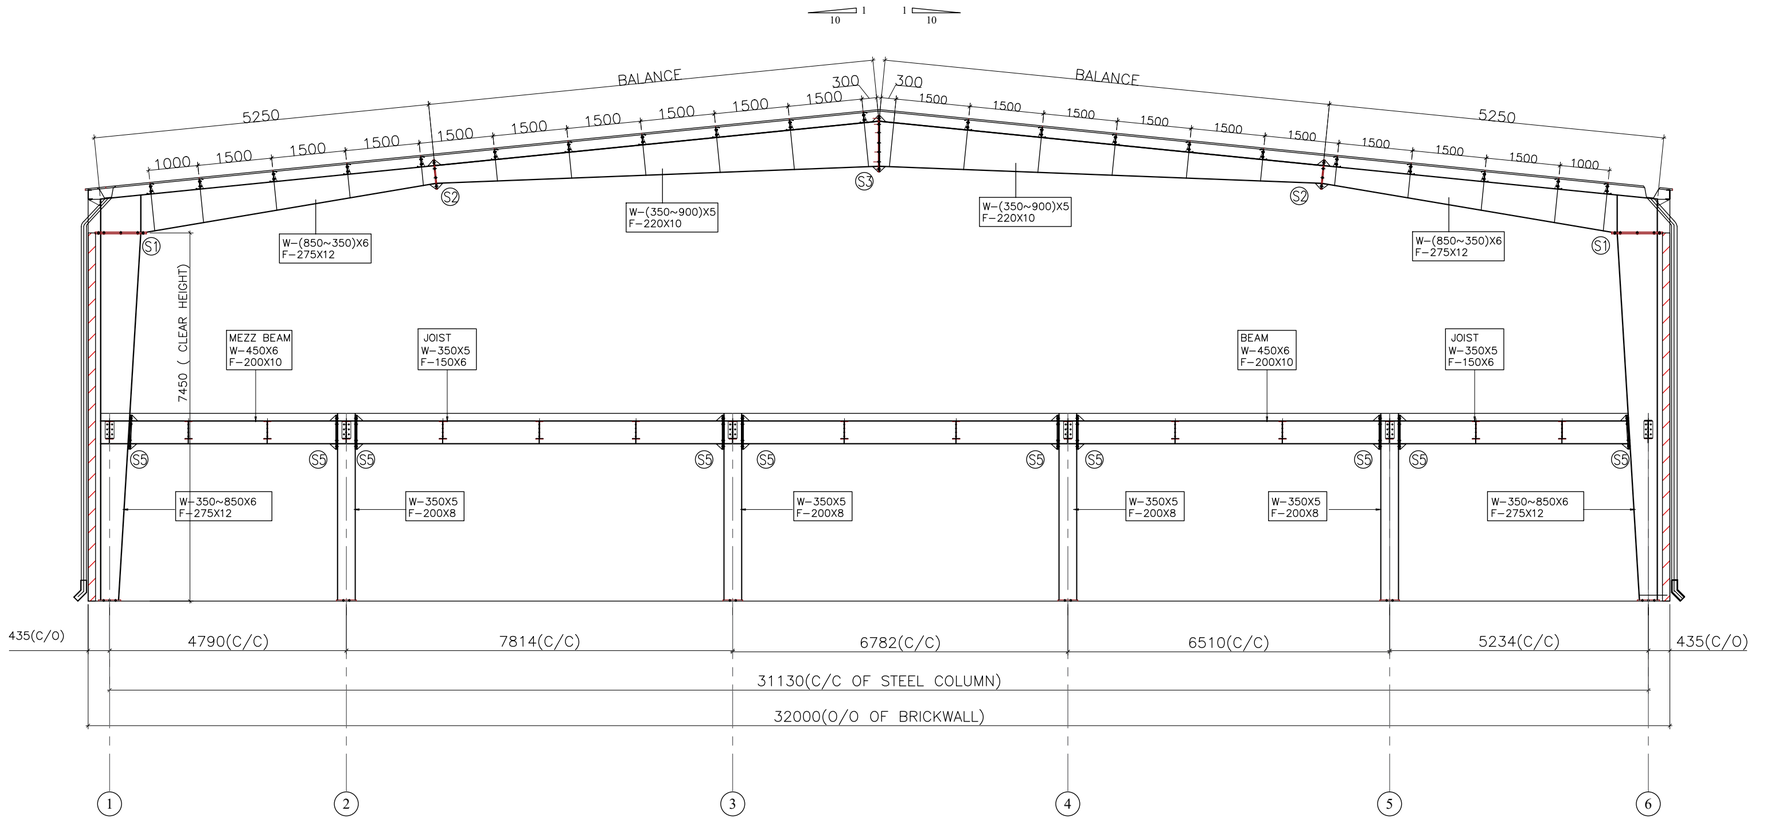

MAIN FRAME CROSS SECTION

(FOR FRAME LINE B)

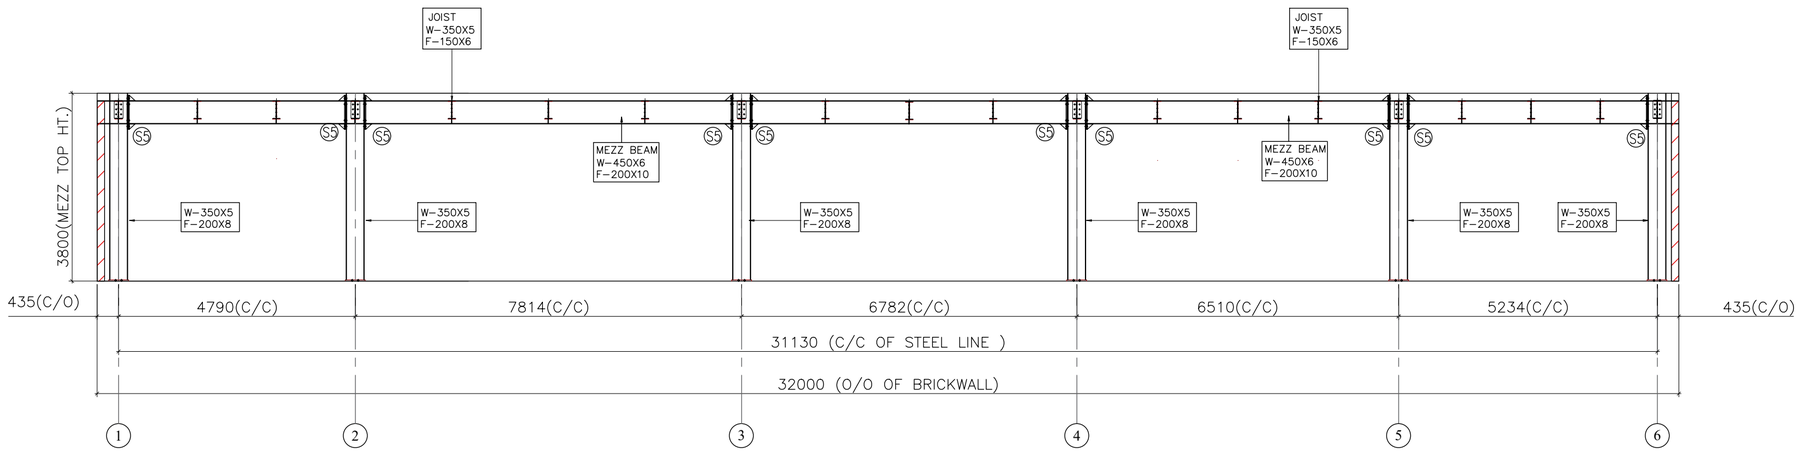

MAIN FRAME CROSS SECTION

(FOR FRAME LINE A)


SWARAJYA STEEL BUILDING
WE BUILD BEST ...

ALL UNITS ARE IN MM & KGS.
DO NOT SCALE THE DRAWING.

REV.	DATE	DESCRIPTION	DSN	DRN	CKD
		ISSUED FOR APPROVAL	AP	PR	AP
R1	9-Feb-2021	ISSUED FOR APPROVAL	AP	PR	AP


PROJECT No.	: SSB-J-2603
ADP JOB No.	: J-293
PROJECT NAME	: JHUNJHUNU AIRPORT
CLIENT NAME	: M/S VG INFRA VENTURES
COMPANY NAME	: AIR GLOBE AVIATION SCHOOL
JOB SITE LOCATION	: MIRA ROAD

MAIN FRAME C/S — DWG. No. GA-10

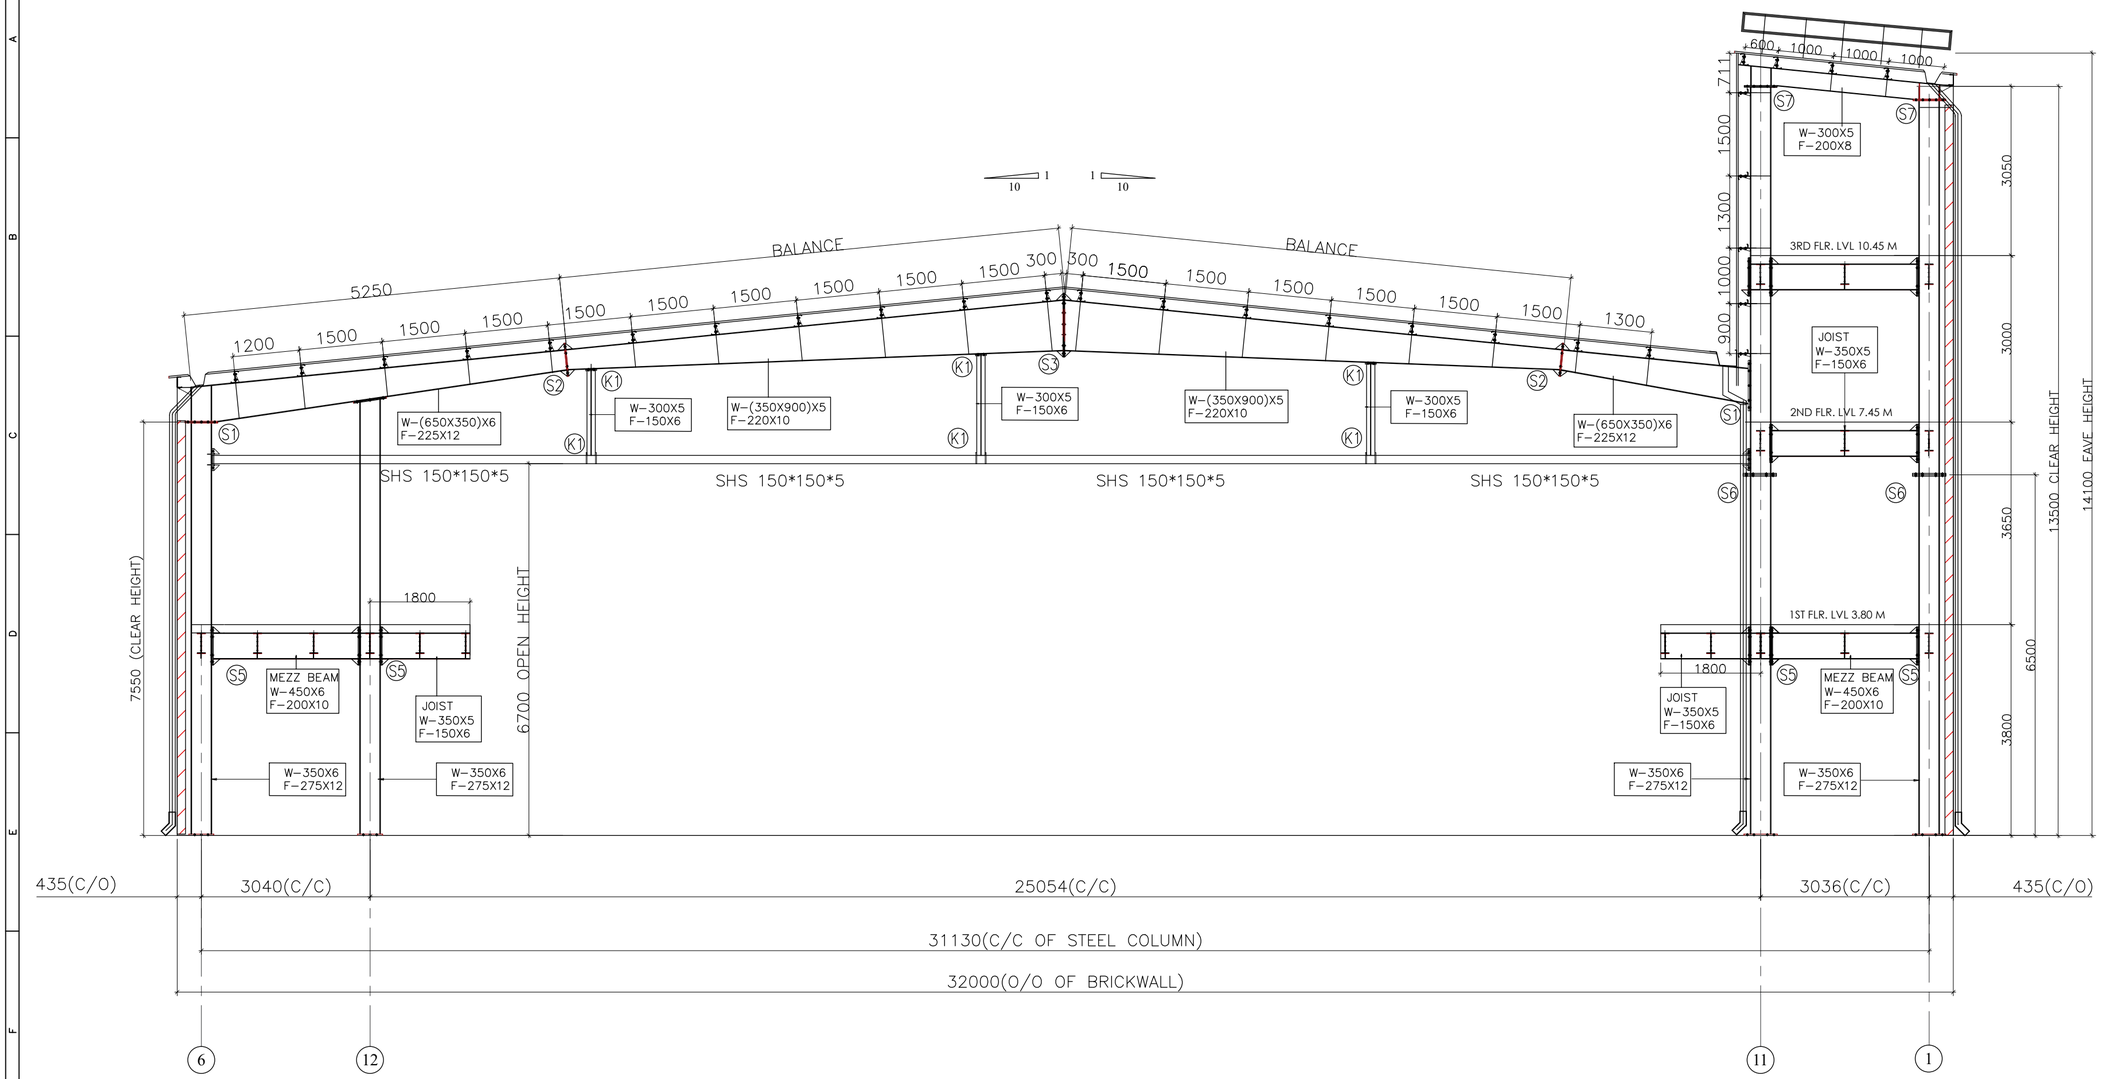


END FRAME CROSS SECTION

(FOR FRAME LINE E)

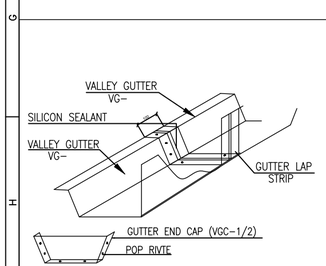

VALLEY GUTTER LAP & END CAP DETAIL

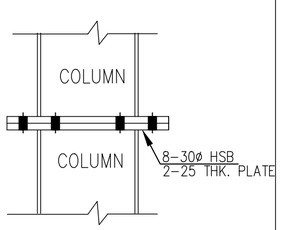

DETAIL-S6

SWARAJYA STEEL BUILDING
WE BUILD BEST ...

ALL UNITS ARE IN MM & KGS.


DO NOT SCALE THE DRAWING.

REV.	DATE	DESCRIPTION	DSN	DRN	CKD
		ISSUED FOR APPROVAL	AP	PW	AP
00	18-06-2026	ISSUED FOR APPROVAL	AP	PW	AP

PROJECT No.	: SSB-J-2603
ASP JOB No.	: J-285
PROJECT NAME	: JHUNJHUNU AIRPORT
CLIENT NAME	: M/S VS INFRA VENTURES
COMPANY NAME	: AIR GLOBE AVIATION SCHOOL
JOB SITE LOCATION	: MIRA ROAD


MAIN FRAME C/S

DWG. No. GA-11

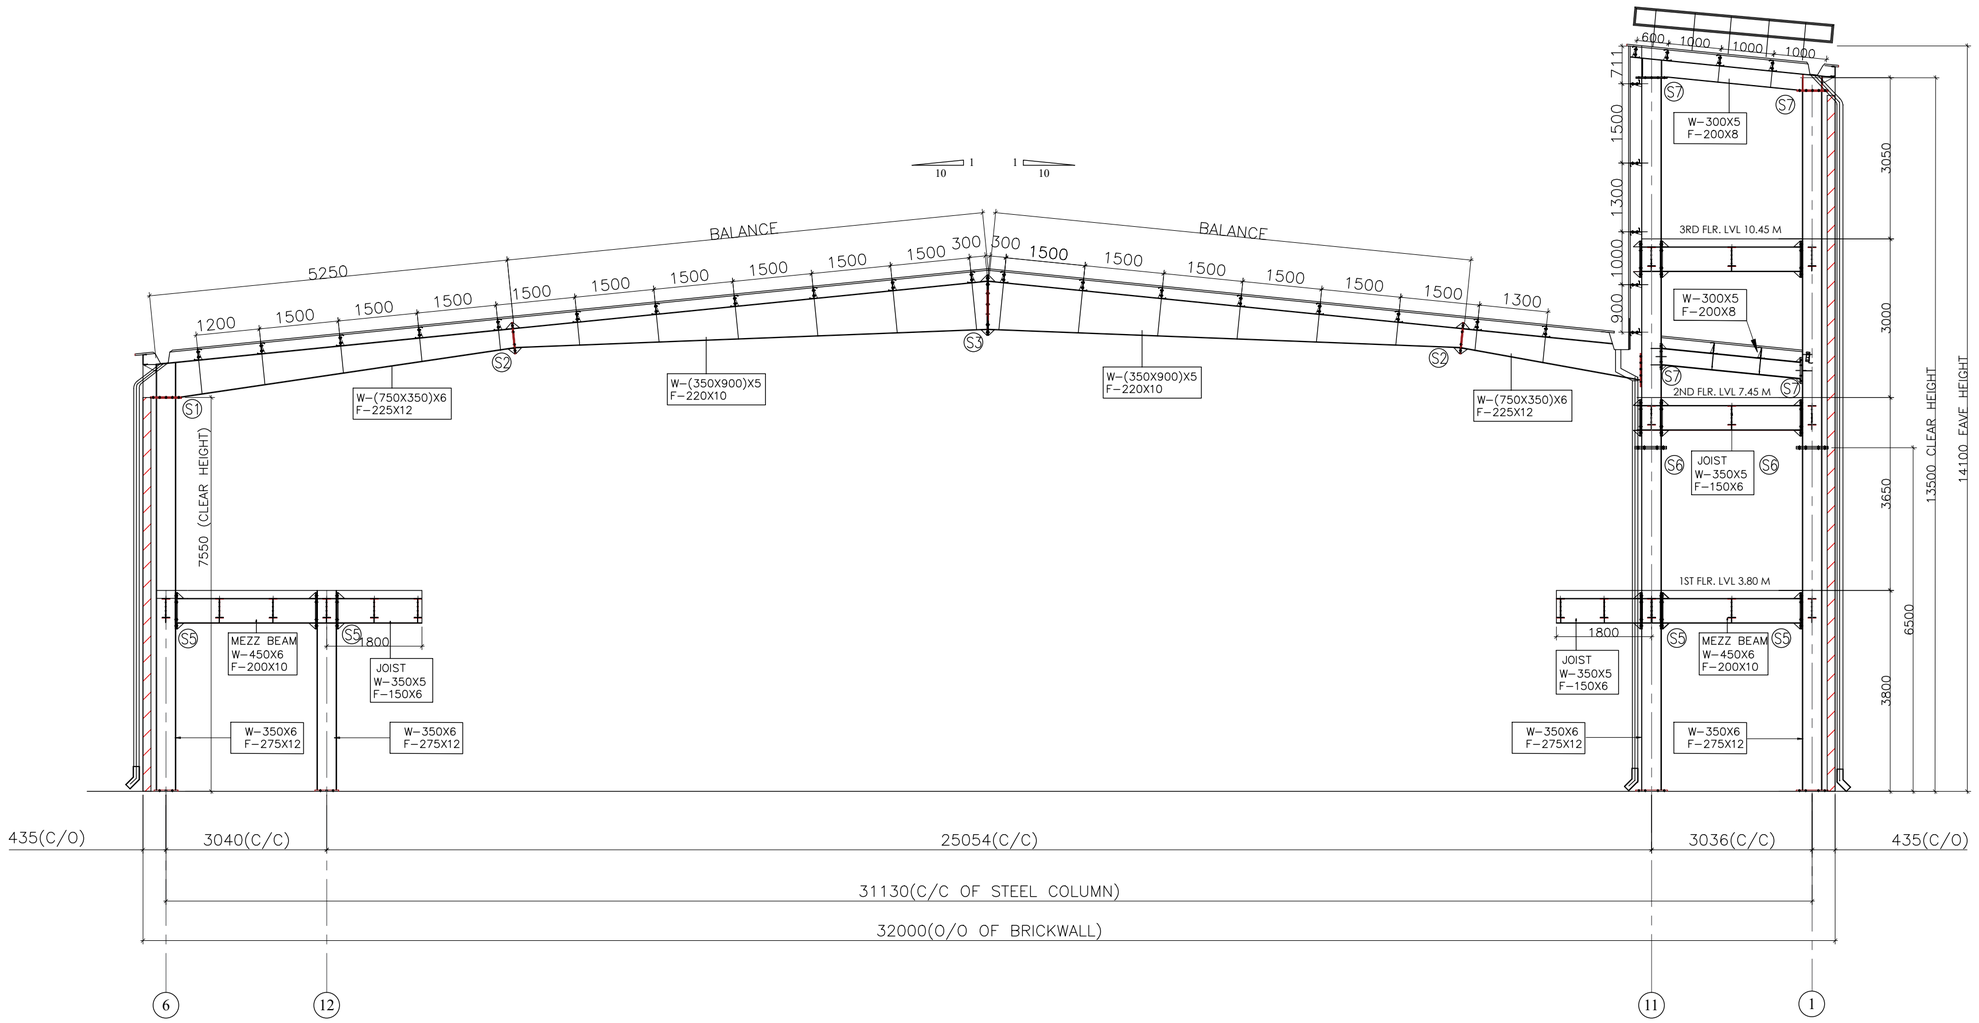

MAIN FRAME CROSS SECTION

(FOR FRAME LINE D)

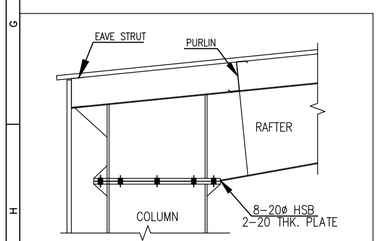

DETAIL-S7

SWARAJYA STEEL BUILDING
WE BUILD BEST ...

ALL UNITS ARE IN MM & KGS.


DO NOT SCALE THE DRAWING.

REV.	DATE	DESCRIPTION			
		ISSUED FOR APPROVAL	AP	PW	AP
00	18-06-2026	ISSUED FOR APPROVAL	AP	PW	AP

PROJECT No.	: SSB-J-2603
ASP JOB No.	: J-285
PROJECT NAME	: JHUNJHUNU AIRPORT
CLIENT NAME	: M/S VS INFRA VENTURES
COMPANY NAME	: AIR GLOBE AVIATION SCHOOL
JOB SITE LOCATION	: MIRA ROAD

MAIN FRAME C/S

DWG. No. GA-12

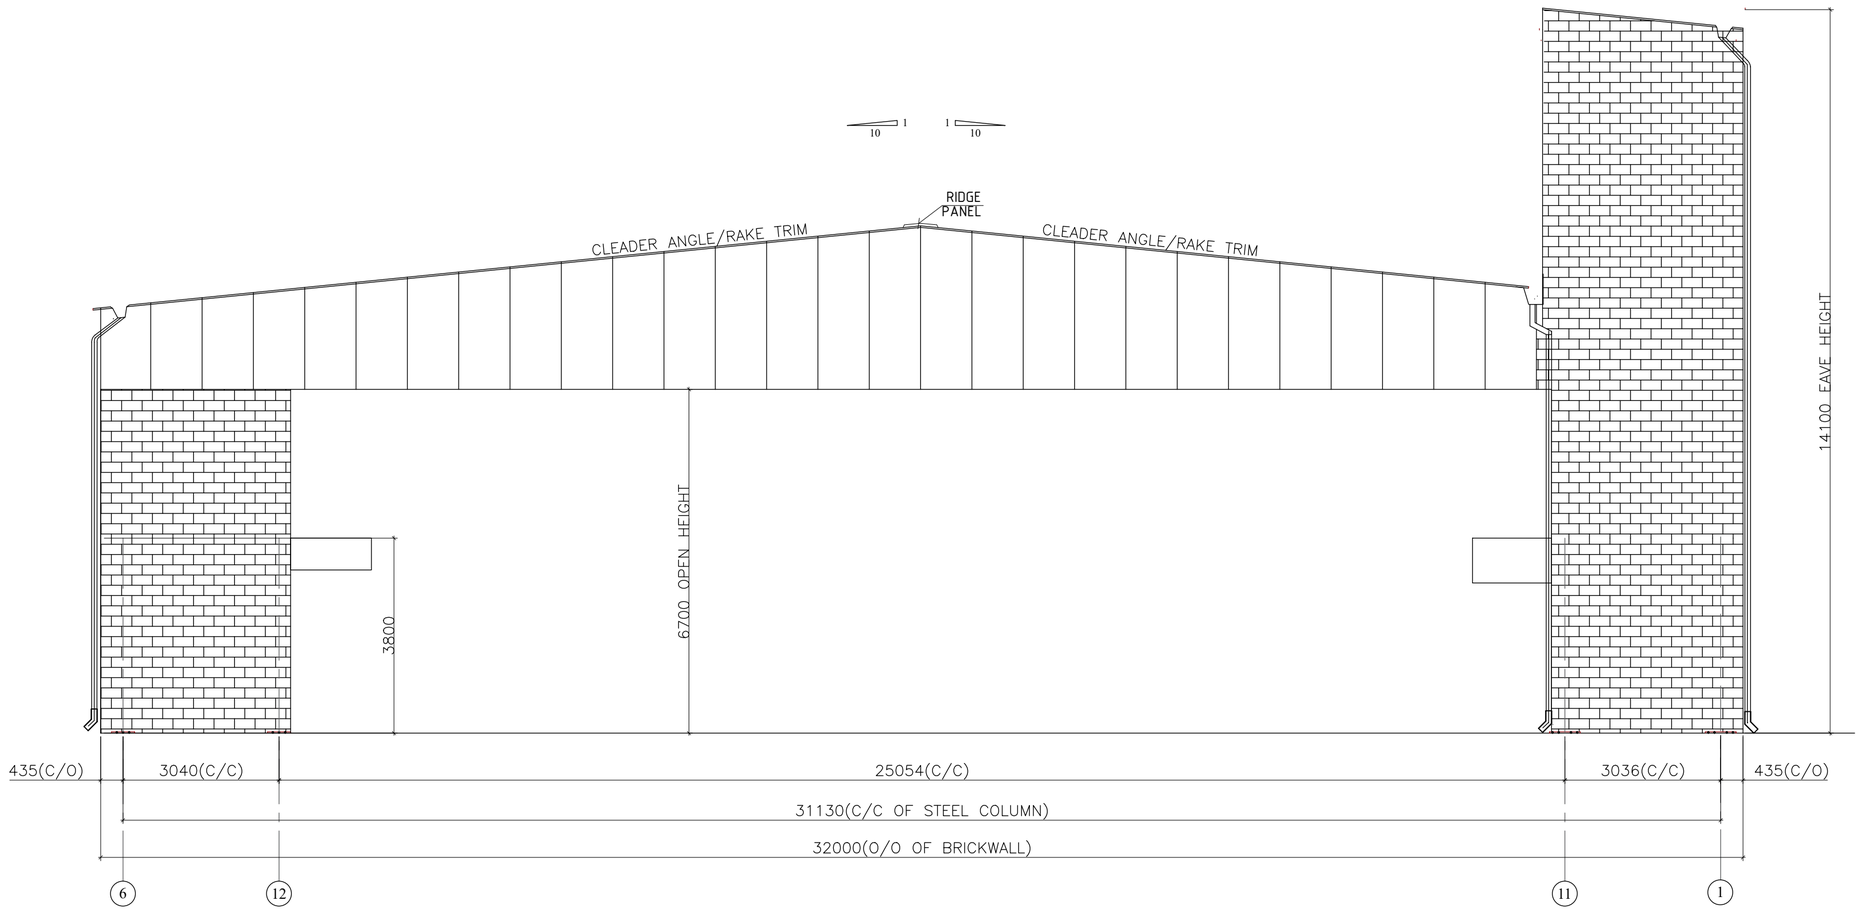

ENDWALL SHEETING ELEVATION


(FOR FRAME LINE E)

SWARAJYA STEEL BUILDING
WE BUILD BEST ...

ALL UNITS ARE IN MM & KGS.
DO NOT SCALE THE DRAWING.

REV.	DATE	DESCRIPTION	DSN	DRN	CKD
		ISSUED FOR APPROVAL	AP	PW	AP
00	18-06-2026	ISSUED FOR APPROVAL	AP	PW	AP

PROJECT No.	: SSB-J-2603
ASP JOB No.	: J-285
PROJECT NAME	: JHUNJHUNU AIRPORT
CLIENT NAME	: M/S VS INFRA VENTURES
COMPANY NAME	: AIR GLOBE AVIATION SCHOOL
JOB SITE LOCATION	: MIRA ROAD
ENDWALL SHEETING ELEVATION	DWG. No. GA-14

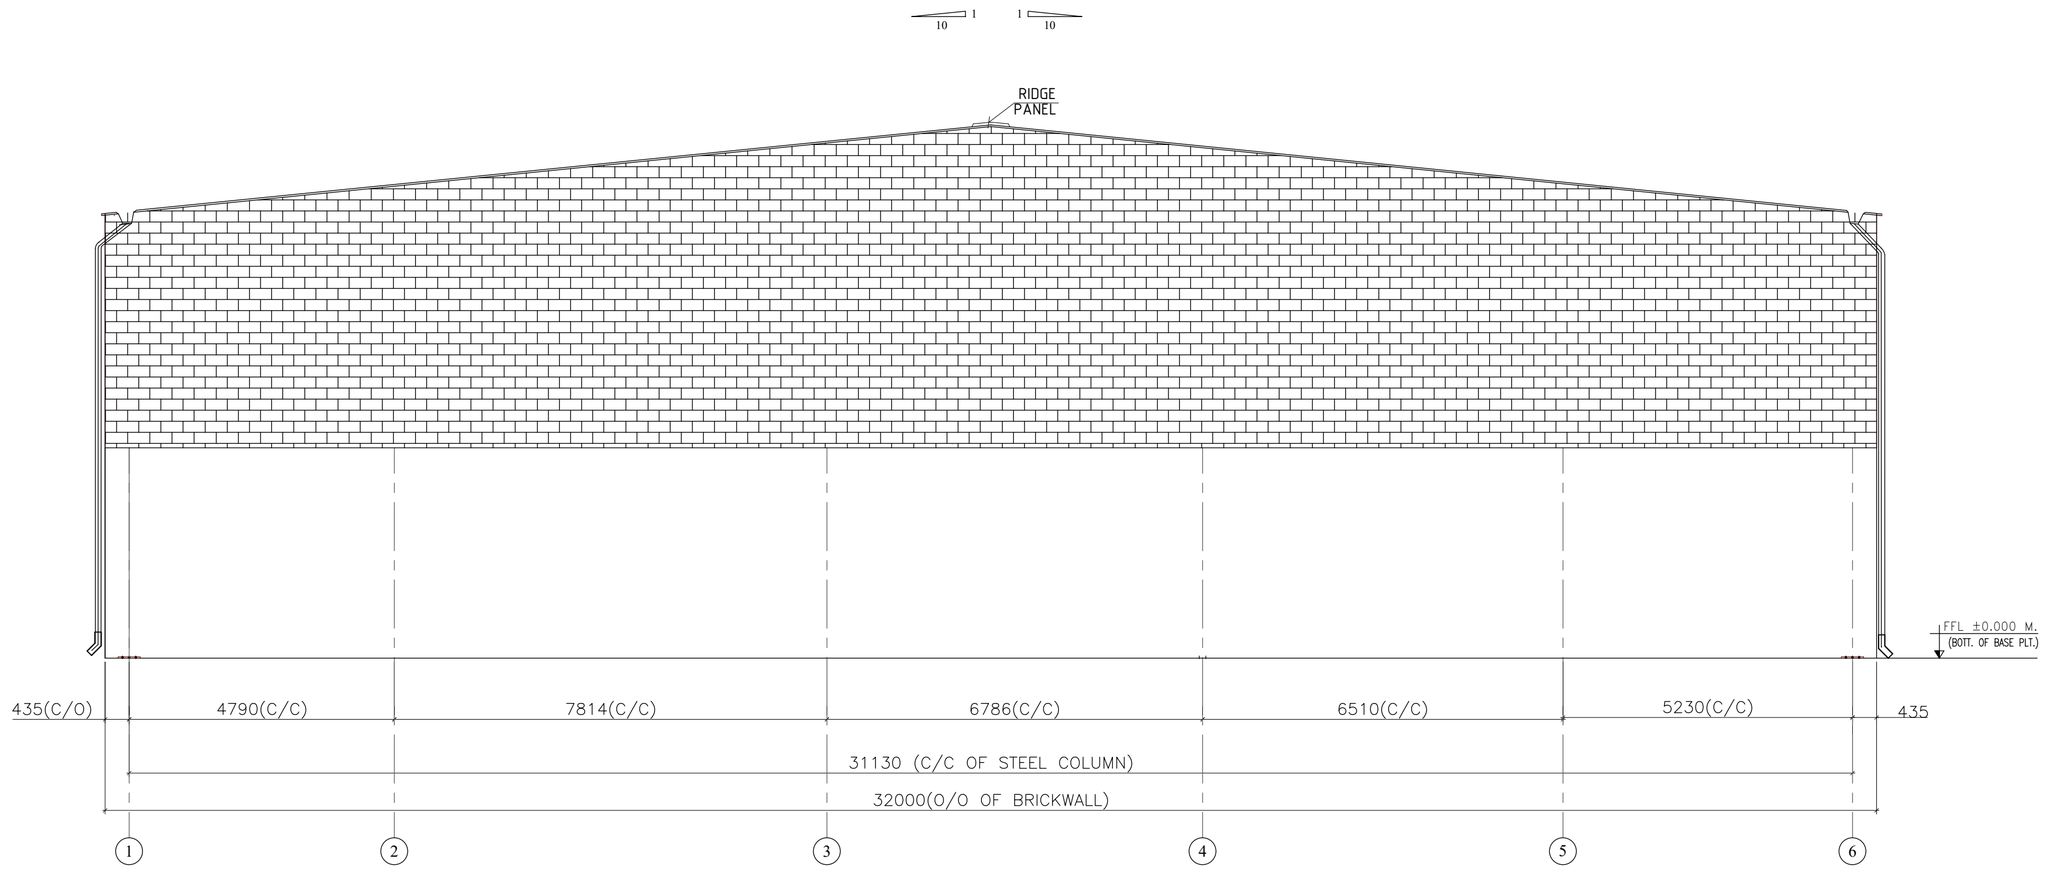

ENDWALL ELEVATION

(FOR FRAME LINE A')

SWARAJYA STEEL BUILDING
WE BUILD BEST ...


ALL UNITS ARE IN MM & KGS.
DO NOT SCALE THE DRAWING.

REV	DATE	DESCRIPTION	DSN	DRN	CKD
		ISSUED FOR APPROVAL	AP	PN	AP
00	18-06-2026	ISSUED FOR APPROVAL	AP	PN	AP

PROJECT No.	: SSB-J-2603
ASP JOB No.	: J-285
PROJECT NAME	: JHUNJHUNU AIRPORT
CLIENT NAME	: M/S VS INFRA VENTURES
COMPANY NAME	: AIR GLOBE AVIATION SCHOOL
JOB SITE LOCATION	: MIRA ROAD

ENDWALL SHEETING ELEVATION

DWG. No.
GA-09

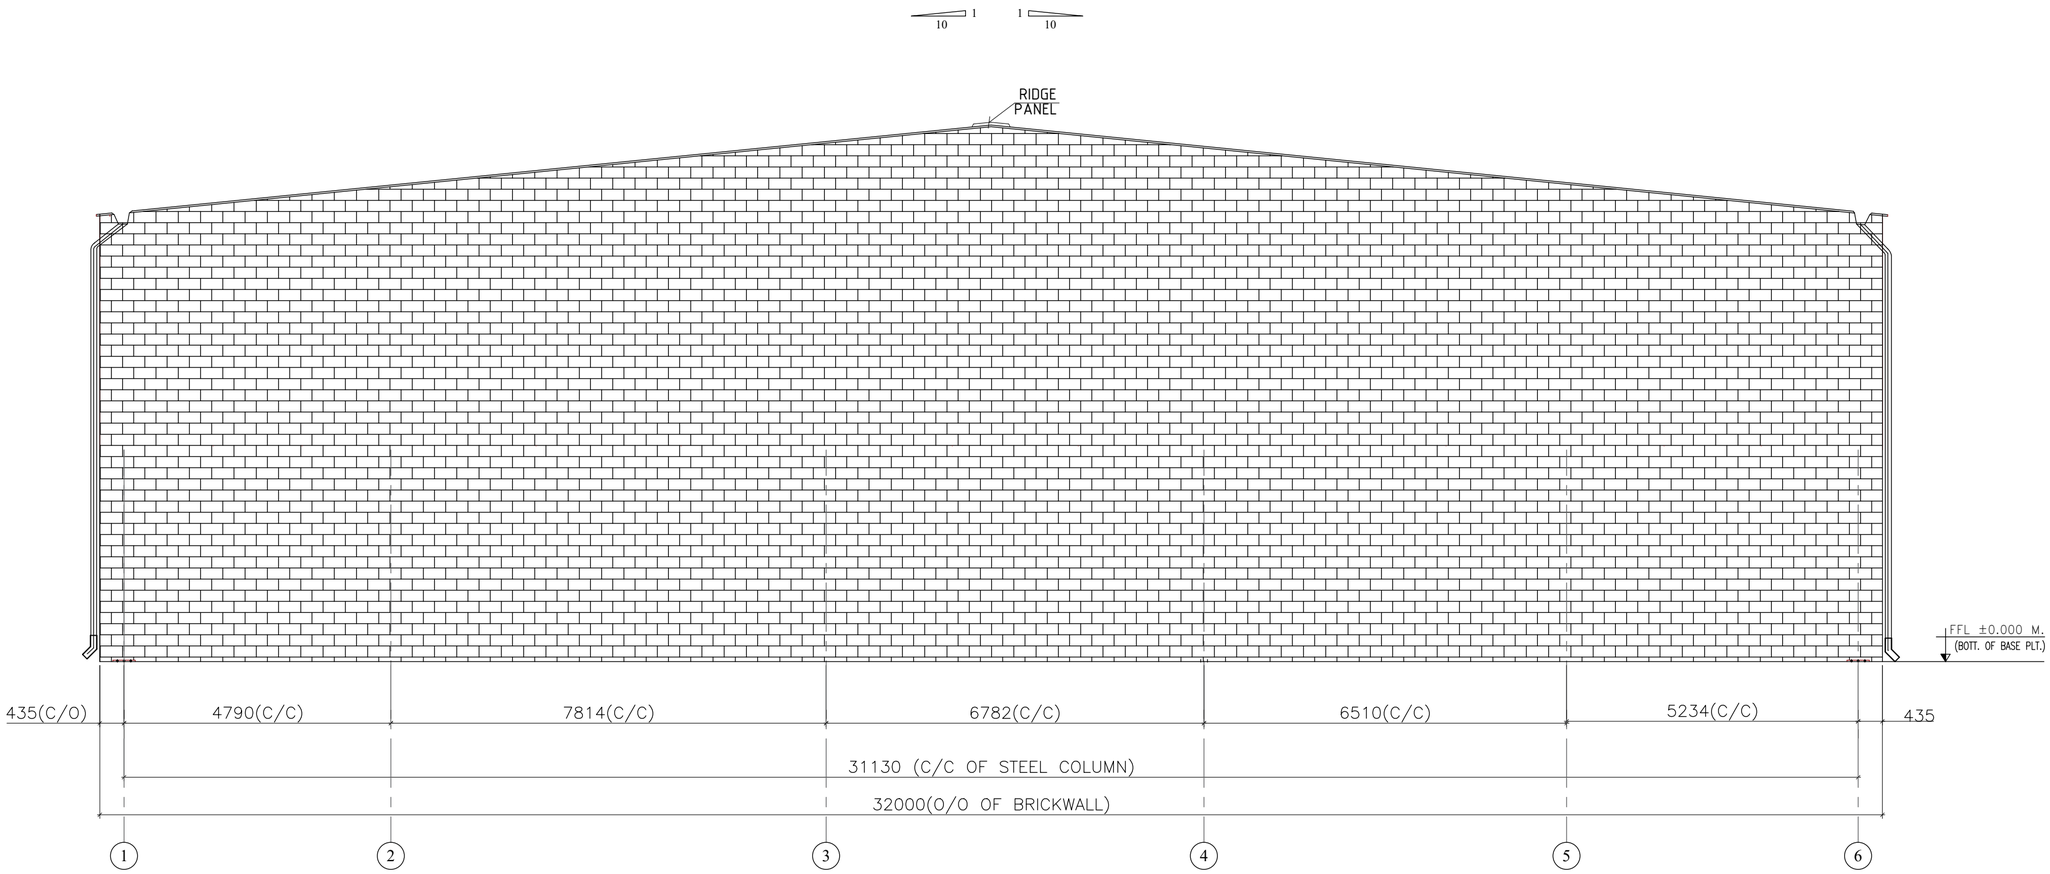

ENDWALL ELEVATION

(FOR FRAME LINE A)

SWARAJYA STEEL BUILDING
WE BUILD BEST ...


ALL UNITS ARE IN MM & KGS.
DO NOT SCALE THE DRAWING.

REV.	DATE	DESCRIPTION	DSN	DRN	CKD
		ISSUED FOR APPROVAL	AP	PW	AP
00	18-06-2026	ISSUED FOR APPROVAL	AP	PW	AP


PROJECT No.	: SSB-J-2603
ASP JOB No.	: J-285
PROJECT NAME	: JHUNJHUNU AIRPORT
CLIENT NAME	: M/S VS INFRA VENTURES
COMPANY NAME	: AIR GLOBE AVIATION SCHOOL
JOB SITE LOCATION	: MIRA ROAD

ENDWALL SHEETING ELEVATION

DWG. No.
GA-09

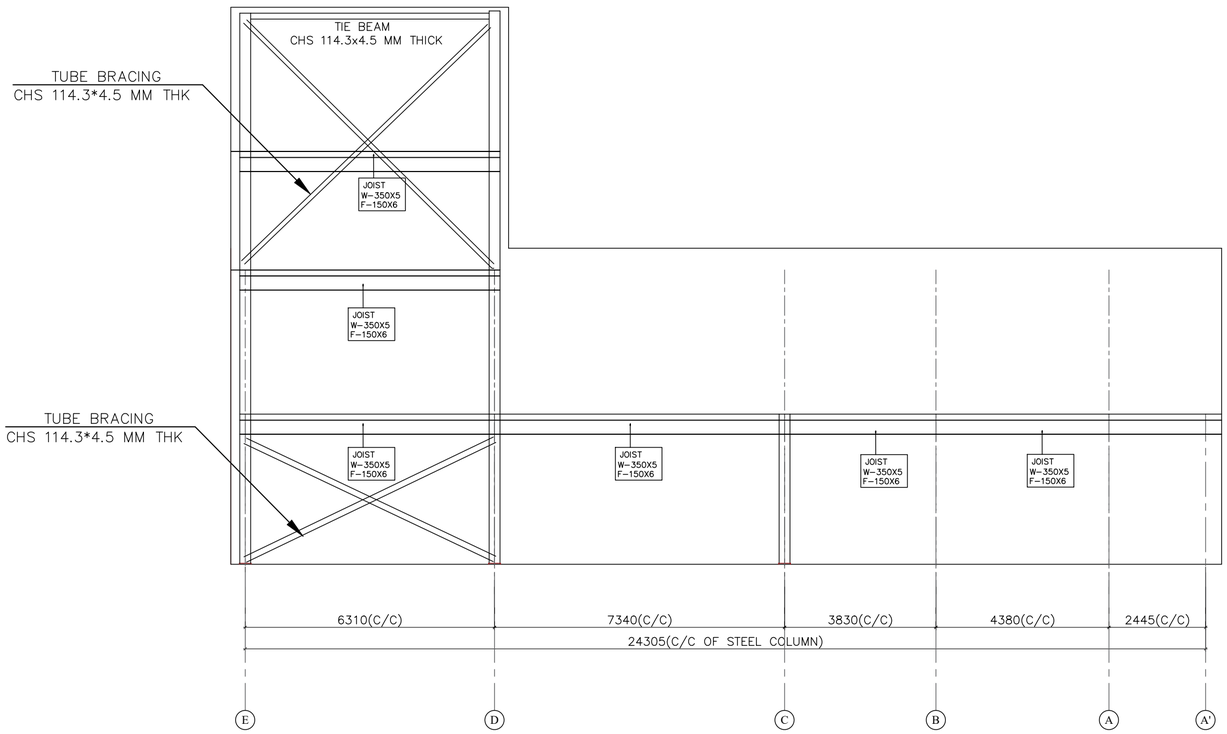

SIDEWALL BRACING ELEVATION @ GRID LINE – 11

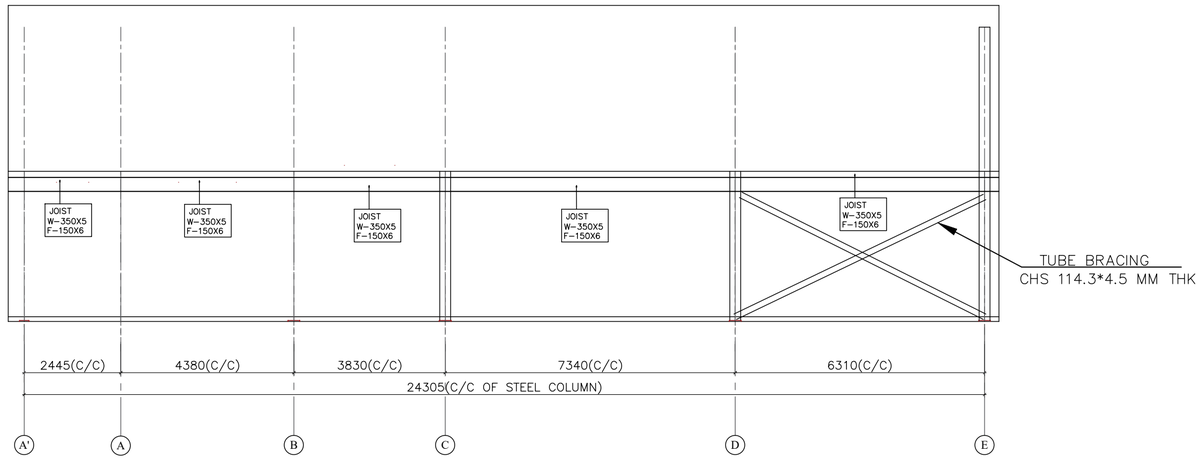

SIDEWALL FRAMING AND BRACING ELEVATION @ GRID LINE – 12

SWARAJYA STEEL BUILDING
WE BUILD BEST ...


ALL UNITS ARE IN MM & KGS.
DO NOT SCALE THE DRAWING.

REV.	DATE	DESCRIPTION	DSN	DRN	CKD
		ISSUED FOR APPROVAL	AP	PW	AP
00	18-06-2026	ISSUED FOR APPROVAL	AP	PW	AP


PROJECT No.	: SSB-J-2603
ASP JOB No.	: J-285
PROJECT NAME	: JHUNJHUNU AIRPORT
CLIENT NAME	: M/S VS INFRA VENTURES
COMPANY NAME	: AIR GLOBE AVIATION SCHOOL
JOB SITE LOCATION	: MIRA ROAD

SIDEWALL BRACING ELEVATION

DWG. No.
GA-15

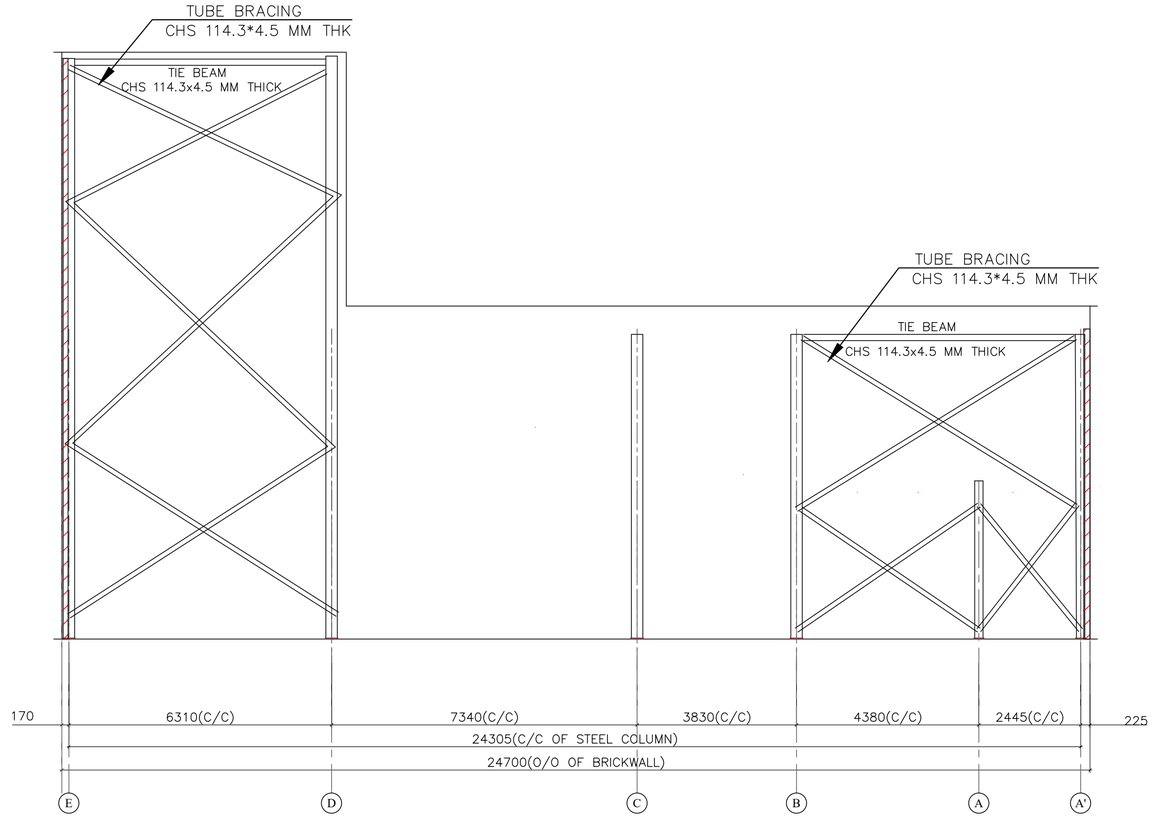

SIDEWALL FRAMING AND BRACING ELEVATION @ GRID LINE – 1

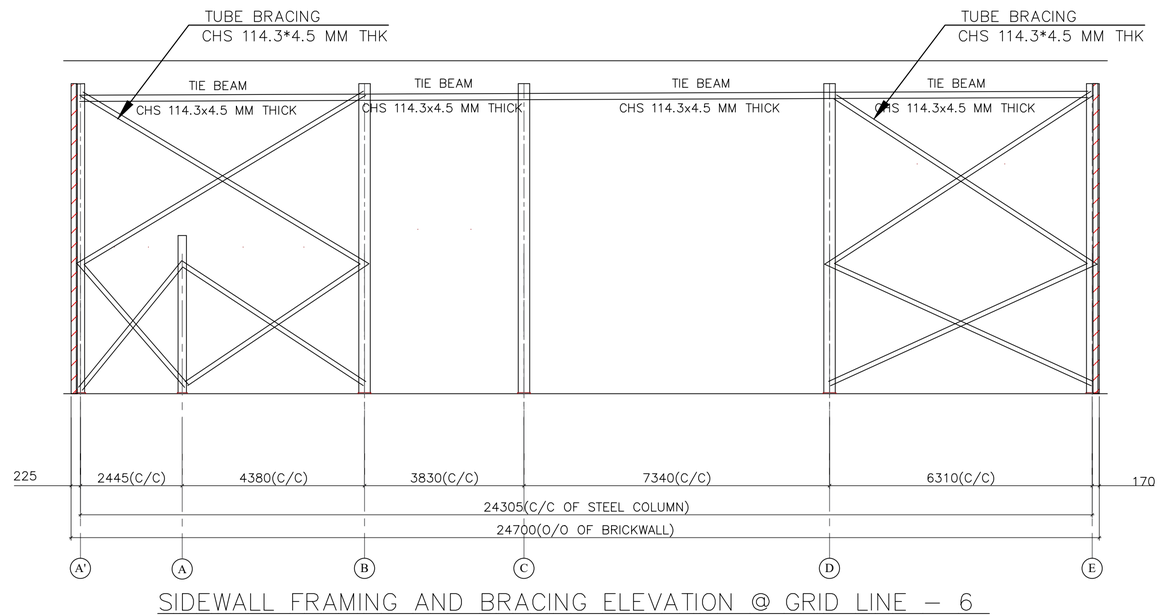

SIDEWALL FRAMING AND BRACING ELEVATION @ GRID LINE – 6

SWARAJYA STEEL BUILDING
WE BUILD BEST ...


ALL UNITS ARE IN MM & KGS.
DO NOT SCALE THE DRAWING.

REV	DATE	DESCRIPTION	DSN	DRN	CKD
		ISSUED FOR APPROVAL	AP	PN	AP
00	18-06-2026	ISSUED FOR APPROVAL	AP	PN	AP


PROJECT No.	: SSB-J-2603
ASP JOB No.	: J-285
PROJECT NAME	: JHUNJHUNU AIRPORT
CLIENT NAME	: M/S VS INFRA VENTURES
COMPANY NAME	: AIR GLOBE AVIATION SCHOOL
JOB SITE LOCATION	: MIRA ROAD

SIDEWALL FRAMING SECTION

DWG. No.
GA-16

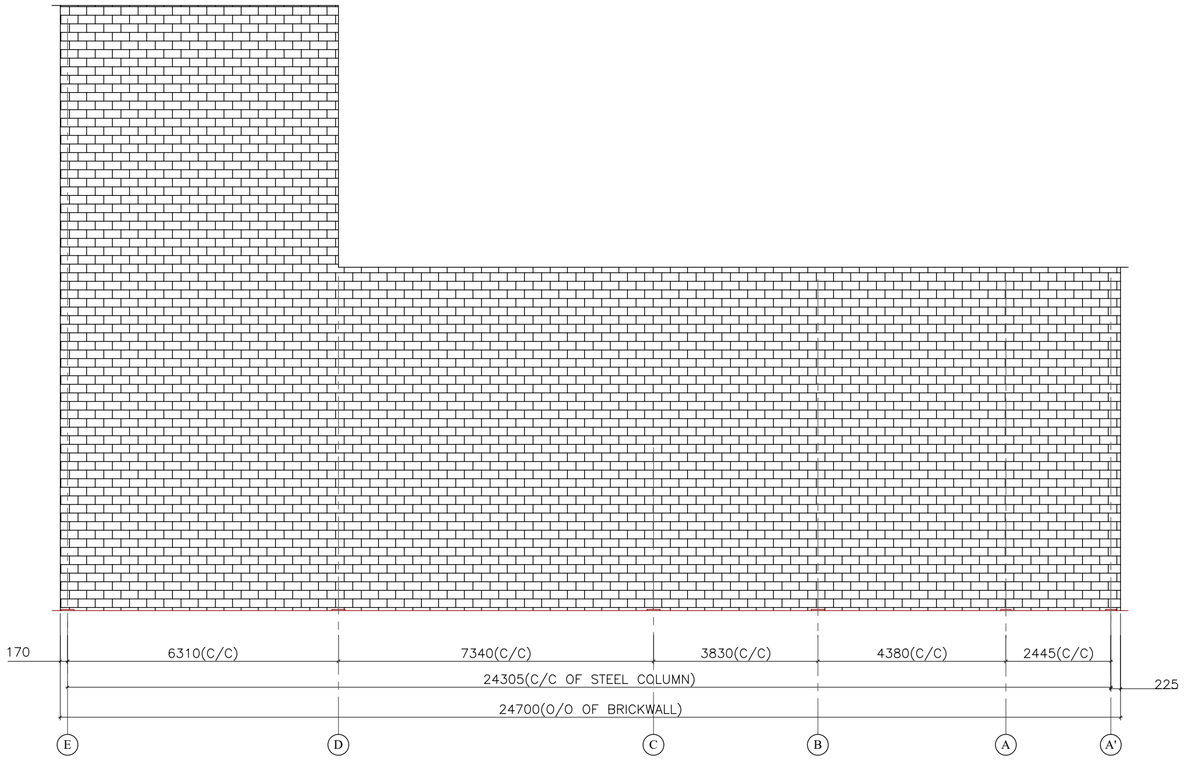

SIDEWALL ELEVATION @ GRID LINE – 1

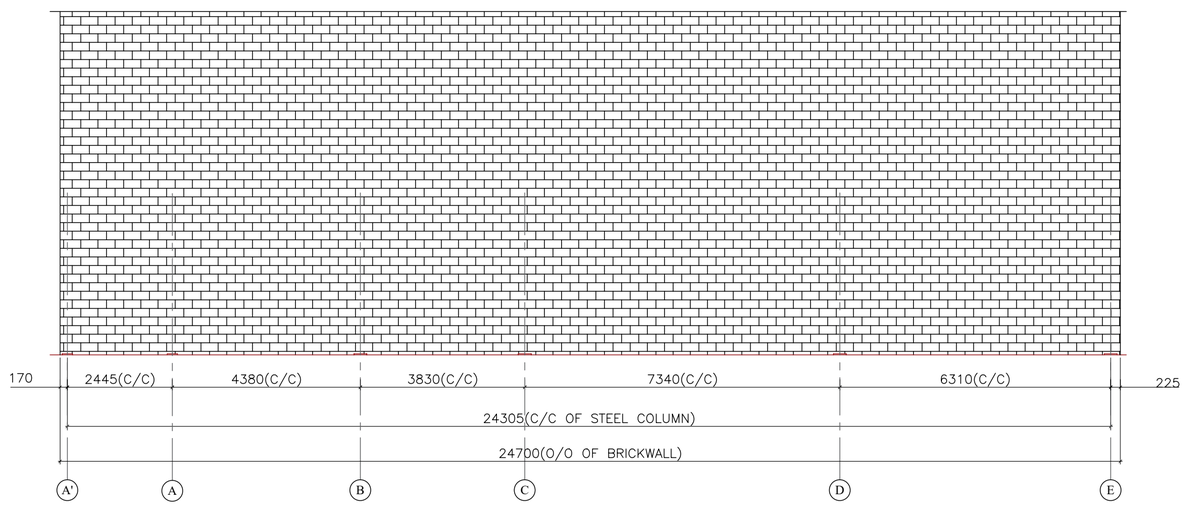

SIDEWALL ELEVATION @ GRID LINE – 6

SWARAJYA STEEL BUILDING
WE BUILD BEST ...


ALL UNITS ARE IN MM & KGS.
DO NOT SCALE THE DRAWING.

REV.	DATE	DESCRIPTION	DSN	DRN	CKD
		ISSUED FOR APPROVAL	AP	PW	AP
00	18-06-2026	ISSUED FOR APPROVAL	AP	PW	AP


PROJECT No.	: SSB-J-2603
ASP JOB No.	: J-285
PROJECT NAME	: JHUNJHUNU AIRPORT
CLIENT NAME	: M/S. VS INFRA VENTURES
COMPANY NAME	: AIR GLOBE AVIATION SCHOOL
JOB SITE LOCATION	: MIRA ROAD

SIDEWALL SHEETING ELEVATION


DWG. No.
GA-17

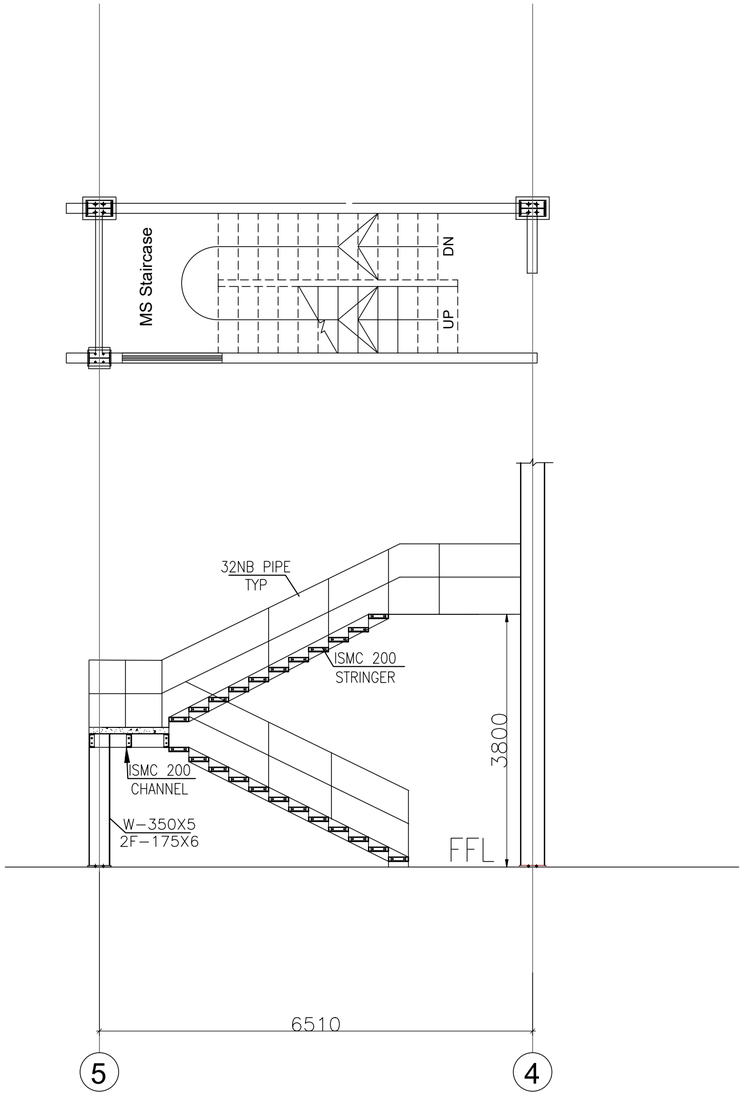


STAIRCASE 1 DEATIL

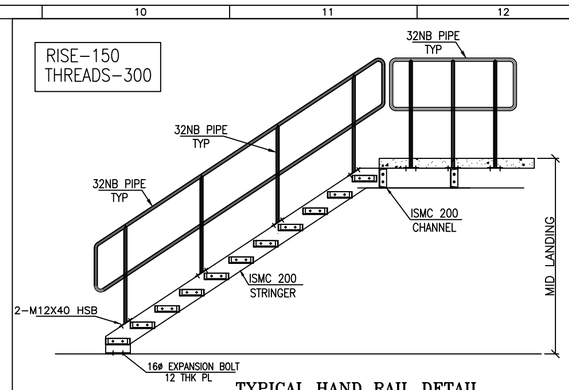


TYPICAL HAND RAIL DETAIL
NTS

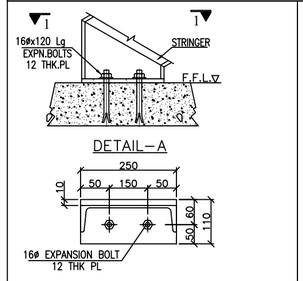


SECTION 1-1

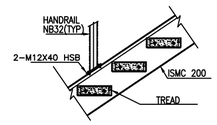

TYPICAL TREAD DETAIL
DETAIL-B

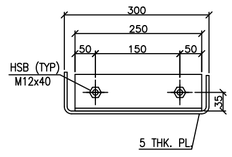

SINGLE TREAD DETAIL

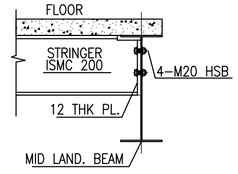


STRINGER TO MID LAND. BEAM CONN.

SWARAJYA STEEL BUILDING
WE BUILD BEST ...


ALL UNITS ARE IN MM & KGS.
DO NOT SCALE THE DRAWING.

REV	DATE	DESCRIPTION	DSN	DRN	CKD
		ISSUED FOR APPROVAL	AP	PW	AP
00	18-06-2026	ISSUED FOR APPROVAL	AP	PW	AP


PROJECT No.	: SSB-J-2603
ASP JOB No.	: J-285
PROJECT NAME	: JHUNJHUNU AIRPORT
CLIENT NAME	: M/S VS INFRA VENTURES
COMPANY NAME	: AIR GLOBE AVIATION SCHOOL
JOB SITE LOCATION	: MIRA ROAD
STAIRCASE DETAIL	DWG. No. GA-18

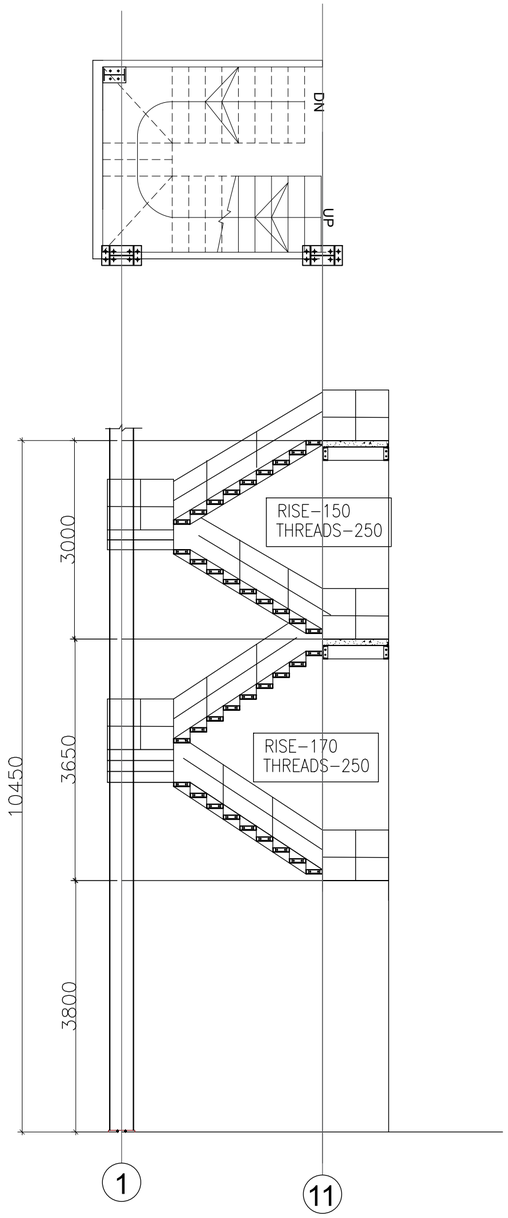


STAIRCASE 2 DEATIL

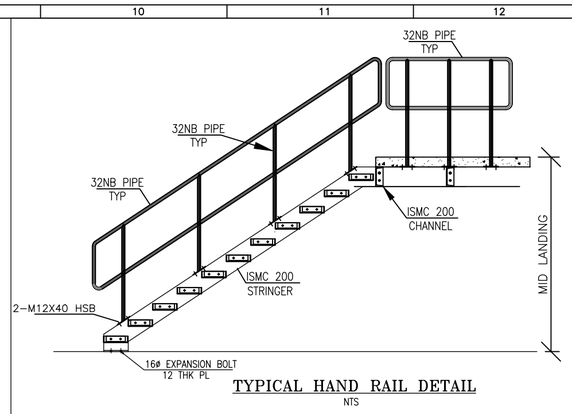


TYPICAL HAND RAIL DETAIL
NTS

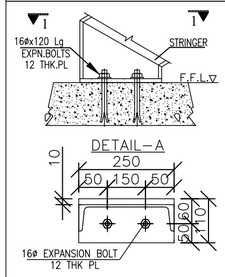


SECTION 1-1

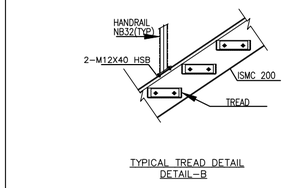

TYPICAL TREAD DETAIL
DETAIL-B

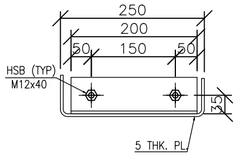

SINGLE TREAD DETAIL

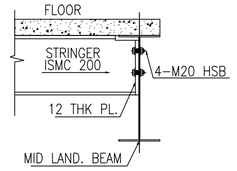

STRINGER TO MID LAND. BEAM CONN.

SWARAJYA STEEL BUILDING
WE BUILD BEST ...

ALL UNITS ARE IN MM & KGS.
DO NOT SCALE THE DRAWING.

REV.	DATE	DESCRIPTION	DSN	DRN	CKD
		ISSUED FOR APPROVAL	AP	PW	AP
00	18-06-2025	ISSUED FOR APPROVAL	AP	PW	AP

PROJECT No.	: SSB-J-2603
ASP JOB No.	: J-285
PROJECT NAME	: JHUNJHUNU AIRPORT
CLIENT NAME	: M/S VS INFRA VENTURES
COMPANY NAME	: AIR GLOBE AVIATION SCHOOL
JOB SITE LOCATION	: MIRA ROAD
STAIRCASE DETAIL	DWG. No. GA-19