

Abbrevation's:
WOW-Wall Opening Width
WOH-Wall Opening Height
CH- Clear Height
UC-Under Cut
FFL-Finished Floor Level

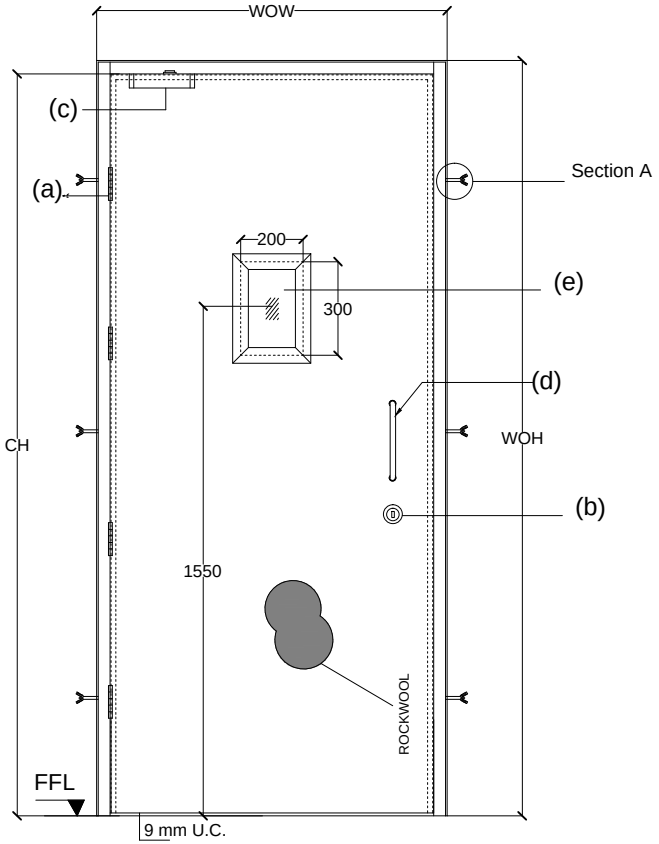

ELEVATION



TOP VIEW

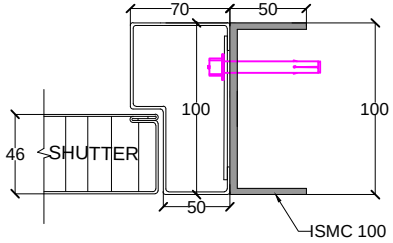

ASSESORIES DETALES

(a) HINGES: DORMA SS hinges 4"x3"x3mm

(b) LOCK : Mortise Dead Lock ML 112-Dorset with cylinder (One side key & other side turn bolt on Rose SSDORSET-CL 204) with escutcheon.

(c) DOOR CLOSER.

(d) HANDLE : D Handle (300x22) pair.

(e) VISION PANEL - 5mm THK. GLASS OF SIZE-200X300mm

Shutter thickness : 46 mm
Frame Sheet thick : 1.5mm
Shutter sheet thick : 1.2mm
Fixing : On MS Structure ISMC100 bolts.

NOTE:- *All Dimensions are in mm.
*Tolerance:-All Linear Dimensions ±3mm,Others ±0.5mm.
*The Drawing Is For Location of Hardware only. Drawing Does Not Represent The Hardware For More Clarity, Please Go Through Hardware Broucher.

Fire door size

WOW	WOH	TYPE 1	TYPE 2	TYPE 3	TYPE 4	QUANTITY
1200	2100					14

REV NO	DATE	DESCRIPTION
REV -0	18/11/17	INITIAL DRAWING
REV -1	25/11/17	DOOR WILL BE INSTALLED ON MS STRUCTURE INSTEAD OF BRICK WALL.

COLOR:-
1.TRAFFIC WHITE:-RAL9016
2.LIGHT GREY:- RAL7035
3.Gentian Blue:- RAL5010
4.Signal Red:-RAL3001

NOTE- CLIENT SHOULD SELECT DOOR TYPE FROM DOOR HANDLING SHEET & COLOR OF DOOR.

This drawing & designing is the property of NIHVA TECHNOLOGIES. Not to be sold or copied to any other concern.

TITLE: 2HRS FIRE RATED STEEL DOOR

	SIGN	DATE
DRAWN	SURAJ.	18/11/17
CHECK	OMKAR	18/11/17
APPROVAL	SHEKHAR	18/11/17
MFG.		

If any queries contact : projects@nihva.com

ALL DIMENSION ARE IN mm

NIHVA TECHNOLOGIES PVT. LTD.
NIHVA TECHNOLOGIES PVT. LTD. PUNE
Tel : 020 66304033
Email:- info@nihva.com
Website:- www.nihva.com

CLIENT- MITTTAL PRECISION HITECH STEEL PVT LTD
PROJECT -
SITE - KHED,PUNE.
DWG. NO. : NIHVA/17-18/0282/R01 | REV. : 1
SCALE: NTS | WT: | SHEET: 01 OF 01