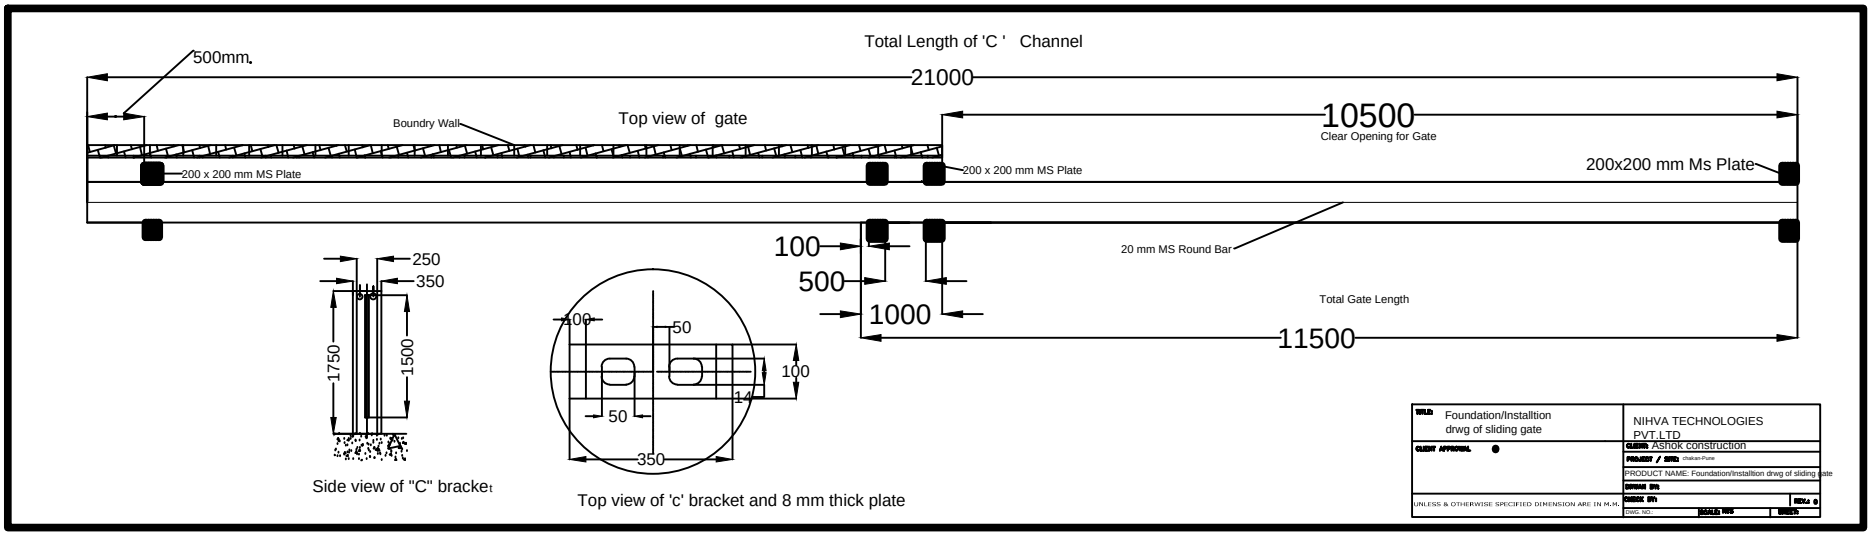
Total Length of 'C ' Channel
500mm.
21000
Boundry Wall
Top view of gate
10500
Clear Opening for Gate
200 x 200 mm MS Plate
200 x 200 mm MS Plate
200x200 mm Ms Plate
20 mm MS Round Bar
100
500
1000
Total Gate Length
11500
250
350
1750
1500
100
50
100
14
50
350
Side view of "C" bracket
Top view of 'c' bracket and 8 mm thick plate
Foundation/Installtion drwg of sliding gate
NIHVA TECHNOLOGIES PVT.LTD
Ashok construction
PRODUCT NAME: Foundation/Installtion drwg of sliding gate
UNLESS & OTHERWISE SPECIFIED DIMENSION ARE IN M.M.