

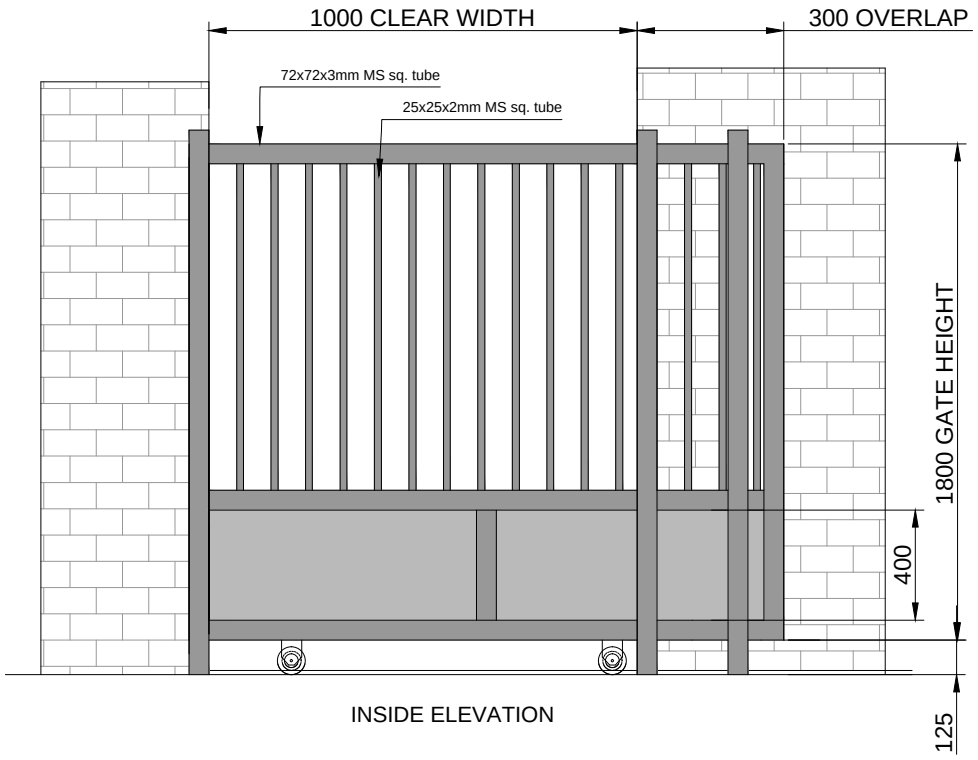



INSIDE ELEVATION

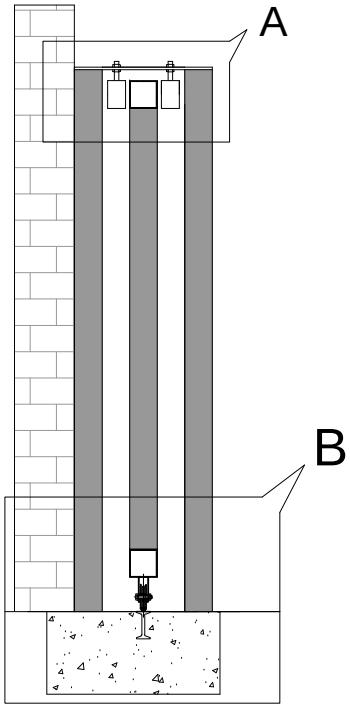


SIDE VIEW

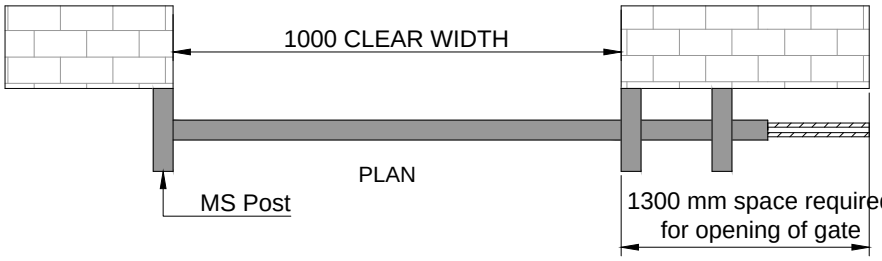

PLAN

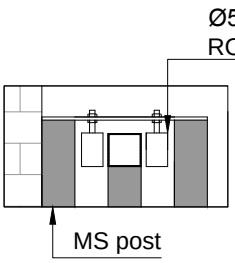

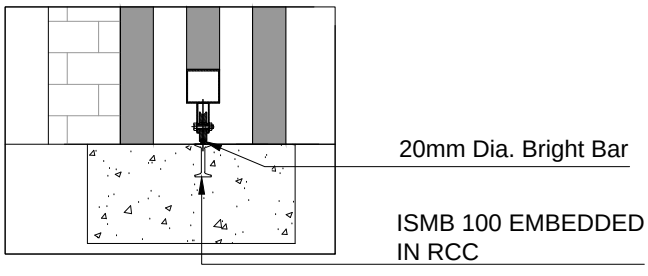

This drawing & designing is the property of NIHVA TECHNOLOGIES. Not to be sold or copied to any other concern.

TITLE

SINGLE LEAF SLIDING GATE (MANUAL)

CLIENT APPROVAL

ALL DIMENSION ARE IN mm

	SIGN	DATE
DRAWN	OMKAR	14/03/17
CHECK	SAGAR P.	14/03/17
REV.		
APPRD.	R.K.	14/03/17
MFG		
Ref. No.		

NIHVA TECHNOLOGIES PVT. LTD.

NIHVA TECHNOLOGIES PVT. LTD. PUNE
Tel : 020 66304033
Email:- info@nihva.com
Website:- www.nihva.com

CLIENT - SHIMZU CORPORATION INDIA PVT.LTD.

PROJECT - GSK

SITE - KOLAR, KARNATAKA

DWG. NO. - NIHVA/16-17/182

SCALE: NTS | WT: | SHEET: 01 OF 01

If any queries contact : projects@nihva.com