
NW N NE

W E

SW S SE

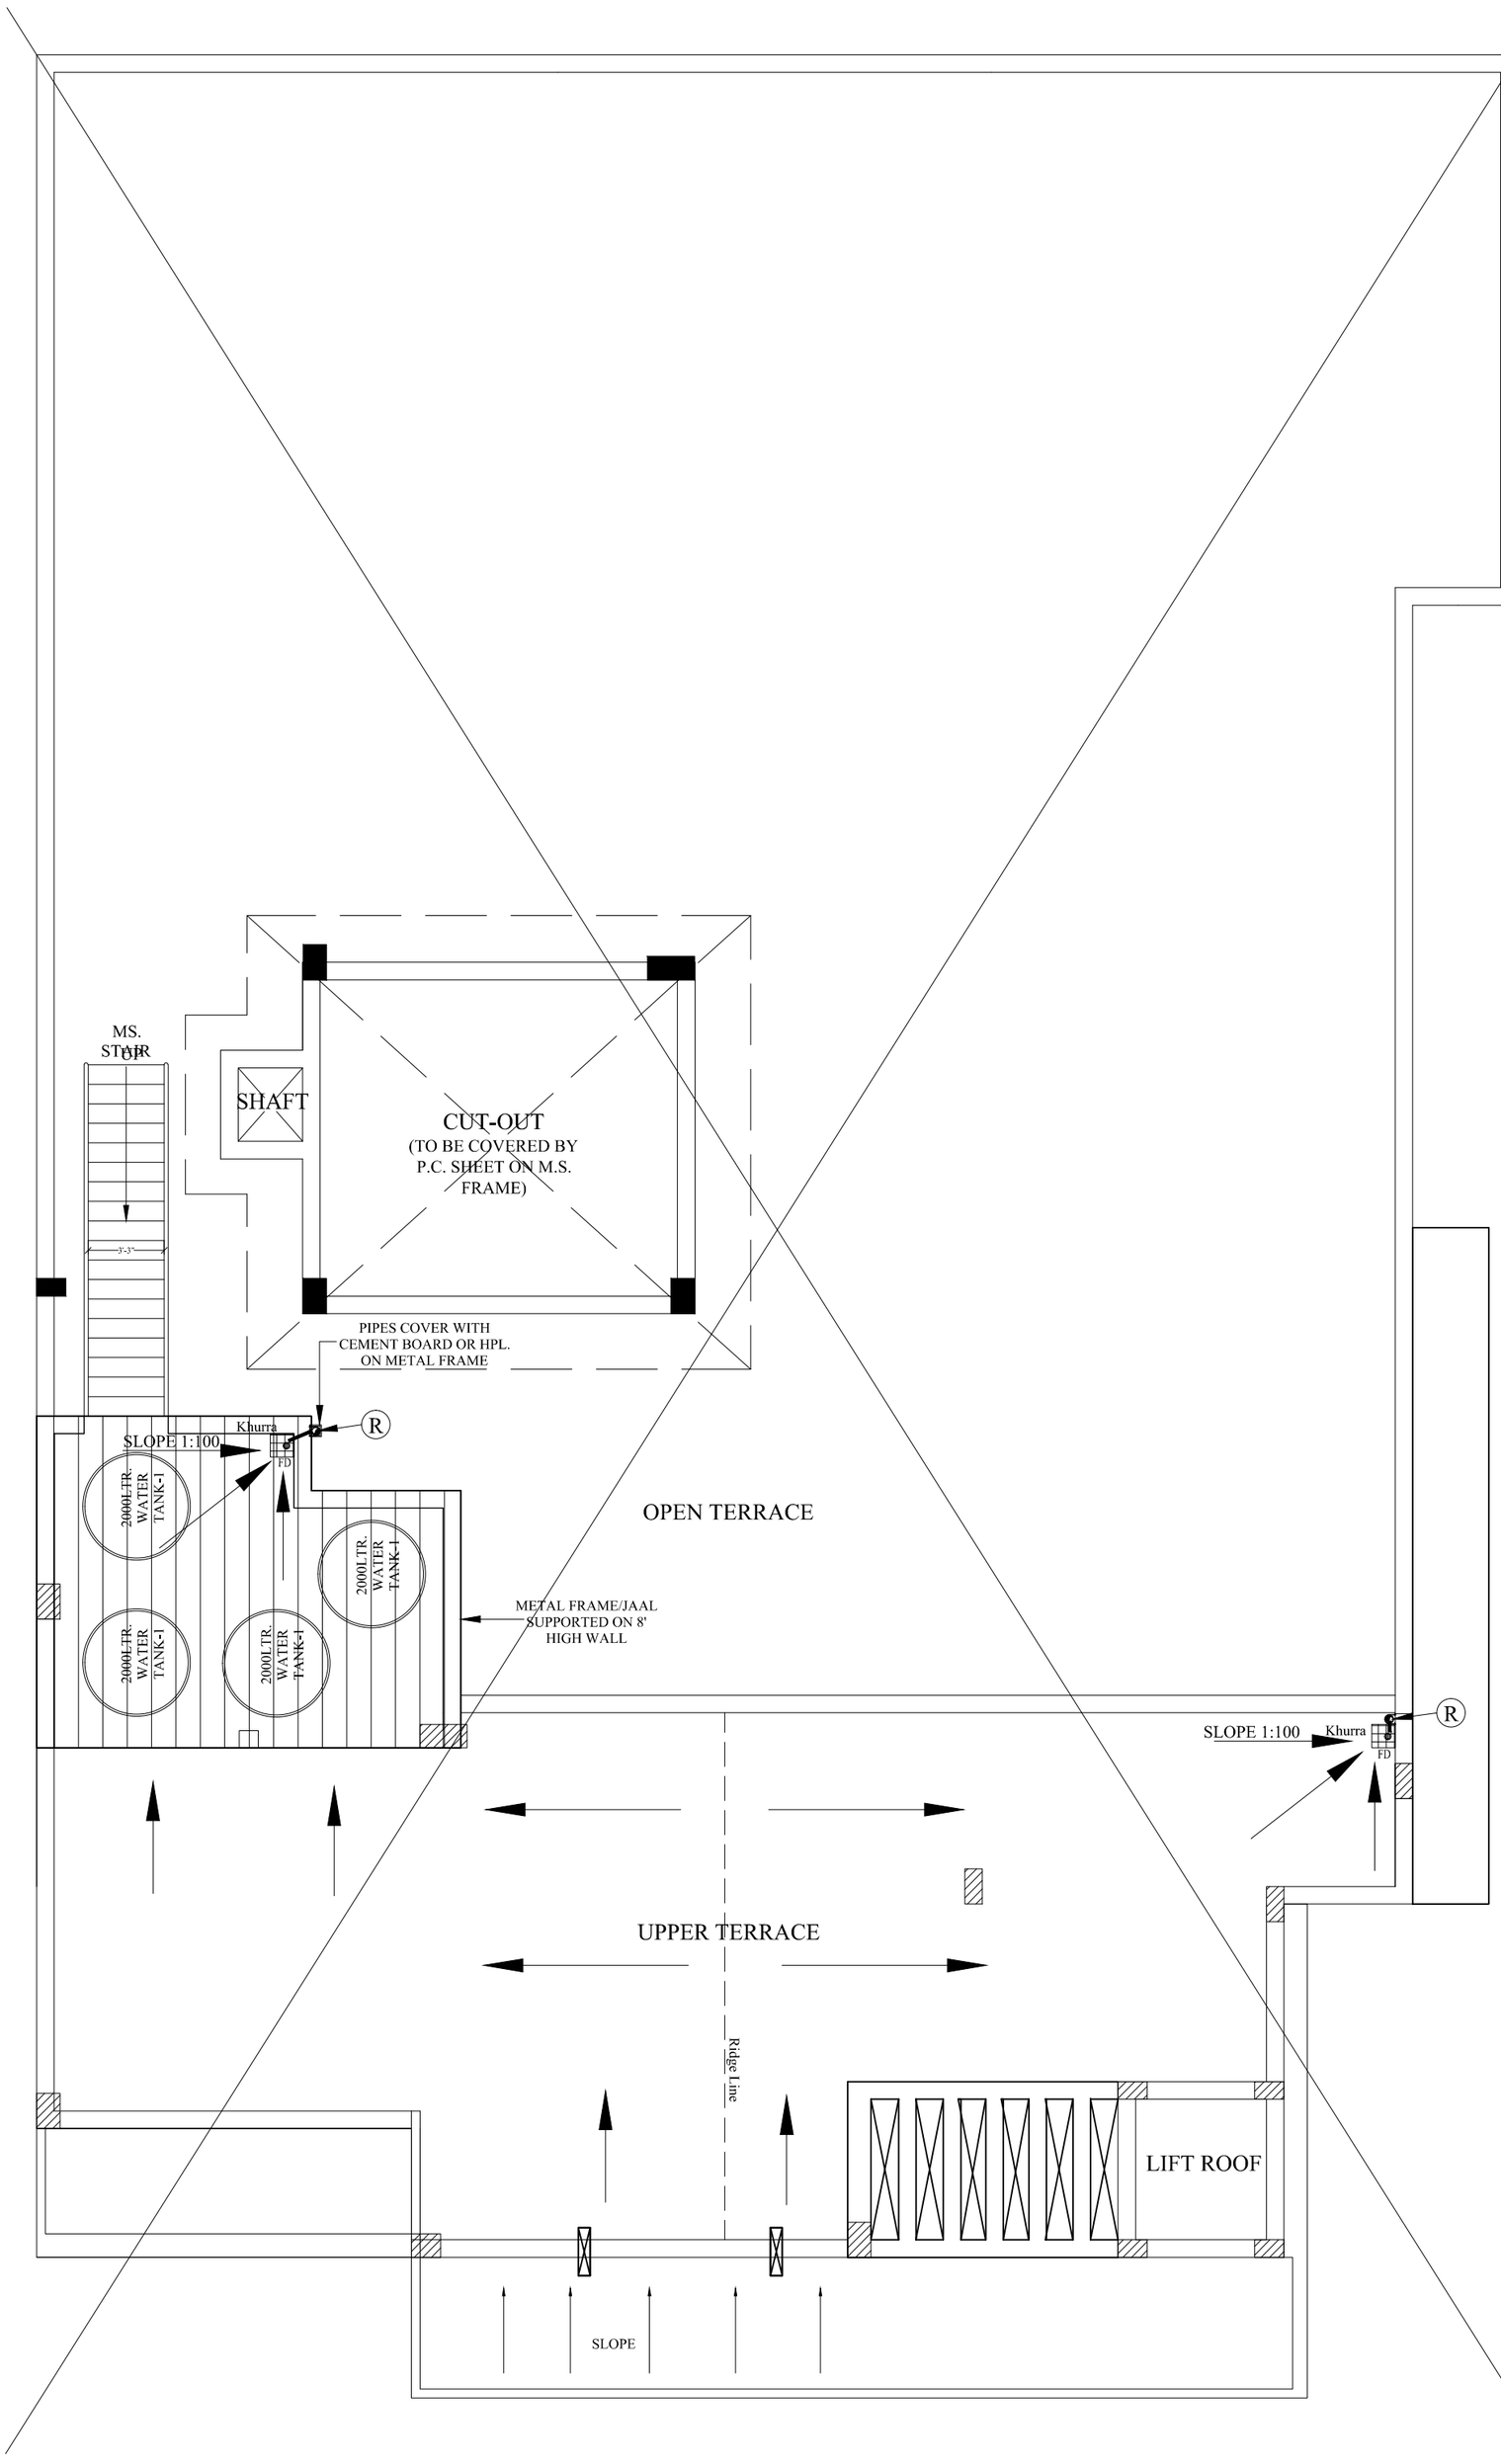

SCHEDULE OF PIPES

LEGEND	DESCRIPTION
Ⓢ	110 OD uPVC SOIL & VENT PIPE
Ⓦ	110 OD uPVC WASTE & VENT PIPE
Ⓡ	110 OD uPVC WASTE & VENT PIPE
Ⓓ	DRINKING WATER SUPPLY

PIPE DIA:

1.	WASH BASIN TO FLOOR DRAIN (FD) 40 OD PIPE.
2.	KITCHEN SINK TO FLOOR TRAP (FT) 40 OD PIPE.
3.	FLOOR DRAIN (FD) TO FLOOR TRAP (FT) 50 OD UPVC WASTE PIPE.
4.	FLOOR TRAP (FT) TO VERTICAL PIPE 110 OD UPVC WASTE PIPE.
5.	FLOOR DRAIN (FD) TO FLOOR TRAP (FT) 50 OD UPVC WASTE PIPE.
6.	(BT) BOTTLE TRAP
☒	150X150mm CUTOUT FOR W.C
☒	150X150mm CUTOUT FOR FLOOR TRAP
☒	150X150mm CUTOUT FOR FLOOR DRAIN
☒	150X150mm CUTOUT FOR BALCONY DRAIN

ARCHITECTS AND CONSULTANTS

AE STUDIO

an architectural design studio

B4/225, GREEN PARK EXT.,
NEW DELHI-110016 , Ph.- 011 47350369
E-Mail : info@aestudio.in , Web.: www.aestudio.in

THIS DRAWING IS A "COPYRIGHT" OF THE ARCHITECT AND SHOULD NOT BE CHANGED, COPIED, REPRODUCED OR USED FOR ANY OTHER PURPOSE OR PROJECT OTHER THAN FOR WHICH IT IS ISSUED WITHOUT THE WRITTEN CONCENT OF THE ARCHITECT

NOTES -
1. READ THIS DRAWING IN CONJUNCTION WITH OTHER DRAWINGS FOR THIS PROJECT.
2. DO NOT SCALE THIS DRAWING, ONLY WRITTEN DIMENSIONS ARE TO BE FOLLOWED.
3. DISCREPANCY IF ANY MUST BE BROUGHT TO THE NOTICE OF THE ARCHITECT IMMEDIATELY.
4. ALL THE DIMENSIONS HAS TO BE TAKEN FROM FINISH FLOOR LEVEL

CLIENT: MR. DHAMIJA

PROJECT: DHAMIJA RESIDENCE

DRAWING TILTLE: SECOND FLOOR PLUMBING LAYOUT

BUILDING BLOCK/FLOOR:

S.NO.	DATE	DRAWN BY	REVISION / COMMENTS

PROJECT NO.: 271

DRAWN BY: KUSH

CHECKED BY: SANDEEP

SCALE: N.T.S.

DATE: 21/06/2021

DRAWING TYPE:

SHEET NO.: OF

DRAWING NAME.: FB_AR_(P-13,23,TERRACE).dwg

FILE LOCATION: Z:\RESIDENCE CIVIL\Original\FARIDABAD\DHAMIJA RESIDENCE (PROJECT NO 271)\SERVICES\FB_AR_(P-13,23,TERRACE)