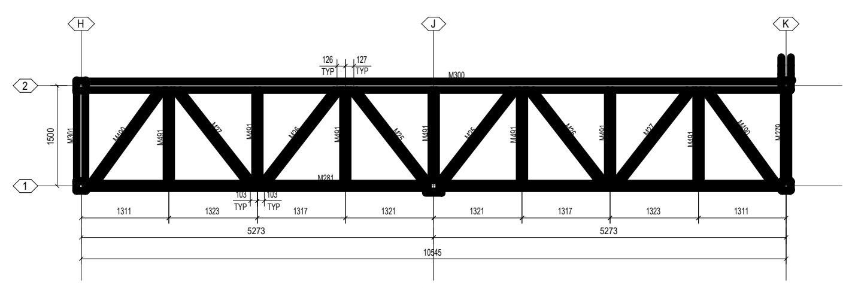

SECTION D - D
1:40

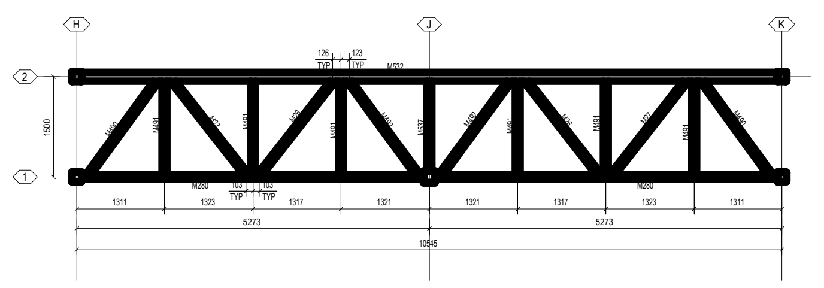

SECTION C - C
1:40

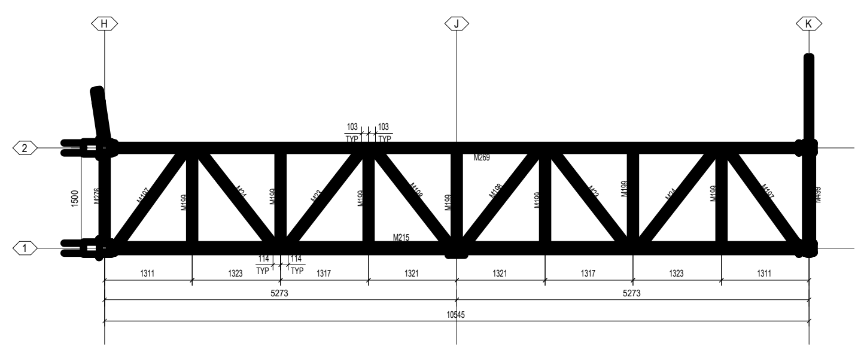

SECTION B - B
1:40

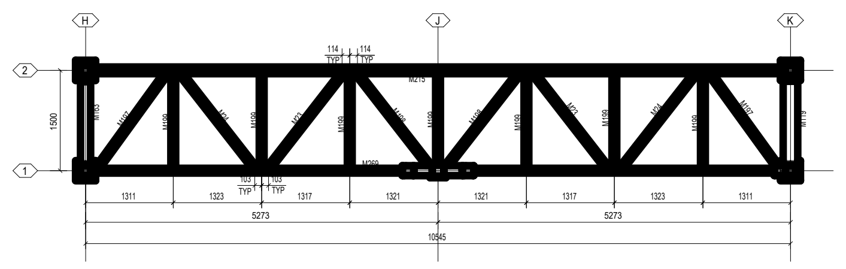

SECTION A - A
1:40

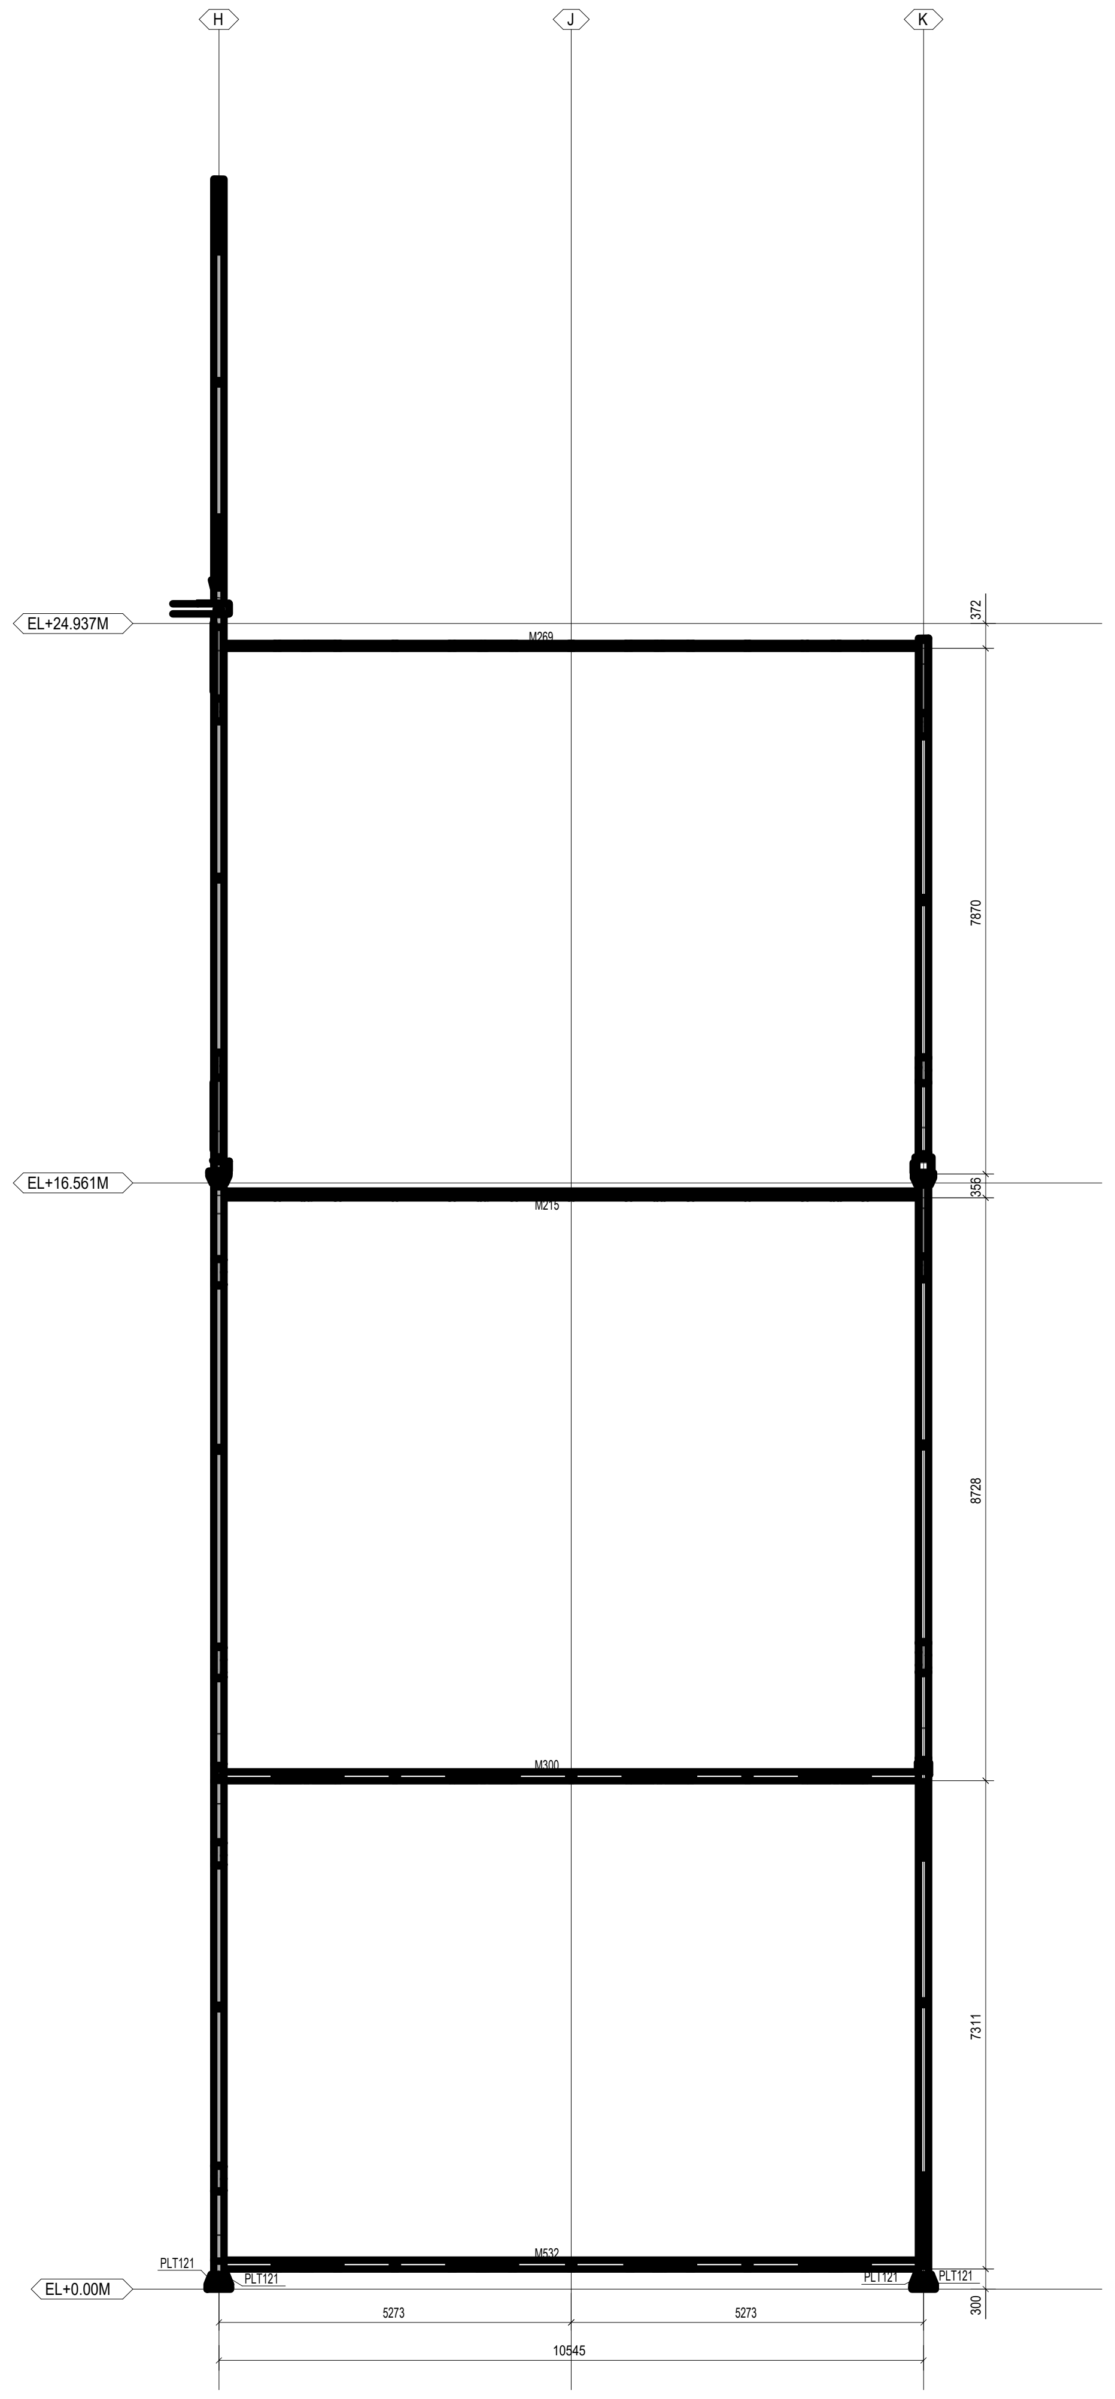

GRID @ 2
1:60

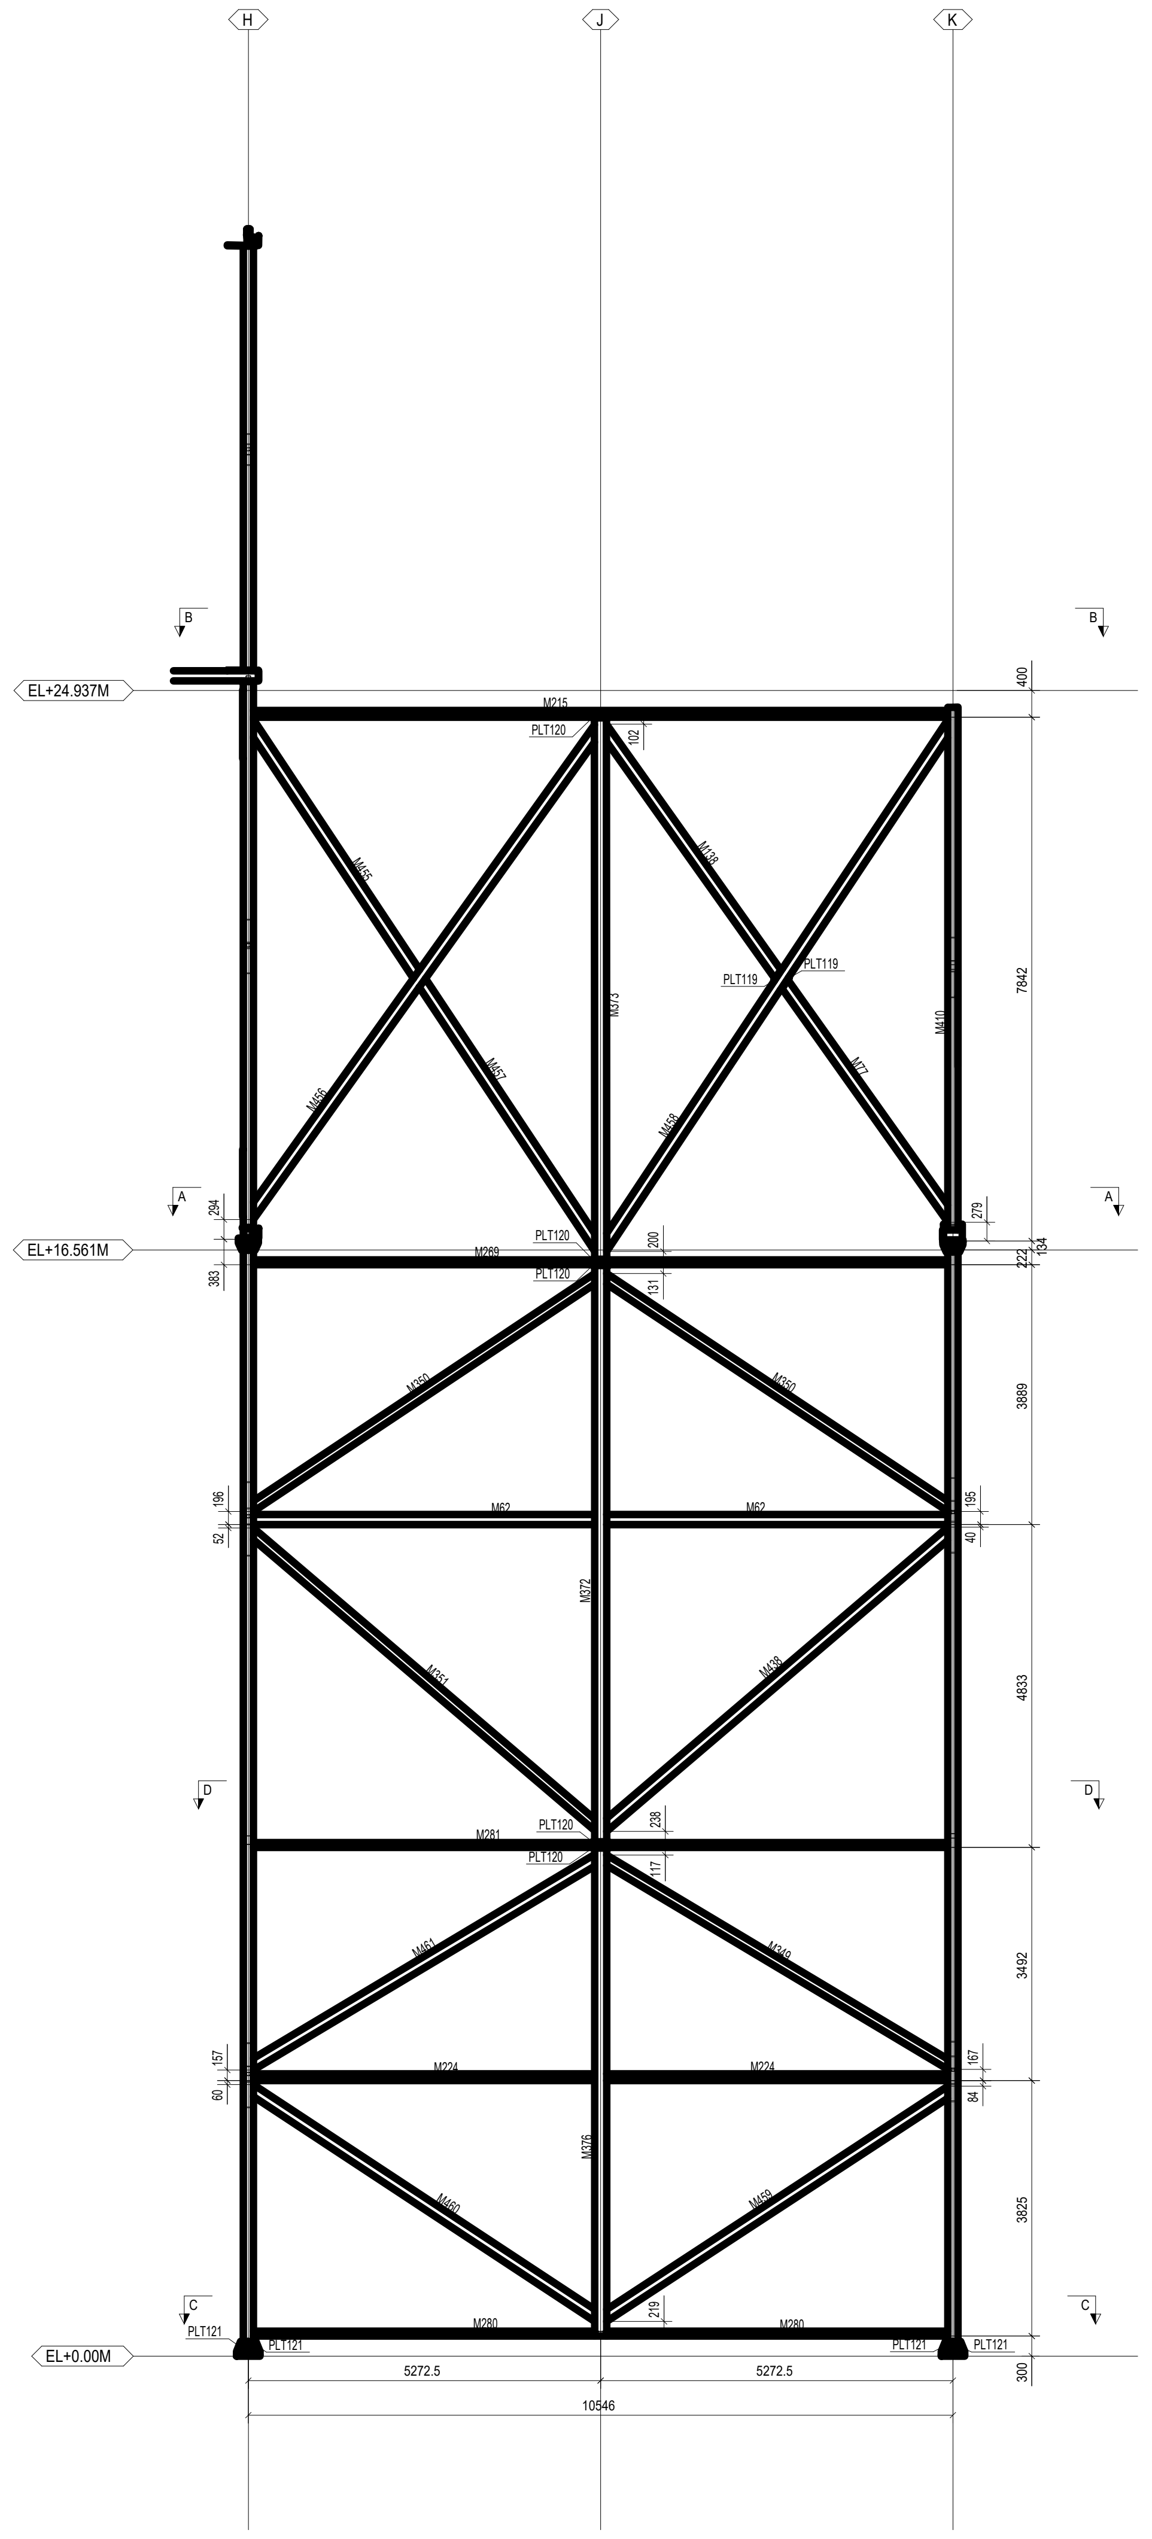

GRID @ 1
1:60

REV.NO.	DESCRIPTION.	REV.DATE	DRAWN.	CHKD.	APPD.
0	ISSUED FOR APPROVAL	05.11.22	IMS	HAB	HAB

DWG.TITLE :- DETAIL DRAWING FOR 84MTR

PROJECT	MEGADOOR INSTALLATION AT HYDRABAD AIRPORT
CLIENT	GMR

SALT DESIGN SERVICES

NIHVA TECHNOLOGIES
PVT. LTD. PUNE
Tel : 020 66304033
Email:- info@nihva.com
Website:- www.nihva.com

DRAWN :RRK	CHECKED : HAB	SCALE: 1:100
APPROVED : HAB	JOB CODE. : 1729	DATE: 05.11.2022

DWG.NO: SALT_1729_FDN_01_R0	(SH-1OF1)	REV. - R0 SIZE. - A1

A1 [841 x 594]