

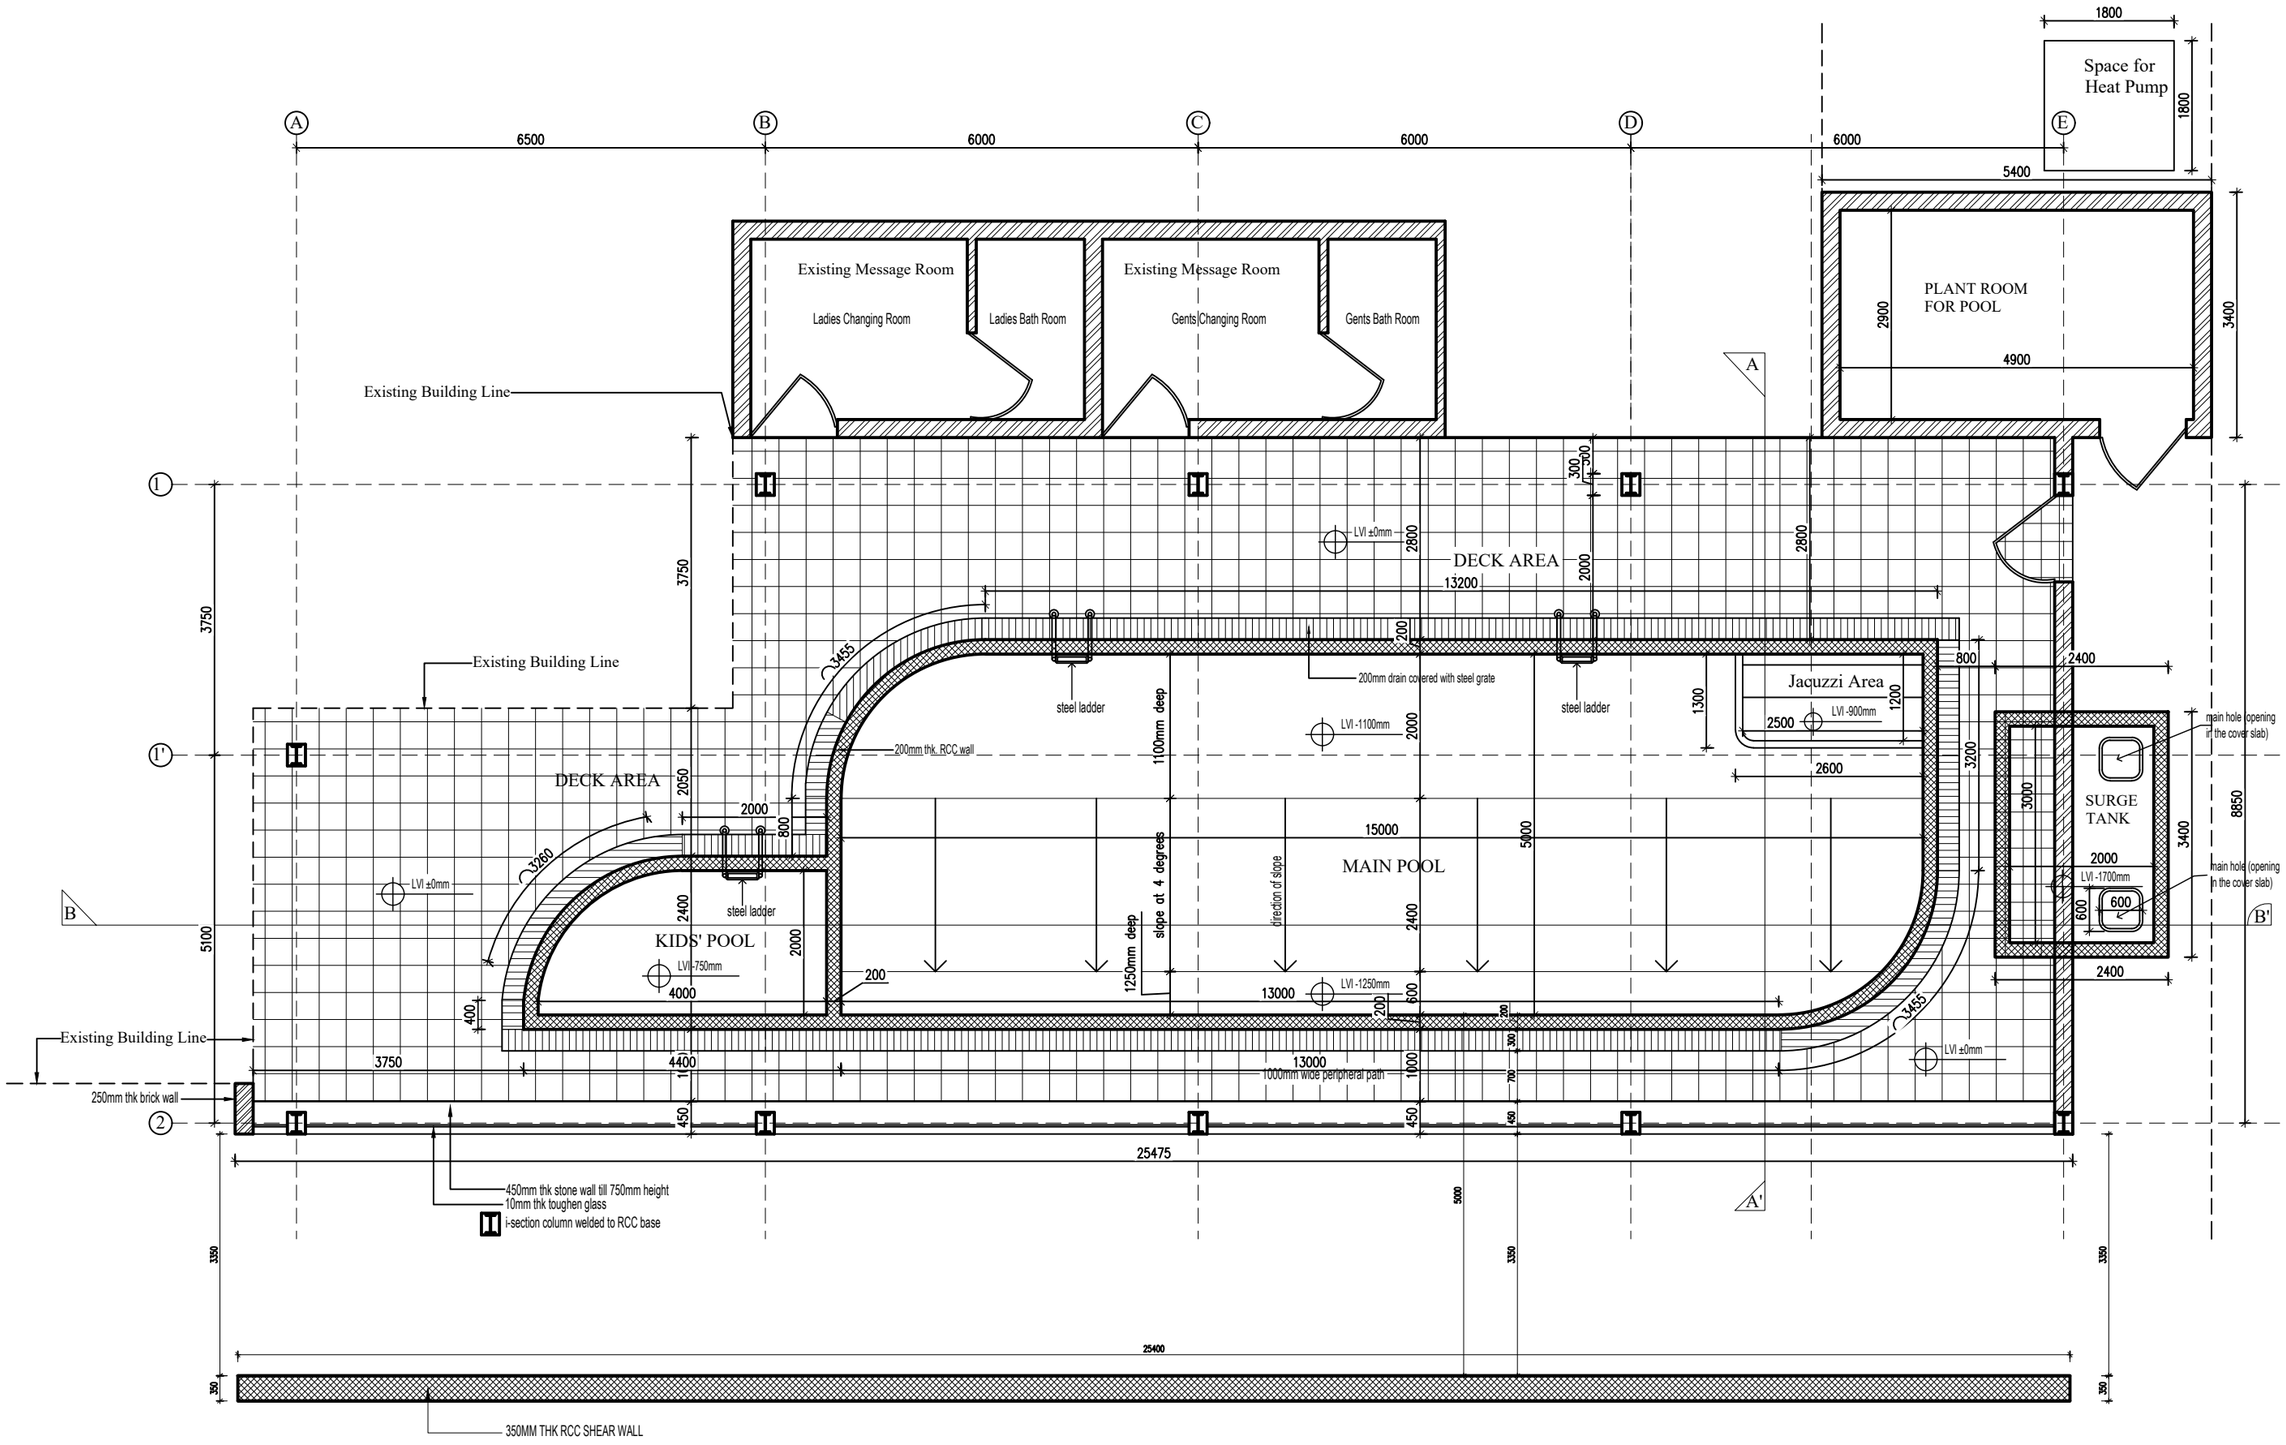


PROJECT: SWIMMING POOL FOR NAK-SEL BOUTIQUE HOTEL & SPA PVT LTD @ NGOBA VILLAGE, UNDER LAMGONG GEWOG, PARO	DRAWING TITLE: PLAN	ARCHITECT: RINCHEN DORJI	SCALE: 1:75 (ALL DIMENSIONS IN MM)	OWNER: CID NO.: SIGN:	SONAM WANGMO 11511002003	THRAM NO.: 119 PLOT NO.: LAM-3761 THRAM AREA: 0.78 ACRES	APPROVED BY:	DWG NO. AR-01

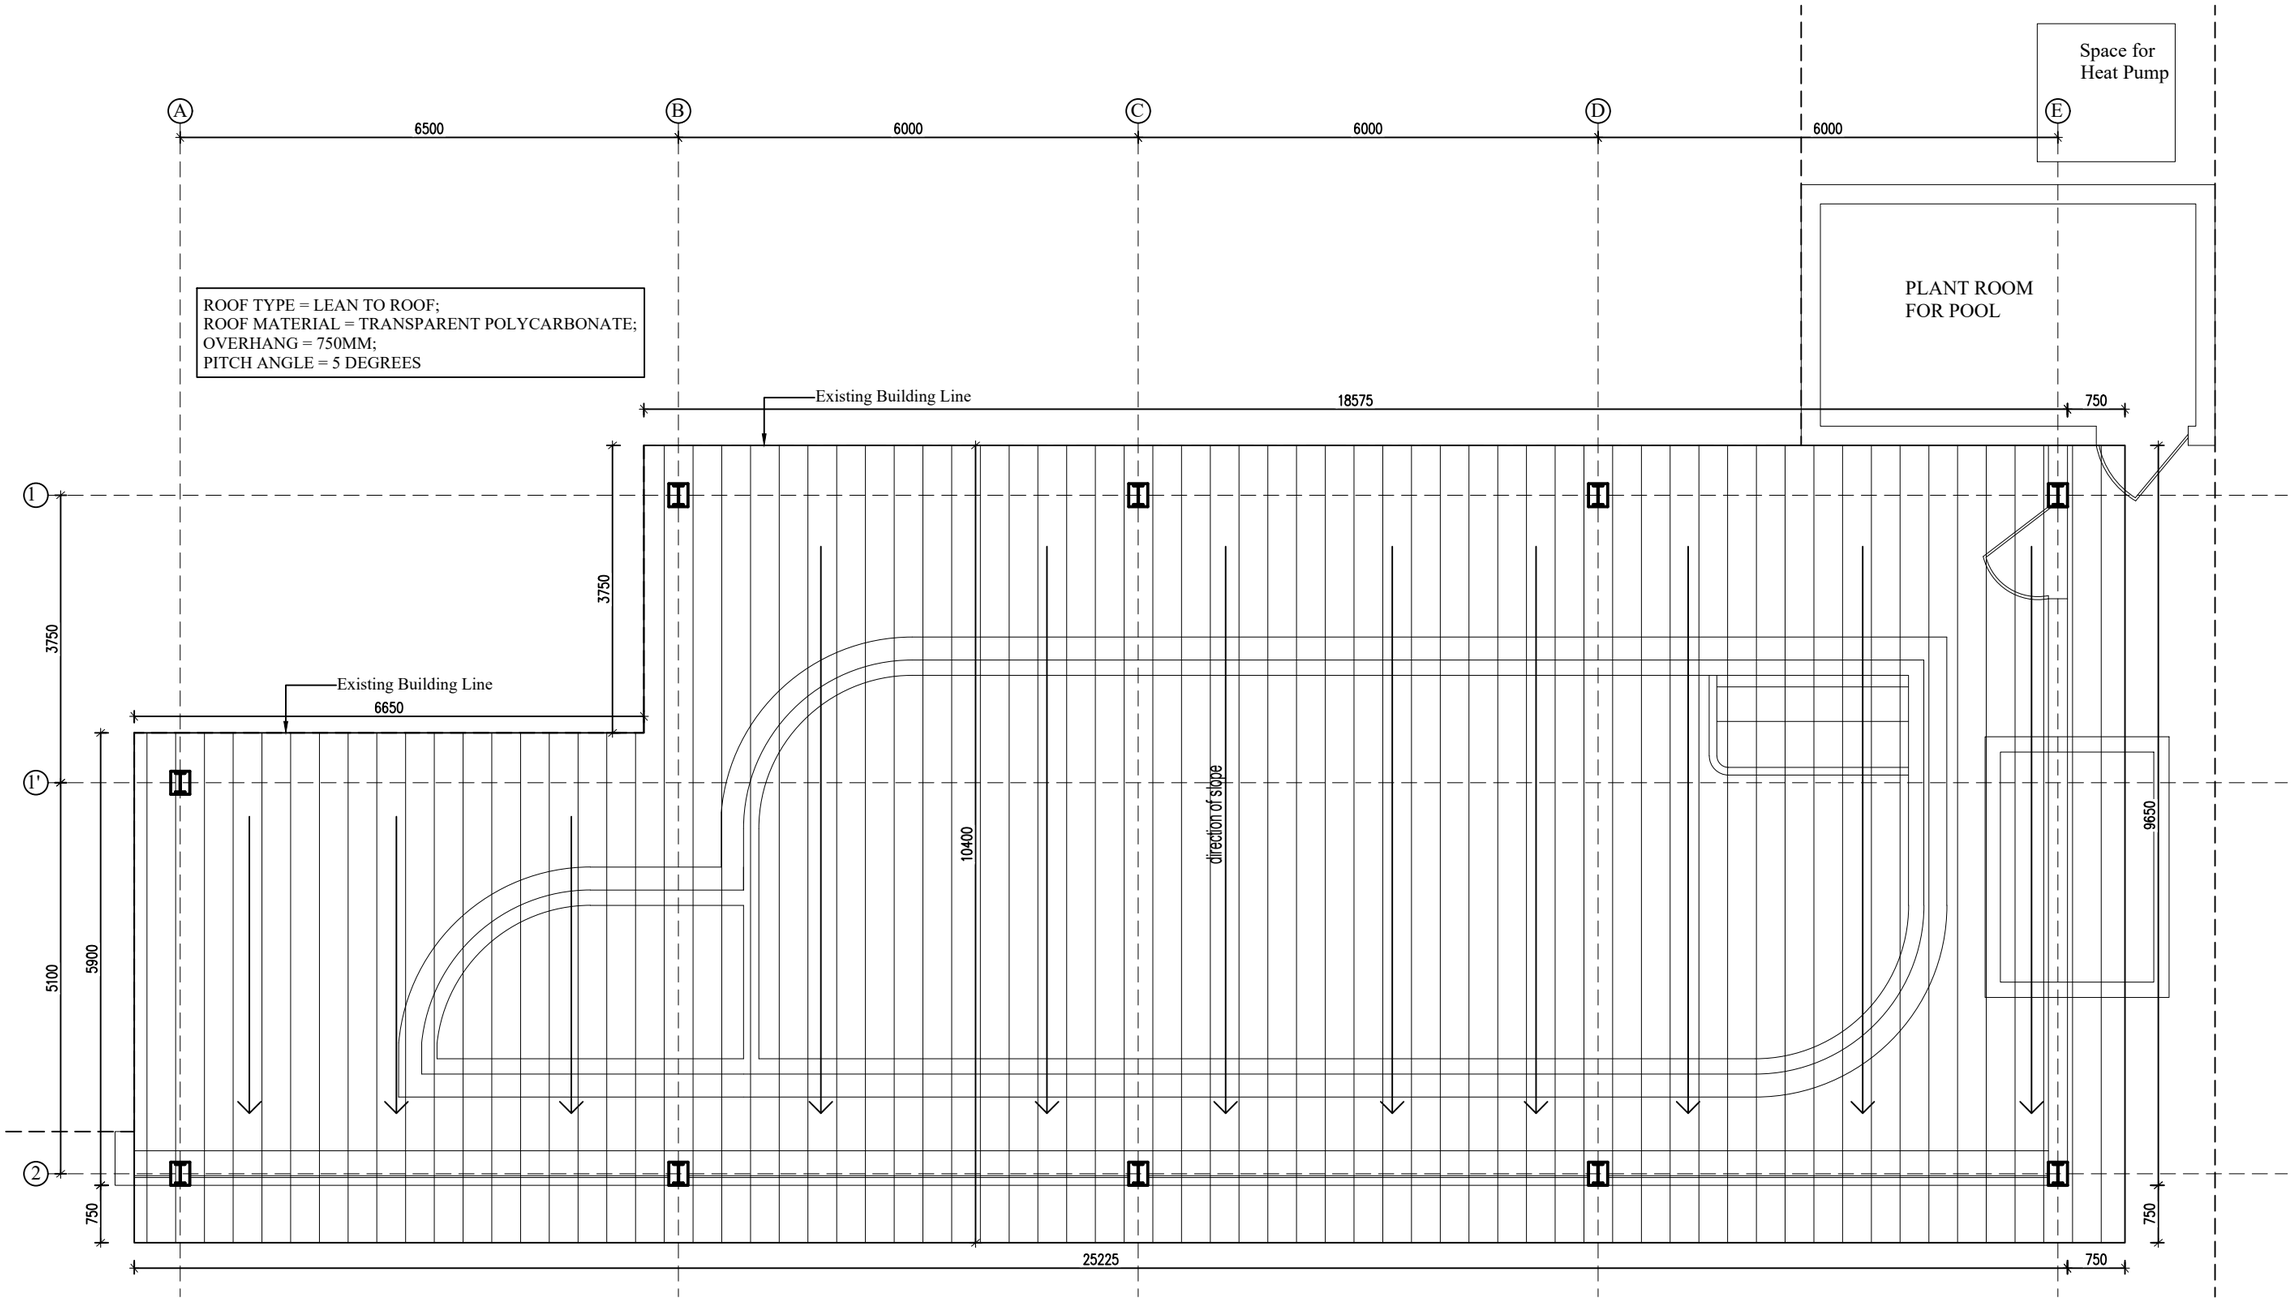


PROJECT: SWIMMING POOL FOR NAK-SEL BOUTIQUE HOTEL & SPA PVT LTD @ NGOBA VILLAGE, UNDER LAMGONG GEWOG, PARO	DRAWING TITLE: ROOF PLAN	ARCHITECT: RINCHEN DORJI	SCALE: 1:75 (ALL DIMENSIONS IN MM)	OWNER:	SONAM WANGMO	THRAM NO.: 119	APPROVED BY:	DWG NO. AR-02
				CID NO.:	11511002003	PLOT NO.: LAM-3761		
				SIGN:		THRAM AREA: 0.78 ACRES		

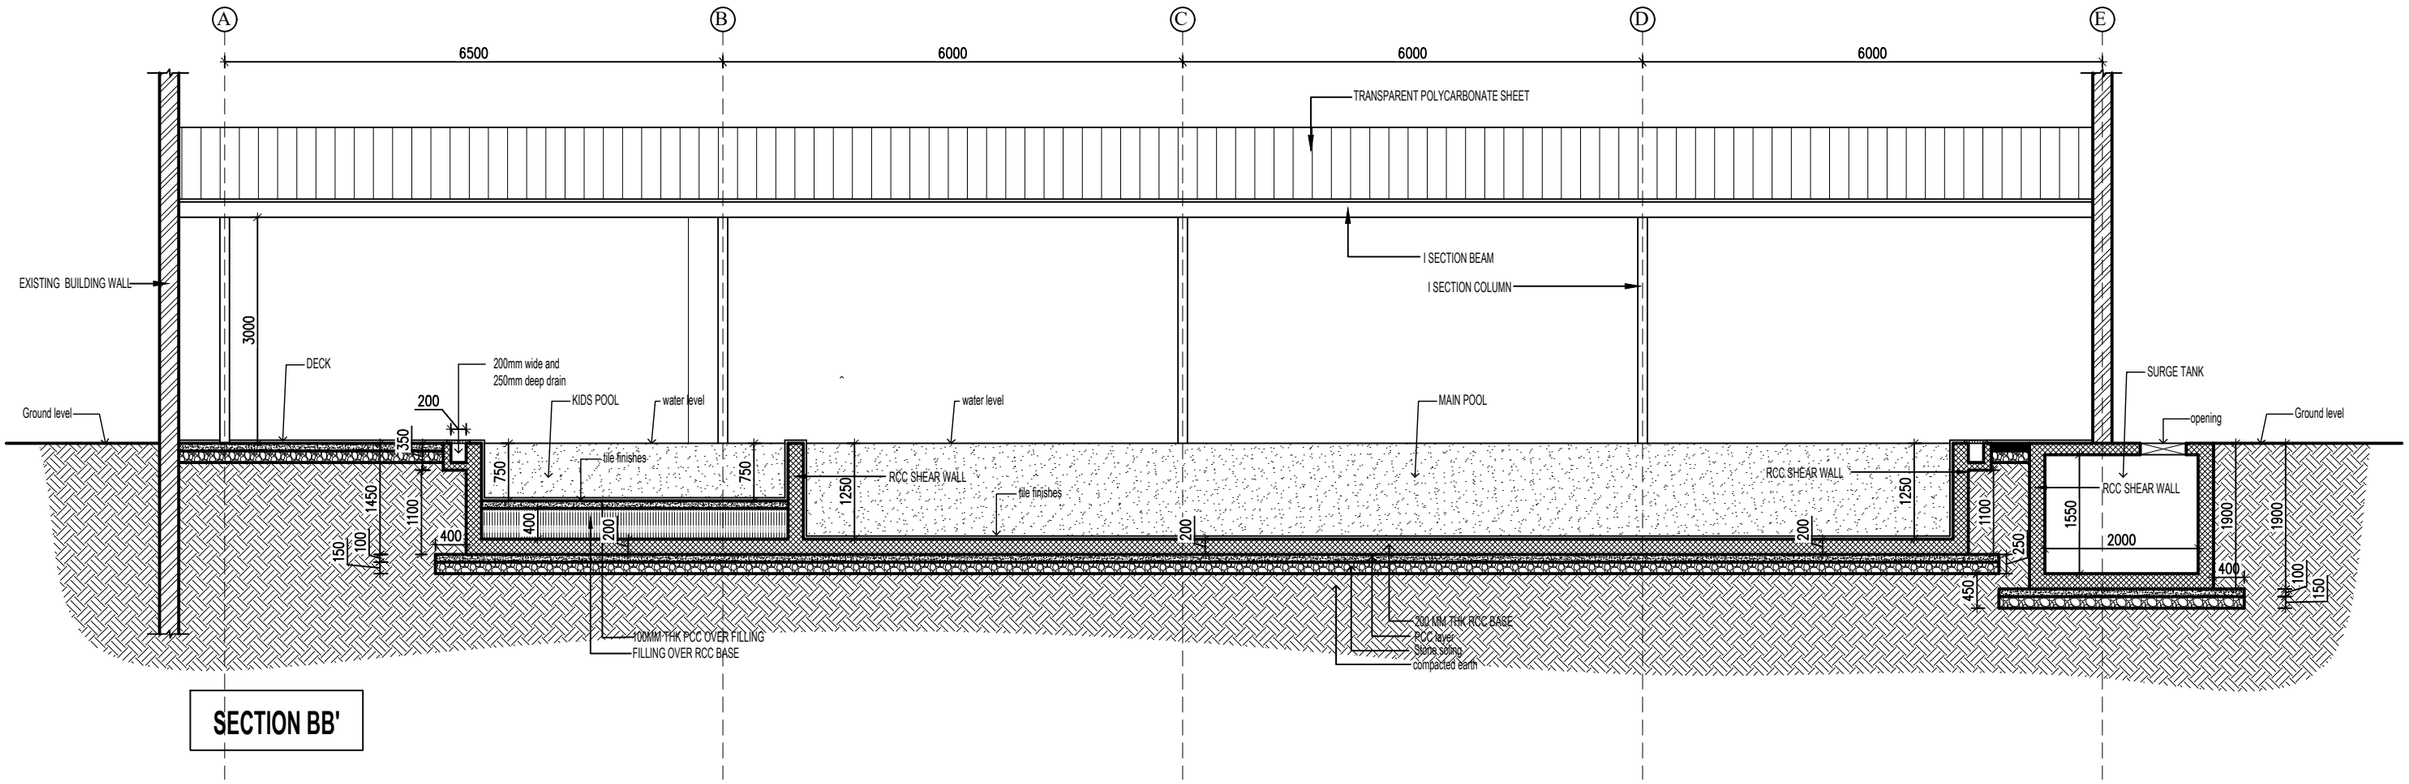


SECTION BB'

PROJECT: SWIMMING POOL FOR NAK-SEL BOUTIQUE HOTEL & SPA PVT LTD @ NGOBA VILLAGE, UNDER LAMGONG GEWOG, PARO	DRAWING TITLE: SECTION BB'	ARCHITECT: RINCHEN DORJI	SCALE: 1:75 (ALL DIMENSIONS IN MM)	OWNER:	SONAM WANGMO	THRAM NO.: 119	APPROVED BY:	DWG NO. AR-03
				CID NO.:	11511002003	PLOT NO.: LAM-3761		
				SIGN:		THRAM AREA: 0.78 ACRES		

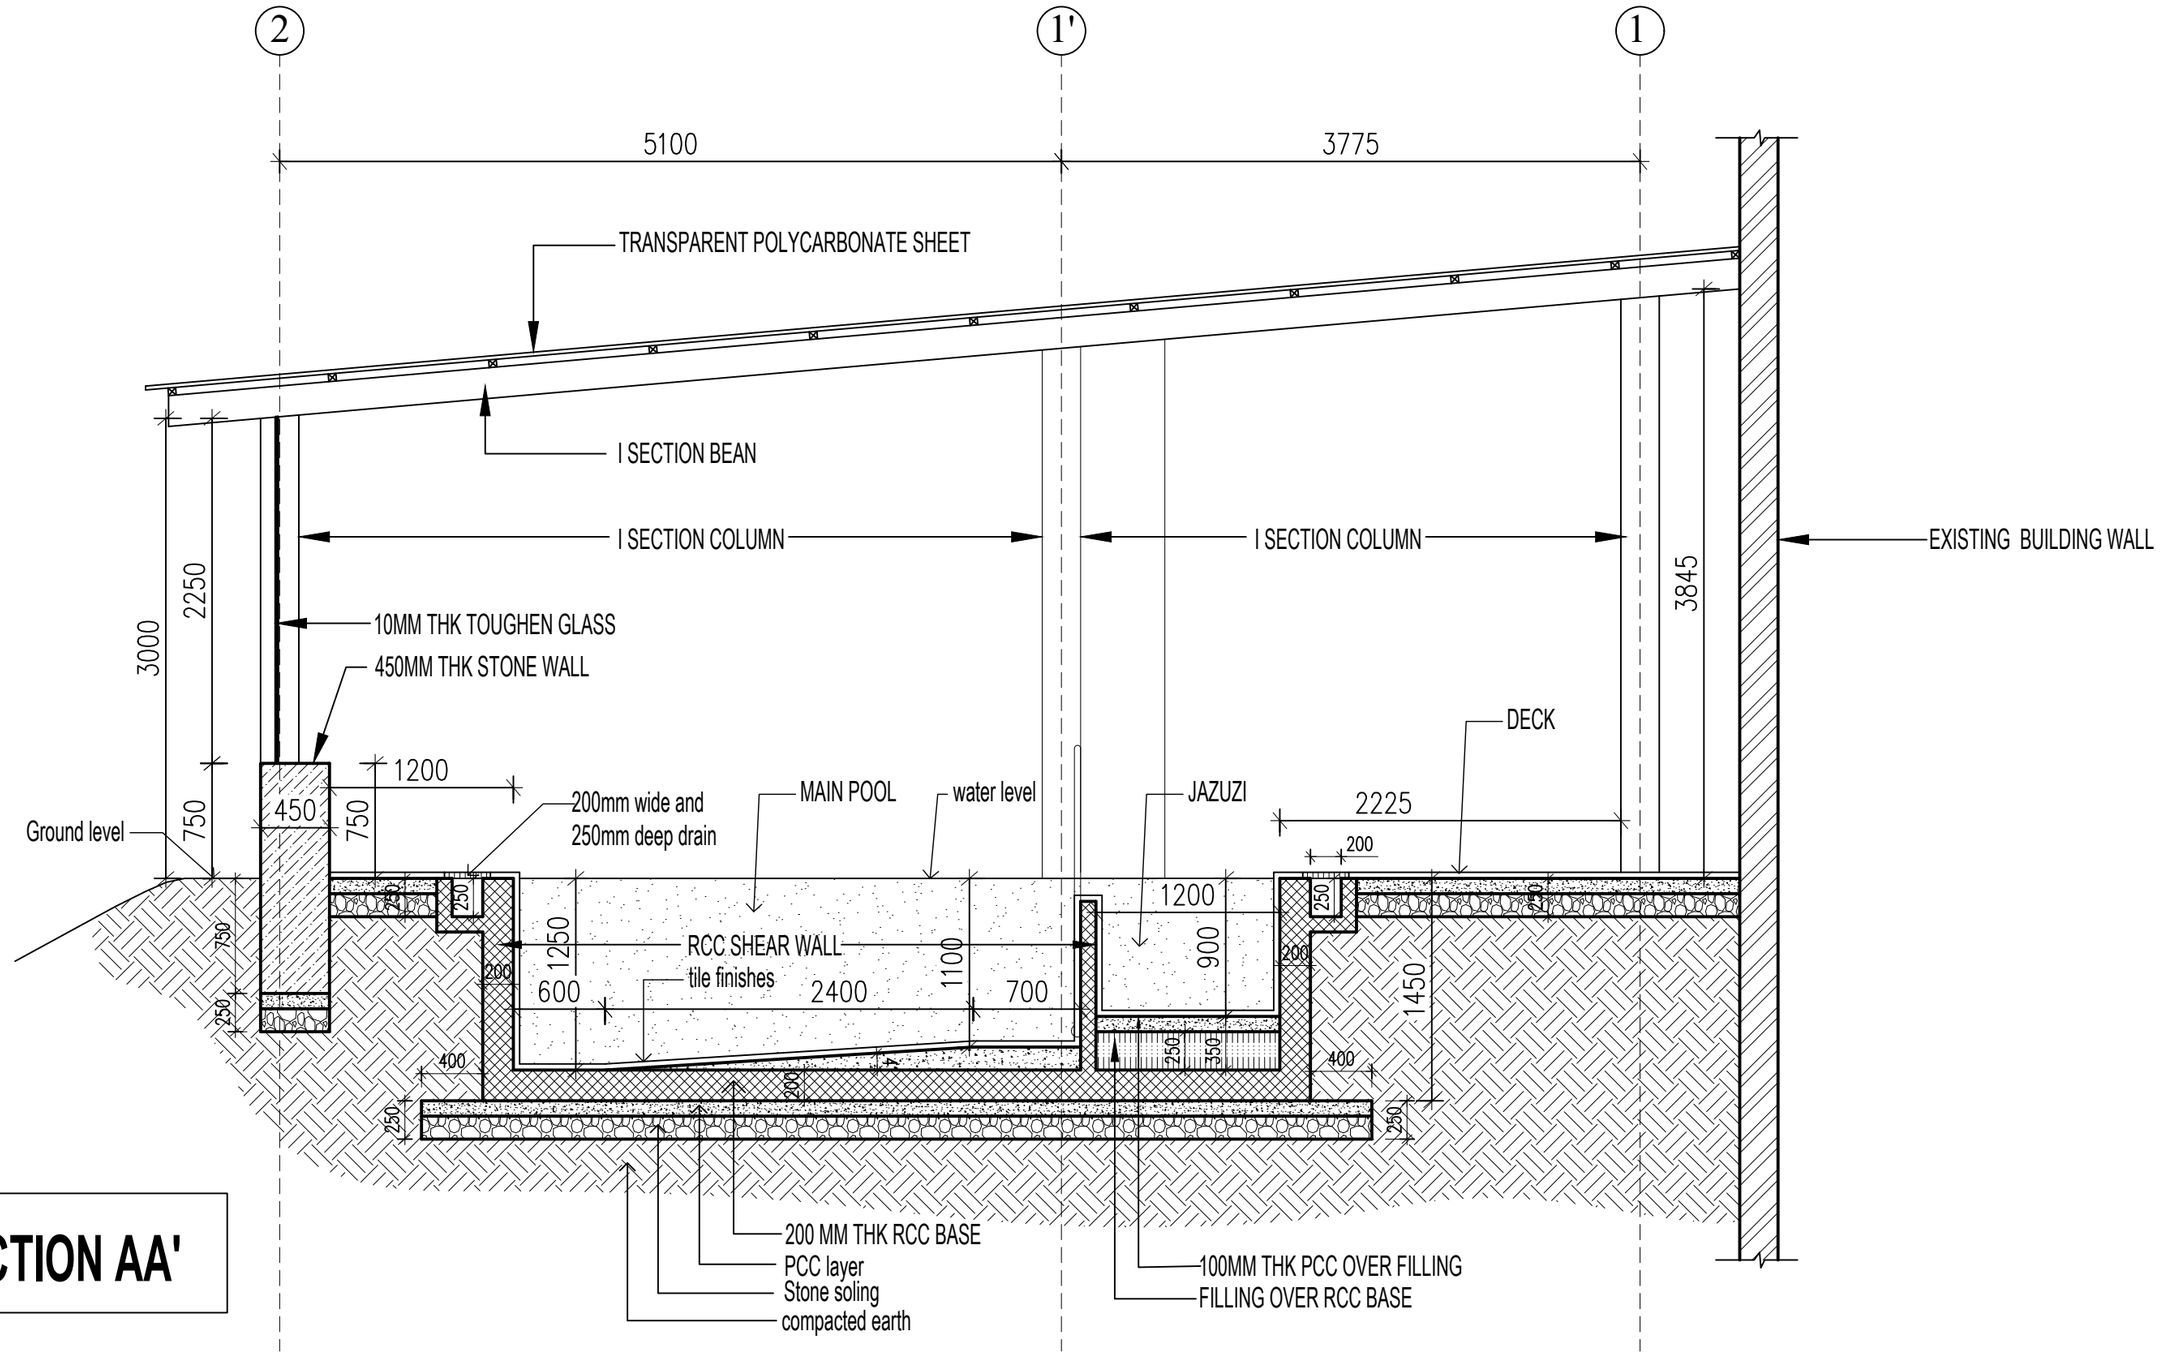

SECTION AA'

PROJECT: SWIMMING POOL FOR NAK-SEL BOUTIQUE HOTEL & SPA PVT LTD @ NGOBA VILLAGE, UNDER LAMGONG GEWOG, PARO	DRAWING TITLE: SECTION AA'	ARCHITECT: RINCHEN DORJI	SCALE: 1:75 (ALL DIMENSIONS IN MM)	OWNER:	SONAM WANGMO	THRAM NO.: 119	APPROVED BY:	DWG NO. AR-04
				CID NO.:	11511002003	PLOT NO.: LAM-3761		
				SIGN:		THRAM AREA: 0.78 ACRES		

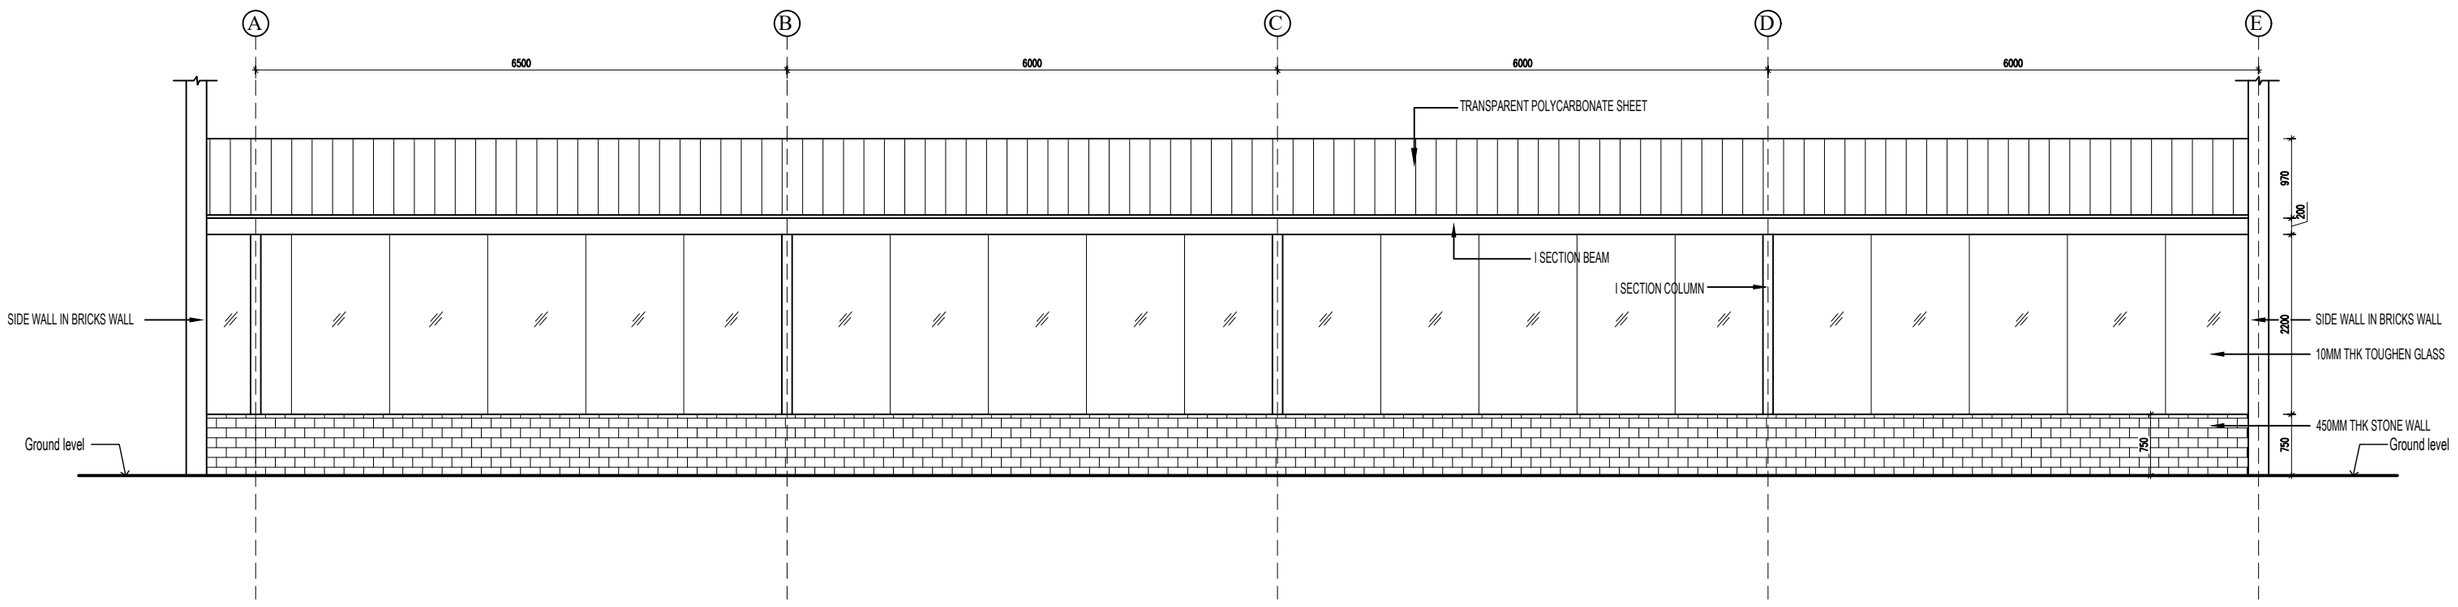

PROJECT: SWIMMING POOL FOR NAK-SEL BOUTIQUE HOTEL & SPA PVT LTD @ NGOBA VILLAGE, UNDER LAMGONG GEWOG, PARO	DRAWING TITLE: FRONT ELEVATION	ARCHITCT: RINCHEN DORJI	SCALE: 1:75 (ALL DIMENSIONS IN MM)	OWNER: CID NO.: SIGN:	SONAM WANGMO 11511002003	THRAM NO.: 119 PLOT NO.: LAM-3761 THRAM AREA: 0.78 ACRES	APPROVED BY:	DWG NO. AR-05