

1

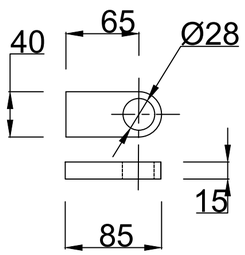


MNTG. BRACKET
40 X 85 X 15 MM THK
MTRL - M.S.
QTY= 60 NOS.

2

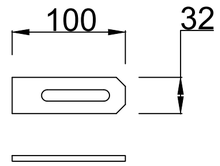


HANDLE PLATE
32 X 100 X 5 MM THK
MTRL - M.S.
QTY= 20 NOS.

3

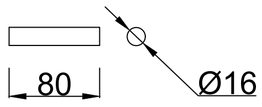


ROUND BAR
- DIA 16 X 80 MM
MTRL - M.S.
QTY= 20 NOS.

4

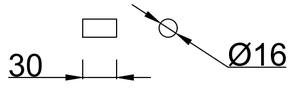

ROUND BAR
- DIA 16 X 30 MM
MTRL - M.S.
QTY= 20 NOS.

5

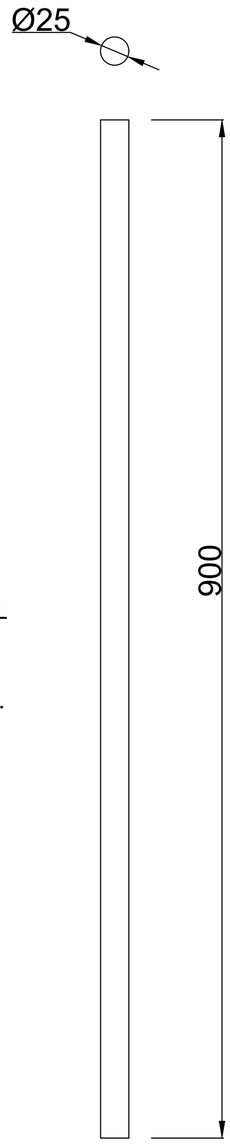


ROD 25 X 900 L
MTRL - M.S.

QTY= 20 NOS.

A


SUBASSEMBLY AT SHOP
PER HEIGHT MNTG PLATE

QTY=65
NOS

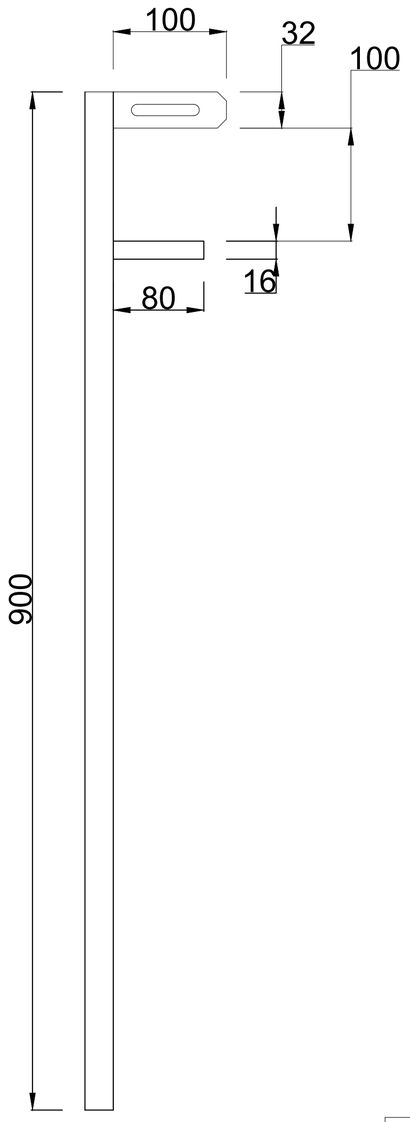

B

FINAL FITTING AT SITE
PER HEIGHT MNTG PLATE

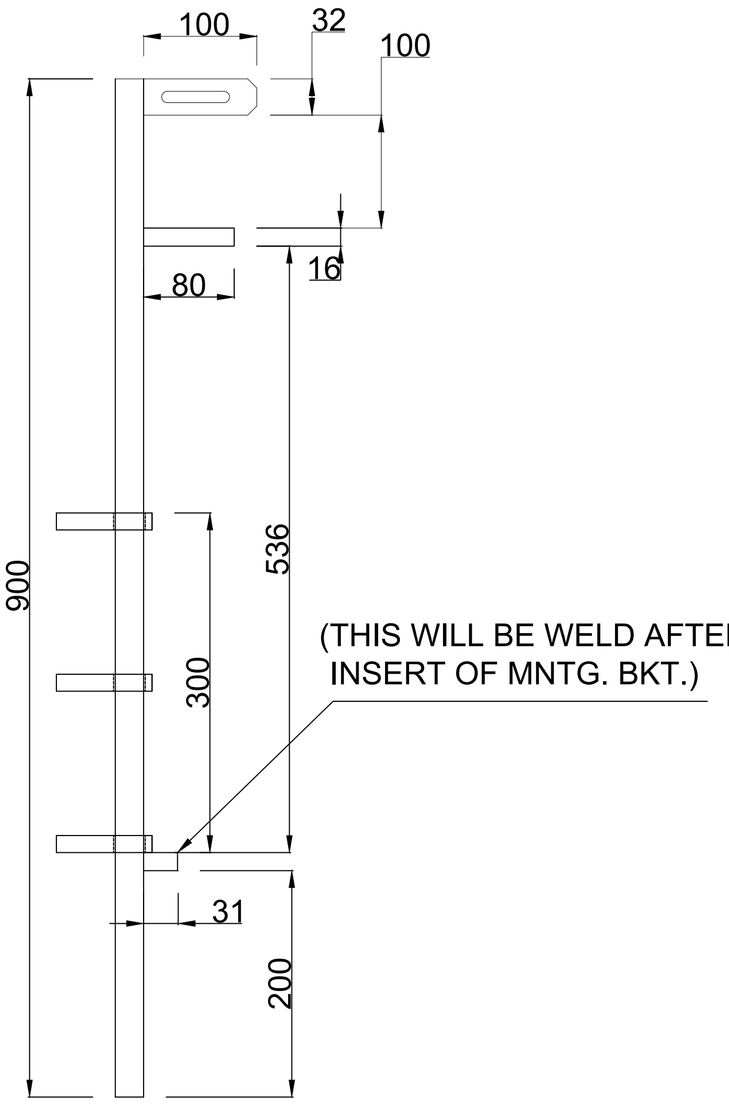

	Date	Revised By

This drawing & design is the property of NIHVA TECHNOLOGIES. Not to be sold or copied to any other concern.

TITLE:- 4 LEAF
CRM DOOR 10

	NAME	DATE	SIGN
DRAWN	M.SUTAR	15/06/2022	
CHECK	M.SUTAR	15/06/2022	
APPRD.			

If any queries contact : design@nihva.com

ALL DIMENSION ARE IN mm

NIHVA
NIHVA TECHNOLOGIES PVT. LTD.
NIHVA TECHNOLOGIES PVT. LTD. PUNE
Tel : 020 66304033
Email:- info@nihva.com
Website:- www.nihva.com

CLIENT - NIHVA TECHNOLOGIES PVT.LTD
LOCATION -
PRODUCT - SLIDING DOOR
DWG NO:-NIHVA/22-23/MNFG/0036 | REV- 0
SCALE: NTS | SCALE:-- 1:1 | SHEET: 01 OF 01