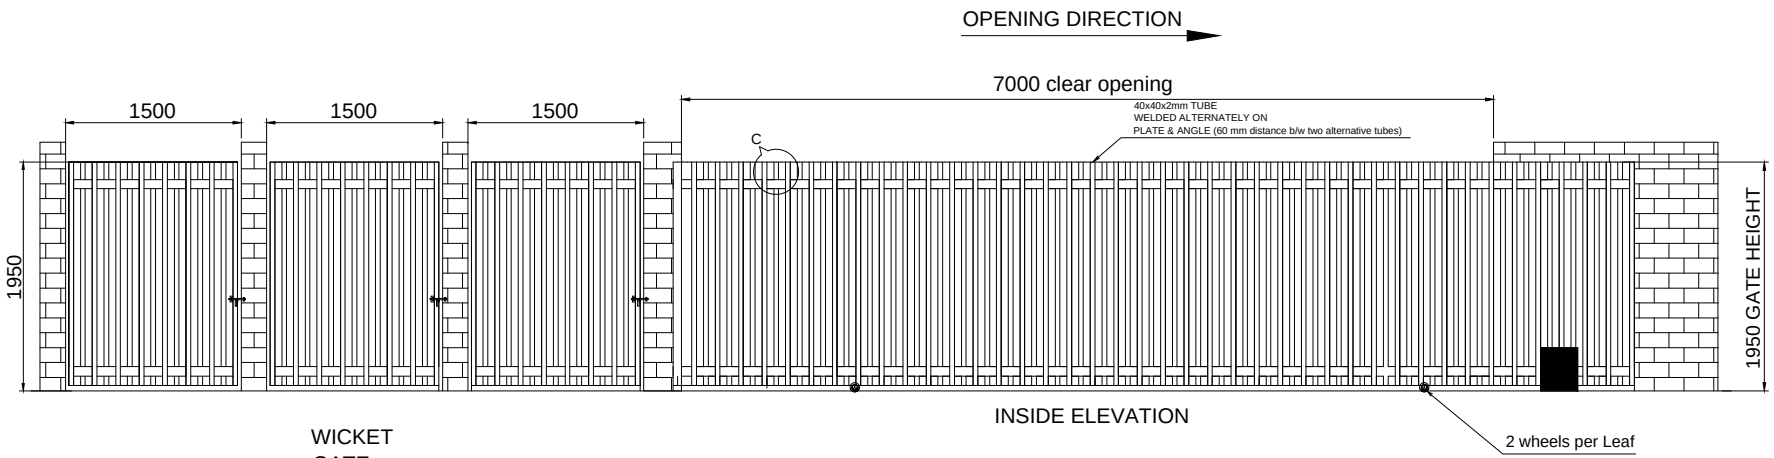
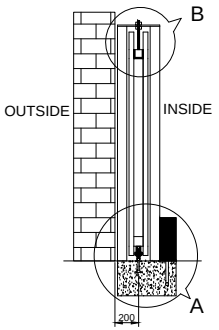
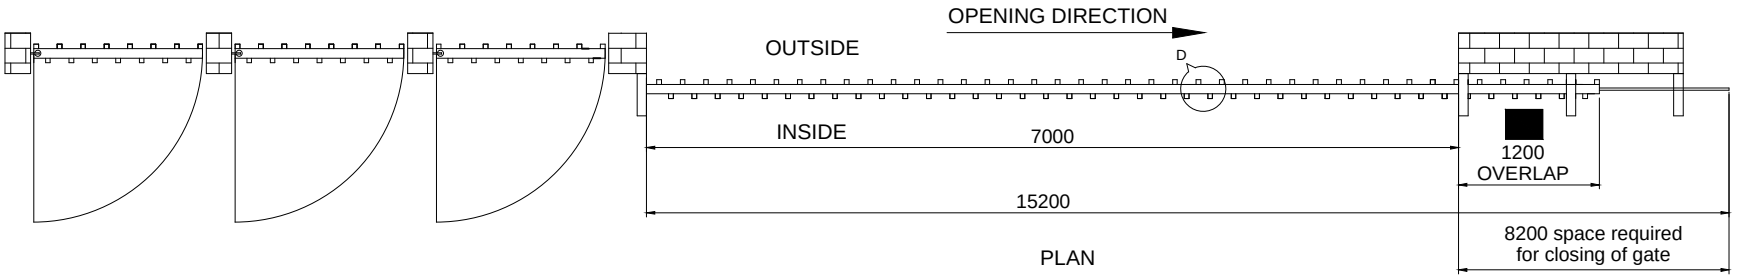
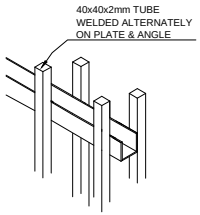


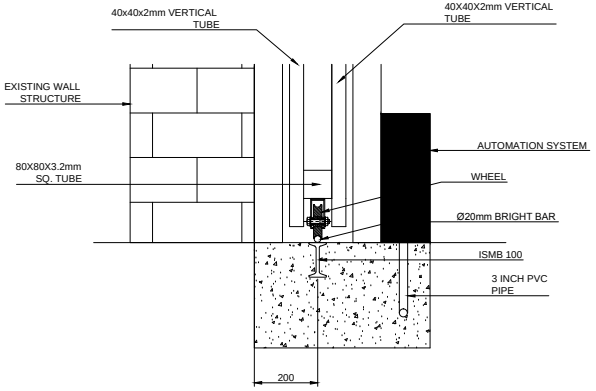

SIDE VIEW



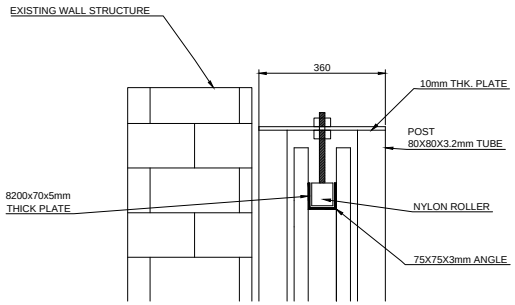

PLAN



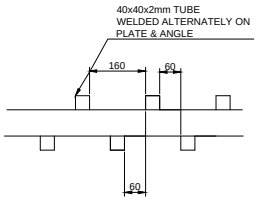

DETAIL VIEW OF C




DETAILED VIEW OF A




DETAILED VIEW OF B




DETAILED VIEW OF D

## MOTORISED SINGLE LEAF SLIDING GATE & WICKET GATE

| DESCRIPTION | CLEAR WIDTH | OVERALL WIDTH | CLEAR HEIGHT | QTY. |
|---|---|---|---|---|
| SLIDING GATE | 7000 | 8200 | 1950 | 1 NOS |
| WICKET GATE | 1500 | | 1950 | 3 NOS |

NOTE- ALL REQUIRED CIVIL WORK WILL BE IN CLIENT'S SCOPE.

This drawing & designing is the property of NIHVA TECHNOLOGIES. Not be sold or copy to any other concern.

TITLE SINGLE LEAF MOTORIZED SLIDING GATE & WICKET GATE

| | SIGN | DATE |
|---|---|---|
| DRAWN | OMKAR | 05/07/16 |
| CHECK | ANIL | 05/07/16 |
| REV. | 02 | |
| APPROVAL | | |

If any queries contact : projects@nihva.com

ALL DIMENSION ARE IN mm

NIHVA TECHNOLOGIES PVT. LTD.
NIHVA TECHNOLOGY
PVT. LTD. PUNE
Tel : 020 66304033
Email:- info@nihva.com
Website:- www.nihva.com

CLIENT - MAHENDRA WINDOOR SOLUTIONS

PROJECT - AUROBINDO PHARMA LIMITED

SITE -

DWG. NO. : NIHVA/16-17/0026/R03

SCALE: NTS | WT: | SHEET: 01 OF 01