

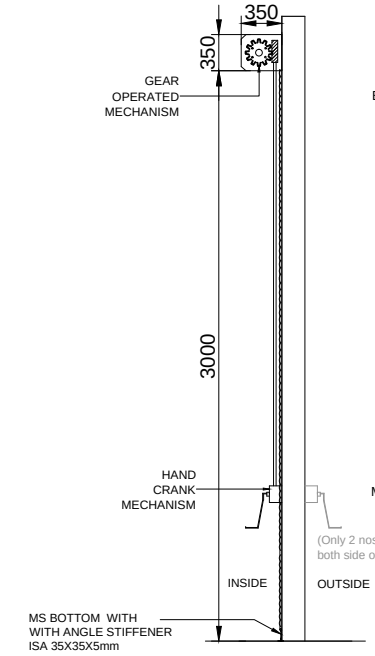



SIDE VIEW

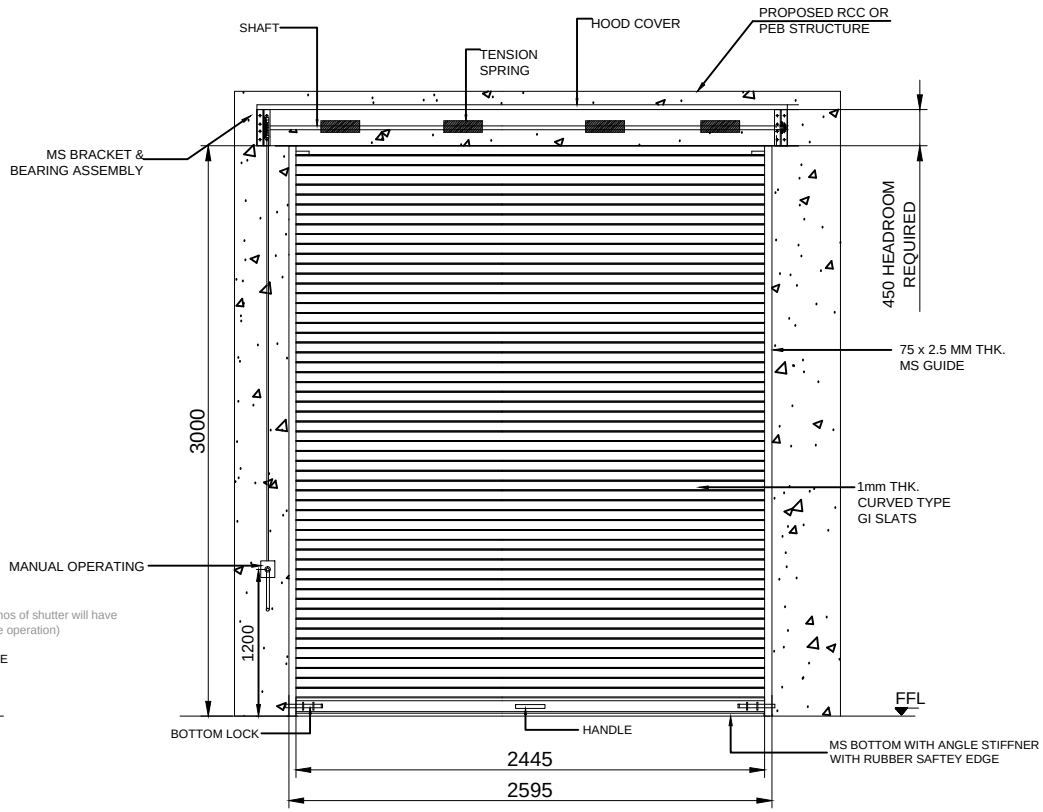

INSIDE ELEVATION

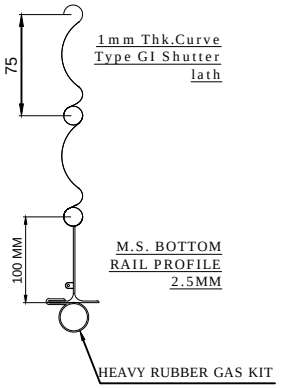

M.S. BOTTOM RAIL PROFILE 2.5MM

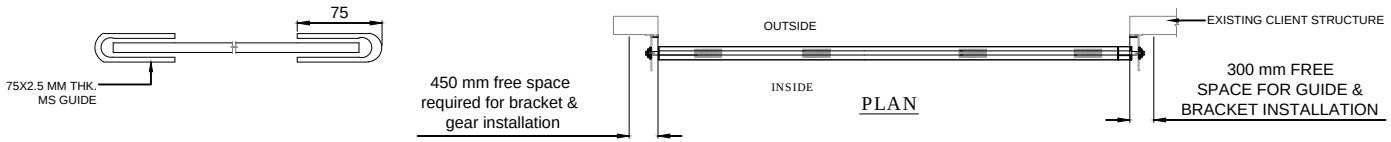

PLAN

TOLERANCE - ±10mm

REV:-28-04-2018 .01.Changed hand crank mechanism location.

S.N.	LOCATION	SIZE	QUANTITY- Left side gearbox
1	B400	2445(W)X3000(H)	07
2	B500	2445(W)X3000(H)	06 (1 nos shutter will have both side operation)
3	B600	2445(W)X3000(H)	05 (1 nos shutter will have both side operation)
TOTAL QTY. OF SHUTTER			18

NOTE-
1. ALL CIVIL WORK WILL BE CLIENT'S SCOPE.
2.STRUCTURE REQUIRED FOR SHUTTER IS IN CLIENT'S SCOPE.
3.FINAL FINISH OF SHUTTER WILL BE IN POWDER COATING OF APPROVED COLOR i.e.RAL 7001.

This drawing & design is the property of NIHVA TECHNOLOGIES. Not to be sold or copied to any other concern.

TITLE: GEAR OPERATED ROLLING SHUTTER 2.445mX3m With Left side gearbox

	NAME	SIGN	DATE
DRAWN	OMKAR		03.05.2018
CHECK	PRADEEP		03.05.2018
APPRD.	PRADEEP		03.05.2018

NIHVA TECHNOLOGIES PVT. LTD.
NIHVA TECHNOLOGIES PVT. LTD. PUNE
Tel : 020 66304033
Email:- info@nihva.com
Website:- www.nihva.com

CLIENT -
PROJECT -
SITE LOCATION -

If any queries contact : design@nihva.com
DWG. NO. : NIHVA/18-19/VDR/016 | REV- 0
ALL DIMENSION ARE IN mm
SCALE: NTS | WT: | SHEET: 01 OF 01