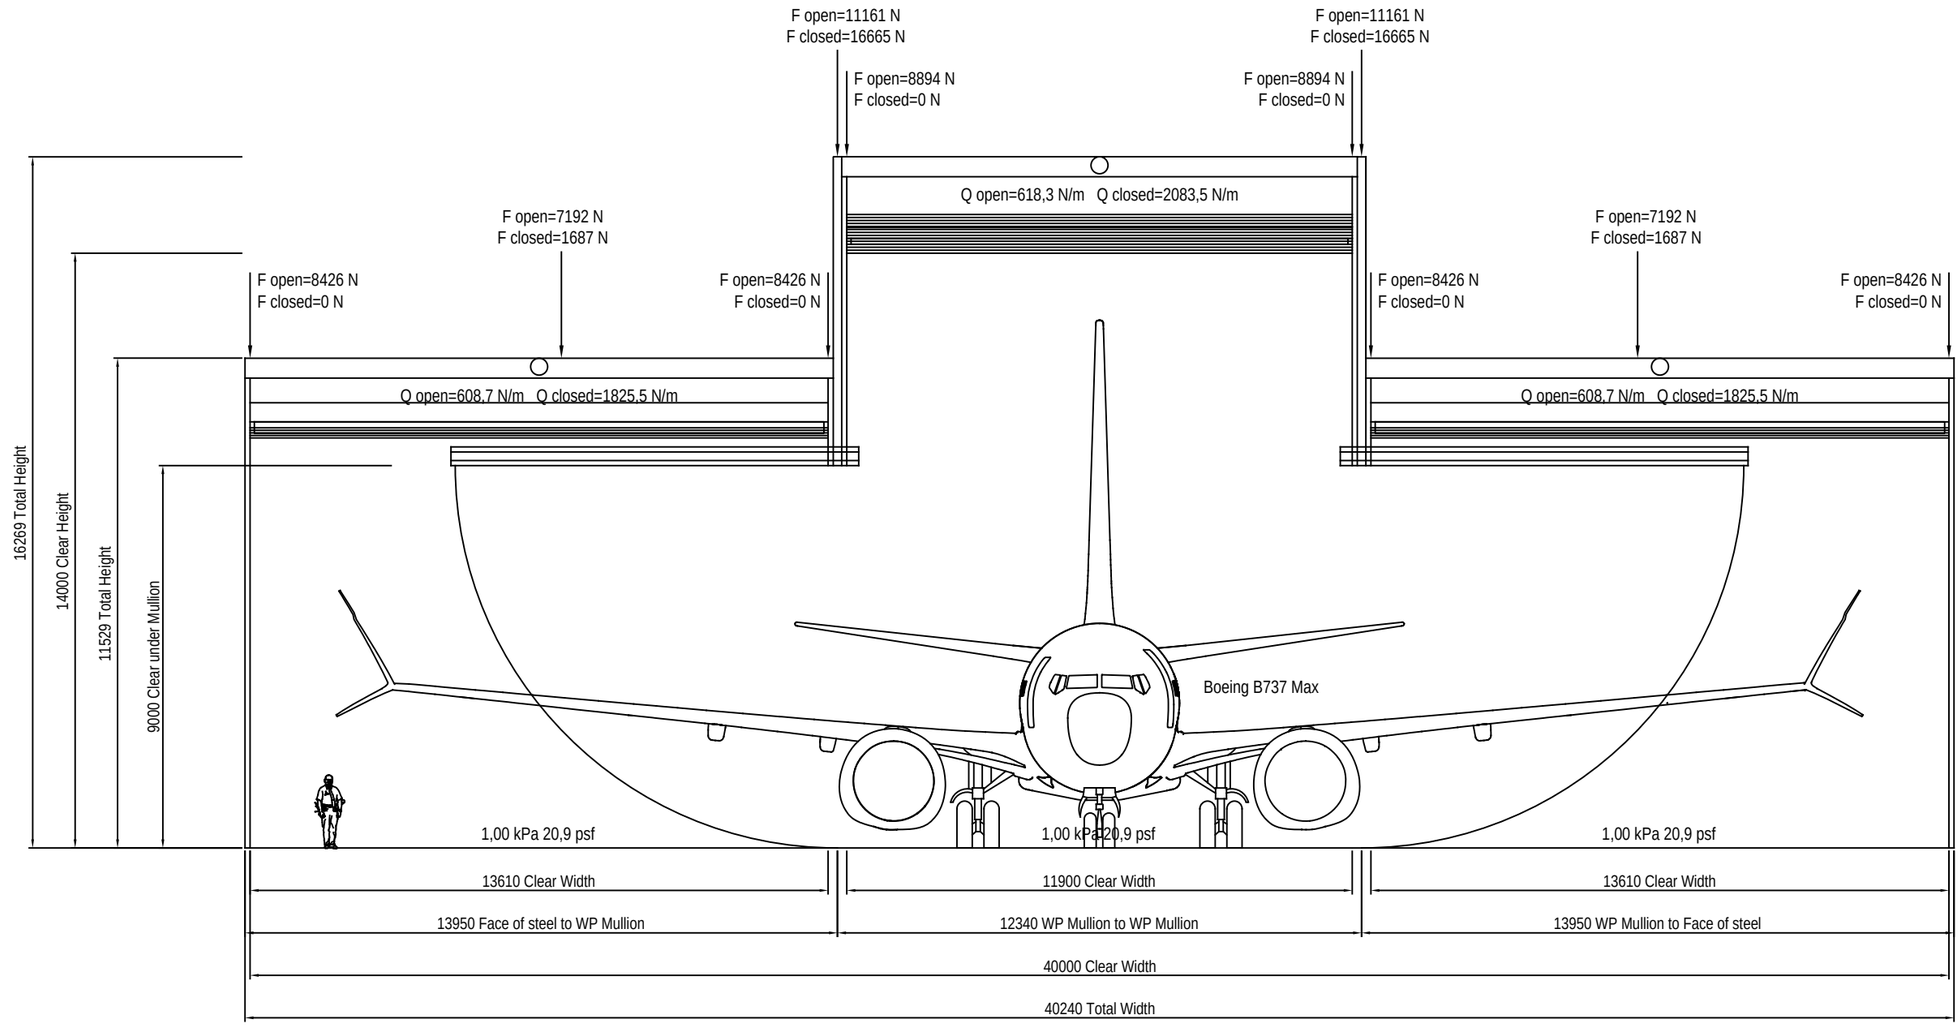


Quotation only. Do not use for design.
Nominal static vertical loads are indicated.
A dynamic surload factor of 1.25 should be added to door leaf loads in open position.
Includes items provided by ASSA ABLOY Entrance Systems only.
Total weight: 11498 kg
Total static weight: 11284 kg
Total motor power: 15,0 kW
Total rated current: 30,6 A
Total peak current: 45,0 A
Power supply: 400V/50Hz/3ph
(max. allowed voltage drop at start: 5%)
Control system: 24V
Mains power to control panel supplied by others than ASSA ABLOY Entrance Systems.

NIHVA
NIHVA Technologies Pvt. Ltd.

ASSA ABLOY

SALES REP. Peter Bergmark	DATE ISSUED 2018-04-26
SALES No. 218146	DATE DRAWN 2018-04-26
SCALE N.T.S.	
DRAWING No. 218146	REVISION A

Aircraft Hangar Door
Cochin International Airport
India

Load diagram