

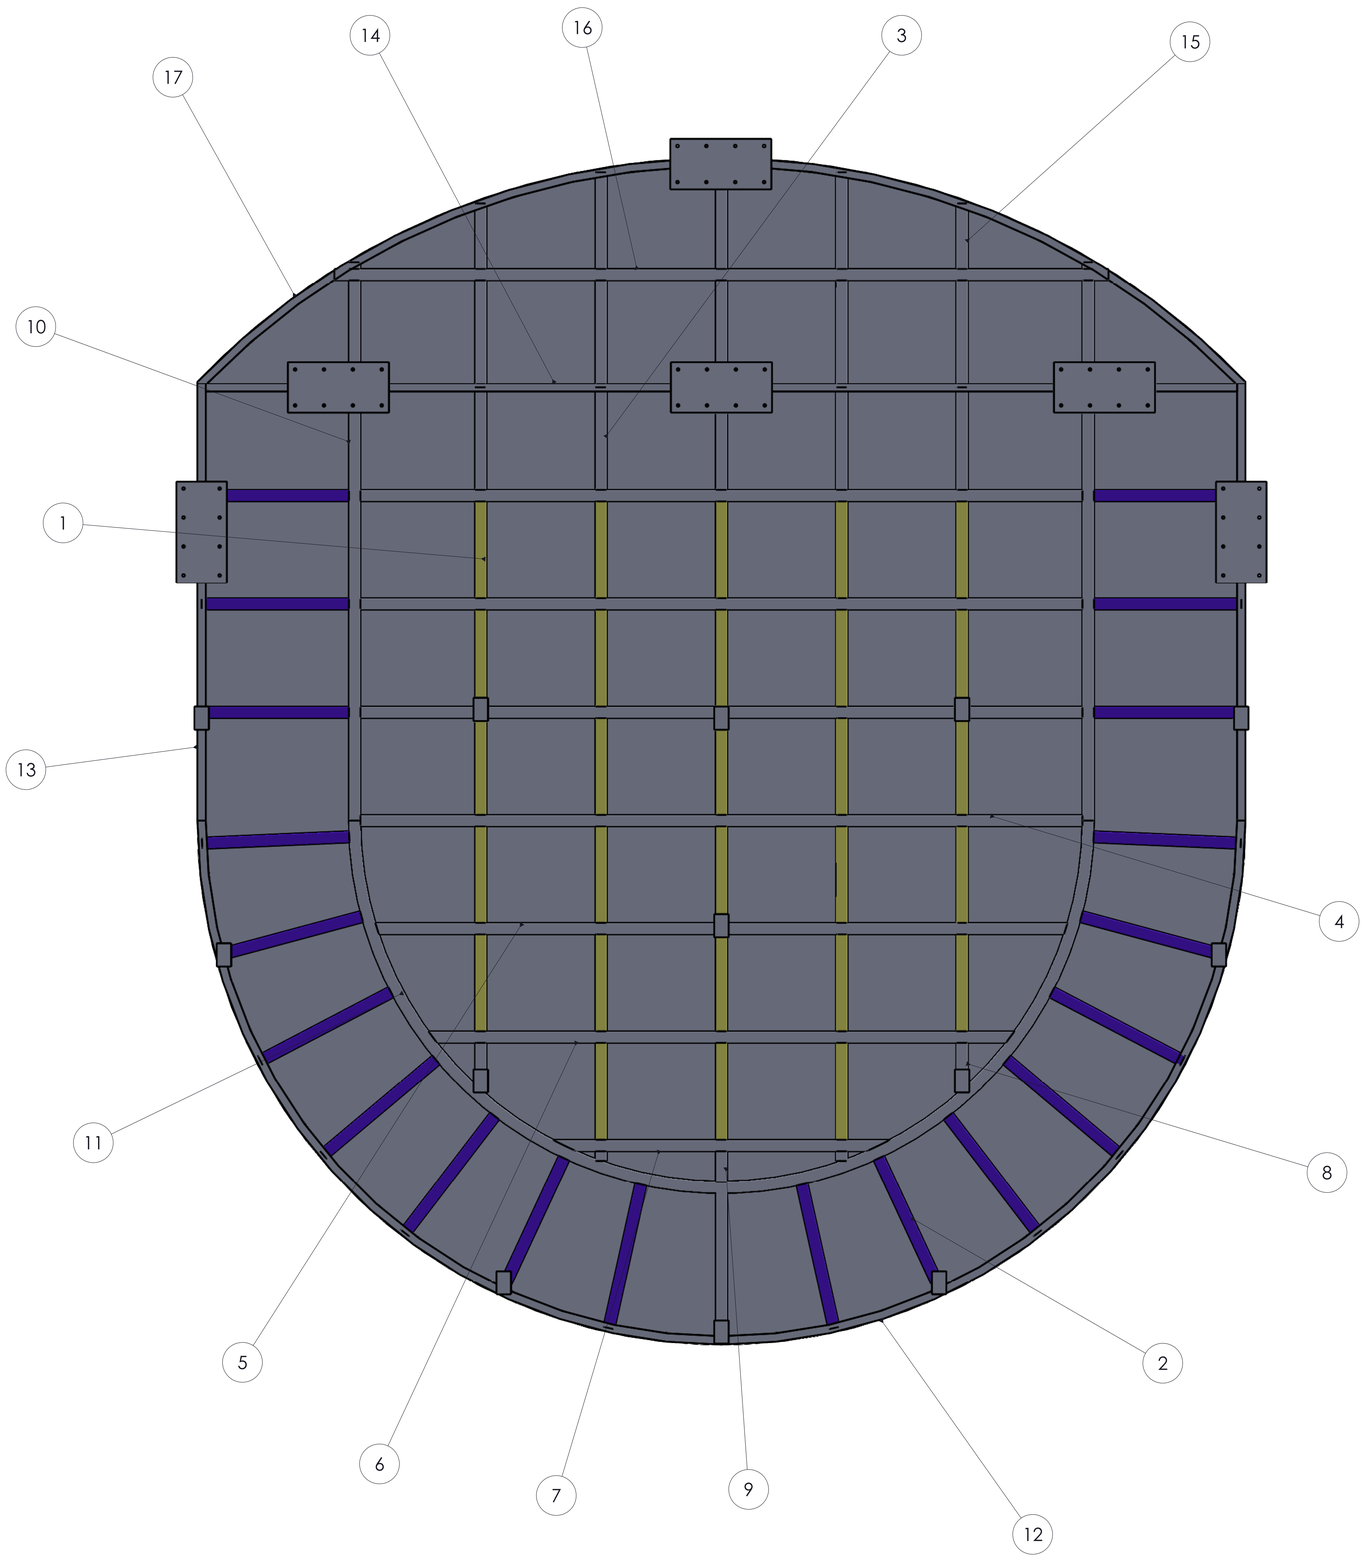


SR NO	PART NAME	DESCRIPTION	LENGTH	QTY
1	RHS-1	120X80X 4 MM	670 MM	28
2	RHS-2	120X80X4 MM	1020 MM	21
3	RHS-3	120X80X4 MM	710 MM	15
4	RHS-4	120X80X4 MM	5000 MM	4
5	RHS-5	120X80X4 MM	4800 MM	1
6	RHS-6	120X80X4 MM	4060 MM	1
7	RHS-7	120X80X4 MM	2340 MM	1
8	RHS-8	120X80X4 MM	325 MM	2
9	RHS-9	120X80X4 MM	210 MM	1
10	RHS-10	120X80X4 MM	3000 MM	2
11	RHS-11 CURVED	120X80X4 MM	AS PER DRAWING	1
12	I BEAM CURVED 1	120X60 BEAM	AS PER DRAWING	1
13	I BEAM SIDE	120X60 BEAM	3030 MM	2
14	I BEAM BACK	120X60 BEAM	7260 MM	1
15	RHS-11	120X80X4 MM	454 MM	2
16	RHS-12	120X80X4 MM	5360 MM	1
17	I BEAM Curved 2	120X60 BEAM	AS PER DRAWING	1


TITLE -	BTM MS STRUCTURE		
QTY -	1		
PROJECT -	MV DOME		
DWG NO -	MVD-2-CL		REV-
DATE -	21-6-23		SHEET: 1/5

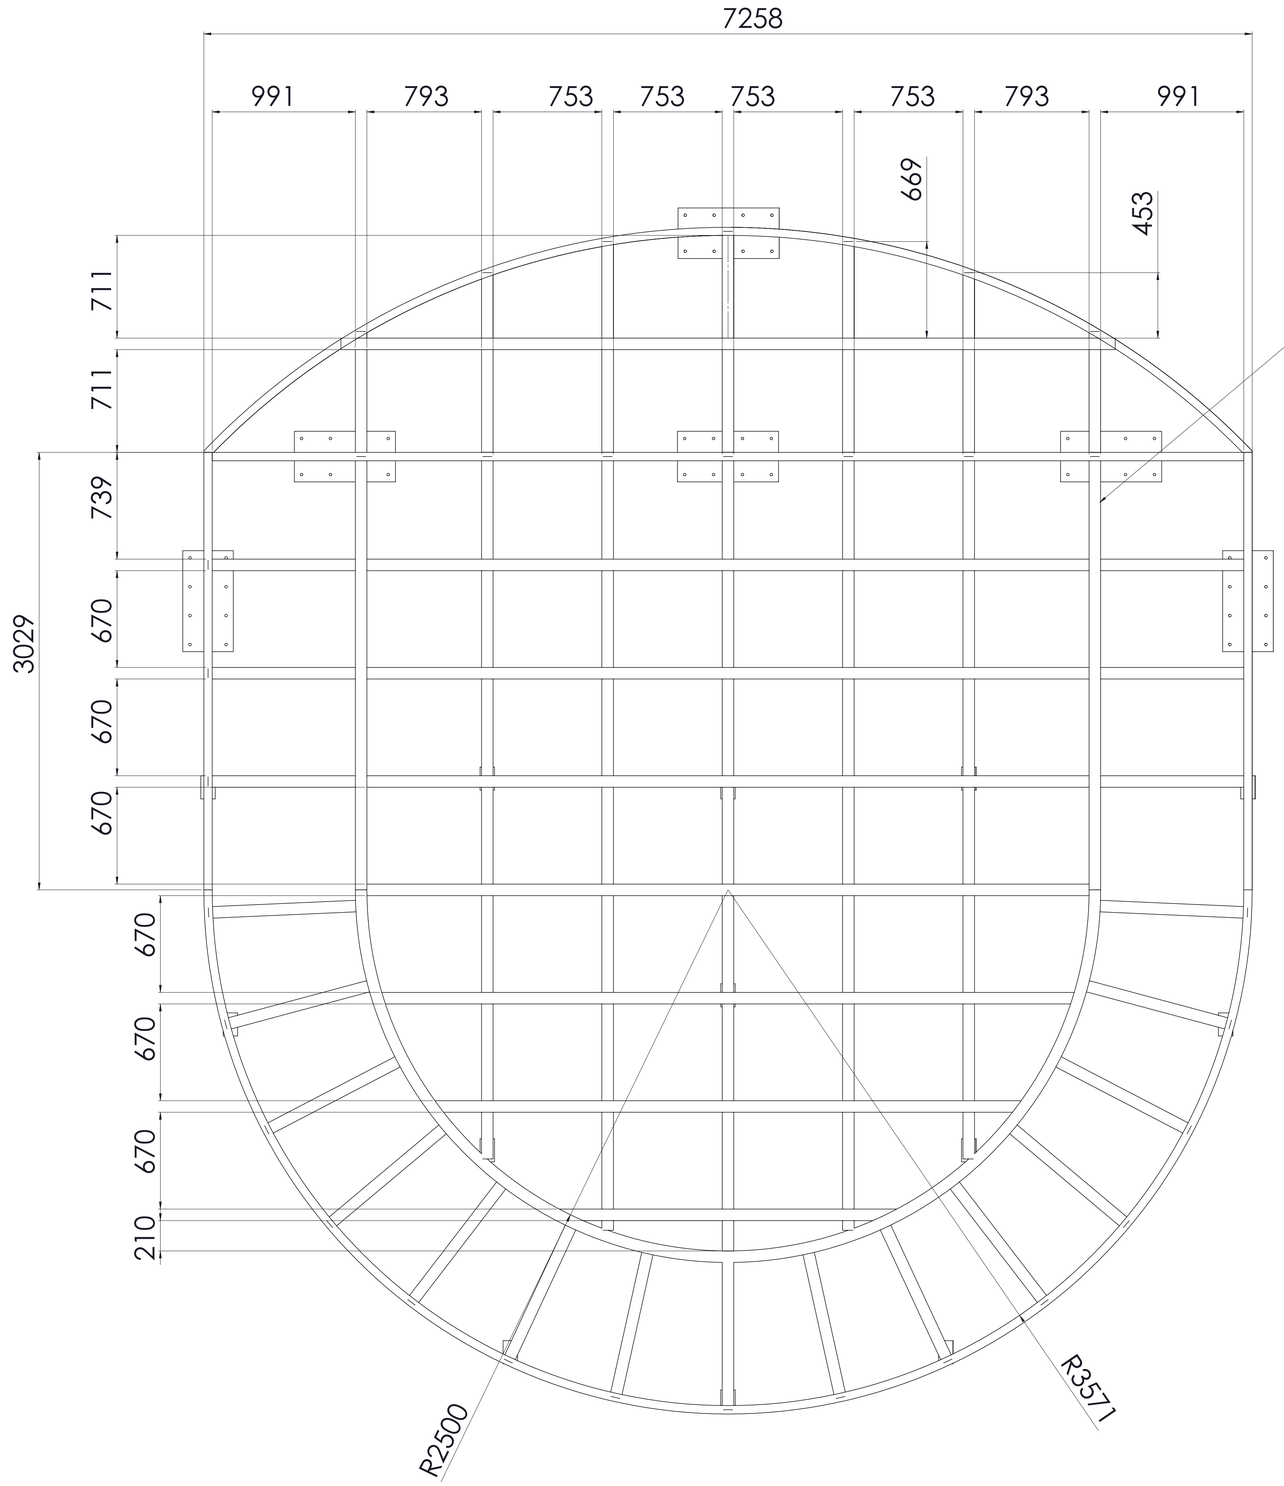

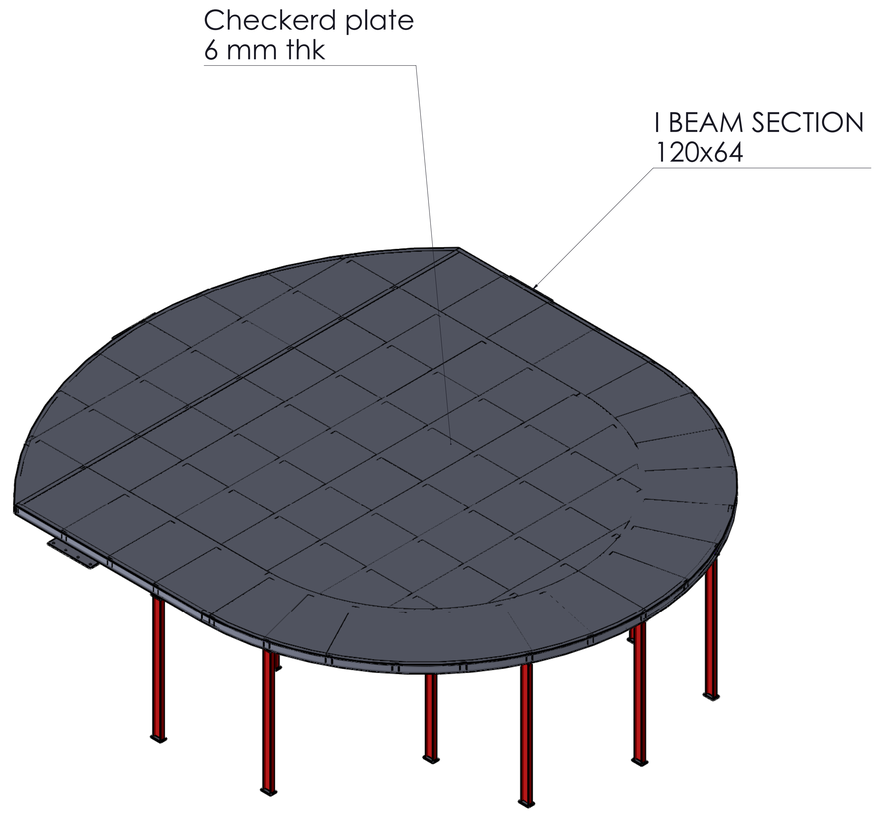

DRAWING NO: MVD-2	SHEET: 2/5


SR NO	PART NAME	DESCRIPTION	LENGTH	QTY
1	CURVE TUBE	RHS 120X80X4 MMTHK	8105 MM	1

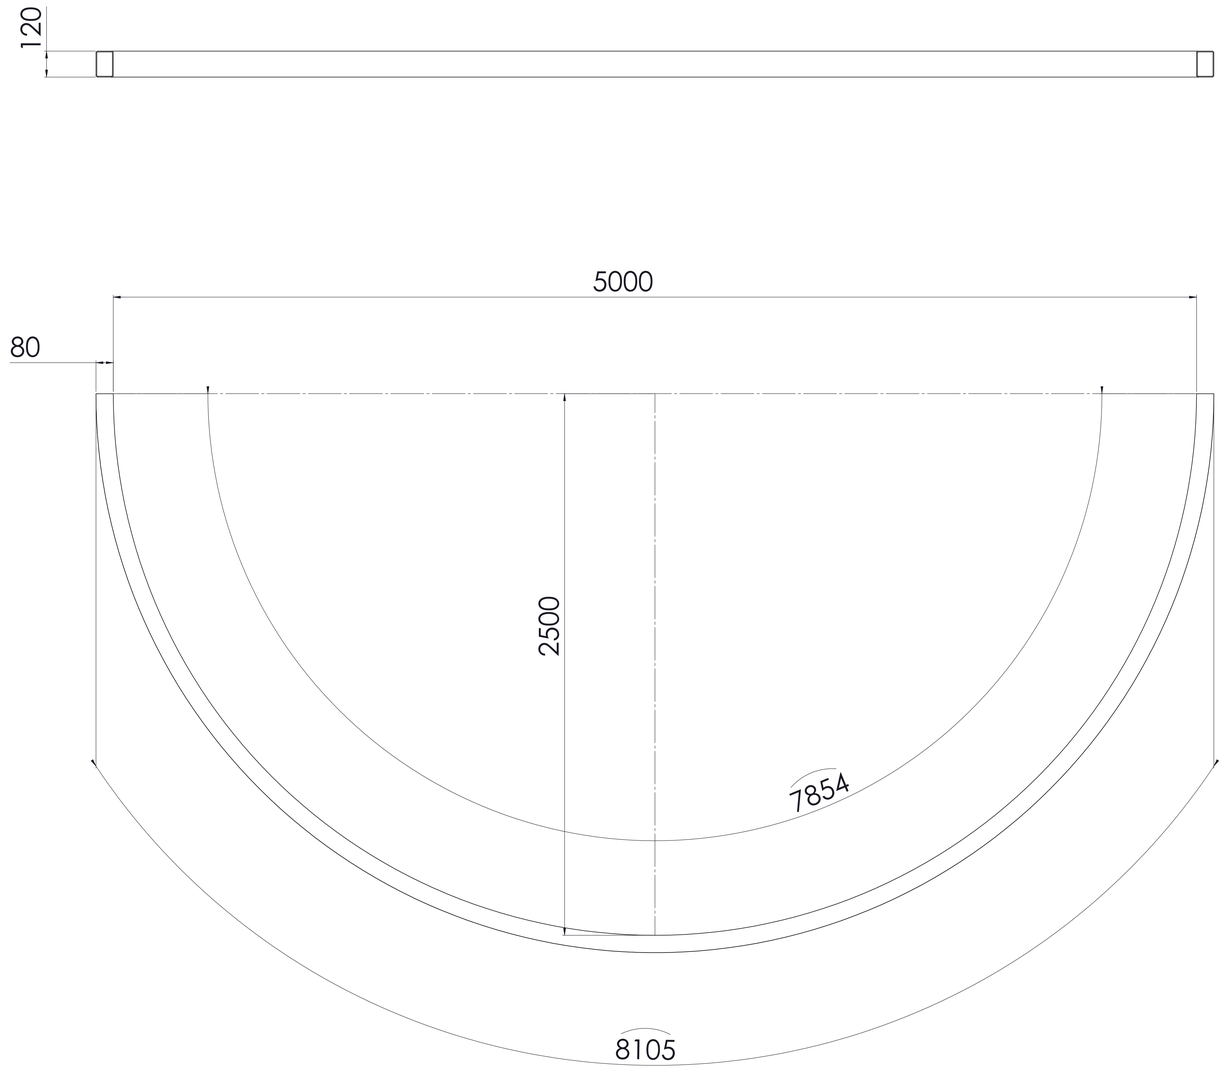

DRAWING NO: MVD-2-11

SHEET: 3/5

sr no	part name	description	length	qty
1	btm curved beam	120x60 I section	11404 MM	1

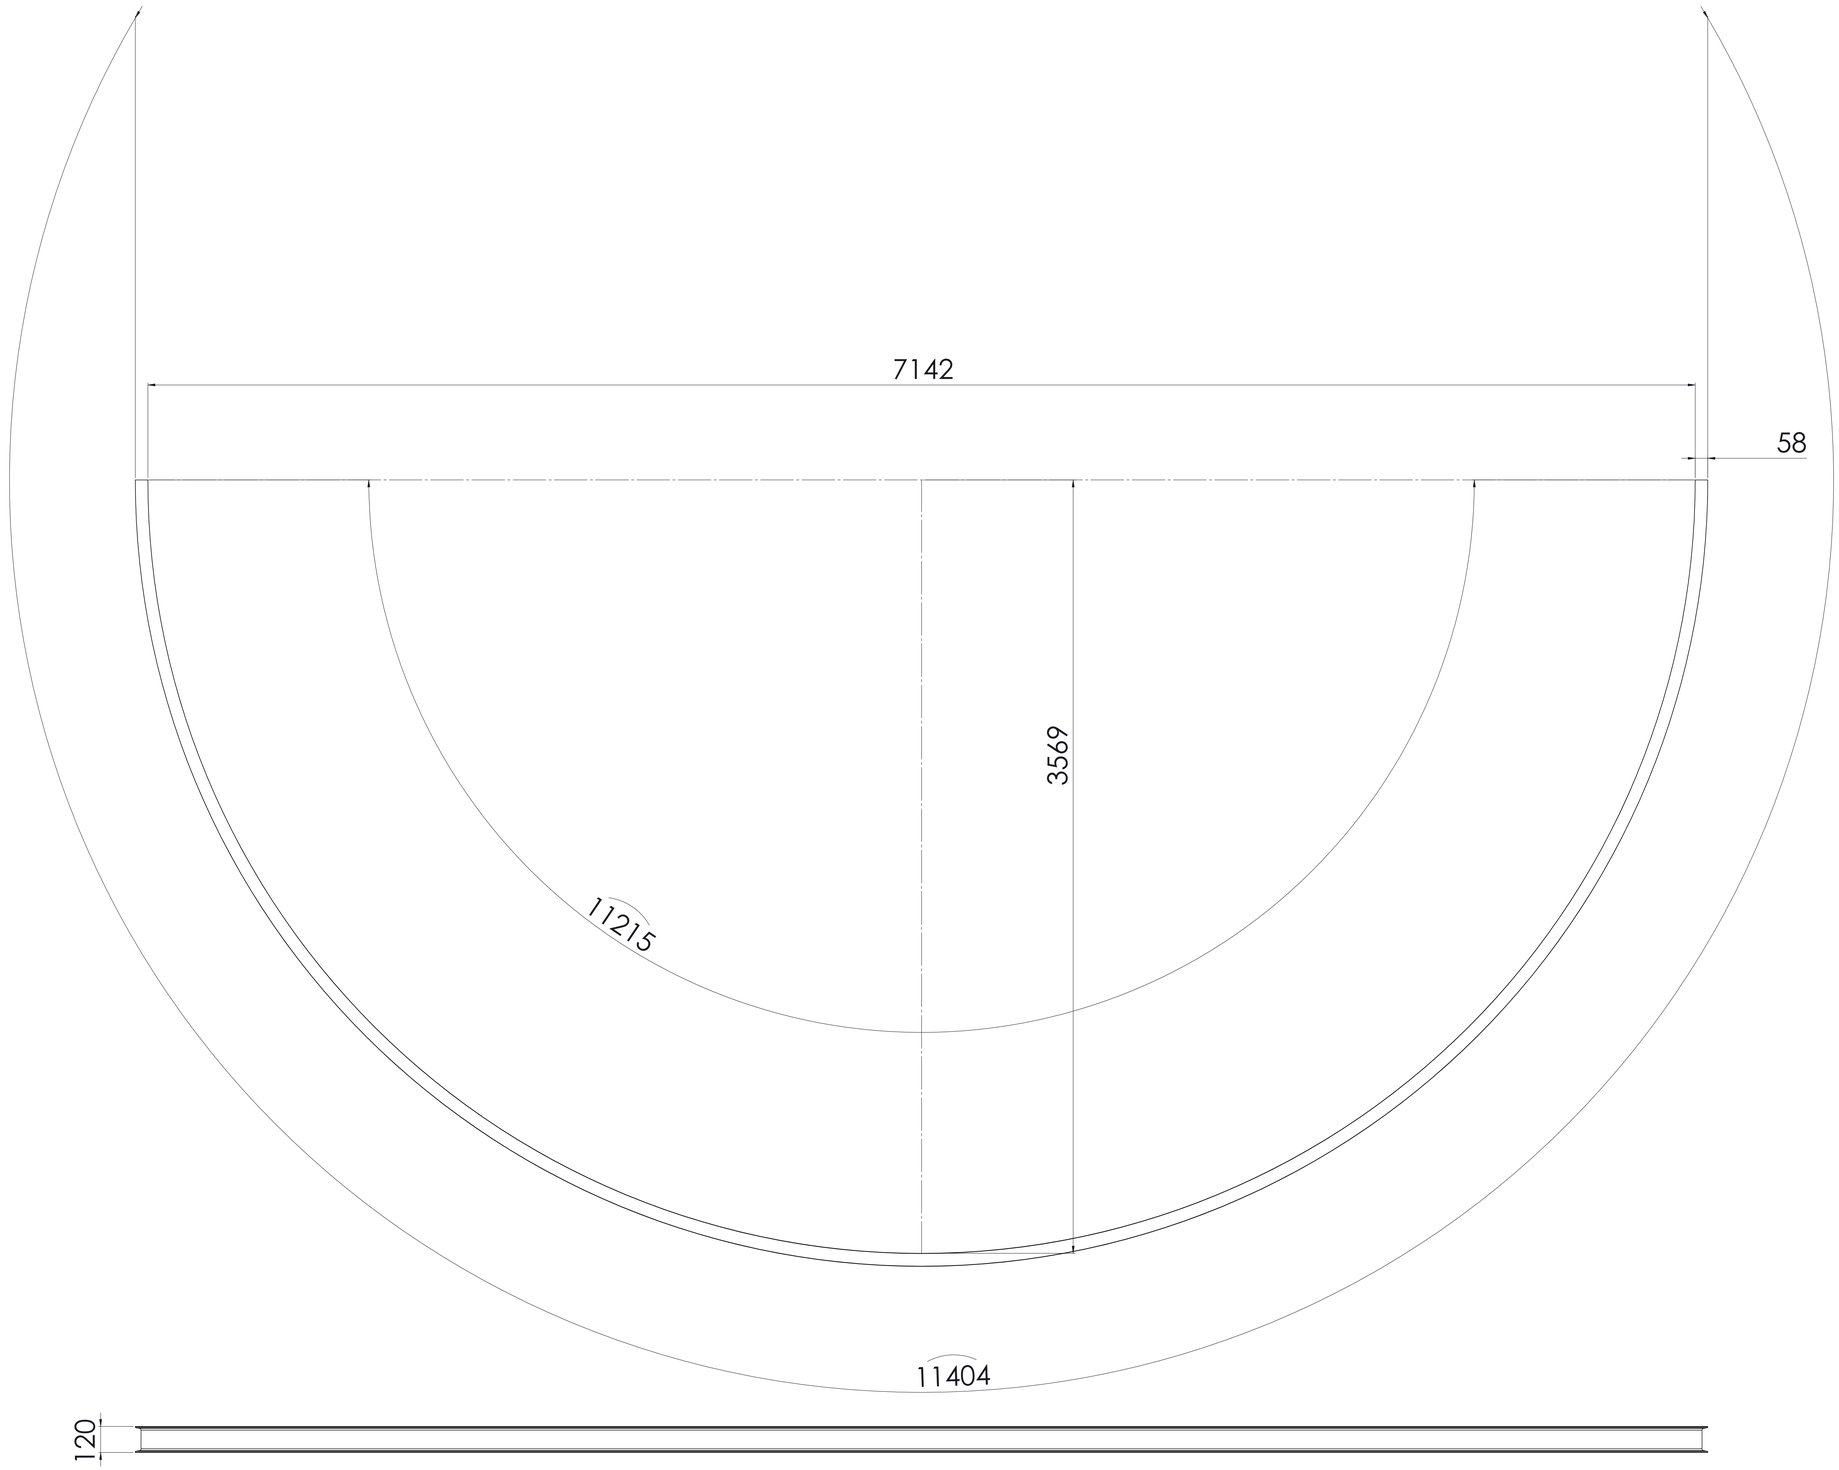


DRAWING NO: MVD-2-12

SHEET: 4/5

SR NO	NAME	DESCRIPTION	LENGTH	QTY
1	CURVED BEAM 2	120X60 I BEAM	8134 MM	1

STRIGHT LENGTH - 8034 MM

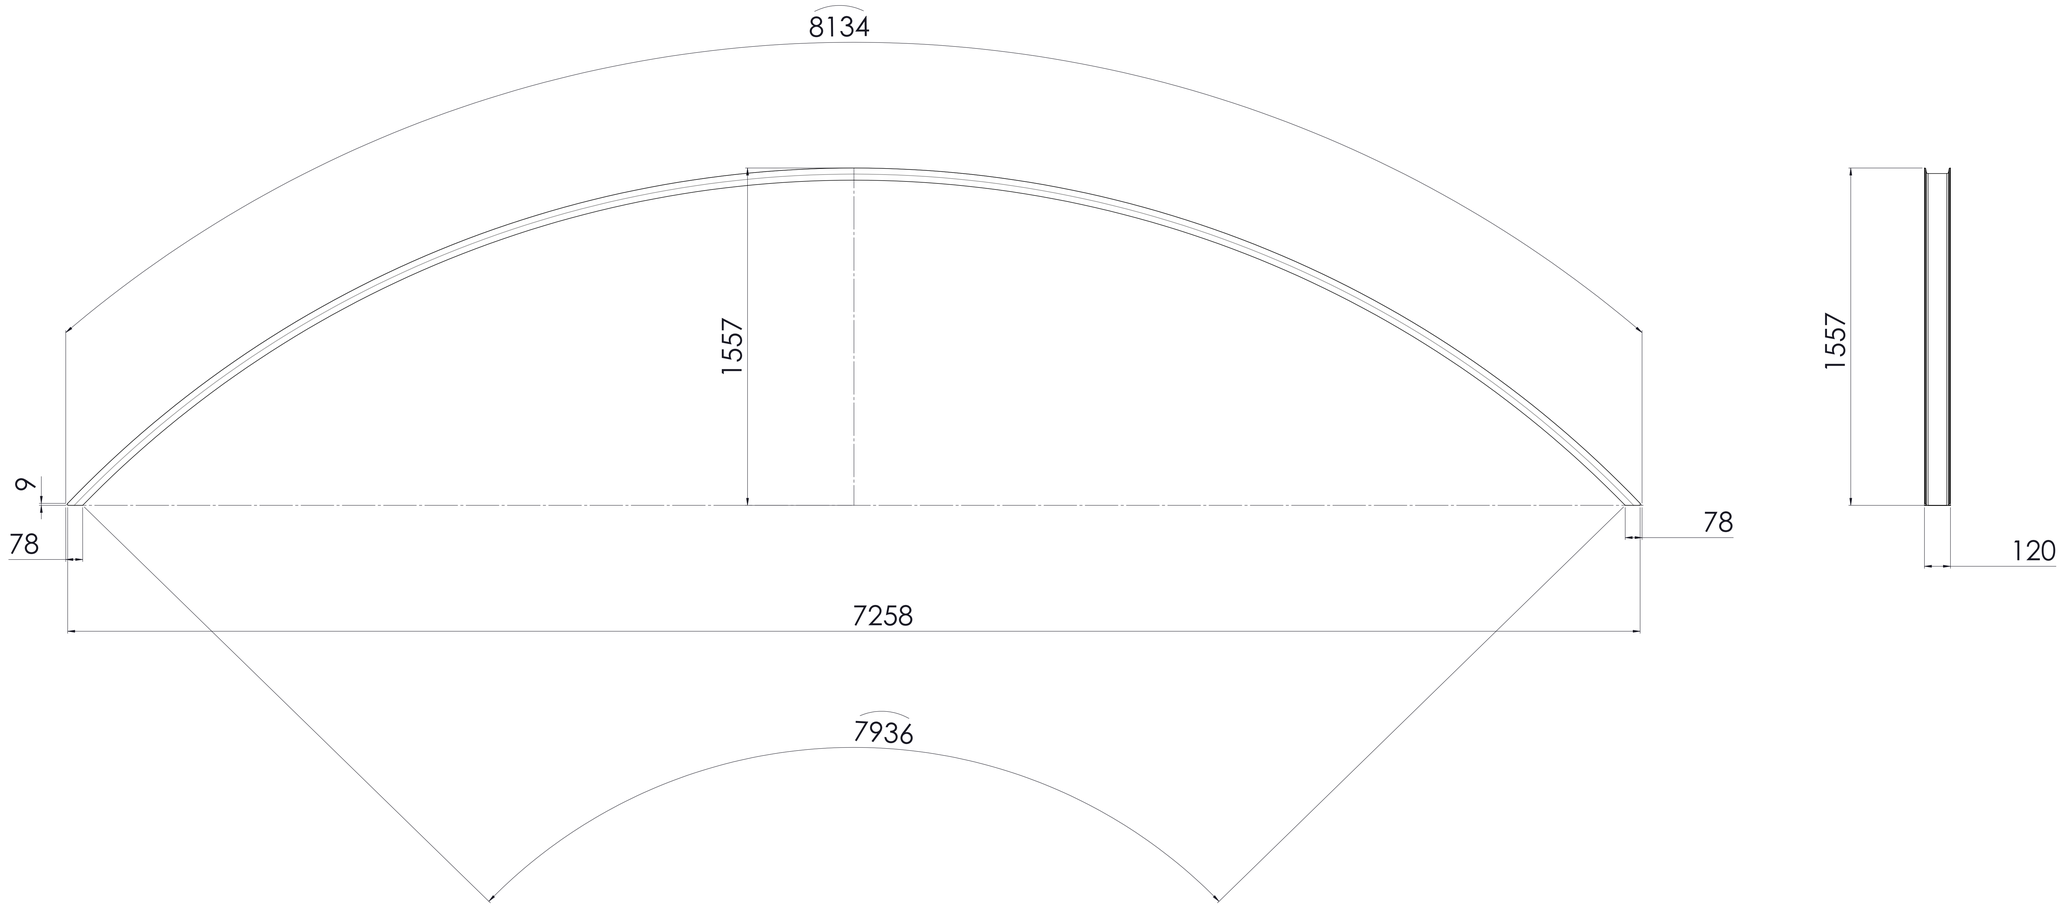

DRAWING NO: MVD-2 -17

SHEET: 5/5