
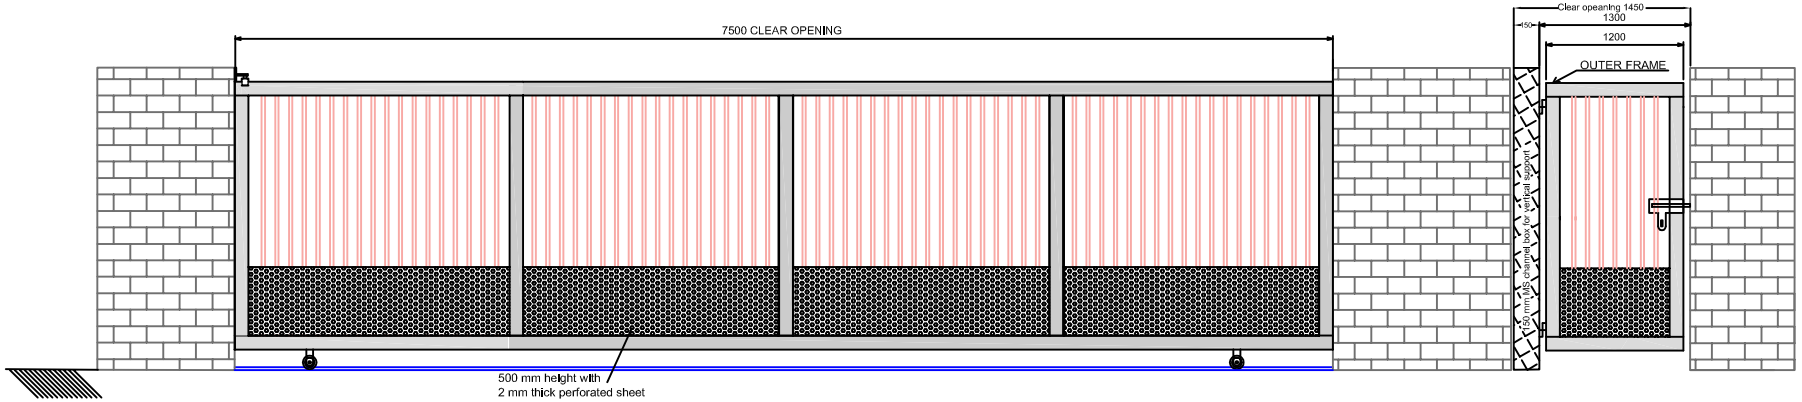


OUTSIDE VIEW

SLIDING DIRECTION →

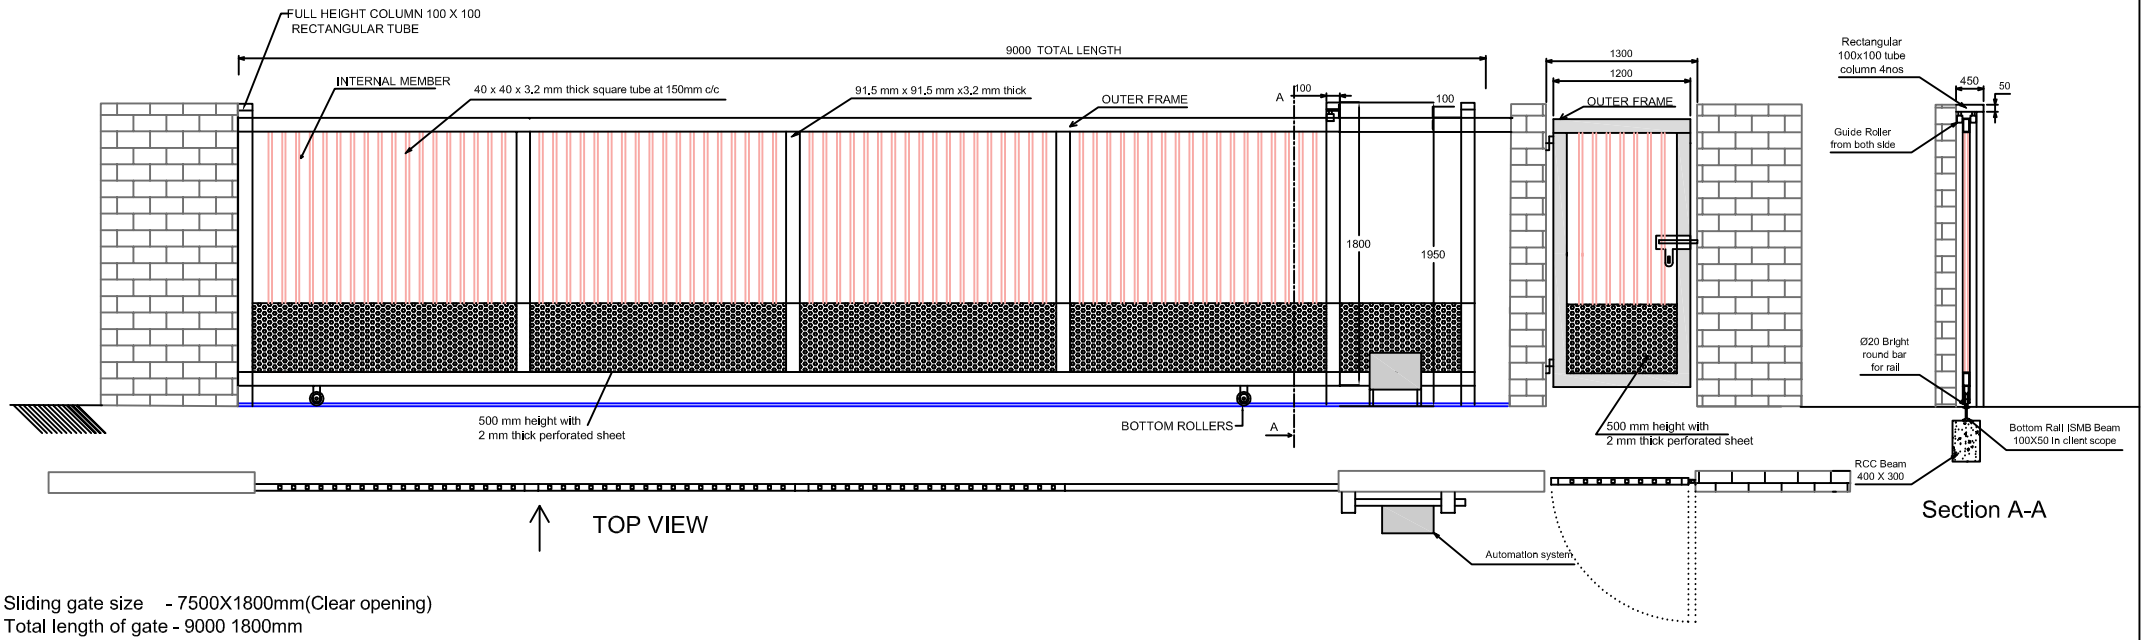

TOP VIEW

Section A-A

Sliding gate size - 7500X1800mm(Clear opening)
Total length of gate - 9000 1800mm
Wicket gate size - 1200X1800mm , Qty - 2 nos.
Saftey Photo cell - 1 pair.
No. Of Column - 4 nos.
Factory paint finish - Red oxide primer coat
NOTE :- Supply of 'c' channel for vertical support of wicket gate in NIHVA scope
Excavation and civil work for grouting of 'c' channel & I beam will be in client scope.

Drawn By:-A.K	Checked By	Approved By - Date		Date 23-07-14	Scale NTS
NIHVA TECHNOLOGIES PVT. LTD.			CLIENT — PMP Drive system Pvt Ltd.		
			DRG. No.NVA/PMP/09/14-15	Revision 00	Sheet 1-1