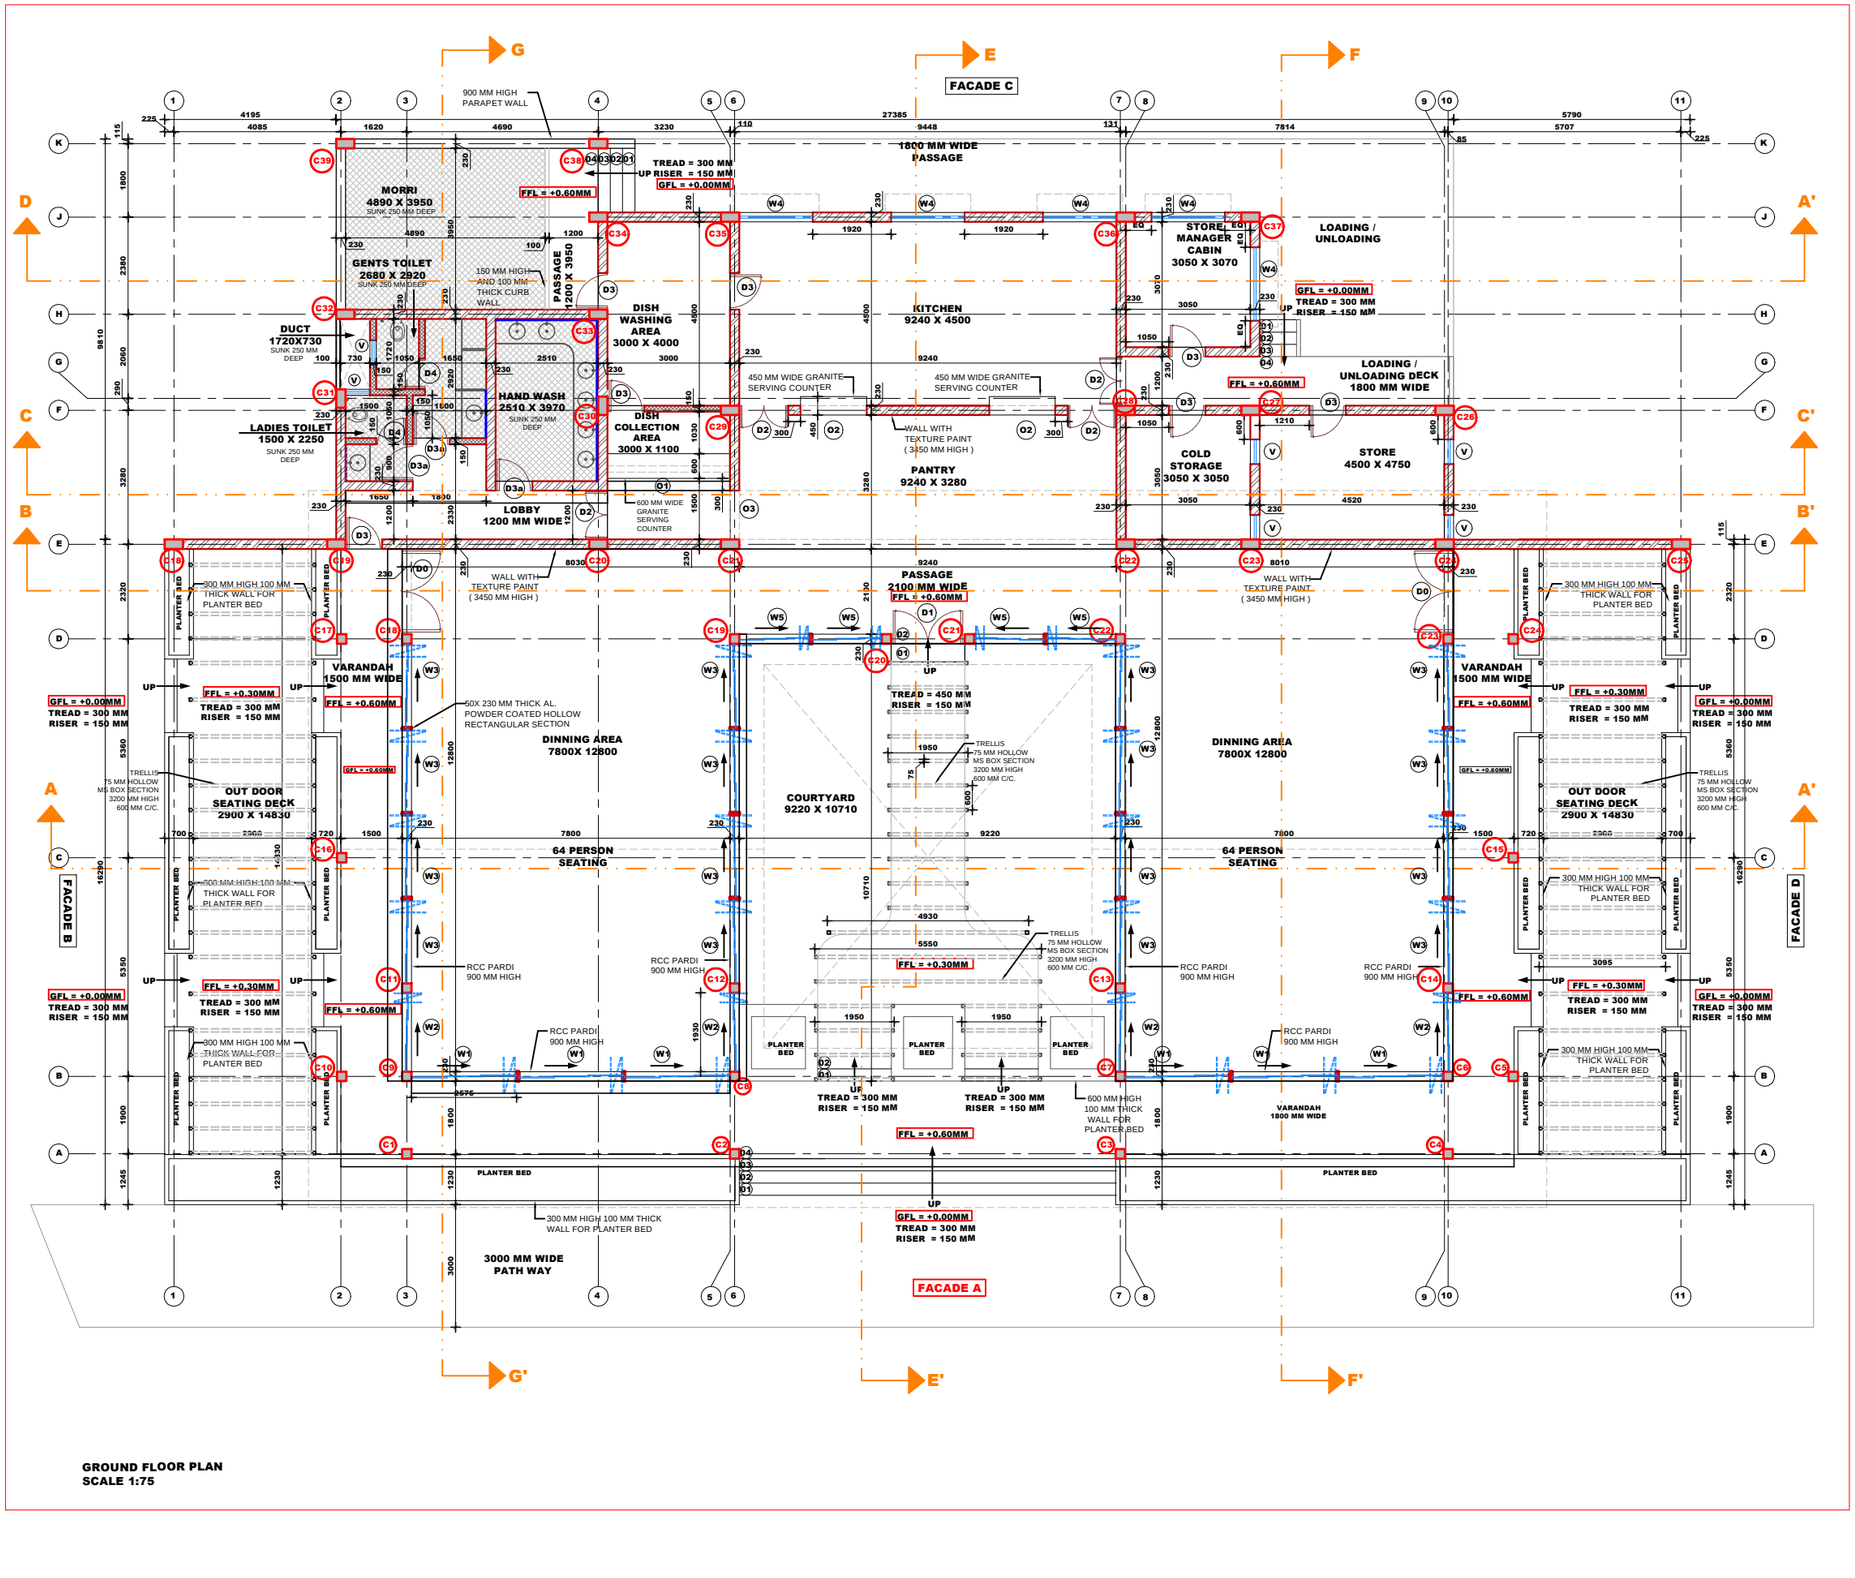



TENDER DRAWING

**project**
CATEEN OF ADOR WELDING

**owner**
ADOR WELDING

**drawing**
TENDER DRAWING
CANTEEN: FLOOR PLAN


• SACHIN P MUJUMDAR REGD. ARCHITECT CA/90/13058
• DEVEN V. GHOTGE REGD. ARCHITECT CA/90/12774
FOUNDER PARTNER
LATE SHRI.ABHAY B. SHARMA LATE SHRI.VIJAY V. GHOTGE
DESIGNED BY: ARCHITECTS UNITED
111/9, 14th Lane Prabhat Road, Pune–411 004
Ph.25441426 E–MAIL: architectunited@vsnl.net


| SCALE | DATE | DRAWN BY |
|---|---|---|
| 1:75 | 03.09.2021 | AKANKSHA |

REVISION

| RVN. NO. | DATE | DRAWN BY |
|---|---|---|
| | | |

job. no.
drg. no.
drg. nm. WKBLD_07_10_N7

**LEGEND:**

- 230 MM THICK CONCRETE BLOCK WALL
- 100 MM THICK CONCRETE BLOCK WALL
- 230 X 450 RCC COLUMN
- 230 X 230 RCC COLUMN

**DOOR SCHEDULE -**

| NAME | SIZE | LINTEL | DESCRIPTION |
|---|---|---|---|
| D0 | 2100X2150 | 3550 | GLASS DOOR (DOUBLE SHUTTER) |
| D1 | 1800X2150 | 3550 | GLASS DOOR (DOUBLE SHUTTER) |
| D2 | 1200X2150 | 2150 | METAL FRAME WITH FLUSH CORE SHUTTER (DOUBLE SHUTTER) |
| D3 | 900X2150 | 2150 | METAL FRAME WITH FLUSH CORE SHUTTER (SINGLE SHUTTER) |
| D3a | 900X2150 | 2150 | GRANITE FRAME WITH GRANITE ARCHITRAVE WITH FLUSH CORE SHUTTER |
| D4 | 750X2150 | 2150 | GRANITE FRAME WITH GRANITE ARCHITRAVE WITH FLUSH CORE SHUTTER |

**WINDOW SCHEDULE -**

| NAME | SIZE | | LINTEL | DESCRIPTION |
|---|---|---|---|---|
| W1 | 2575X2650 | 900 | 3550 | AL. POWDER COATED SLIDING FOLDING - 3 TRACK WINDOW - 3 GLASS SHUTTERS |
| W2 | 1930X2650 | 900 | 3550 | AL. POWDER COATED SLIDING FOLDING - 3 TRACK WINDOW - 3 GLASS SHUTTERS |
| W3 | 2055X2650 | 900 | 3550 | AL. POWDER COATED SLIDING FOLDING - 3 TRACK WINDOW - 3 GLASS SHUTTERS |
| W4 | 1800X1250 | 900 | 2150 | Al. Powder Coated Window - 3 Track Window- 2 Sliding Glass Shutter 1 Mosquito Net Shutter |
| W5 | 1720X2650 | 900 | 3550 | AL. POWDER COATED SLIDING FOLDING - 3 TRACK WINDOW - 3 GLASS SHUTTERS |
| V1 | 600X900 | 1250 | 2150 | Al. Powder Coated - With Glass Louvers |
| O1 | 3000X950 | 1200 | 3550 | CIVIL OPENING IN WALL ACTING AS WINDOW FOR DISH WASH AREA |
| O2 | 1620X950 | 1200 | 3550 | CIVIL OPENING IN WALL ACTING AS WINDOW FOR SERVING COUNTER OF KITCHEN |
| O3 | 1200X2150 | ----- | 3550 | CIVIL OPENING IN WALL |