




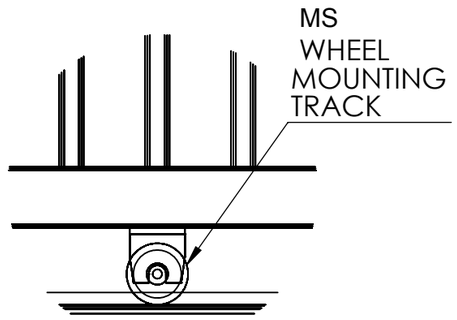


DETAIL I
SCALE 1 : 10

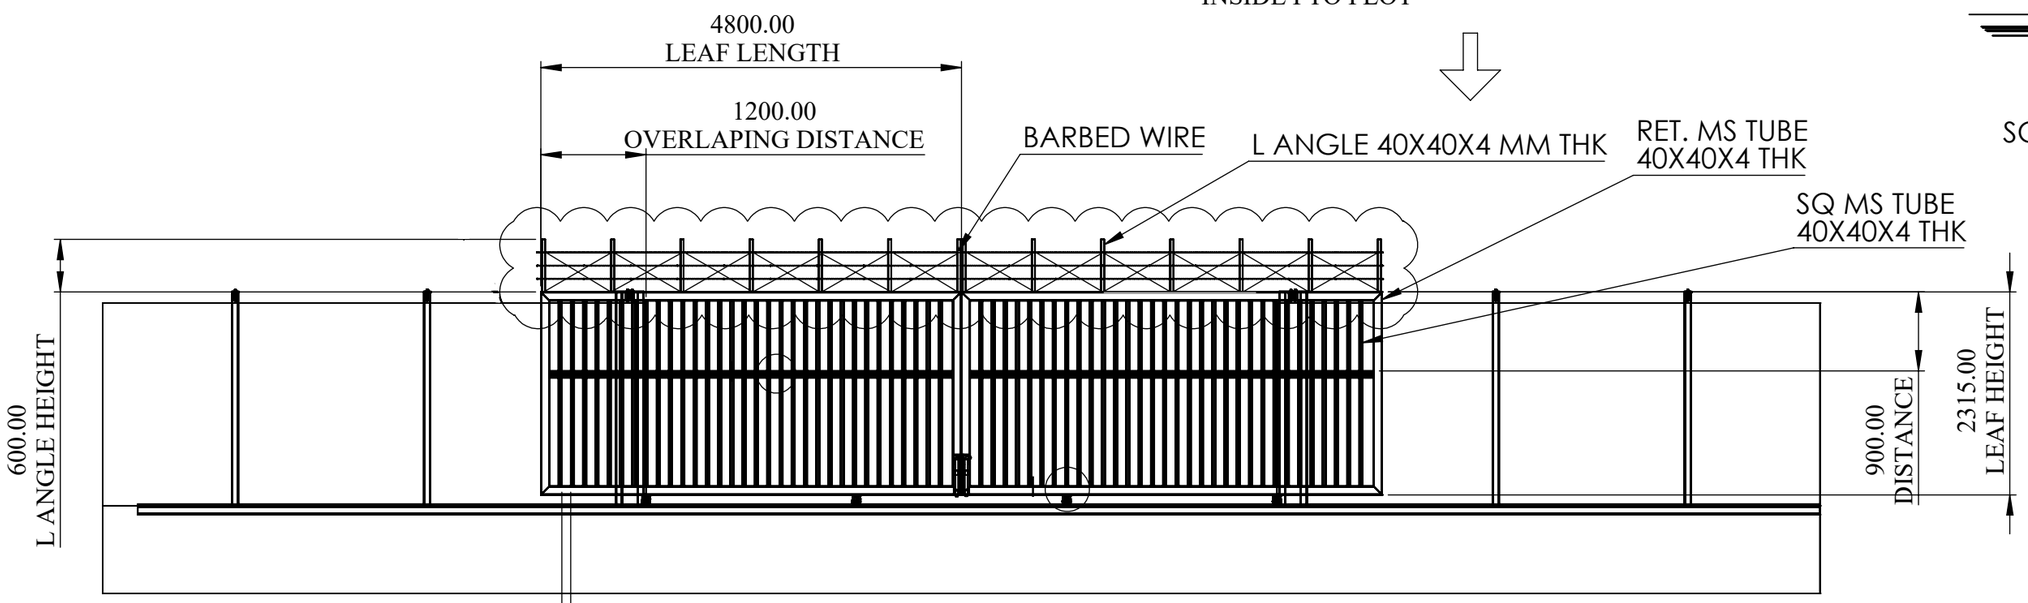

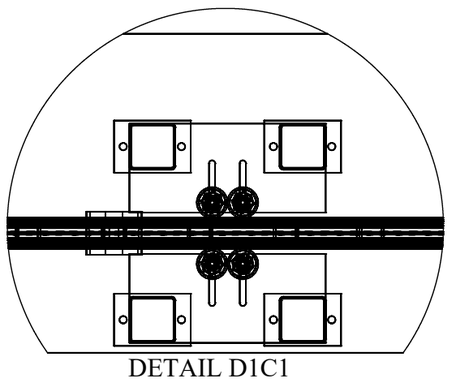


DETAIL D1C1
SCALE 1 : 10
POST1 AND NYLON
BEARING ASM

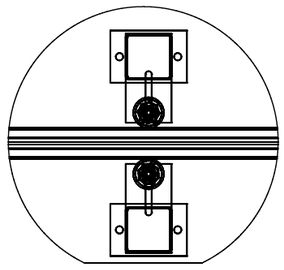


DETAIL A2
SCALE 1 : 10

POST 2 AND NYLON
BEARING ASM

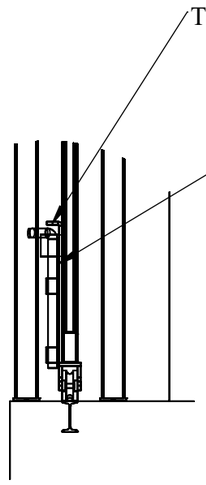

DETAIL SCALE E
1 : 20

TOWER BOLT LOCKING
ARRANGEMENT

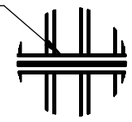

DETAIL H
SCALE 1 : 25

NOTE: 1) GA DRAWING TYPE NO 02
2) BARBED WIRE DESIGN IS ZIGZAG PATTERN.
3) Total Column- 8 (A1,B1,C1,D1 Same as right side add 4 Post)
4) 04 column posts when the gate is in the closed position.(C1,D1 & C2,D2)
5) 08 column posts when the gate is in the open position.(A1,B1,C1,D1 &A2,B2,C2,D2)

TITLE - GATE AUTOMATION				NIHVA TECHNOLOGIES PVT.LTD.PUNE
DWG NO - NTPL-290-PM			QTY - 1	Website - www.nihva.com
	NAME	SIGNATURE	DATE	PROJECT NO - NTPL-290-PM
DRAWN	V.B.		29-07-2025	PRODUCT - BY PARTING SLIDING GATE
CHK'D	B.S.		29-07-2025	SITE LOCATION - AMRAVATI
APPV'D	V.T.		29-07-2025	
if any queries contact - supportautomation@nihva.com				REVISION -
ALL DIMENSION ARE IN mm			A3	SCALE - SHEET 1 OF 1