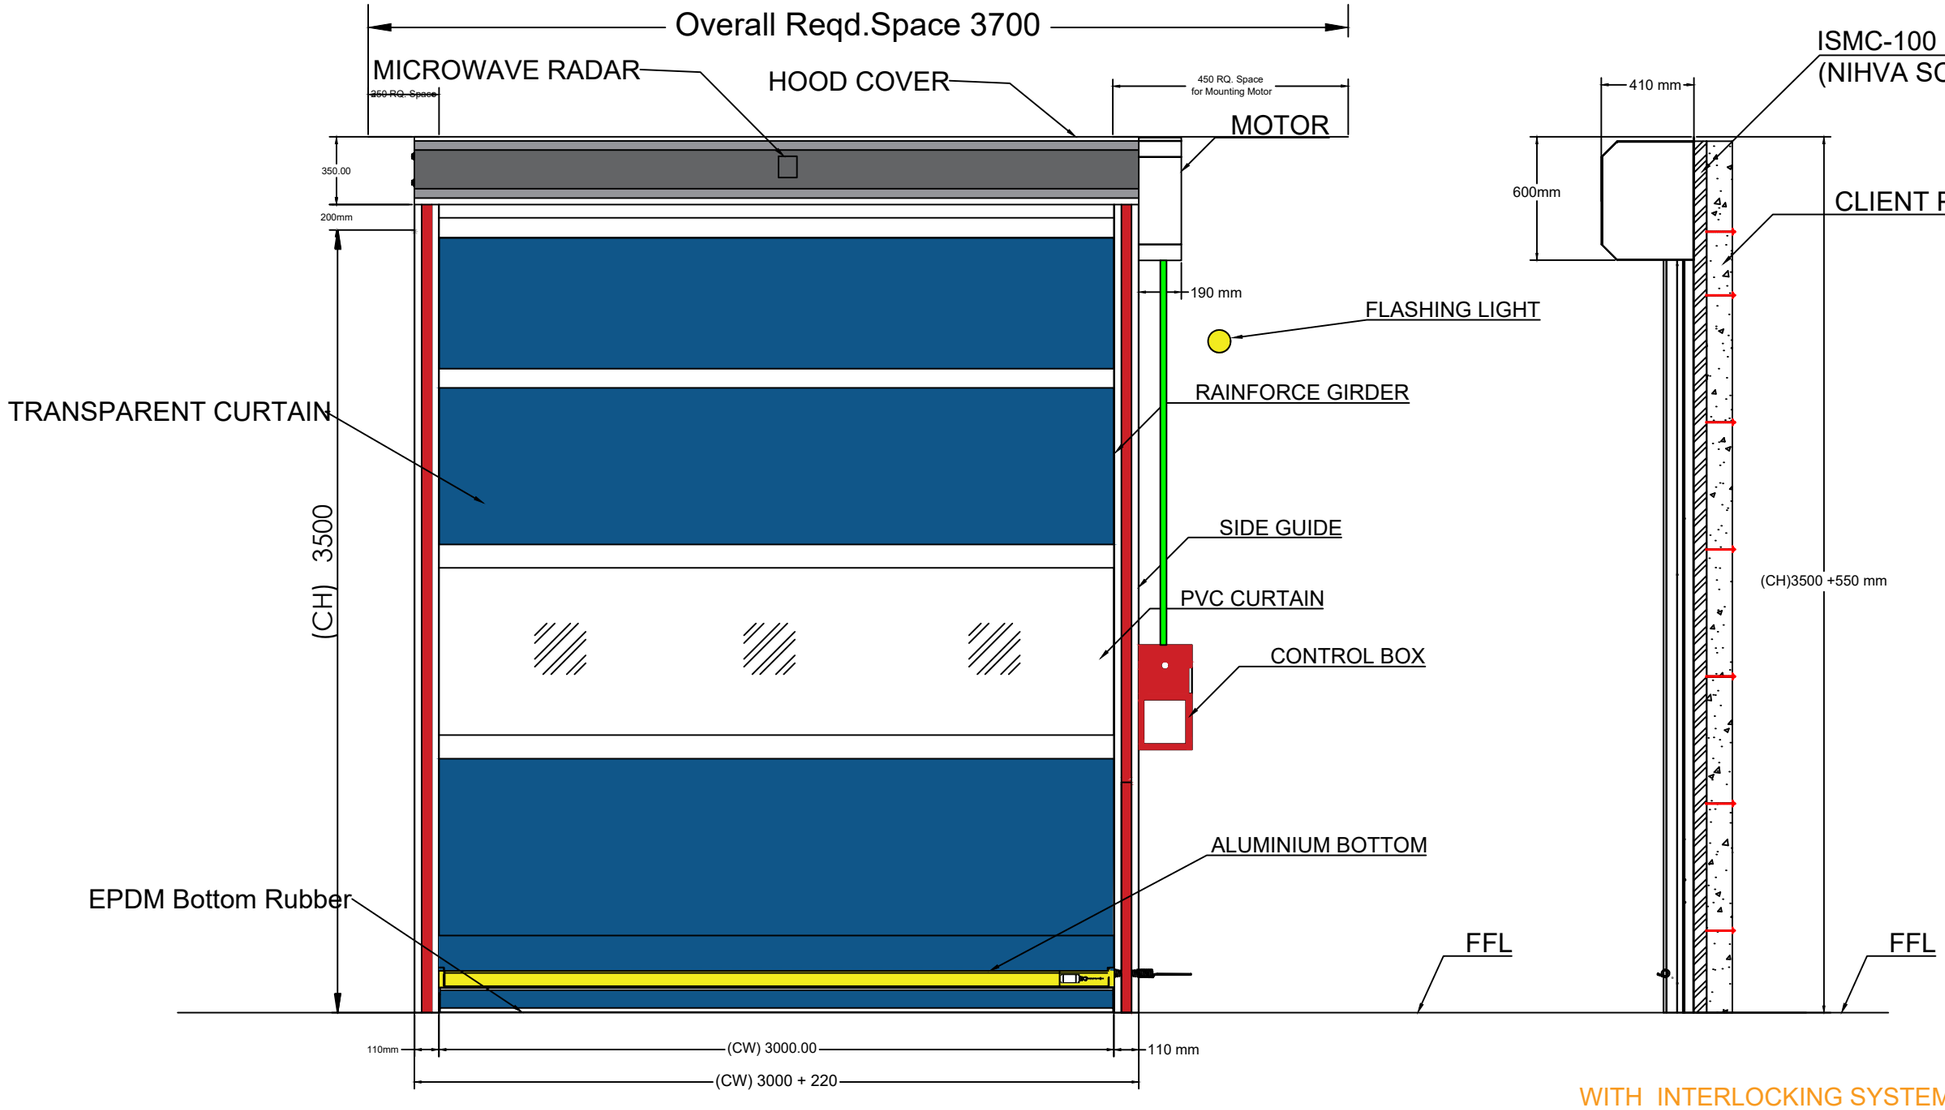



WITH INTERLOCKING SYSTEM

## TECHNICAL SPECIFICATION :

| SR. | SPECIFICATIONS | DETAILS |
|---|---|---|
| 1 | Control Panel | LED Display Servo Controller : -<br>Operating Speed (Adjustable) : 1.4~2.5 min/<br>Working Temperature : -35 degree to 65 degree -<br>Water Resistant : IP65 Make IDER, manufactured under European Standards |
| 2 | Drive | IDER Make ,CE Certified |
| 3 | Motor Power ,Torque | Power : 1.1 kW Torque : 65 Nm |
| 4 | Door Travel Speed | Opening: 2 m/Sec & Closing:0.9m/Sec |
| 5 | Safety Device | Safety Photocell Pair & Safety Edges |
| 6 | Surface Finish | As Per Client Requirement |
| 7 | Accessories | Radar Sensor ,Magnetic Loop Detector ,Flashing Light Buzzer |

## NOTE:

All Cables & Ele.Conduits to be provided by NIHVA
(1) All Civil Work in Client Scope
(2) Required M.S.Structure & Fittings at NIHVA Scope

| Sr | Clear Width (CW) | Clear Height (CH) | QTY |
|---|---|---|---|
| 1 | **3000** | **3500** | 2 |

This drawing & design is the property of NIHVA TECHNOLOGIES. Not to be sold or copied to any other concern.


TITLE: HIGH SPEED DOOR WITH SENSOR GA DRAWING


| | NAME | SIGN | DATE |
|---|---|---|---|
| DRAWN | S.J | | 18.01.2024 |
| CHECK | A.K | | 18.01.2024 |
| APPRD. | V.T | | 18.01.2024 |


NIHVA TECHNOLOGIES PVT. LTD.
NIHVA TECHNOLOGIES PVT. LTD. PUNE
Tel : 020 66304033
Email:- info@nihva.com
Website:- www.nihva.com


If any queries contact : projectsupport@nihva.com

CLIENT - RINAC
PROJECT - HIGH SPEED DOOR
FORMAT NO - NIHVA-DD-F-03
DWG. NO. : NIHVA/23-24/00XX
REV- R00
ALL DIMENSION ARE IN mm
SCALE: NTS
WT:
SHEET:

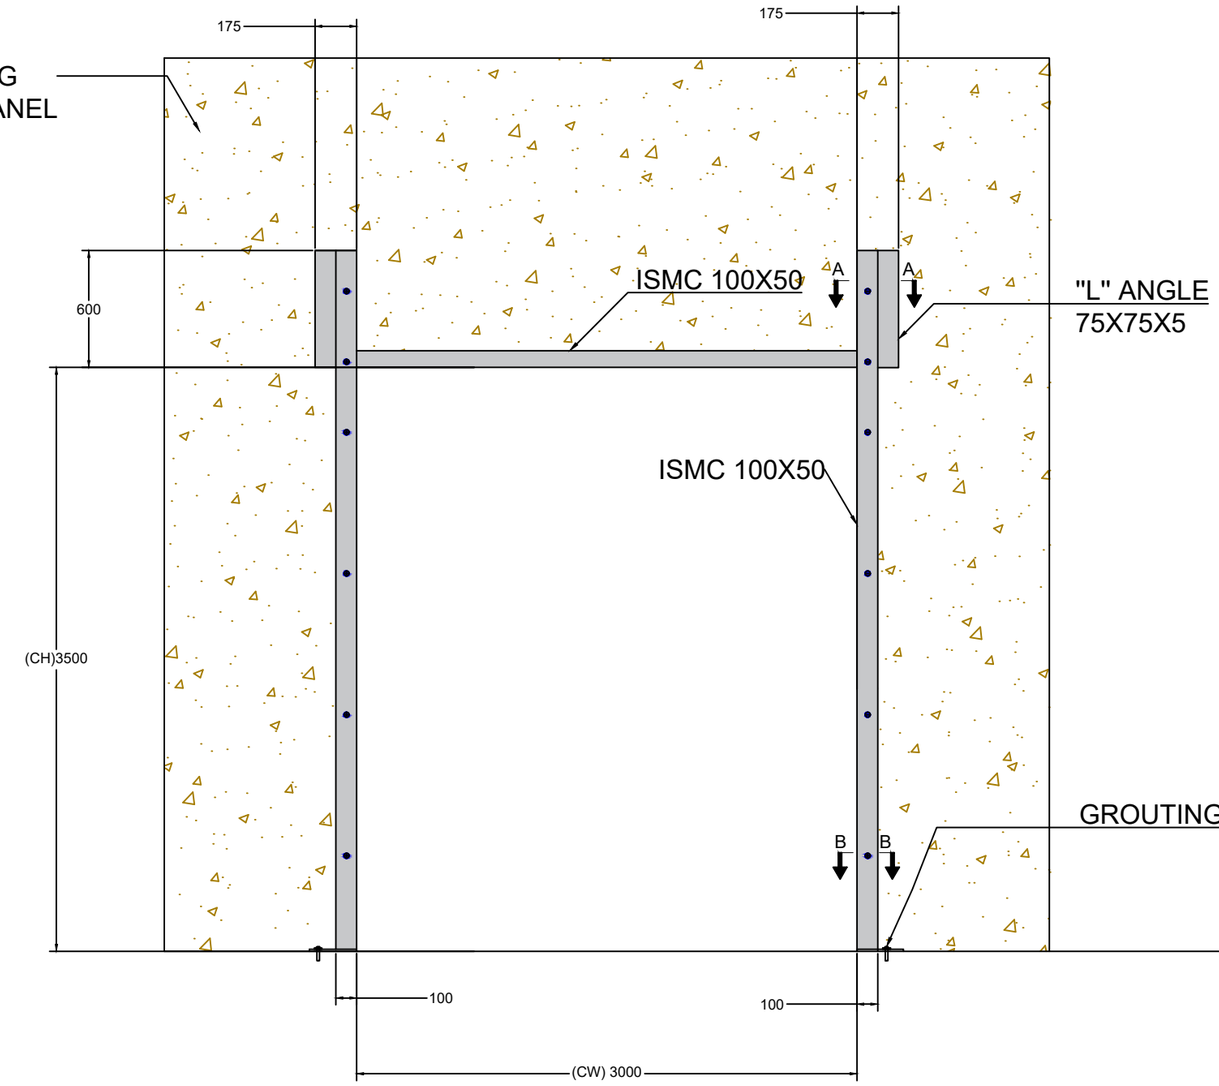

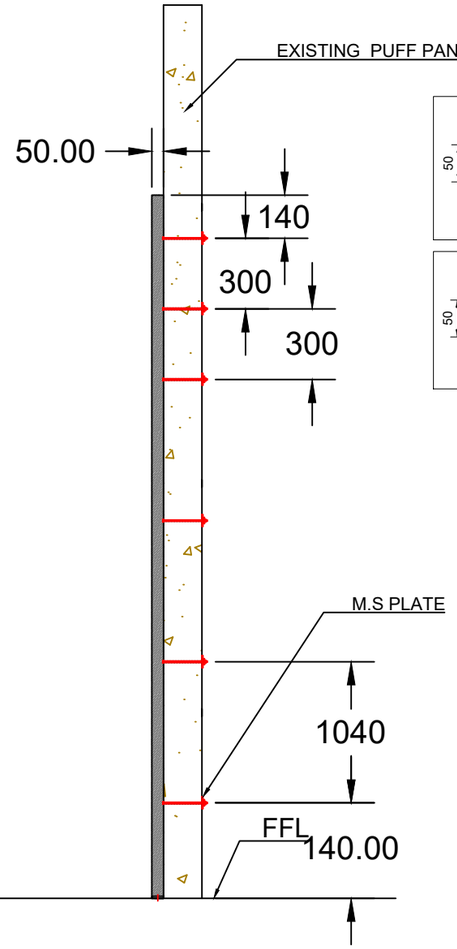


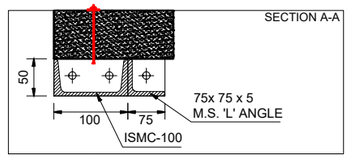

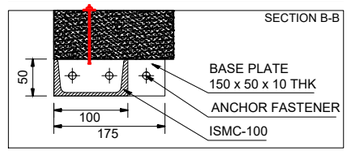M.S. STRUCTURE DETAILS

| Sr | Description | Clear Width (CW) | Clear Height (CH) | QTY |
|---|---|---|---|---|
| 1 | HSD With Sensor | **3000** | **3500** | 2 |

This drawing & design is the property of NIHVA TECHNOLOGIES. Not to be sold or copied to any other concern.
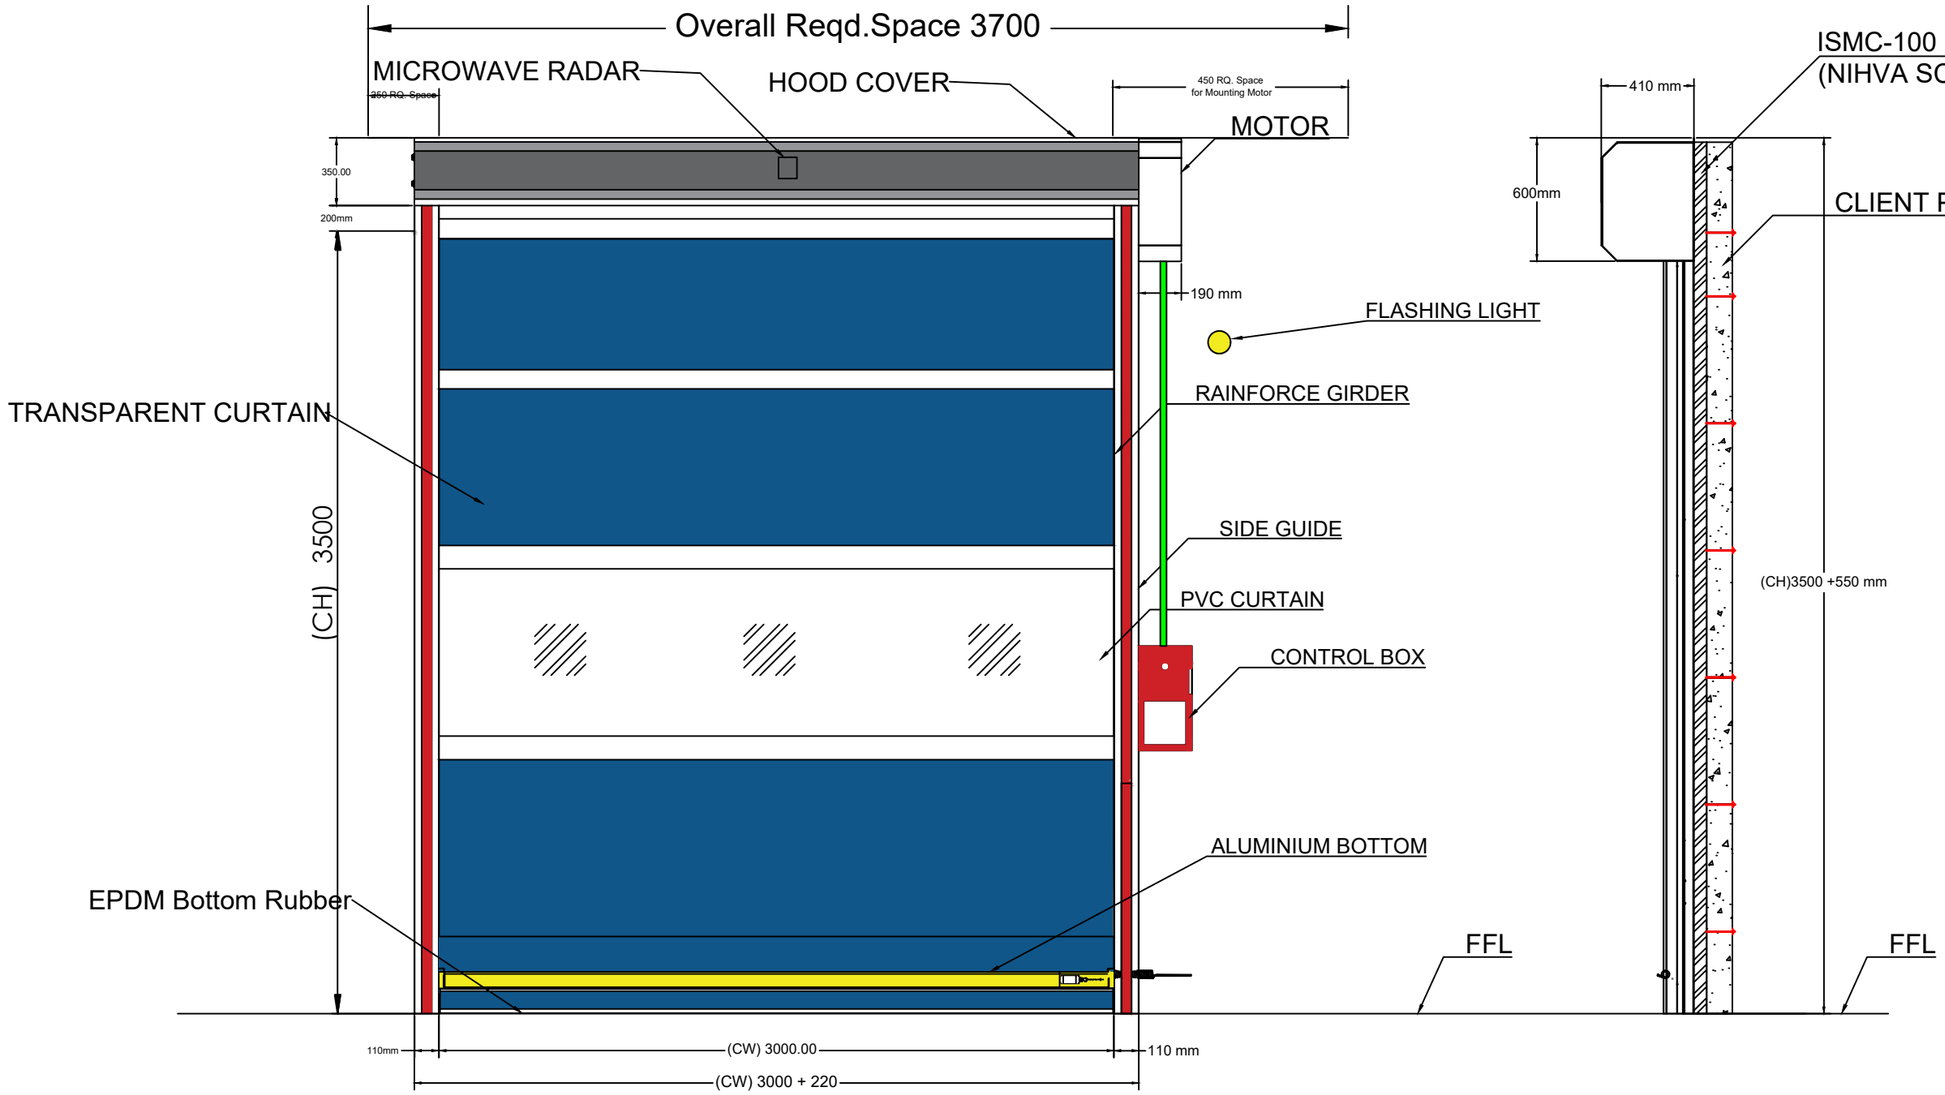
| TITLE | HIGH SPEED DOOR STRUCTURE DRAWING | | | NIHVA TECHNOLOGIES PVT. LTD. PUNE<br>Tel : 020 66304033<br>Email:- info@nihva.com<br>Website:- www.nihva.com |
|---|---|---|---|---|
| | NAME | SIGN | DATE | |
| DRAWN | S.J | | 18.01.2024 | CLIENT - RINAC |
| CHECK | A.K | | 18.01.2024 | PROJECT - HIGH SPEED DOOR ST. |
| APPRD. | V.T | | 18.01.2024 | FORMAT NO - NIHVA-DD-F-03 |
| If any queries contact : projectsupport@nihva.com | | | | DWG. NO. : NIHVA/23-24/00XX / REV- R00 |
| ALL DIMENSION ARE IN mm | | | | SCALE: NTS / WT: / SHEET: |




## TECHNICAL SPECIFICATION :

| SR. | SPECIFICATIONS | DETAILS |
|---|---|---|
| 1 | Control Panel | LED Display Servo Controller : -<br>Operating Speed (Adjustable) : 1.4~2.5 min/<br>Working Temperature : -35 degree to 65 degree -<br>Water Resistant : IP65 Make IDER, manufactured under European Standards |
| 2 | Drive | IDER Make ,CE Certified |
| 3 | Motor Power ,Torque | Power : 1.1 kW Torque : 65 Nm |
| 4 | Door Travel Speed | Opening: 2 m/Sec & Closing:0.9m/Sec |
| 5 | Safety Device | Safety Photocell Pair & Safety Edges |
| 6 | Surface Finish | As Per Client Requirement |
| 7 | Accessories | Radar Sensor ,Magnetic Loop Detector ,Flashing Light Buzzer |

## NOTE:

All Cables & Ele.Conduits to be provided by NIHVA
(1) All Civil Work in Client Scope
(2) Required M.S.Structure & Fittings at NIHVA Scope

| Sr | Clear Width (CW) | Clear Height (CH) | QTY |
|---|---|---|---|
| 1 | **3000** | **3500** | 1 |

This drawing & design is the property of NIHVA TECHNOLOGIES. Not to be sold or copied to any other concern.


TITLE: HIGH SPEED DOOR WITH SENSOR GA DRAWING


| | NAME | SIGN | DATE |
|---|---|---|---|
| DRAWN | S.J | | 18.01.2024 |
| CHECK | A.K | | 18.01.2024 |
| APPRD. | V.T | | 18.01.2024 |


NIHVA TECHNOLOGIES PVT. LTD.
NIHVA TECHNOLOGIES PVT. PUNE
Tel : 020 66304033
Email:- info@nihva.com
Website:- www.nihva.com


If any queries contact : projectsupport@nihva.com

CLIENT - RINAC
PROJECT - HIGH SPEED DOOR
FORMAT NO - NIHVA-DD-F-03
DWG. NO. : NIHVA/23-24/00XX
REV- R00
ALL DIMENSION ARE IN mm
SCALE: NTS
WT:
SHEET:

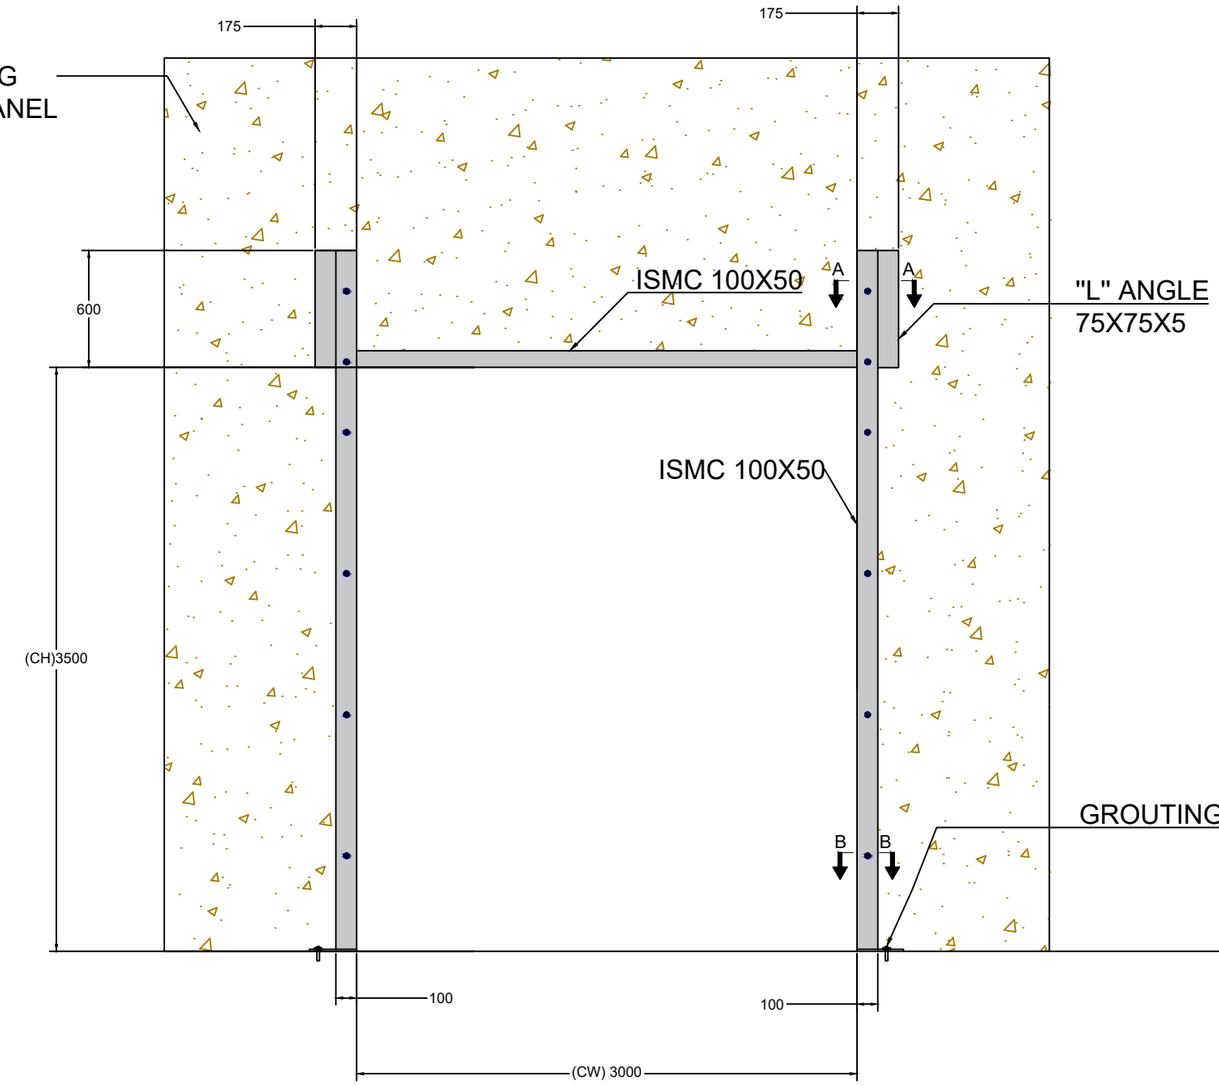

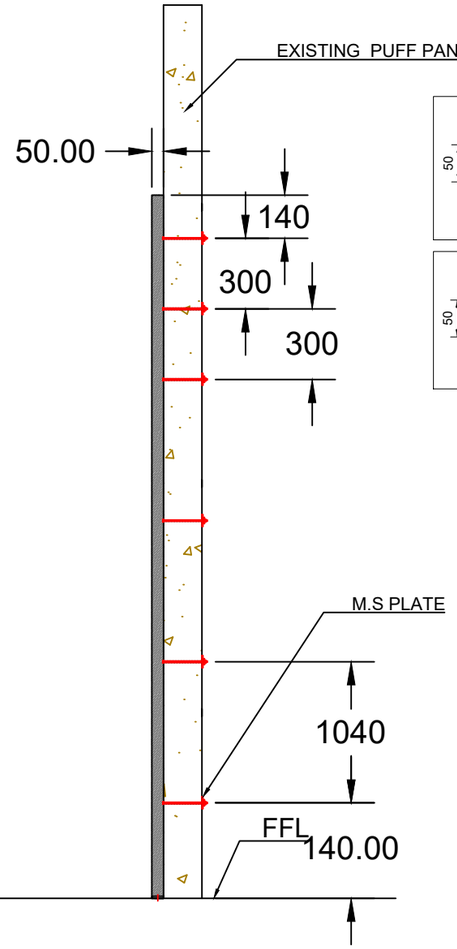
M.S. STRUCTURE DETAILS
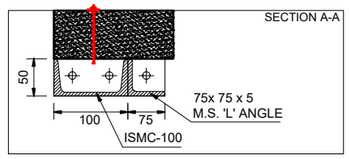
| Sr | Description | Clear Width (CW) | Clear Height (CH) | QTY |
|---|---|---|---|---|
| 1 | HSD With Sensor | **3000** | **3500** | 1 |

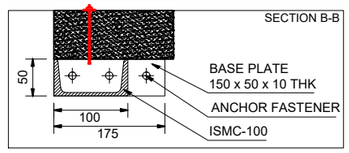This drawing & design is the property of NIHVA TECHNOLOGIES. Not to be sold or copied to any other concern.

TITLE HIGH SPEED DOOR STRUCTURE DRAWING

NIHVA TECHNOLOGIES PVT. LTD.

NIHVA TECHNOLOGIES PVT. LTD. PUNE
Tel : 020 66304033
Email:- info@nihva.com
Website:- www.nihva.com

| | NAME | SIGN | DATE |
|---|---|---|---|
| DRAWN | S.J | | 18.01.2024 |
| CHECK | A.K | | 18.01.2024 |
| APPRD. | V.T | | 18.01.2024 |

CLIENT - RINAC

PROJECT - HIGH SPEED DOOR ST.

FORMAT NO - NIHVA-DD-F-03

If any queries contact : projectsupport@nihva.com

DWG. NO. : NIHVA/23-24/00XX


REV- R00

ALL DIMENSION ARE IN mm

SCALE: NTS

WT:

SHEET:

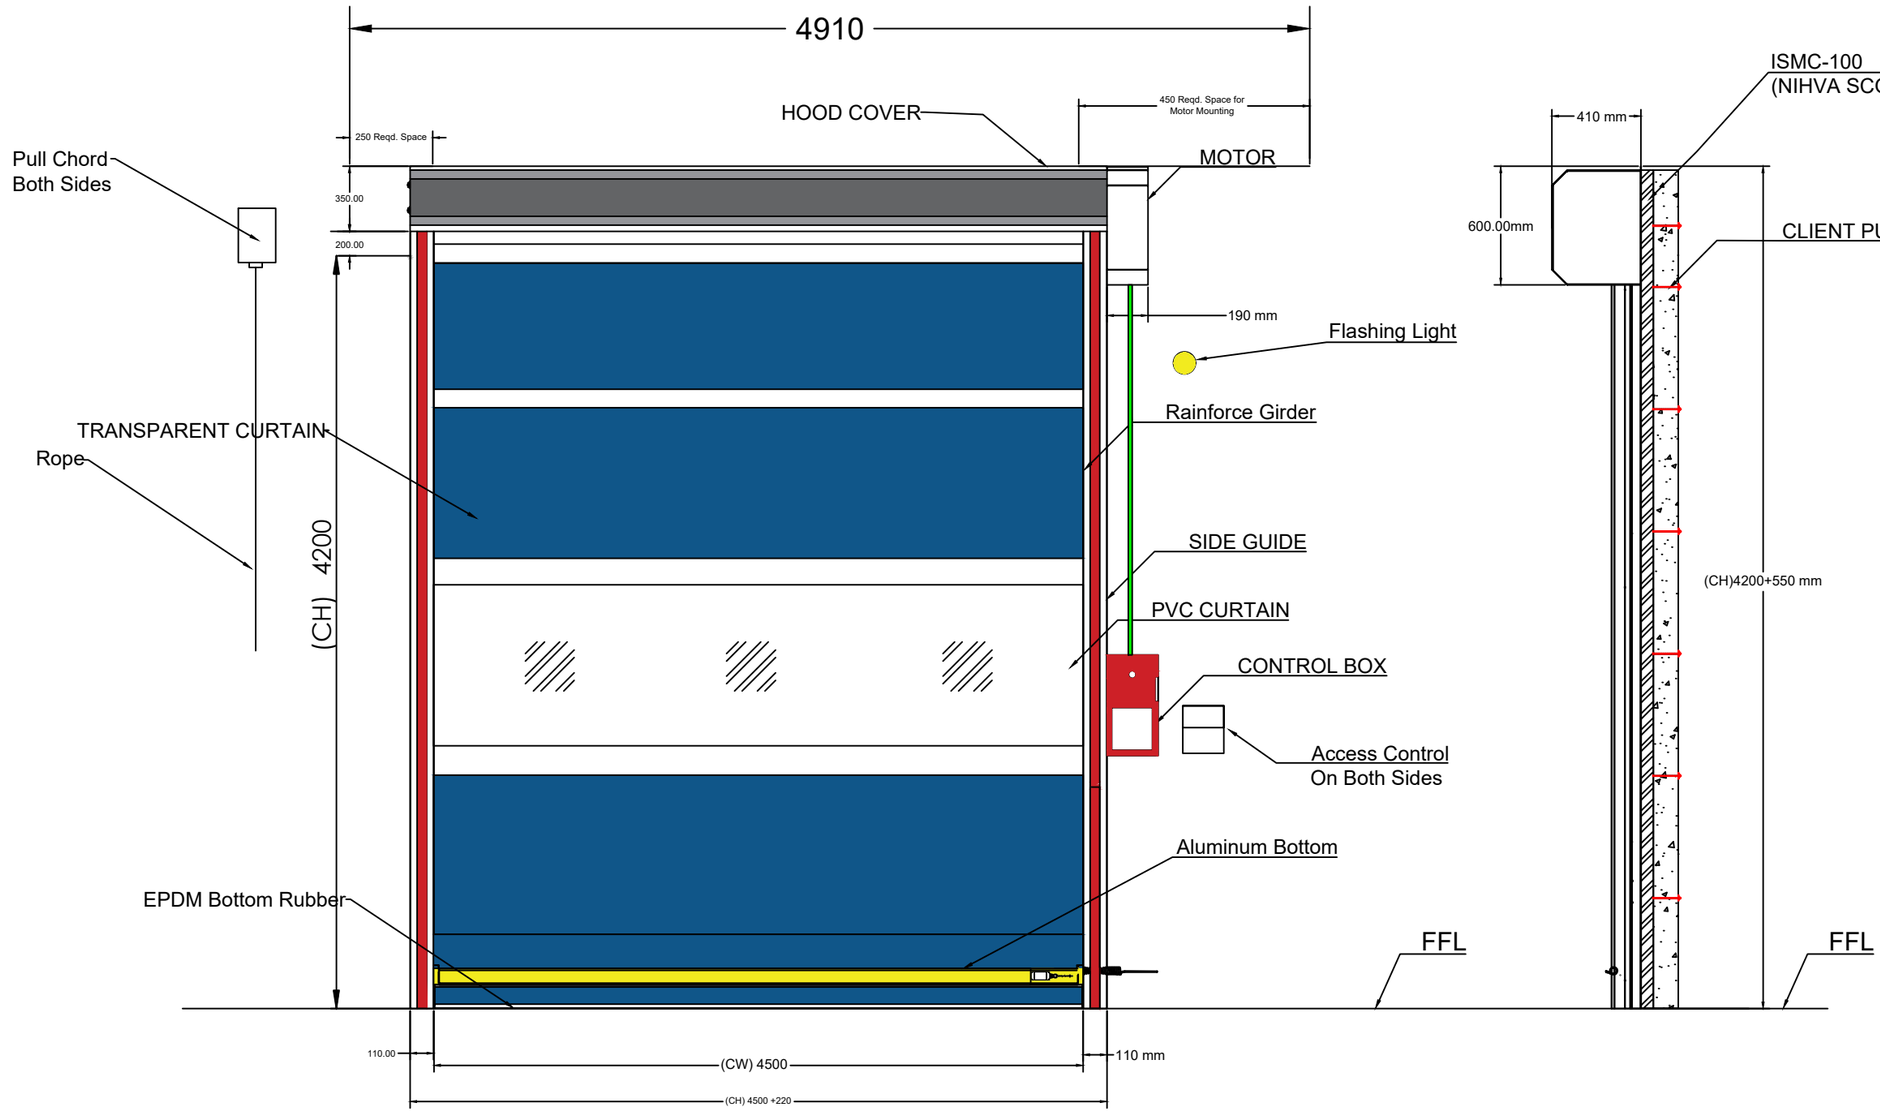


## TECHNICAL SPECIFICATION :

| SR. | SPECIFICATIONS | DETAILS |
|---|---|---|
| 1 | Control Panel | LED Display Servo Controller : - Operating Speed (Adjustable) : 1.4~2.5 min/ Working Temperature : -35 degree to 65 degree - Water Resistant : IP65 Make IDER, manufactured under European Standards |
| 2 | Drive | IDER Make ,CE Certified |
| 3 | Motor Power ,Torque | Power : 1.1 kW Torque : 65 Nm |
| 4 | Door Travel Speed | Opening: 2 m/Sec & Closing:0.9m/Sec |
| 5 | Safety Device | Safety Photocell Pair & Safety Edges |
| 6 | Surface Finish | As Per Client Requirement |
| 7 | Accessories | Flashing Light with Buzzer , Pull Chord |

## NOTE:

(1) All Cables & Ele.Conduits to be provided by NIHVA
(2) All Civil Work in Client Scope
(3) Required M.S.Structure & Fittings at NIHVA Scope

| Sr | Clear Width (CW) | Clear Height (CH) | QTY |
|---|---|---|---|
| 1 | 4500 | 4200 | 1 |


This drawing & design is the property of NIHVA TECHNOLOGIES. Not to be sold or copied to any other concern.


| TITLE | HIGH SPEED DOOR WITH ACCESS CONTROL GA DRAWING | | |
|---|---|---|---|
| | NAME | SIGN | DATE |
| DRAWN | S.J | | 19.01.2024 |
| CHECK | A.K | | 19.01.2024 |
| APPRD. | V.T | | 19.01.2024 |

NIHVA TECHNOLOGIES PVT. LTD.
NIHVA TECHNOLOGIES PVT. PUNE
Tel : 020 66304033
Email:- info@nihva.com
Website:- www.nihva.com

If any queries contact : projectsupport@nihva.com

CLIENT - RINAC
PROJECT - HIGH SPEED DOOR
FORMAT NO - NIHVA-DD-F-03
DWG. NO. : NIHVA/23-24/00XX
REV- R00
ALL DIMENSION ARE IN mm
SCALE: NTS
WT:
SHEET:

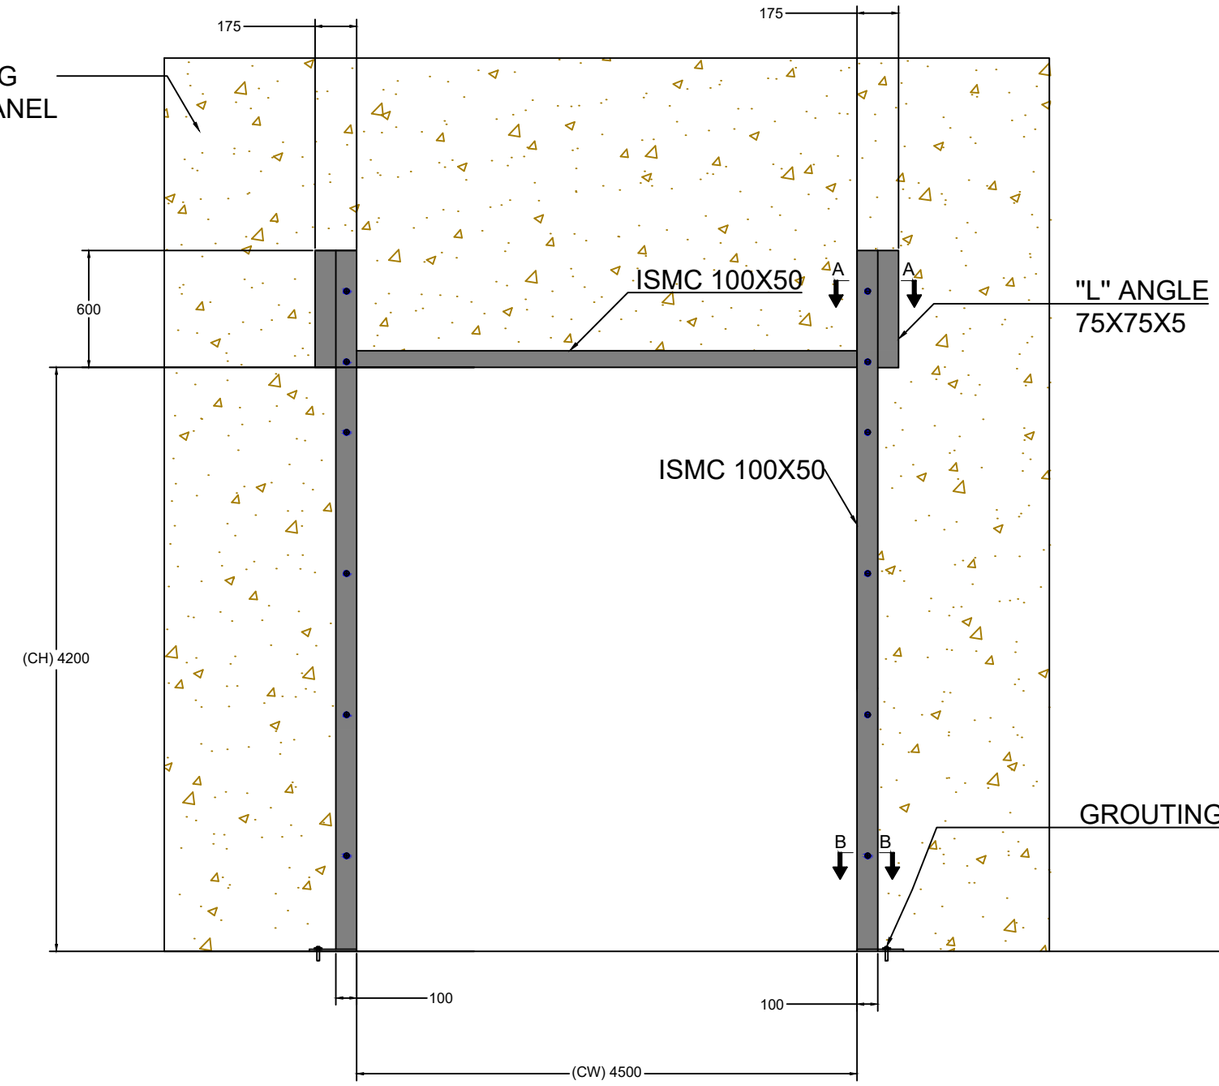

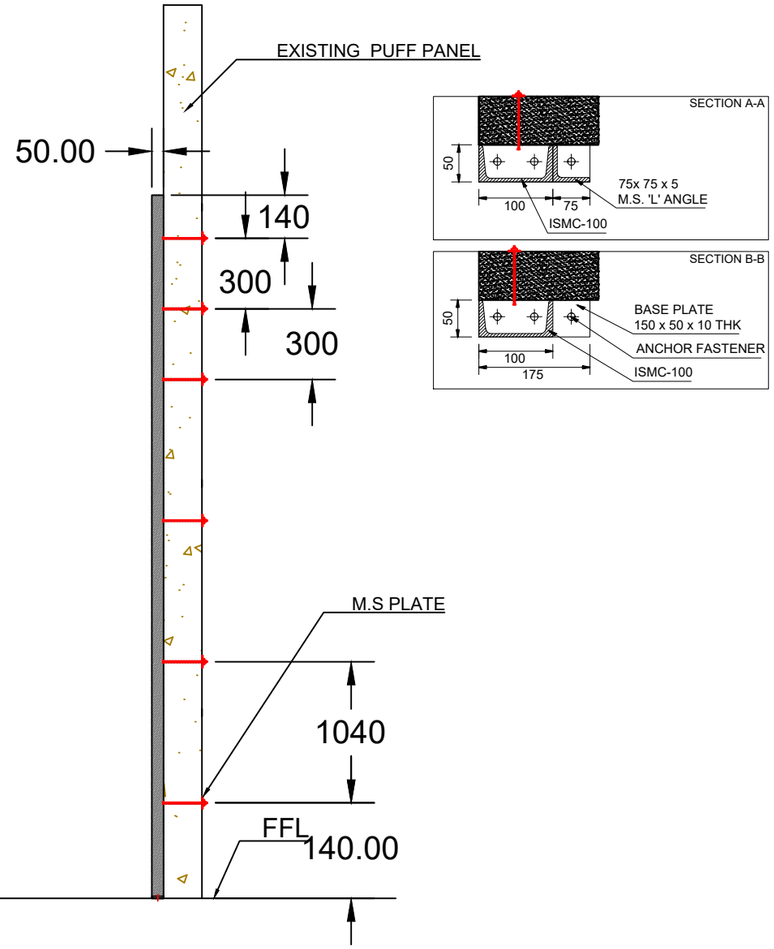



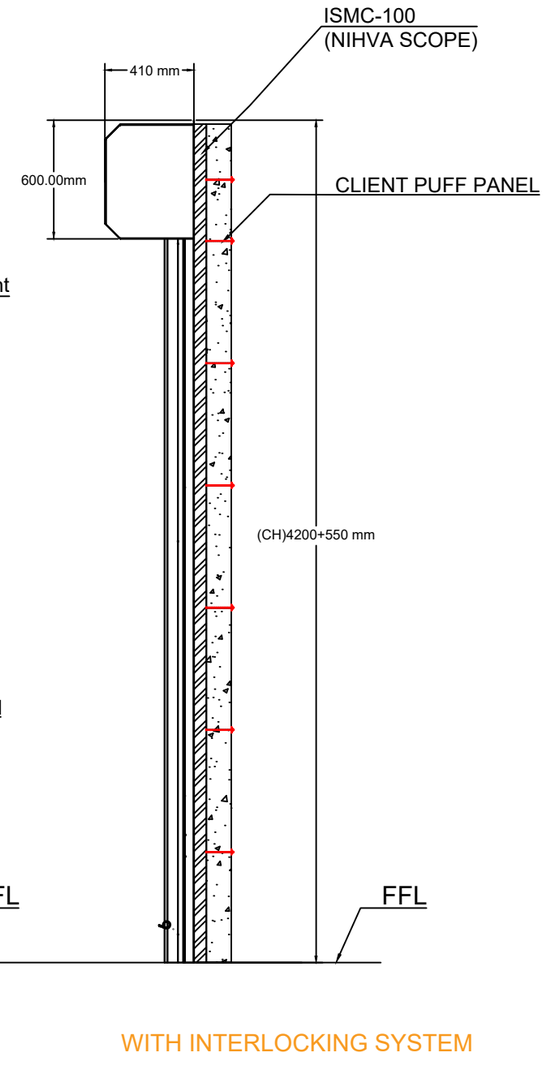

M.S. STRUCTURE DETAILS

| Sr | Description | Clear Width (CW) | Clear Height (CH) | QTY |
|---|---|---|---|---|
| 1 | HSD Without Sensor With Access Control | **4500** | **4200** | 1 |

This drawing & design is the property of NIHVA TECHNOLOGIES. Not to be sold or copied to any other concern.

| TITLE | HIGH SPEED DOOR STRUCTURE DRAWING | | | NIHVA TECHNOLOGIES PVT. LTD. PUNE<br>Tel : 020 66304033<br>Email:- info@nihva.com<br>Website:- www.nihva.com | |
|---|---|---|---|---|---|
| | NAME | SIGN | DATE | CLIENT - RINAC | |
| DRAWN | S.J | | 18.01.2024 | | |
| CHECK | A.K | | 18.01.2024 | PROJECT - HIGH SPEED DOOR ST. | |
| APPRD. | V.T | | 18.01.2024 | FORMAT NO - NIHVA-DD-F-03 | |
| If any queries contact : projectsupport@nihva.com | | | | DWG. NO. : NIHVA/23-24/00XX | REV- R00 |
| ALL DIMENSION ARE IN mm | | | | SCALE: NTS | WT: SHEET: |

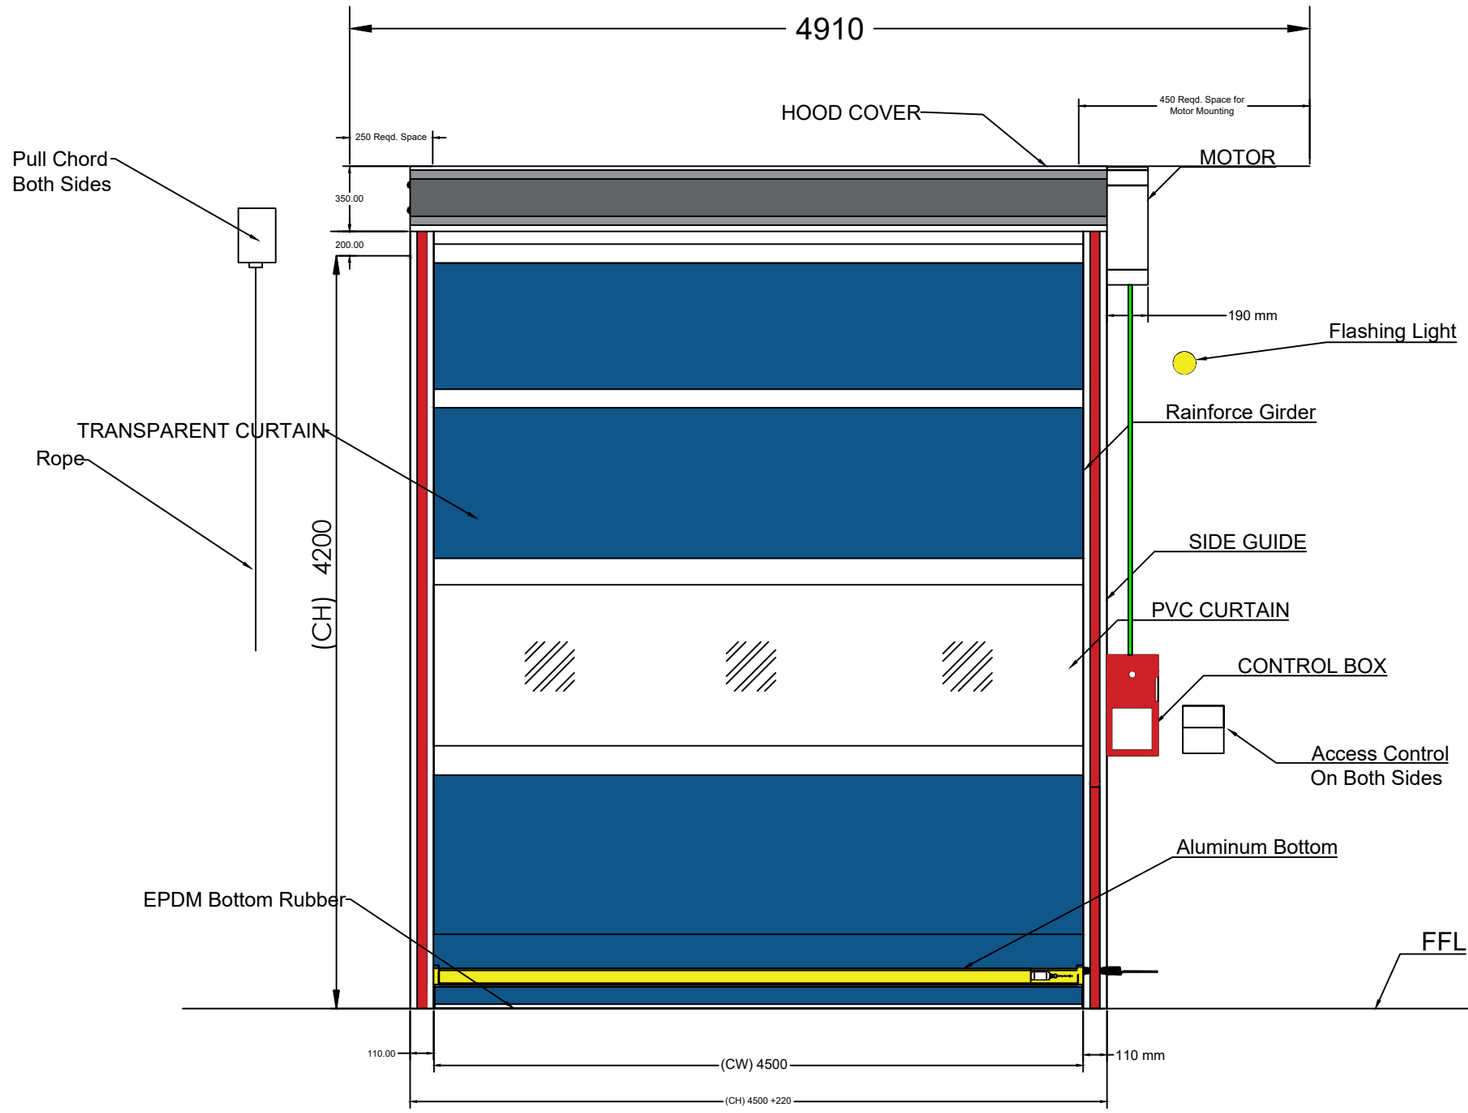


WITH INTERLOCKING SYSTEM

## TECHNICAL SPECIFICATION :

| SR. | SPECIFICATIONS | DETAILS |
|---|---|---|
| 1 | Control Panel | LED Display Servo Controller : - Operating Speed (Adjustable) : 1.4~2.5 min/ Working Temperature : -35 degree to 65 degree - Water Resistant : IP65 Make IDER, manufactured under European Standards |
| 2 | Drive | IDER Make ,CE Certified |
| 3 | Motor Power ,Torque | Power : 1.1 kW Torque : 65 Nm |
| 4 | Door Travel Speed | Opening: 2 m/Sec & Closing:0.9m/Sec |
| 5 | Safety Device | Safety Photocell Pair & Safety Edges |
| 6 | Surface Finish | As Per Client Requirement |
| 7 | Accessories | Flashing Light with Buzzer , Pull Chord |

## NOTE:

(1) All Cables & Ele.Conduits to be provided by NIHVA
(2) All Civil Work in Client Scope
(3) Required M.S.Structure & Fittings at NIHVA Scope

| Sr | Clear Width (CW) | Clear Height (CH) | QTY |
|---|---|---|---|
| 1 | 4500 | 4200 | 2 |

This drawing & design is the property of NIHVA TECHNOLOGIES. Not to be sold or copied to any other concern.

| TITLE | HIGH SPEED DOOR WITH ACCESS CONTROL GA DRAWING | | |
|---|---|---|---|
| | NAME | SIGN | DATE |
| DRAWN | S.J | | 19.01.2024 |
| CHECK | A.K | | 19.01.2024 |
| APPRD. | V.T | | 19.01.2024 |

If any queries contact : projectsupport@nihva.com

ALL DIMENSION ARE IN mm

NIHVA TECHNOLOGIES PVT. LTD.
NIHVA TECHNOLOGIES PVT. LTD. PUNE
Tel : 020 66304033
Email:- info@nihva.com
Website:- www.nihva.com


CLIENT - RINAC


PROJECT - HIGH SPEED DOOR

FORMAT NO - NIHVA-DD-F-03

DWG. NO. : NIHVA/23-24/00XX | REV- R00

SCALE: NTS | WT: | SHEET:

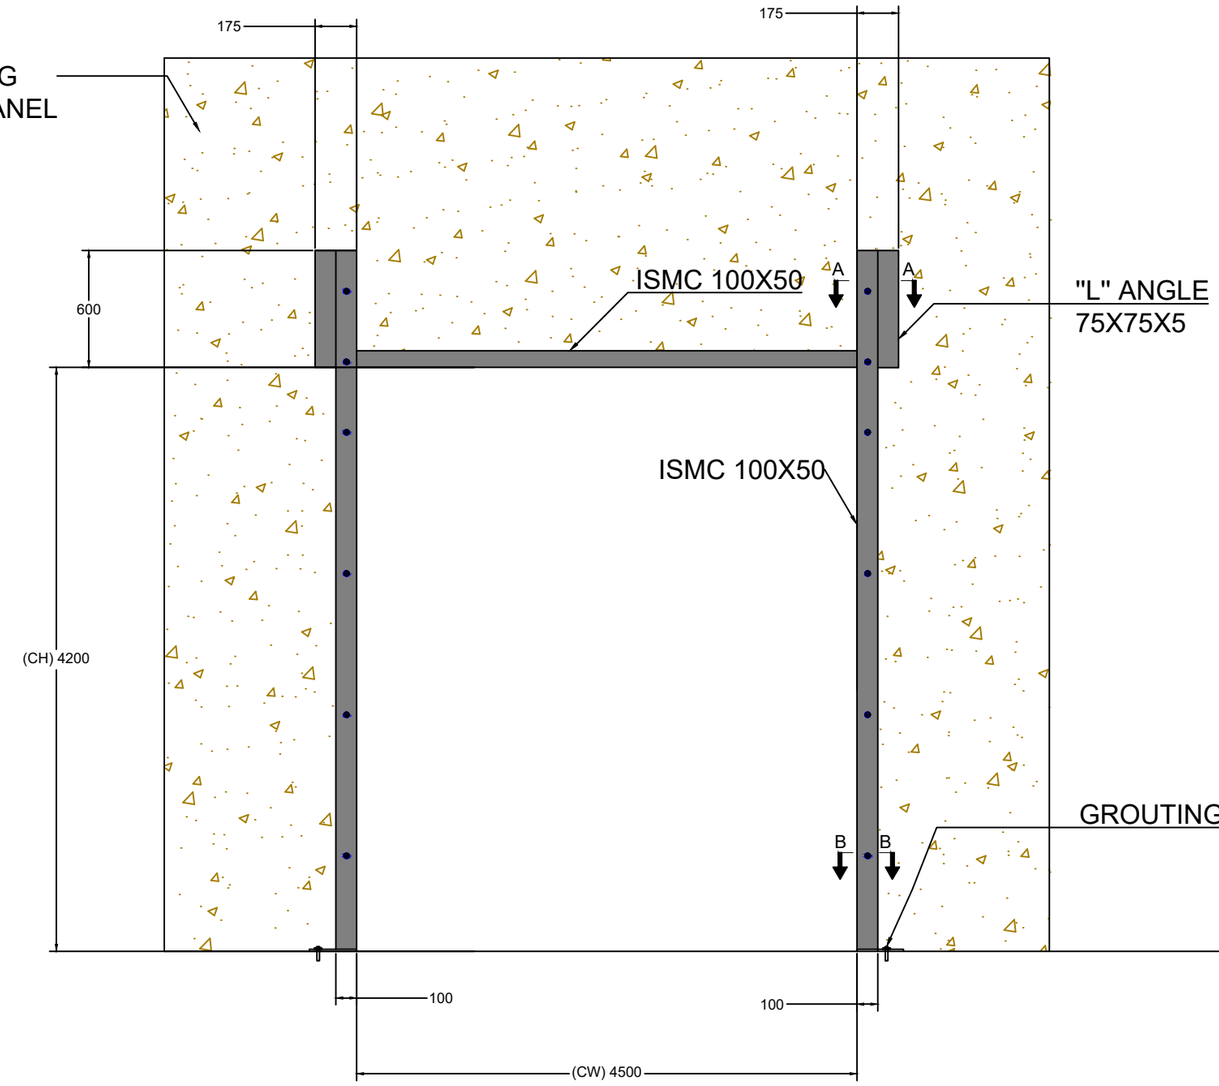

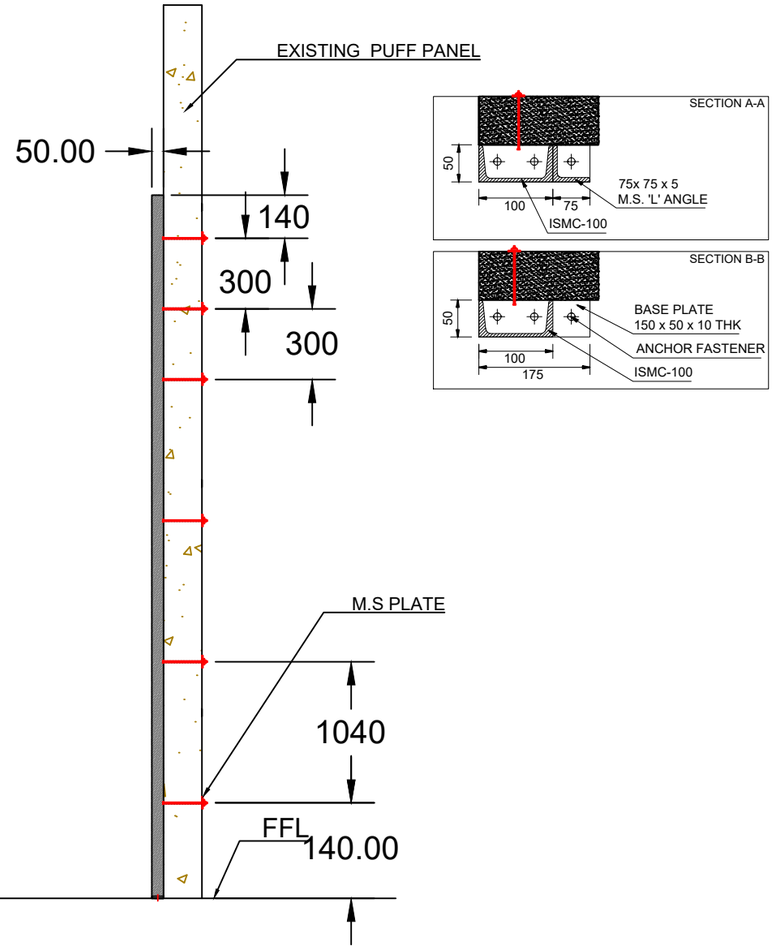




M.S. STRUCTURE DETAILS

| Sr | Description | Clear Width (CW) | Clear Height (CH) | QTY |
|---|---|---|---|---|
| 1 | HSD Without Sensor With Access Control | **4500** | **4200** | 2 |

This drawing & design is the property of NIHVA TECHNOLOGIES. Not to be sold or copied to any other concern.
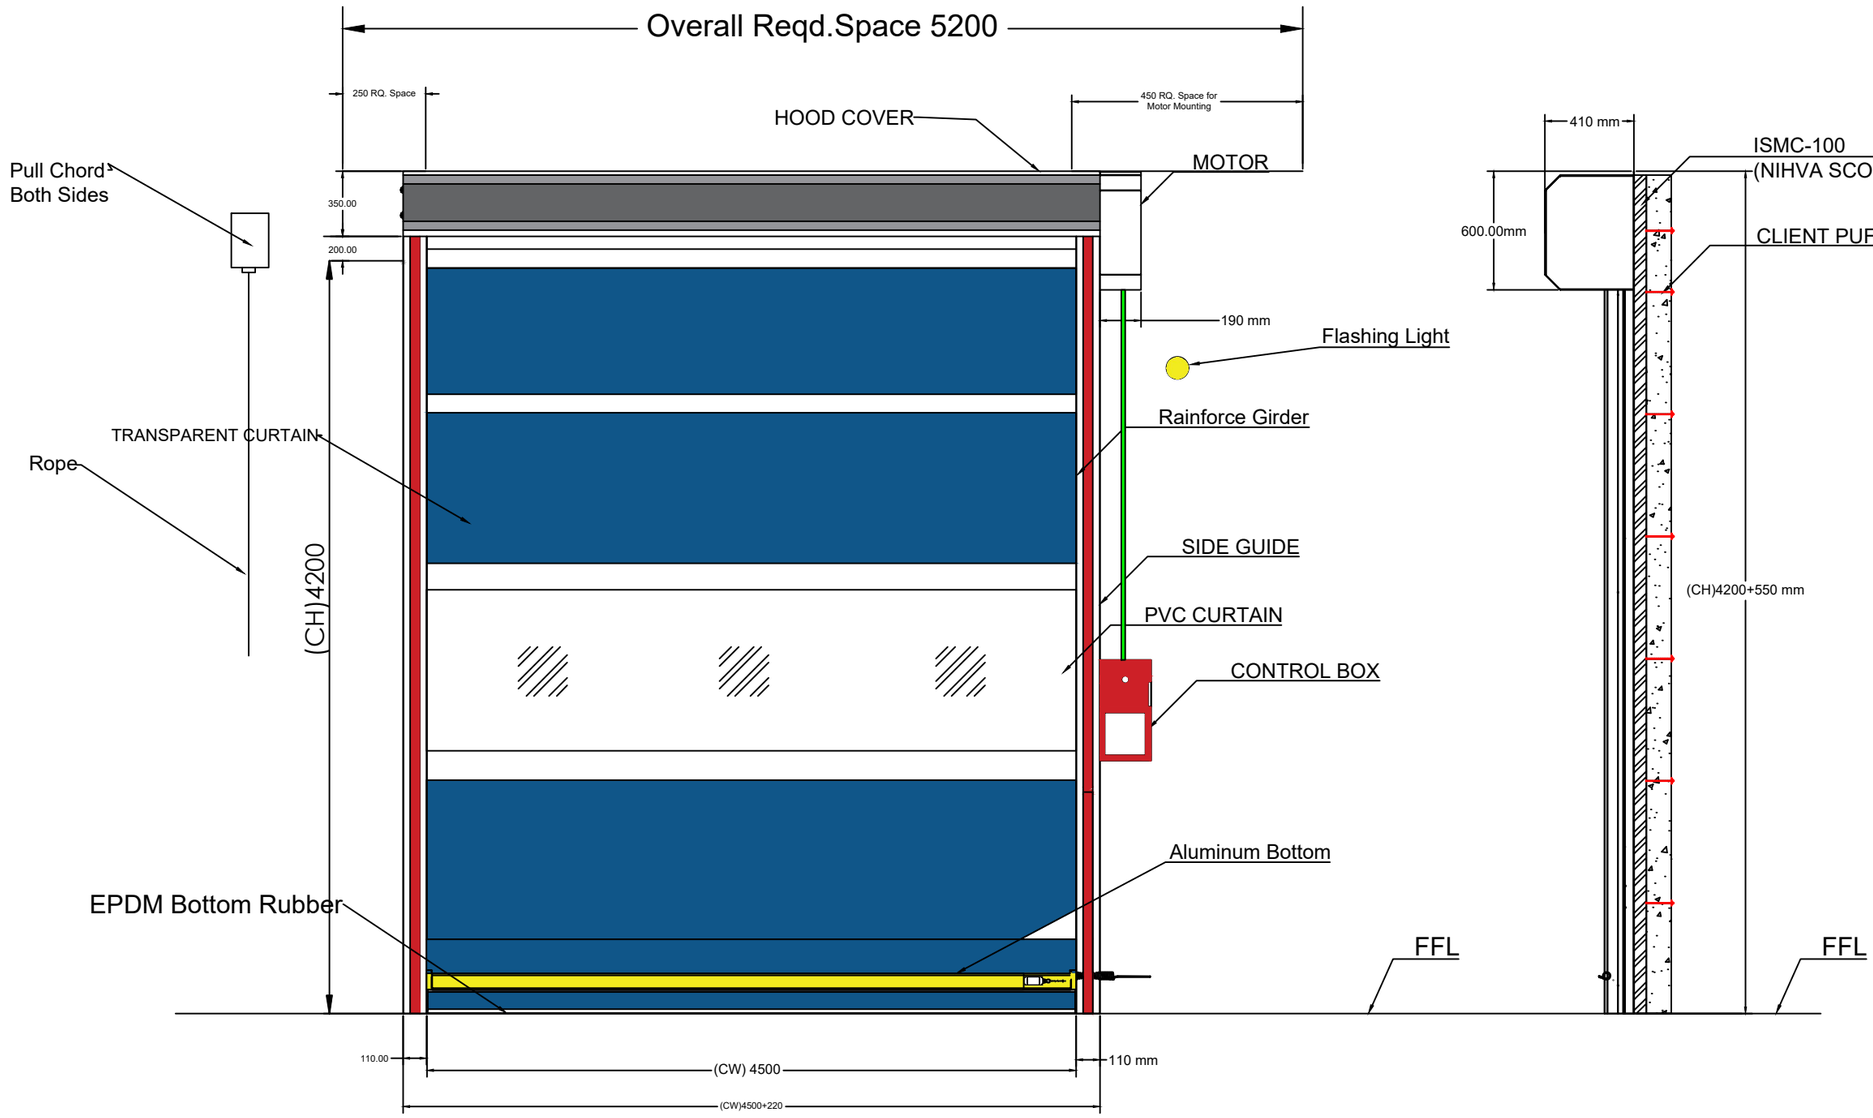
| TITLE | HIGH SPEED DOOR STRUCTURE DRAWING | | | NIHVA TECHNOLOGIES PVT. LTD. PUNE<br>Tel : 020 66304033<br>Email:- info@nihva.com<br>Website:- www.nihva.com |
|---|---|---|---|---|
| | NAME | SIGN | DATE | |
| DRAWN | S.J | | 18.01.2024 | CLIENT - RINAC |
| CHECK | A.K | | 18.01.2024 | PROJECT - HIGH SPEED DOOR ST. |
| APPRD. | V.T | | 18.01.2024 | FORMAT NO - NIHVA-DD-F-03 |
| If any queries contact : projectsupport@nihva.com | | | | DWG. NO. : NIHVA/23-24/00XX / REV- R00 |
| ALL DIMENSION ARE IN mm | | | | SCALE: NTS / WT: / SHEET: |




## TECHNICAL SPECIFICATION :

| SR. | SPECIFICATIONS | DETAILS |
|---|---|---|
| 1 | Control Panel | LED Display Servo Controller : - Operating Speed (Adjustable) : 1.4~2.5 min/ Working Temperature : -35 degree to 65 degree - Water Resistant : IP65 Make IDER, manufactured under European Standards |
| 2 | Drive | IDER Make ,CE Certified |
| 3 | Motor Power ,Torque | Power : 1.1 kW Torque : 65 Nm |
| 4 | Door Travel Speed | Opening: 2 m/Sec & Closing:0.9m/Sec |
| 5 | Safety Device | Safety Photocell Pair & Safety Edges |
| 6 | Surface Finish | As Per Client Requirement |
| 7 | Accessories | Flashing Light with Buzzer , Pull Chord |

## NOTE:

(1) All Cables & Ele.Conduits to be provided by NIHVA
(2) All Civil Work in Client Scope
(3) Required M.S.Structure & Fittings at NIHVA Scope

## Revision :

| Rev | Revision | Date | Revised BY |
|---|---|---|---|
| R01 | Removed Access Control System | 23-02-2024 | Y.K. |

| Sr | Clear Width (CW) | Clear Height (CH) | QTY |
|---|---|---|---|
| 1 | 4500 | 4200 | 5 |

This drawing & design is the property of NIHVA TECHNOLOGIES. Not to be sold or copied to any other concern.


TITLE: HIGH SPEED DOOR WITHOUT SENSOR GA DRAWING


| | NAME | SIGN | DATE |
|---|---|---|---|
| DRAWN | S.J | | 19.01.2024 |
| CHECK | A.K | | 19.01.2024 |
| APPRD. | V.T | | 19.01.2024 |

NIHVA TECHNOLOGIES PVT. LTD.
NIHVA TECHNOLOGIES PVT. PUNE
Tel : 020 66304033
Email:- info@nihva.com
Website:- www.nihva.com

If any queries contact : projectsupport@nihva.com

CLIENT - RINAC
PROJECT - HIGH SPEED DOOR
FORMAT NO - NIHVA-DD-F-03
DWG. NO. : NIHVA/23-24/00XX
REV- R01
ALL DIMENSION ARE IN mm
SCALE: NTS
WT:
SHEET:

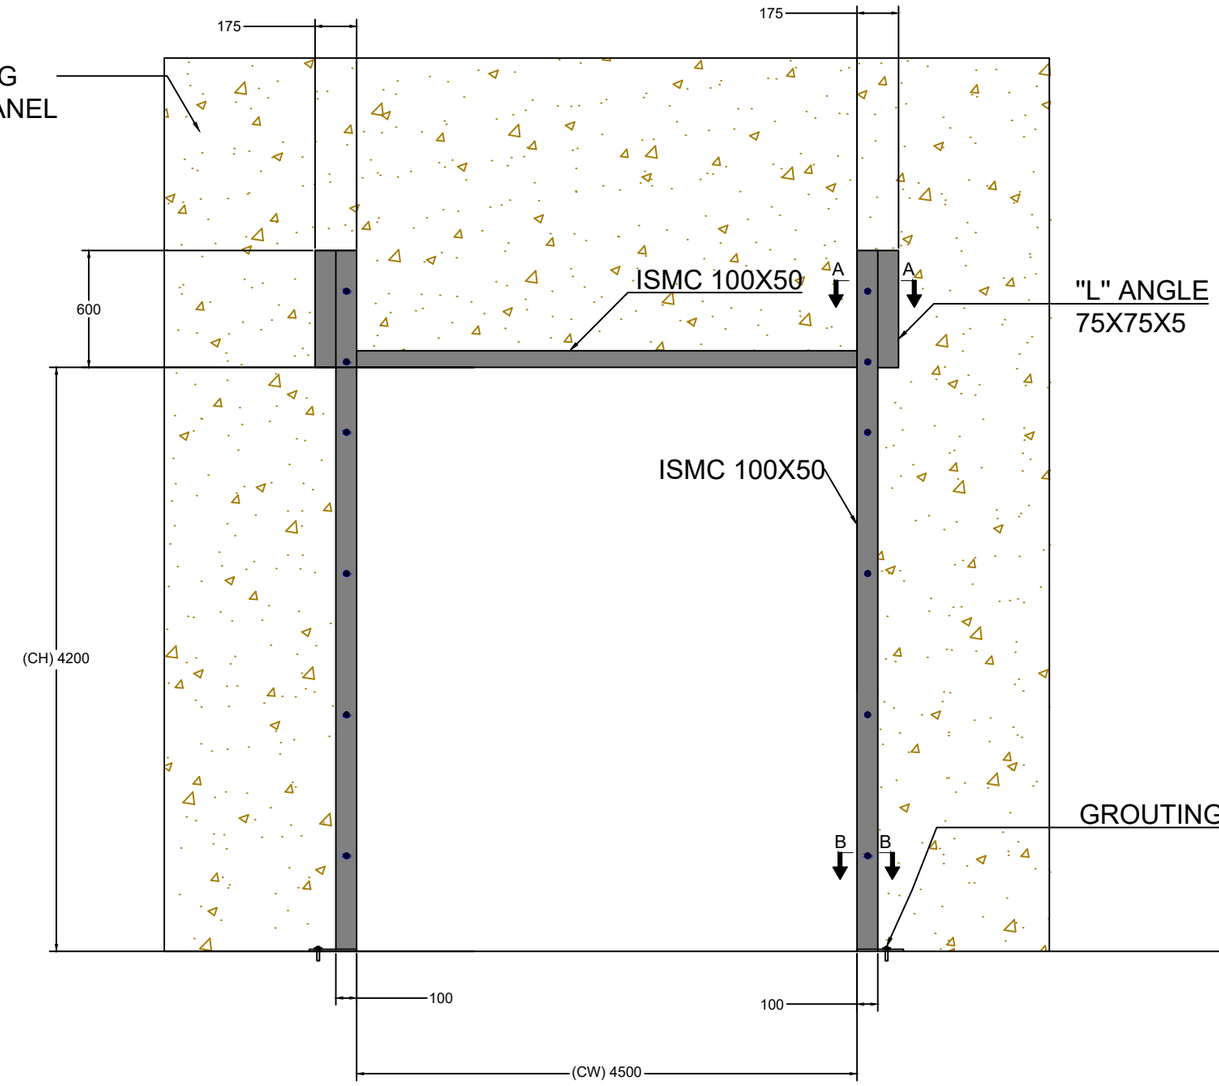

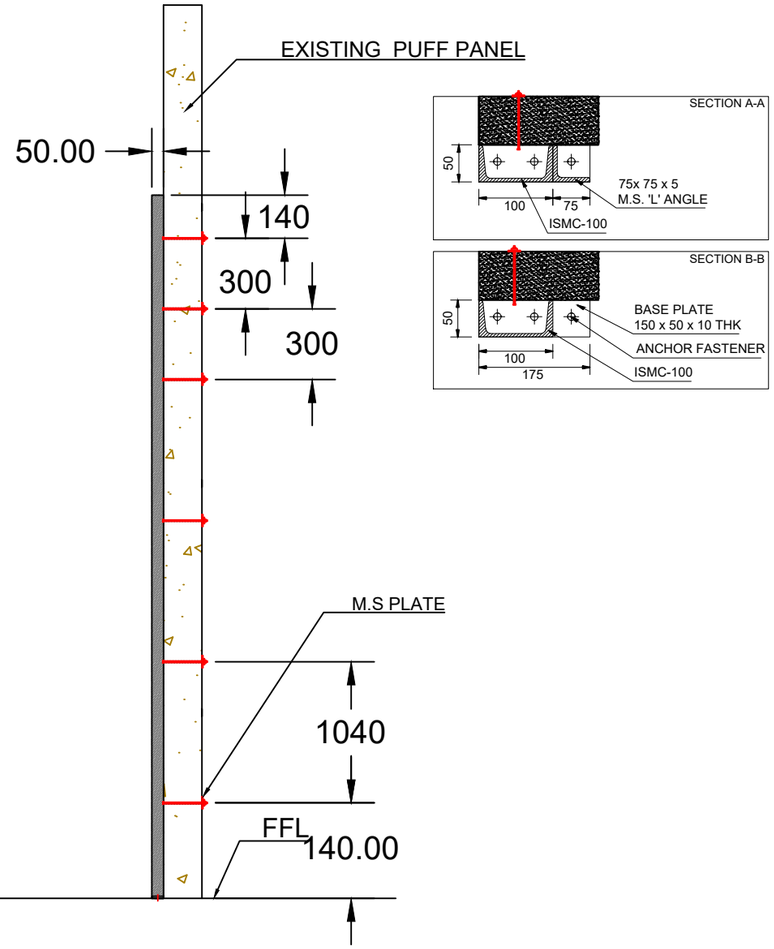




M.S. STRUCTURE DETAILS

| Sr | Description | Clear Width (CW) | Clear Height (CH) | QTY |
|---|---|---|---|---|
| 1 | HSD Without Sensor | **4500** | **4200** | 5 |

This drawing & design is the property of NIHVA TECHNOLOGIES. Not to be sold or copied to any other concern.
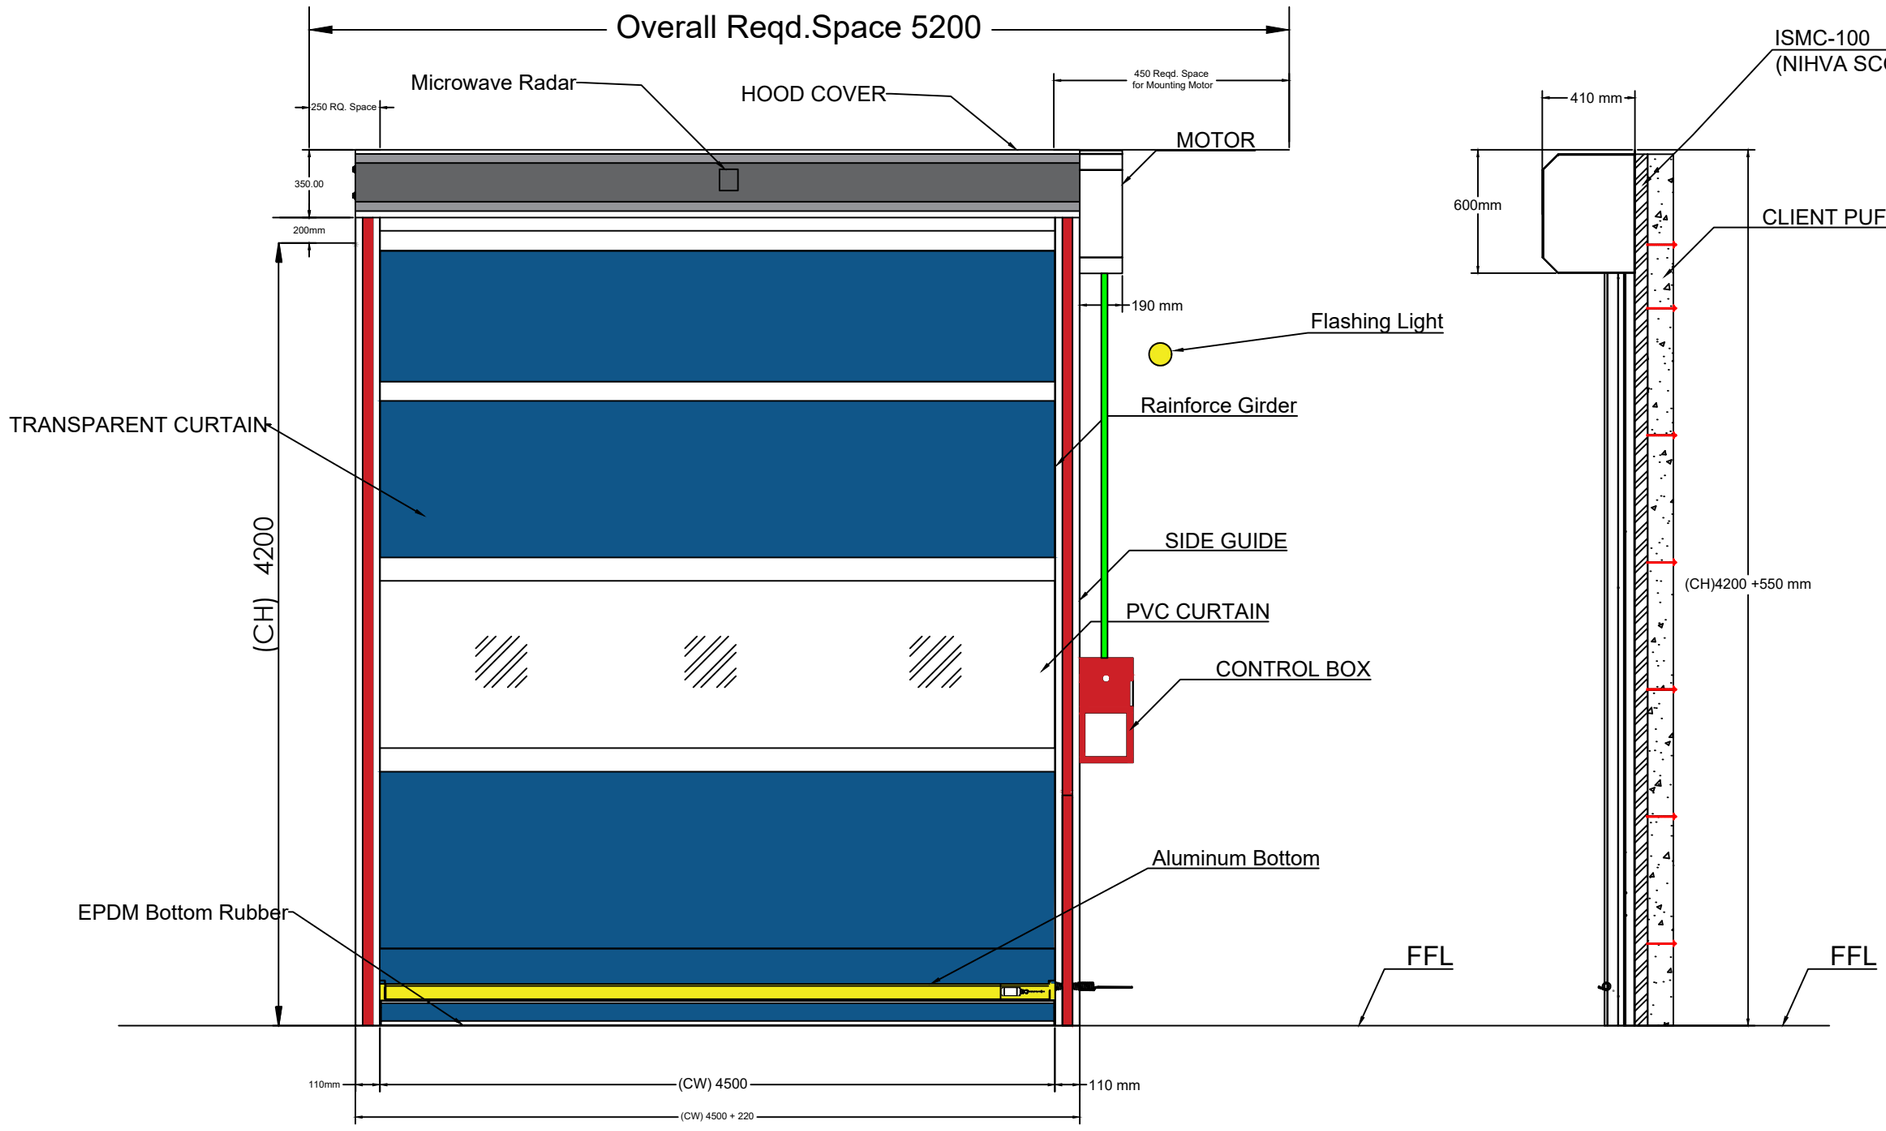
| TITLE | HIGH SPEED DOOR STRUCTURE DRAWING | | | NIHVA TECHNOLOGIES PVT. LTD. PUNE<br>Tel : 020 66304033<br>Email:- info@nihva.com<br>Website:- www.nihva.com |
|---|---|---|---|---|
| | NAME | SIGN | DATE | |
| DRAWN | S.J | | 18.01.2024 | CLIENT - RINAC |
| CHECK | A.K | | 18.01.2024 | PROJECT - HIGH SPEED DOOR ST. |
| APPRD. | V.T | | 18.01.2024 | FORMAT NO - NIHVA-DD-F-03 |
| If any queries contact : projectsupport@nihva.com | | | | DWG. NO. : NIHVA/23-24/00XX / REV- R00 |
| ALL DIMENSION ARE IN mm | | | | SCALE: NTS / WT: / SHEET: |




## TECHNICAL SPECIFICATION :

| SR. | SPECIFICATIONS | DETAILS |
|---|---|---|
| 1 | Control Panel | LED Display Servo Controller : -<br>Operating Speed (Adjustable) : 1.4~2.5 min/<br>Working Temperature : -35 degree to 65 degree -<br>Water Resistant : IP65 Make IDER, manufactured under European Standards |
| 2 | Drive | IDER Make ,CE Certified |
| 3 | Motor Power ,Torque | Power : 1.1 kW Torque : 65 Nm |
| 4 | Door Travel Speed | Opening: 2 m/Sec & Closing:0.9m/Sec |
| 5 | Safety Device | Safety Photocell Pair & Safety Edges |
| 6 | Surface Finish | As Per Client Requirement |
| 7 | Accessories | Radar Sensor ,Magnetic Loop Detector ,Flashing Light |

## NOTE:

(1) All Cables & Ele.Conduits to be provided by NIHVA
(2) All Civil Work in Client Scope
(3) Required M.S.Structure & Fittings at Nihva Scope

| Sr | Clear Width (CW) | Clear Height (CH) | QTY |
|---|---|---|---|
| 1 | 4500 | 4200 | 1 |

This drawing & design is the property of NIHVA TECHNOLOGIES. Not to be sold or copied to any other concern.


TITLE : HIGH SPEED DOOR WITH SENSOR GA DRAWING


| | NAME | SIGN | DATE |
|---|---|---|---|
| DRAWN | S.J | | 18.01.2024 |
| CHECK | A.K | | 18.01.2024 |
| APPRD. | V.T | | 18.01.2024 |

NIHVA TECHNOLOGIES PVT. LTD.
NIHVA TECHNOLOGIES PVT. PUNE
Tel : 020 66304033
Email:- info@nihva.com
Website:- www.nihva.com

If any queries contact : projectsupport@nihva.com

CLIENT - RINAC
PROJECT - HIGH SPEED DOOR
FORMAT NO - NIHVA-DD-F-03
DWG. NO. : NIHVA/23-24/00XX
REV- R00
ALL DIMENSION ARE IN mm
SCALE: NTS
WT:
SHEET:

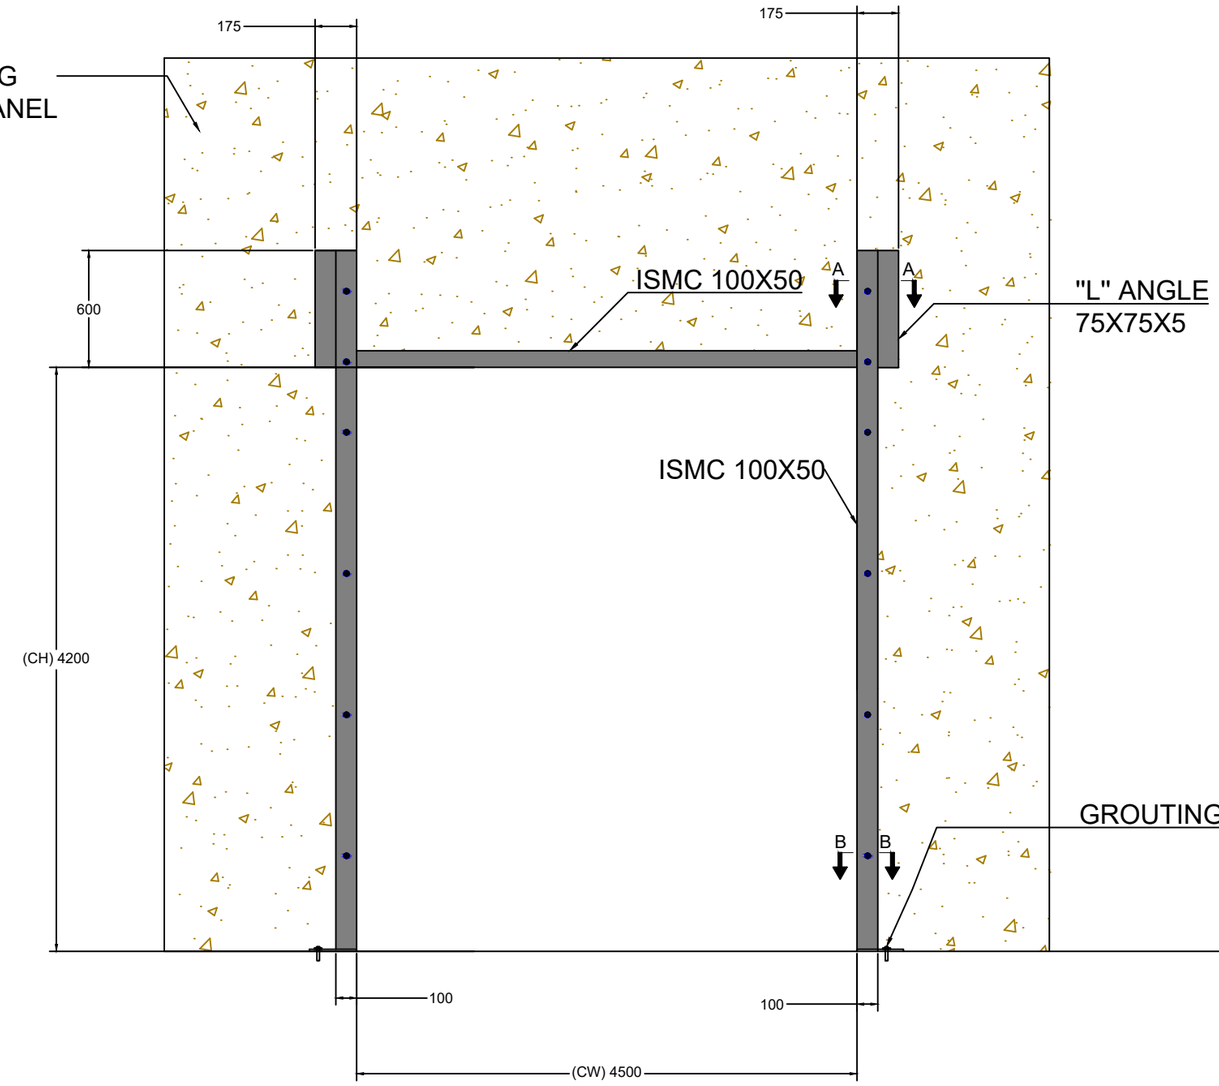

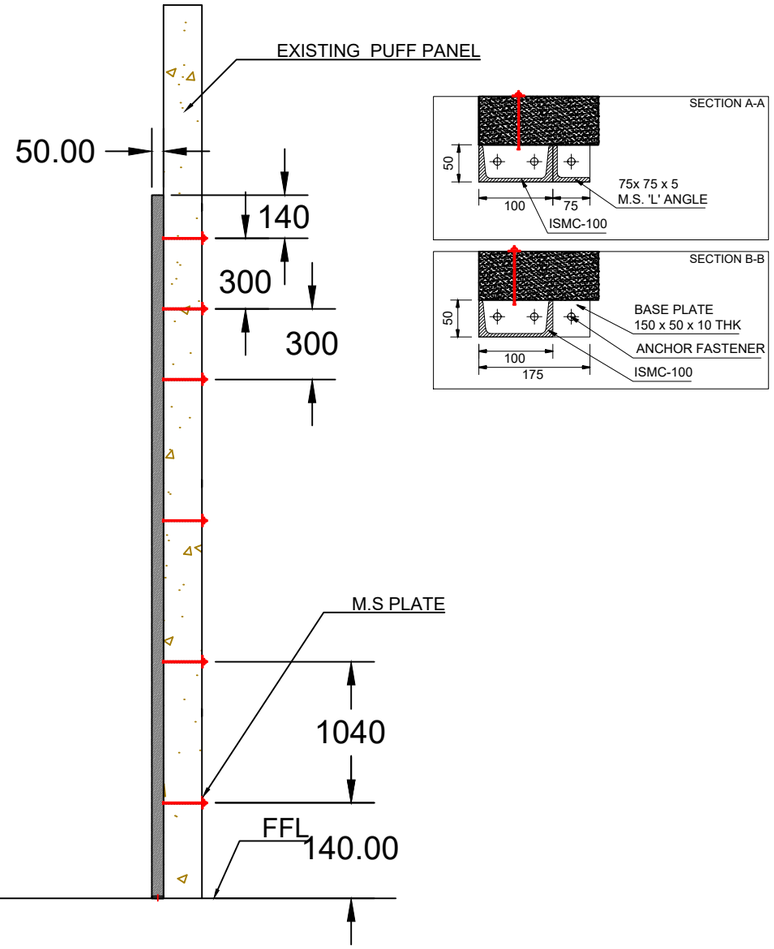




M.S. STRUCTURE DETAILS

| Sr | Description | Clear Width (CW) | Clear Height (CH) | QTY |
|---|---|---|---|---|
| 1 | HSD With Sensor | **4500** | **4200** | 1 |

This drawing & design is the property of NIHVA TECHNOLOGIES. Not to be sold or copied to any other concern.
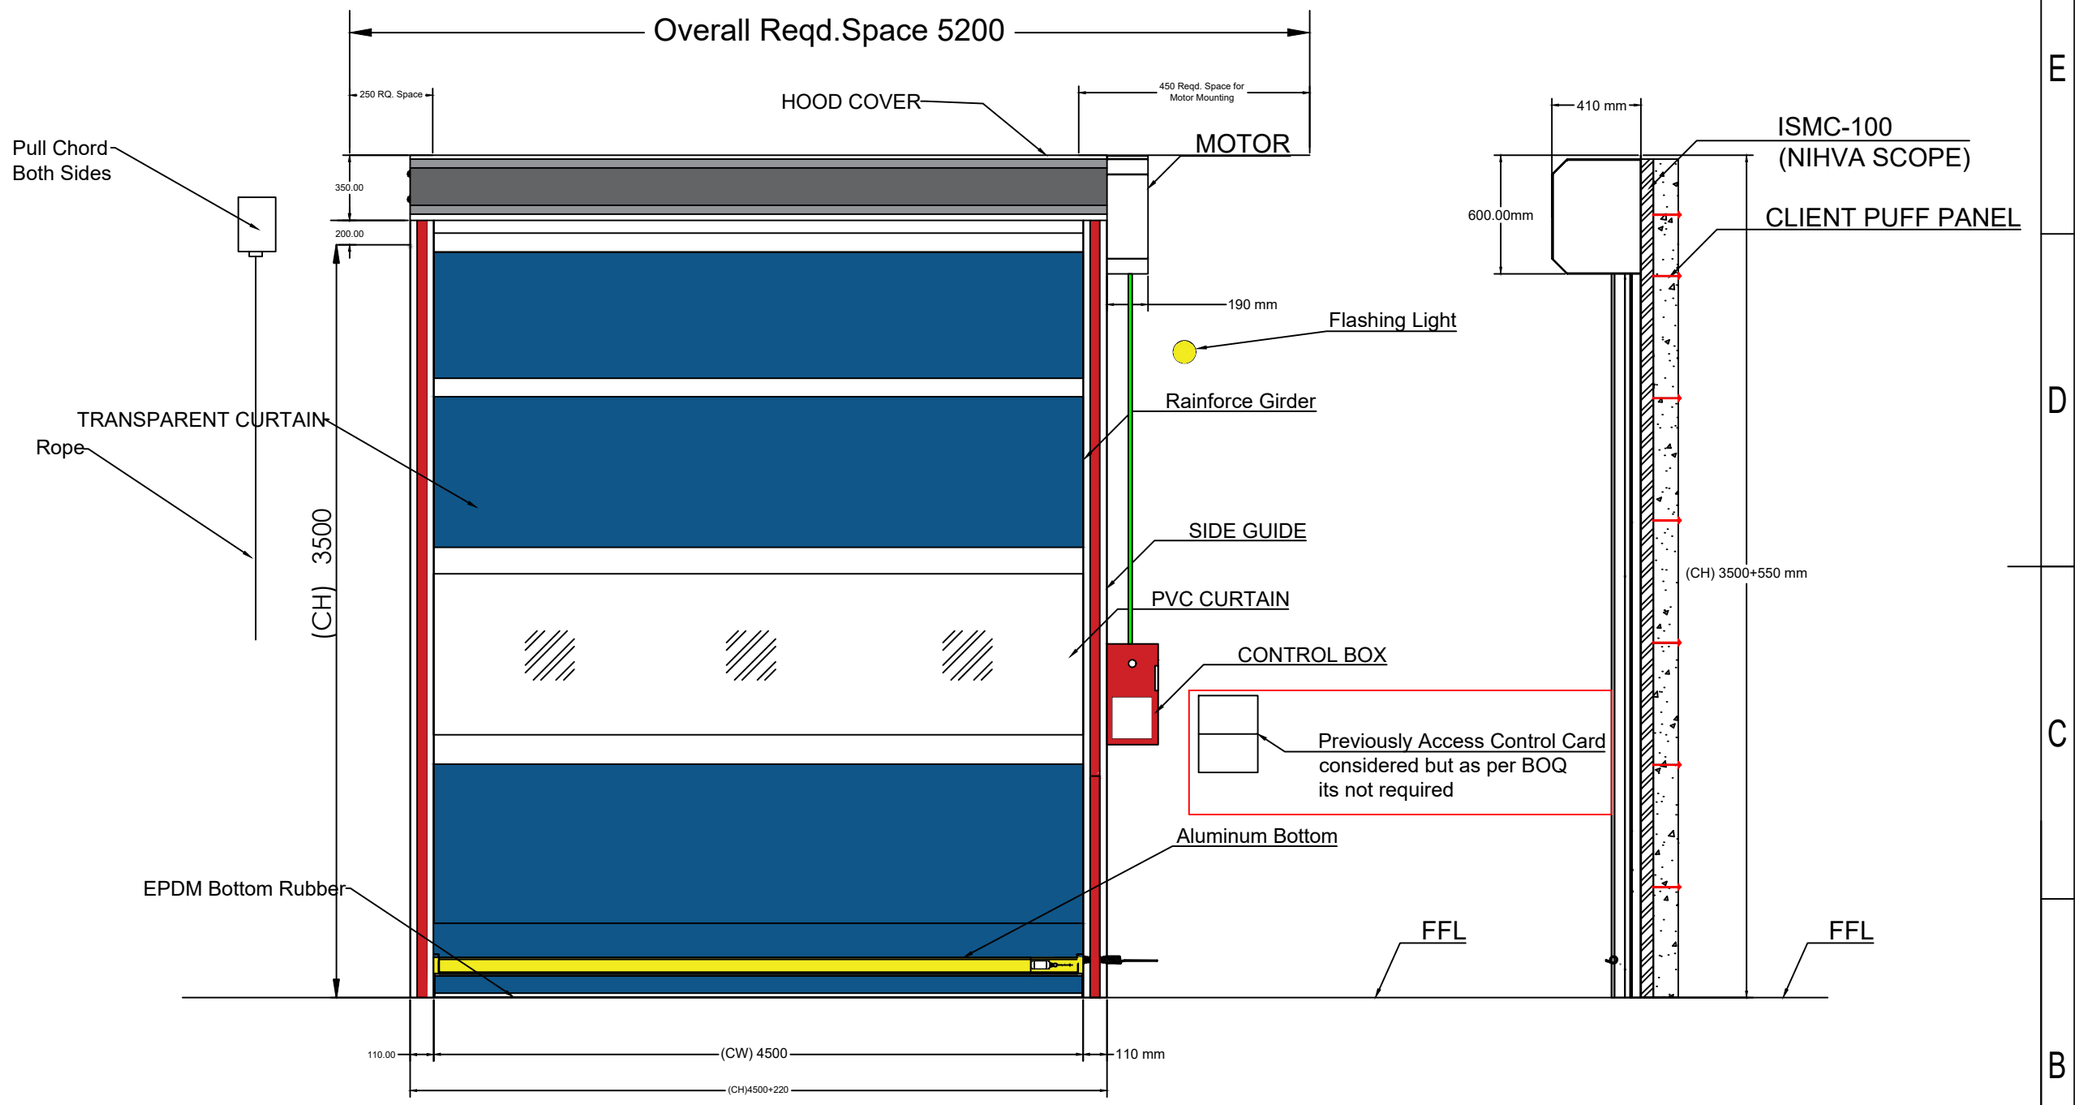
| TITLE | HIGH SPEED DOOR STRUCTURE DRAWING | | | NIHVA TECHNOLOGIES PVT. LTD. PUNE<br>Tel : 020 66304033<br>Email:- info@nihva.com<br>Website:- www.nihva.com |
|---|---|---|---|---|
| | NAME | SIGN | DATE | |
| DRAWN | S.J | | 18.01.2024 | CLIENT - RINAC |
| CHECK | A.K | | 18.01.2024 | PROJECT - HIGH SPEED DOOR ST. |
| APPRD. | V.T | | 18.01.2024 | FORMAT NO - NIHVA-DD-F-03 |
| If any queries contact : projectsupport@nihva.com | | | | DWG. NO. : NIHVA/23-24/00XX / REV- R00 |
| ALL DIMENSION ARE IN mm | | | | SCALE: NTS / WT: / SHEET: |




## TECHNICAL SPECIFICATION :

| SR. | SPECIFICATIONS | DETAILS |
|---|---|---|
| 1 | Control Panel | LED Display Servo Controller : - Operating Speed (Adjustable) : 1.4~2.5 min/ Working Temperature : -35 degree to 65 degree - Water Resistant : IP65 Make IDER, manufactured under European Standards |
| 2 | Drive | IDER Make ,CE Certified |
| 3 | Motor Power ,Torque | Power : 1.1 kW Torque : 65 Nm |
| 4 | Door Travel Speed | Opening: 2 m/Sec & Closing:0.9m/Sec |
| 5 | Safety Device | Safety Photocell Pair & Safety Edges |
| 6 | Surface Finish | As Per Client Requirement |
| 7 | Accessories | Flashing Light with Buzzer , Pull Chord |

## NOTE :

(1) All Cables & Ele.Conduits to be provided by NIHVA
(2) All Civil Work in Client Scope
(3) Required M.S.Structure & Fittings at NIHVA Scope

## Revision :

| Rev | Revision | Date | Revised BY |
|---|---|---|---|
| R01 | Removed Access Control System | 23-02-2024 | Y.K. |

| Sr | Clear Width (CW) | Clear Height (CH) | QTY |
|---|---|---|---|
| 1 | 4500 | 3500 | 2 |

This drawing & design is the property of NIHVA TECHNOLOGIES. Not to be sold or copied to any other concern.


TITLE : HIGH SPEED DOOR WITHOUT SENSOR GA DRAWING


| | NAME | SIGN | DATE |
|---|---|---|---|
| DRAWN | S.J | | 19.01.2024 |
| CHECK | A.K | | 19.01.2024 |
| APPRD. | V.T | | 19.01.2024 |

NIHVA TECHNOLOGIES PVT. LTD.
NIHVA TECHNOLOGIES PVT. PUNE
Tel : 020 66304033
Email:- info@nihva.com
Website:- www.nihva.com

If any queries contact : projectsupport@nihva.com

CLIENT - RINAC
PROJECT - HIGH SPEED DOOR
FORMAT NO - NIHVA-DD-F-03
DWG. NO. : NIHVA/23-24/00XX
REV- R01
ALL DIMENSION ARE IN mm
SCALE: NTS
WT:
SHEET:

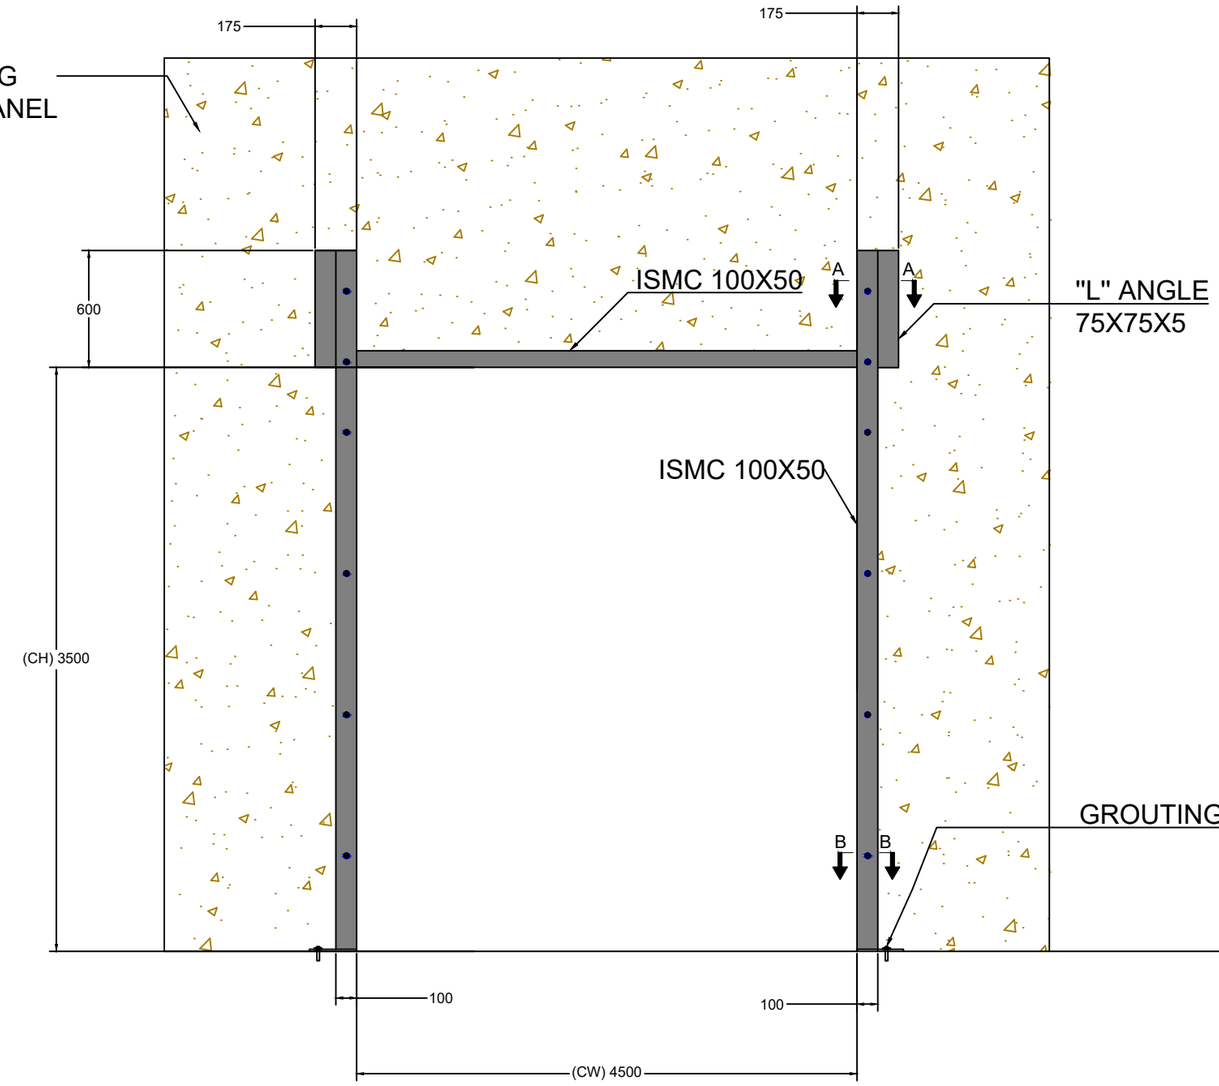

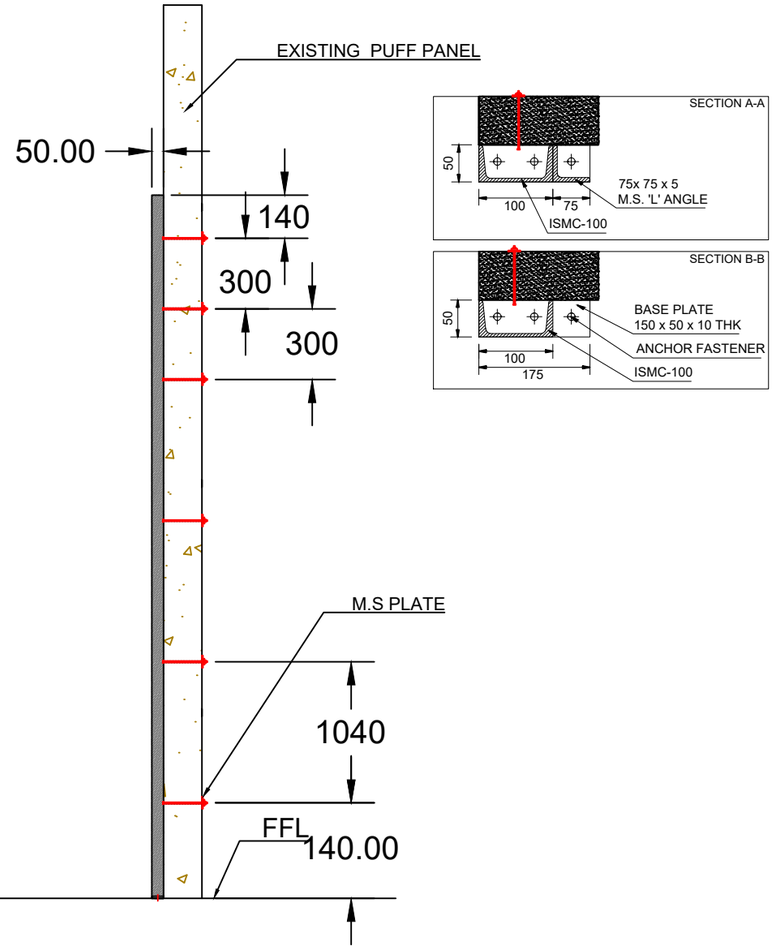




M.S. STRUCTURE DETAILS

| Sr | Description | Clear Width (CW) | Clear Height (CH) | QTY |
|---|---|---|---|---|
| 1 | HSD Without Sensor | **4500** | **3500** | 2 |

This drawing & design is the property of NIHVA TECHNOLOGIES. Not to be sold or copied to any other concern.
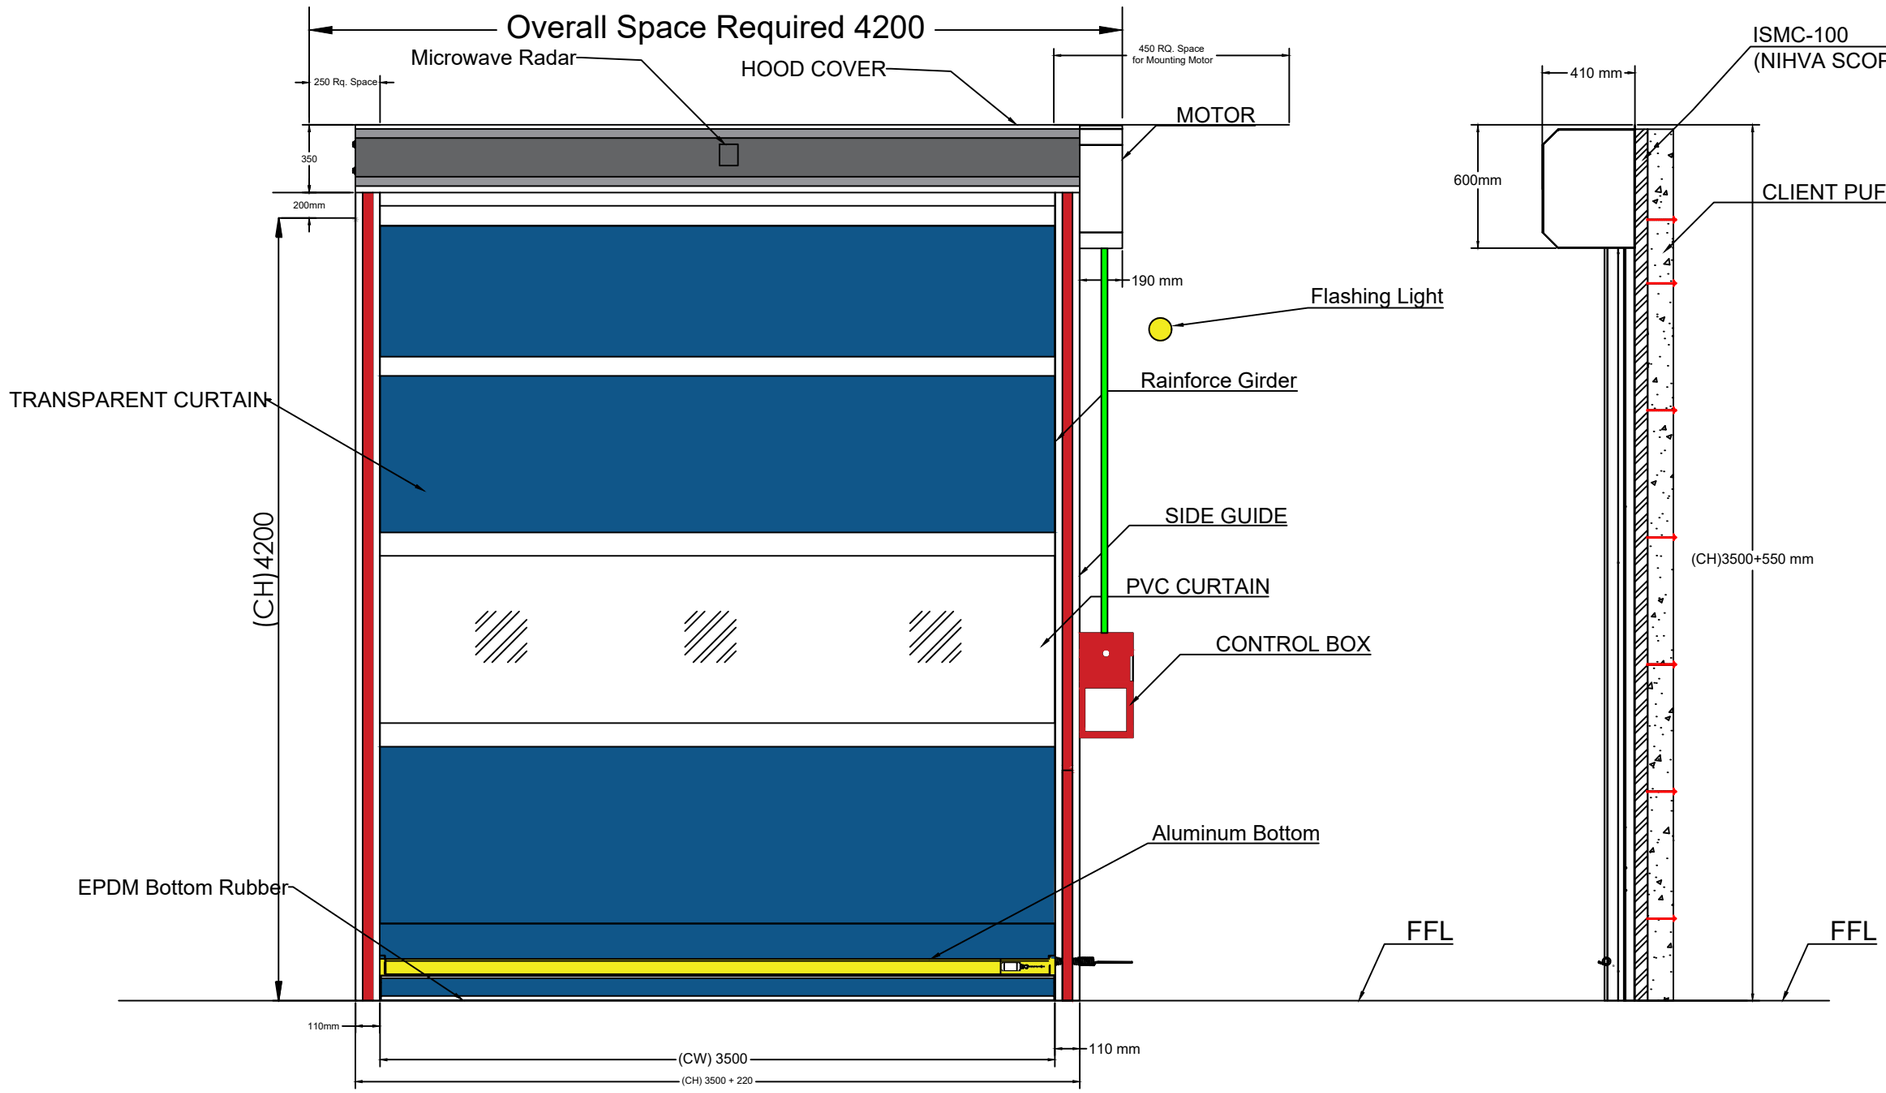
| TITLE | HIGH SPEED DOOR STRUCTURE DRAWING | | | NIHVA TECHNOLOGIES PVT. LTD. PUNE<br>Tel : 020 66304033<br>Email:- info@nihva.com<br>Website:- www.nihva.com |
|---|---|---|---|---|
| | NAME | SIGN | DATE | |
| DRAWN | S.J | | 18.01.2024 | CLIENT - RINAC |
| CHECK | A.K | | 18.01.2024 | PROJECT - HIGH SPEED DOOR ST. |
| APPRD. | V.T | | 18.01.2024 | FORMAT NO - NIHVA-DD-F-03 |
| If any queries contact : projectsupport@nihva.com | | | | DWG. NO. : NIHVA/23-24/00XX / REV- R00 |
| ALL DIMENSION ARE IN mm | | | | SCALE: NTS / WT: / SHEET: |




## TECHNICAL SPECIFICATION :

| SR. | SPECIFICATIONS | DETAILS |
|---|---|---|
| 1 | Control Panel | LED Display Servo Controller : -<br>Operating Speed (Adjustable) : 1.4~2.5 min/<br>Working Temperature : -35 degree to 65 degree -<br>Water Resistant : IP65 Make IDER, manufactured under European Standards |
| 2 | Drive | IDER Make ,CE Certified |
| 3 | Motor Power ,Torque | Power : 1.1 kW Torque : 65 Nm |
| 4 | Door Travel Speed | Opening: 2 m/Sec & Closing:0.9m/Sec |
| 5 | Safety Device | Safety Photocell Pair & Safety Edges |
| 6 | Surface Finish | As Per Client Requirement |
| 7 | Accessories | Radar Sensor ,Magnetic Loop Detector ,Flashing Light Buzzer |

## NOTE:

(1) All Cables & Ele.Conduits to be provided by NIHVA
(2) All Civil Work in Client Scope
(3) Required M.S.Structure & Fittings at NIHVA Scope

| Sr | Clear Width (CW) | Clear Height (CH) | QTY |
|---|---|---|---|
| 1 | 3500 | 4200 | 1 |

This drawing & design is the property of NIHVA TECHNOLOGIES. Not to be sold or copied to any other concern.


TITLE: HIGH SPEED DOOR WITH SENSOR GA DRAWING


| | NAME | SIGN | DATE |
|---|---|---|---|
| DRAWN | S.J | | 18.01.2024 |
| CHECK | A.K | | 18.01.2024 |
| APPRD. | V.T | | 18.01.2024 |

NIHVA TECHNOLOGIES PVT. LTD.
NIHVA TECHNOLOGIES PVT. LTD. PUNE
Tel : 020 66304033
Email:- info@nihva.com
Website:- www.nihva.com

If any queries contact : projectsupport@nihva.com

CLIENT - RINAC
PROJECT - HIGH SPEED DOOR
FORMAT NO - NIHVA-DD-F-03
DWG. NO. : NIHVA/23-24/00XX
REV- R00
ALL DIMENSION ARE IN mm
SCALE: NTS
WT:
SHEET:

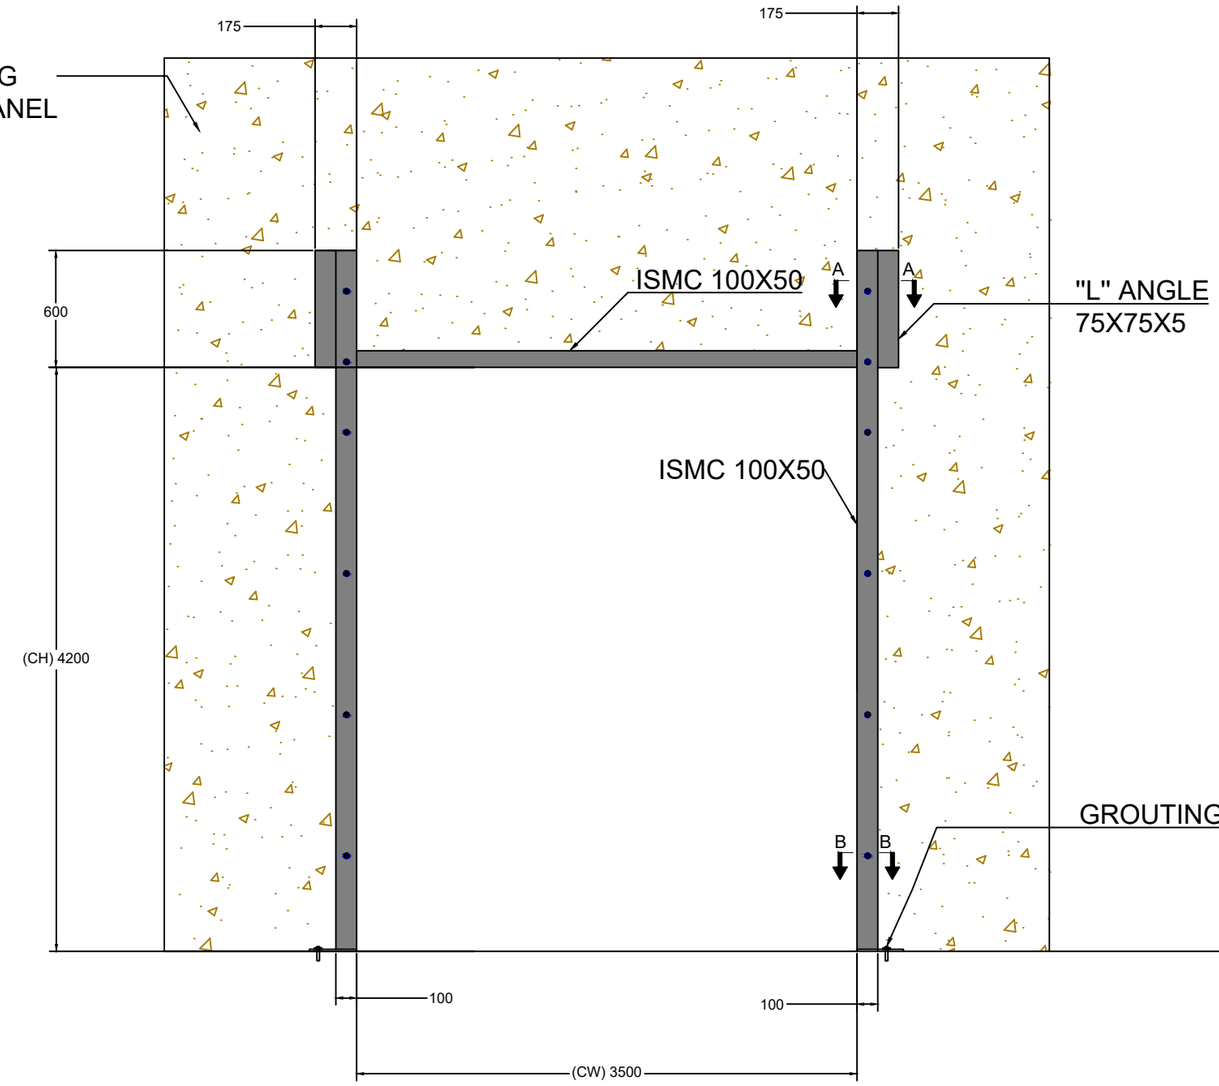

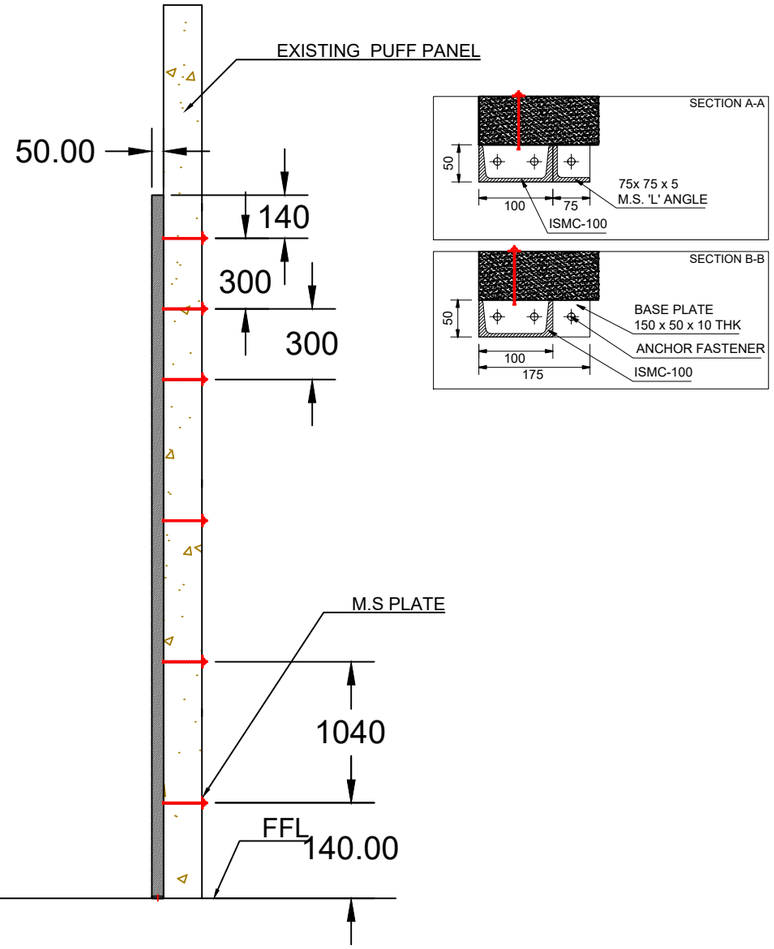
## M.S. STRUCTURE DETAILS

| Sr | Description | Clear Width (CW) | Clear Height (CH) | QTY |
|---|---|---|---|---|
| 1 | HSD With Sensor | **3500** | **4200** | 1 |

This drawing & design is the property of NIHVA TECHNOLOGIES. Not to be sold or copied to any other concern.

| TITLE | HIGH SPEED DOOR STRUCTURE DRAWING | | | NIHVA TECHNOLOGIES PVT. LTD. PUNE<br>Tel : 020 66304033<br>Email:- info@nihva.com<br>Website:- www.nihva.com |
|---|---|---|---|---|
| | NAME | SIGN | DATE | |
| DRAWN | S.J | | 18.01.2024 | CLIENT - RINAC |
| CHECK | A.K | | 18.01.2024 | PROJECT - HIGH SPEED DOOR ST. |
| APPRD. | V.T | | 18.01.2024 | FORMAT NO - NIHVA-DD-F-03 |
| If any queries contact : projectsupport@nihva.com | | | | DWG. NO. : NIHVA/23-24/00XX / REV- R00 |
| ALL DIMENSION ARE IN mm | | | | SCALE: NTS / WT: / SHEET: |