

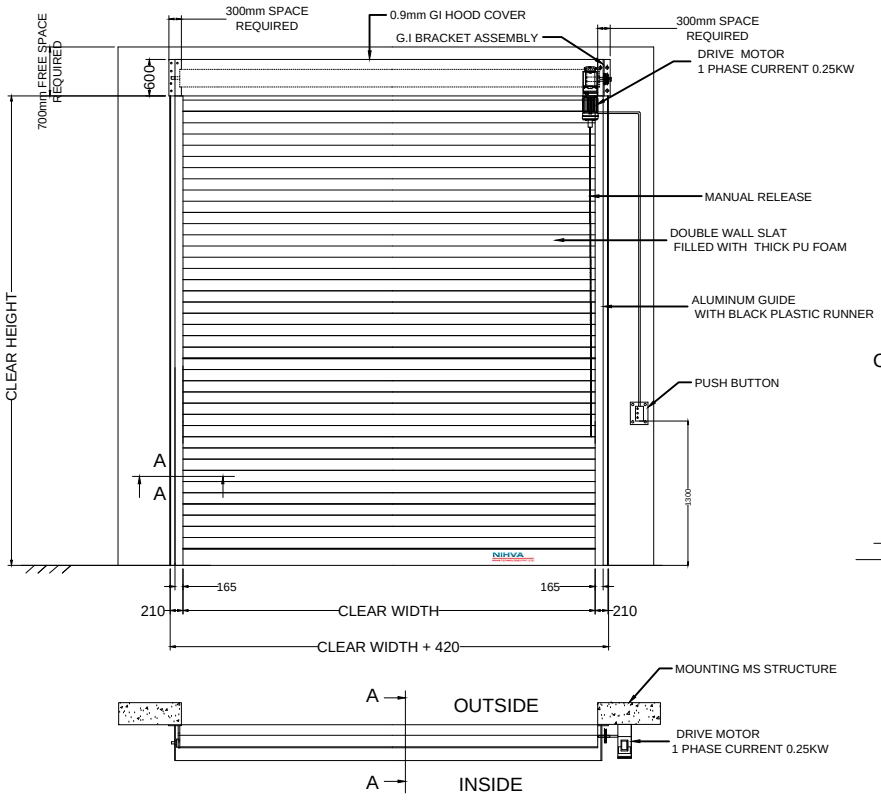


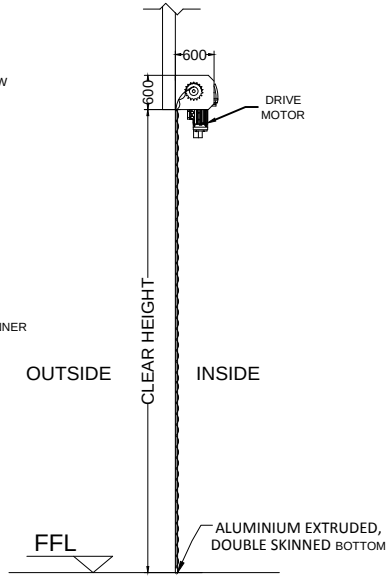


Section A-A

MOUTING OPTIONS-
(1) ON CONCRETE WALL
(2) ON PUFF PANEL
(3) ON MS STRUCTURE

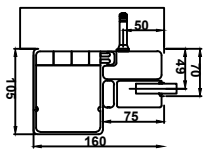

SECTION DETAIL

MAIN SLATS
DOUBLE WALL ROLLING SHUTTER

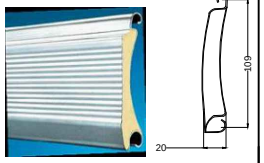

NOTES-
(1) M.S. STRUCTURE , FITTING & ALL CIVIL WORK IS IN CLIENT SCOPE .
(2) KINDLY CONFIRM FIXING OPTION AS PER SITE CONDITION.
(3) MS STRUCTURE DRAWING WILL BE SHARED IF IN CASE REQUIRED AS PER SITE CONDITION.

STANDARD COLOR OF SLATS & SHUTTER -RAL9002 (GRAY WHITE)

CLEAR WIDTH	CLEAR HEIGHT	QUANTITY
5500 mm	5530 mm	1 NO

NOTE : DOOR TO BE FIXED FROM INSIDE ONLY

This drawing & design is the property of NIHVA TECHNOLOGIES. Not to be sold or copied to any other concern.

TITLE	DOUBLE WALL ROLLING SHUTTER	NIHVA TECHNOLOGIES PVT. LTD.	NIHVA TECHNOLOGIES PVT. LTD. PUNE Tel : 020 66304033 Email:- info@nihva.com Website :- www.nihva.com
	NAME / SIGN / DATE		
DRAWN	S.M.S. / 6.10.2020	CLIENT - SCON PROJECTS PVT LTD	
CHECK		PROJECT - GESTAMP AUTOMOTIVE INDIA PVT LTD	
APPRD.		SITE LOCATION - PUNE	
If any queries contact : projectsupport@nihva.com		DWG. NO. : NIHVA/20-21/0113	REV- R01
ALL DIMENSION ARE IN mm		SCALE: NTS / WT: / SHEET:	