




ELEVATION

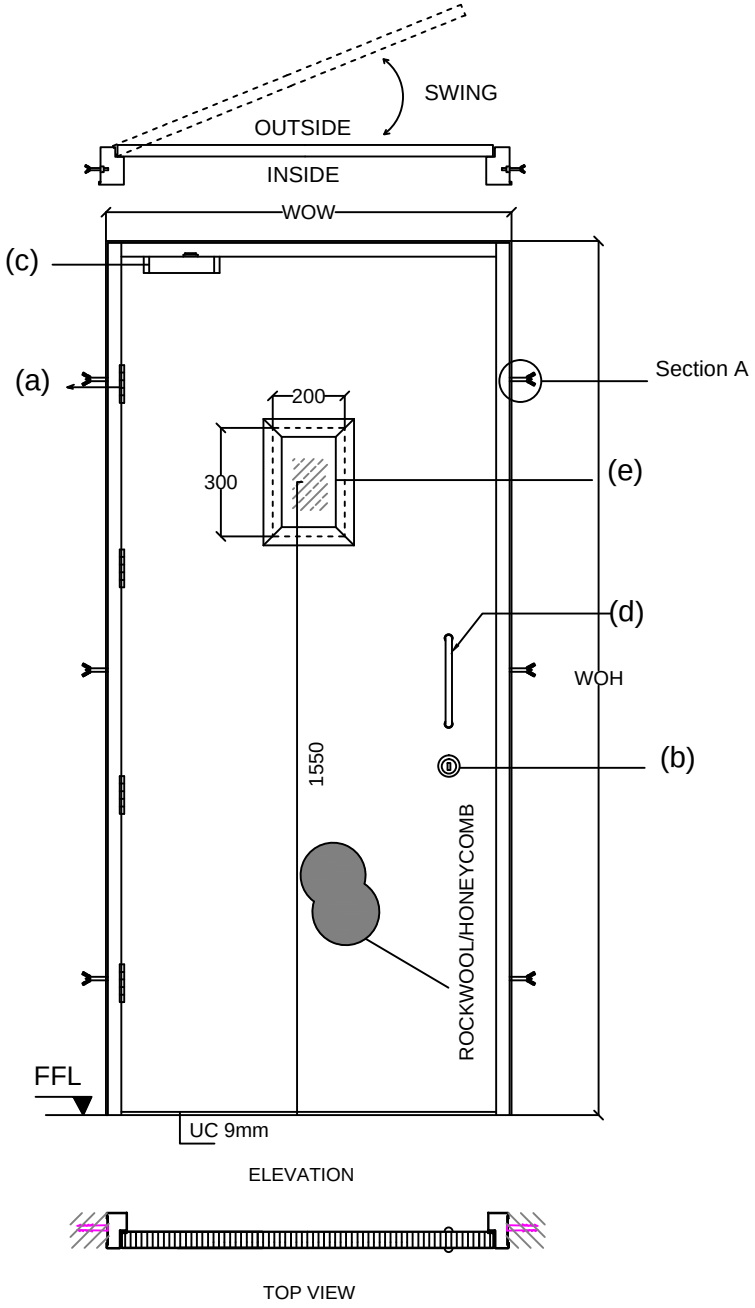

TOP VIEW

Abbrevation's:
WOW-Wall Opening Width
WOH-Wall Opening Height
UC-Under Cut
FFL-Finished Floor Level

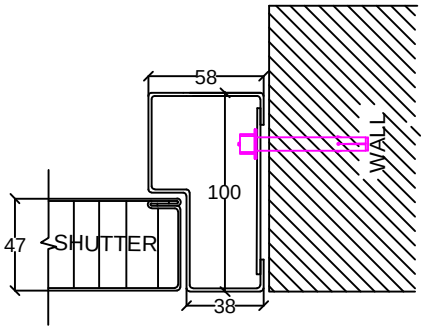


Section A

## ASSESORIES DETALES

(a) HINGES: SS Ball bearing butt hinges size 100x75x3mm

(b) LOCK : Mortise Dead lock,Cylinder(Both side key) with Escutcheon

(c) DOOR CLOSER :

(d) HANDLE : SS D HANDLE

(e) VISION PANEL : 5 mm THK. VISION GLASS 200(W) X 300(H)mm

Shutter thickness : 47 mm
Frame Sheet thick : 1.20mm
Shutter sheet thick : 0.80mm
Fixing : On Soliid Brick plasterd wall with Anchors

NOTE:- *All Dimensions are in mm.
*Tolerance:-All Linear Dimensions ±3mm,Others ±0.5mm.
*The Drawing Is For Location of Hardware only. Drawing Does Not Represent The Hardware For More Clarity, Please Go Through Hardware Broucher.

## Steel door size

| | WOW | WOH | TYPE 1 | TYPE 2 | TYPE 3 | TYPE 4 | QUANTITY |
|---|---|---|---|---|---|---|---|
| DOOR 3 | 990 | 2145 | | | | 1 | 1 |

This drawing & designing is the property of NIHVA TECHNOLOGIES. Not be sold or copy to any other concern.

FIRE RATED STEEL DOOR (SINGLE LEAF)

CLIENT APPROVAL

ALL DIMENSION ARE IN mm

| | NAME | DATE | SIGN. |
|---|---|---|---|
| DRAWN BY | OMKAR | 15/03/17 | |
| CHECK BY | SAGAR P. | 15/03/17 | |
| REV. | | | |
| APPROVED BY | R.K. | 15/03/17 | |
| MFG | | | |
| | | | |

NIHVA TECHNOLOGIES PVT. LTD. PUNE
Tel : 020 66304033
Email:- info@nihva.com
Website:-www.nihva.com

CLIENT -
PROJECT -
SITE -
DWG. NO. - NIHVA/16-17/VDR/068
SCALE: NTS | WT: | SHEET: 01 OF 01
If any queries contact : projects@nihva.com