
Weitergabe sowie Vervielfältigung dieses Dokuments, Verwertung und Mitteilung seines Inhalts sind nur nach vorheriger ausdrücklicher schriftlicher Zustimmung von SMS Meer GmbH gestattet. Das Dokument ist vor unberechtigtem Zugriff Dritter zu schützen. Zuwiderhandlungen verpflichten zu Schadensersatz. Alle Rechte aus Patent-/Gebrauchsmuster-/Markenschutz vorbehalten

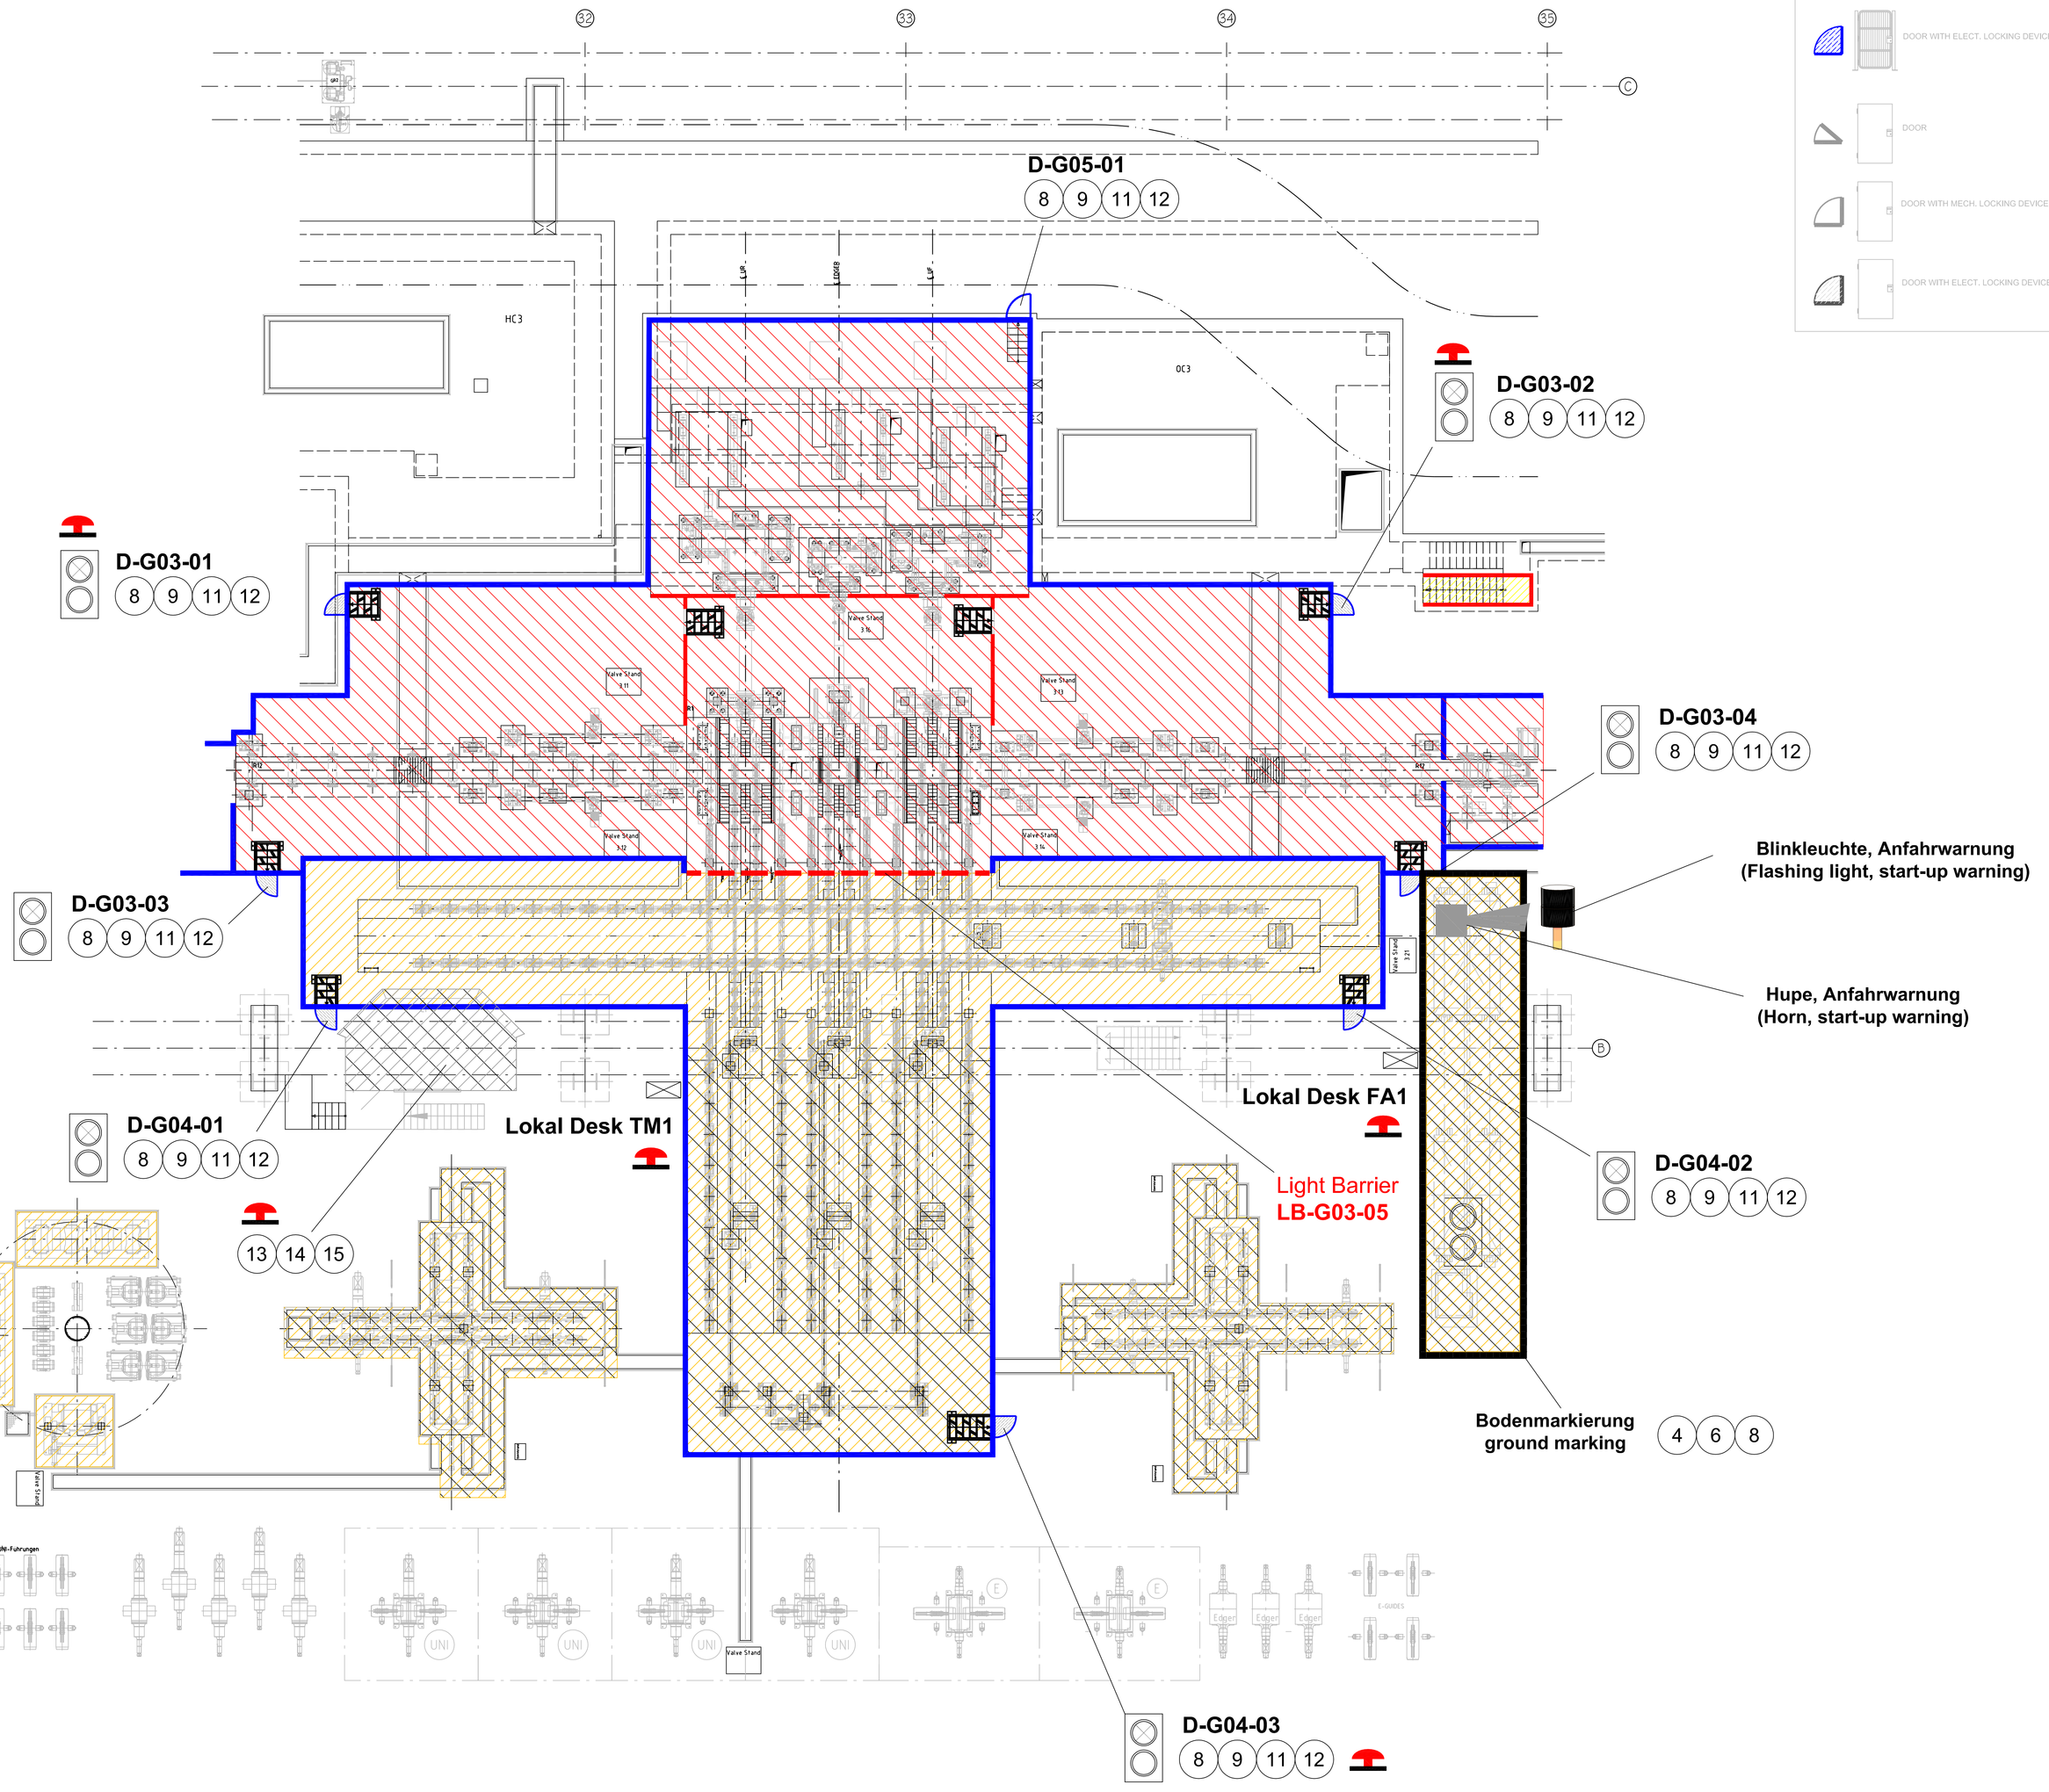

- GATE
- GATE WITH MECH. LOCKING DEVICE
- GATE WITH ELECT. LOCKING DEVICE
- DOOR WITH MECH. LOCKING DEVICE
- DOOR WITH ELECT. LOCKING DEVICE
- DOOR
- DOOR WITH MECH. LOCKING DEVICE
- DOOR WITH ELECT. LOCKING DEVICE

- DANGER ZONE 1: No access while unit is in operation.
- DANGER ZONE 2: Access only to qualified and authorized persons possible in defined operating states. High Residual Risks. Note safety instructions in operating and maintenance manual.
- DANGER ZONE 3: Access only to qualified and authorized persons possible in defined operating states. Low Residual Risks. Note safety instructions in operating and maintenance manual.
- DANGER ZONE 4: Permanente working place. Unrestricted access possible while unit is in operation. Note general safety instructions.
- WORKING PLACE: Part of no access zone, that can be entered by trained operators under particular conditions only. Note safety instructions in operating and maintenance manual.

- REQUEST-/ ACKNOWLEDGEMENT BUTTON
- EMERGENCY STOP
- ACKNOWLEDGEMENT BUTTON

- ESCAPE ROUTES
- RAILING
- REMOVABLE RAILING
- FENCE
- REMOVABLE FENCE
- REMOVABLE CHAIN
- LIGHT CURTAIN

9463 0000 / RAILBHIL

CATEGORY OF DRWG.	APPROVAL	INFORMATION	REFERENCE	RECORD	CONSTRUCTION

BHILAI STEEL PLANT, BHILAI, CHATTISGARH
7,0 MTPA EXPANSION

मेकॉन लिमिटेड
MECON LIMITED

VENSDOR'S NAME: SMS Meer/SMS Meer India/ABB
PACKAGE DESCRIPTION: UNIVERSAL RAIL MILL (Pkg No-047)
TITLE OF DRAWING. PARTITION 5, SAFETY LAYOUT
SCALE-
VENDOR'S DRG NO.-
PROJECT DRG. NO. BSP-SMS Meer-08-047-21-130-35-BE-06653 REV. -

Fertigungsvorschriften / Manufacturing Instructions: SN 200
Ursprung / Origin
Fertiggewicht / Finished weight: kg
Modell-Nr. / Pattern-No.
Werkstoff / Material
Projektionsmethode 1 / First angle projection method ISO 128

	Datum / Date	Name
Bearb. / Drawn	27.09.11	Fryen
Gepr. / Checked	27.09.11	Pratzel
Norm / Stand		

Typ / Type: Safety Layout
Benennung: Teilbereich. 5
Title: PARTITION 5
Maßstab / Scale: 1:100
Sach-Nr / Drawing-No: 0100133-00.653
Blatt / Sheet 1, Blätter / Sheets 2
Ersatz für / Supersedes
Ersetzt durch / Superseded by:

Aus-gabe	Änderung / Revision	Datum / Date	Name

SMS MEER
SMS group

Diese Zeichnung und alle darauf enthaltenen Informationen sind vertraulich. This drawing and all information on it is confidential.

Weitergabe sowie Vervielfältigung dieses Dokuments, Verwertung und Mitteilung seines Inhalts sind nur nach vorheriger ausdrücklicher schriftlicher Zustimmung von SMS Meer GmbH gestattet. Das Dokument ist vor unberechtigtem Zugriff Dritter zu schützen. Zuwiderhandlungen verpflichten zu Schadensersatz. Alle Rechte aus Patent-/Gebrauchsmuster-/Markenschutz vorbehalten