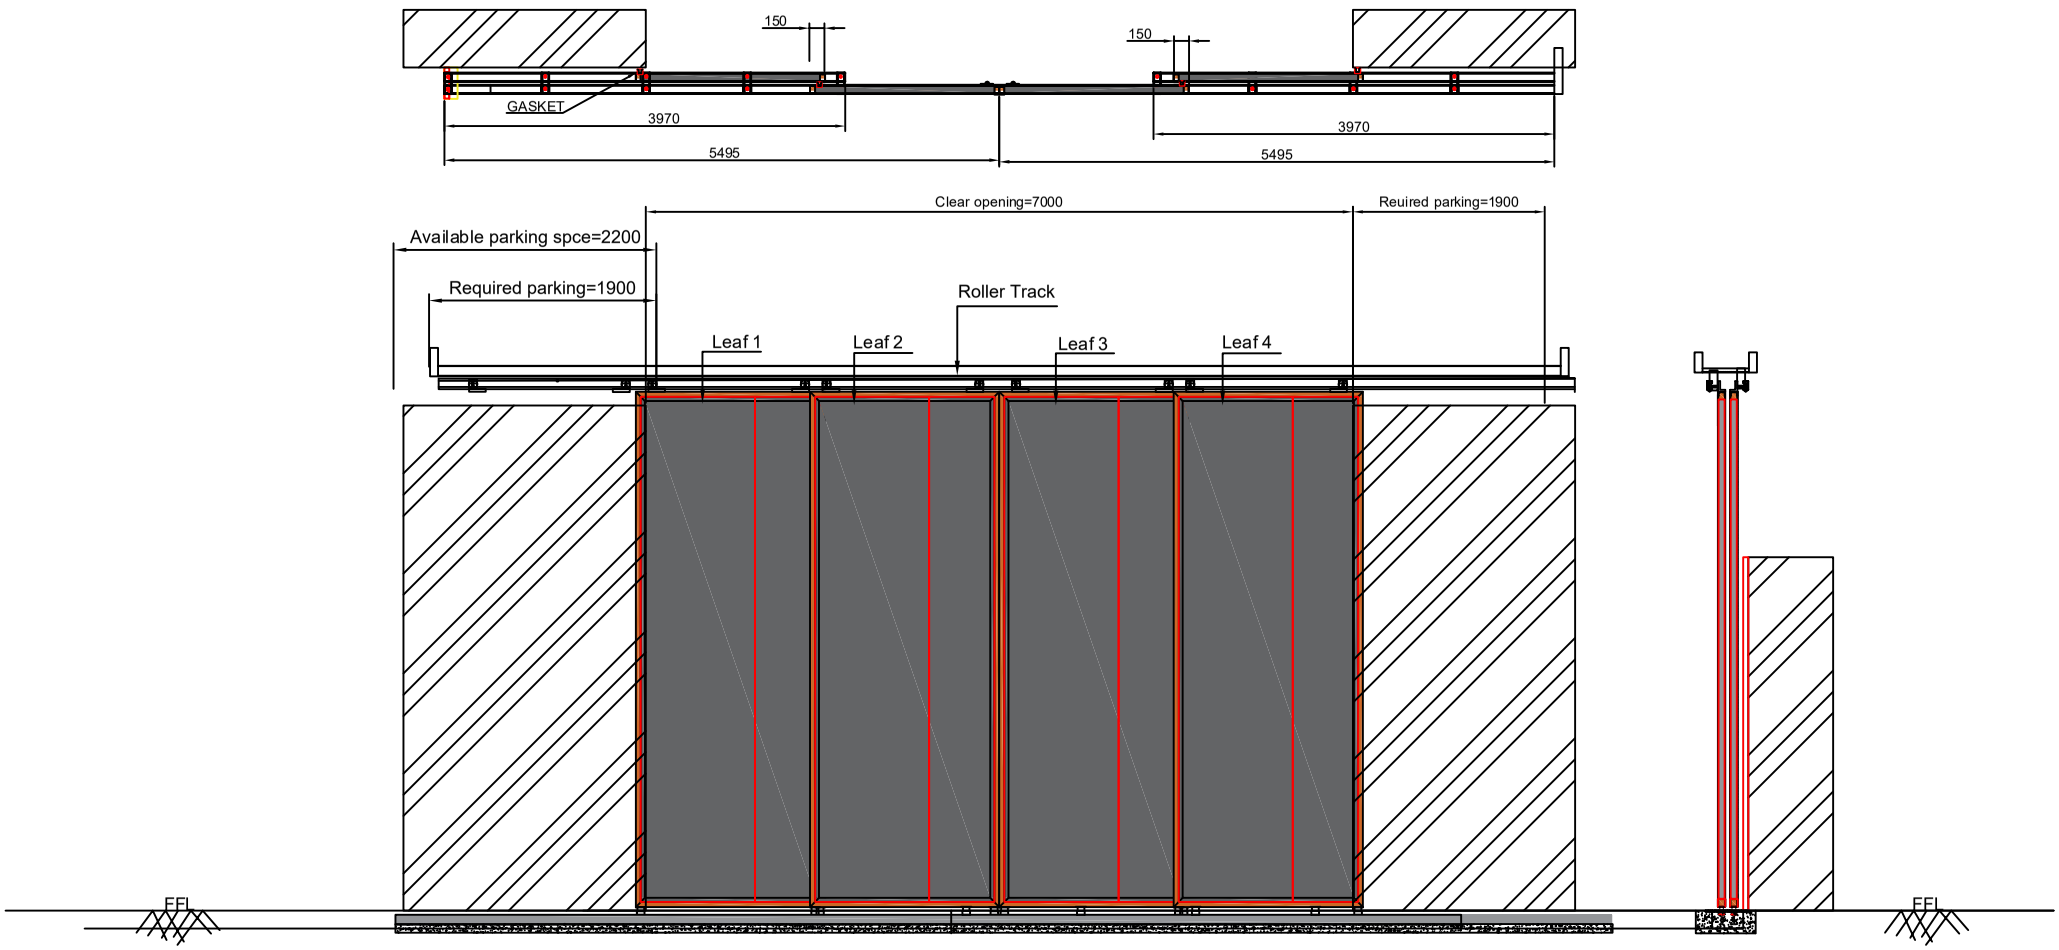


1.All dimension are in MM

Client scope
*Roof need to be shift at top Approx 300mm *Drainage area need to be remove frome left side appox.200mm *Gutter area need to be remove *Civil foundation need to be done for tracks

This drawing & design is the property of NIHVA TECHNOLOGIES. Not to be sold or copied to any other concern.

TITLE:-4LEAF BOTH SIDE SLIDING
CRM DOOR-10

	NAME	DATE	SIGN
DRAWN	SUJATA	20/04/2022	
CHECK	M.SUTAR	20/04/2022	
APPRD.	V.TARAK	20/04/2022	

NIHVA TECHNOLOGIES PVT. LTD.
NIHVA TECHNOLOGIES PVT. LTD. PUNE
Tel : 020 66304033
Email:- info@nihva.com
Website:- www.nihva.com

CLIENT - LESTECH
LOCATION - POSCO MANGAON
PRODUCT - SLIDING DOOR
If any queries contact : design@nihva.com
DWG NO:-NIHVA/22-23/CLT/0017 REV- 0
ALL DIMENSION ARE IN mm
SCALE: NTS SCALE:-- 1:1 SHEET: 01 OF 01

Rev No.	Revision	Date	Revised By