


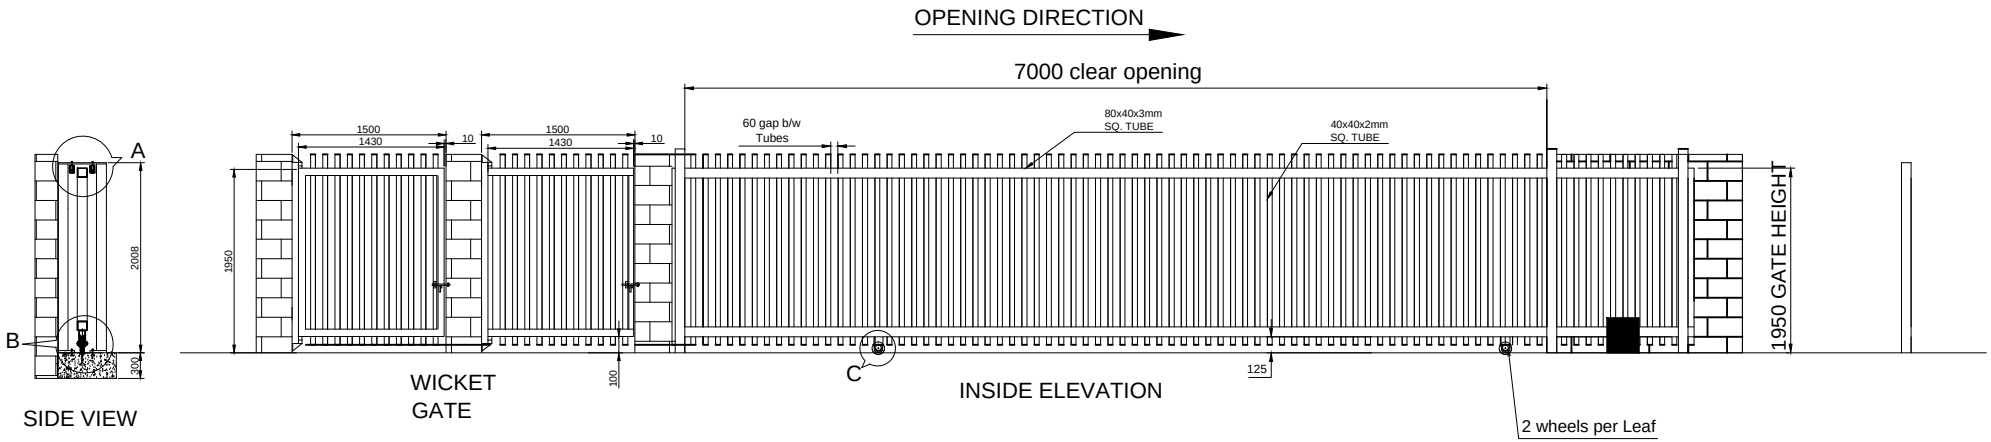


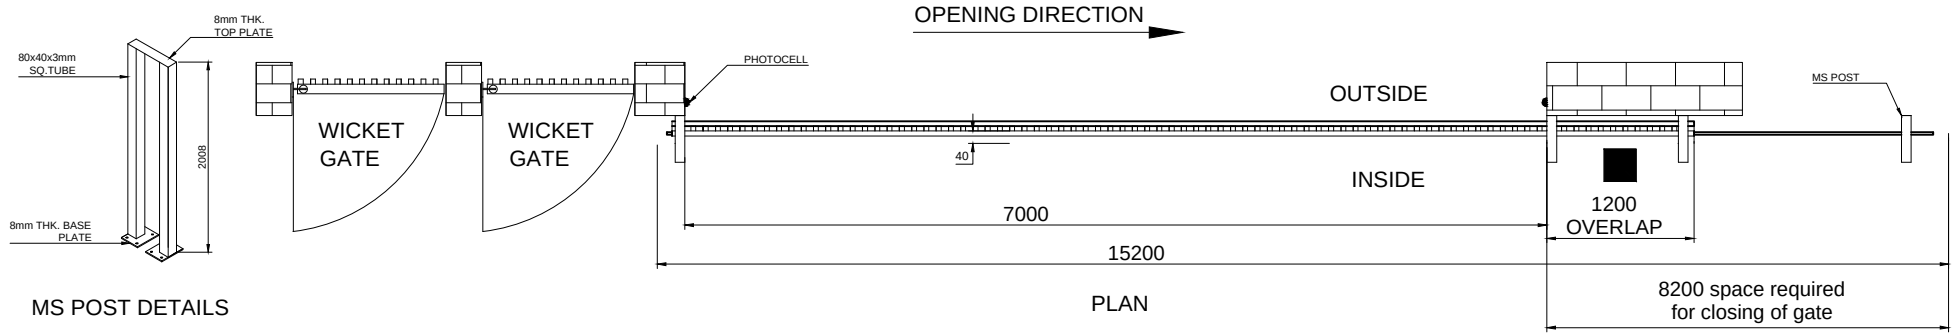


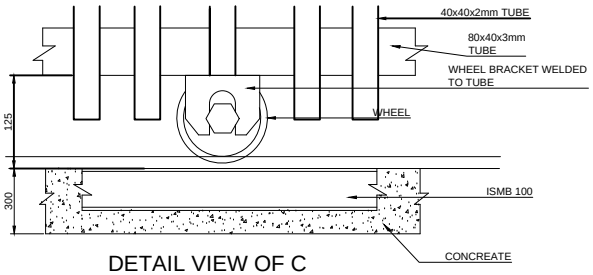

DETAIL VIEW OF C

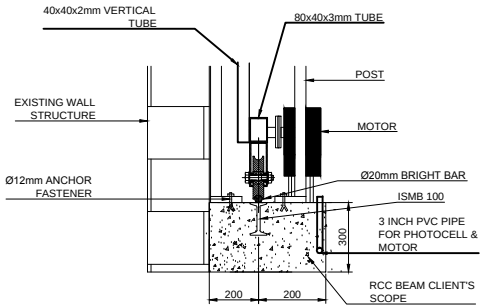


DETAIL VIEW OF B

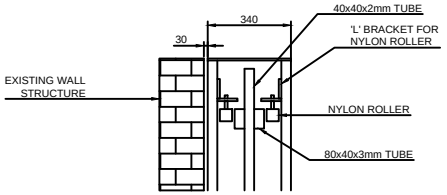


DETAIL VIEW OF A

| MOTORISED SINGLE LEAF SLIDING GATE & WICKET GATE | | | | |
|---|---|---|---|---|
| DESCRIPTION | CLEAR WIDTH | OVERALL WIDTH | CLEAR HEIGHT | QTY. |
| SLIDING GATE | 7000 | 8200 | 1950 | 1 NOS |
| WICKET GATE | 1500 | | 1950 | 1 NOS |
| NOTE- ALL REQUIRED CIVIL WORK WILL BE IN CLIENT'S SCOPE. | | | | |

This drawing & designing is the property of NIHVA TECHNOLOGIES. Not be sold or copy to any other concern.

| | | |
|---|---|---|
| TITLE: SINGLE LEAF MOTORIZED SLIDING GATE | NIHVA TECHNOLOGIES PVT. LTD. | NIHVA TECHNOLOGY PVT. LTD. PUNE<br>Tel : 020 66304033<br>Email:- info@nihva.com<br>Website:- www.nihva.com |
| | SIGN | DATE |
| DRAWN | OMKAR | 21/06/16 |
| CHECK | ANIL | 21/06/16 |
| REV. | 01 | |
| APPROVAL | | |
| If any queries contact : projects@nihva.com | | |
| ALL DIMENSION ARE IN mm | | |

| | | |
|---|---|---|
| CLIENT - MAHENDRA WINDOOR SOLUTIONS | | |
| PROJECT - AUROBINDO PHARMA LIMITED | | |
| SITE - | | |
| DWG. NO. : NIHVA/16-17/0026/R01 | | |
| SCALE: NTS | WT: | SHEET: 01 OF 01 |