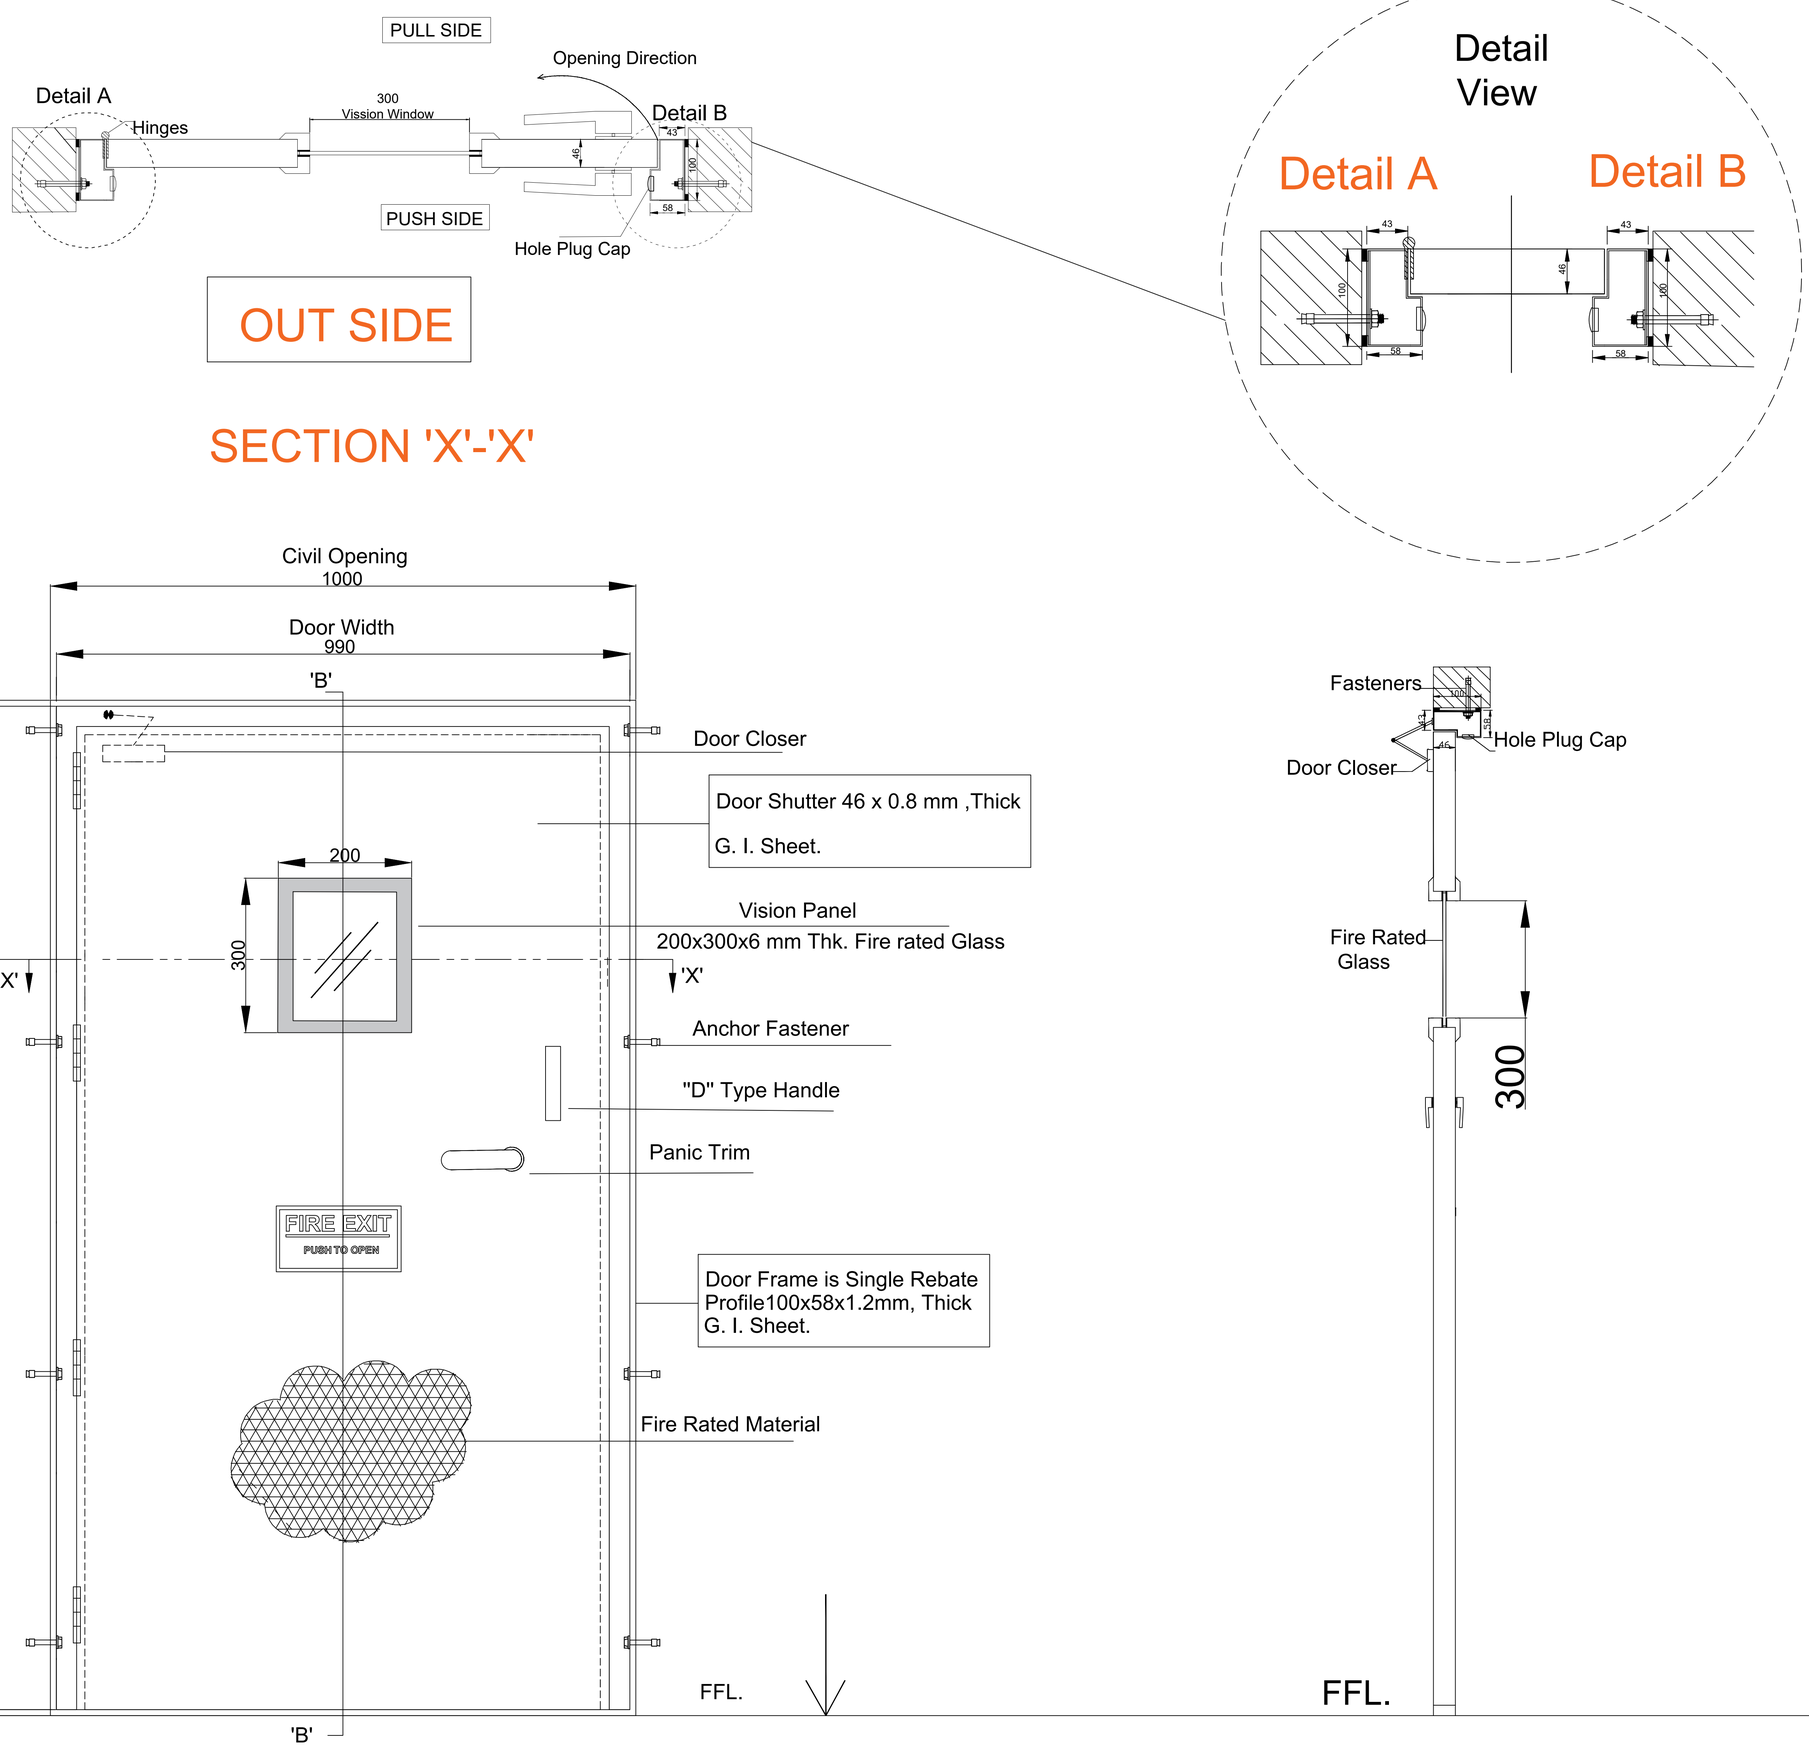


FRONT VIEW

TECHNICAL SPECIFICATION :

Sr.	DESCRIPTION & DETAILS
01	Door frame - 100X58 mm x1.2mm thick G.I. Sheet
02	Door Shutter - 46 mm x0.8mm thick G.I. Sheet
03	SS Ball Bearing Hinges 4"x3"x3mm
04	Single Leaf Panic Bar (1 Point) With silverfinish ASSA ABLOY Make
05	External " D " Type Handle With silverfinish ASSA ABLOY Make
06	Anchor Fasteners CSK Type With GI Plating Size : 8mmx80mm With PVC Sleve
07	Door Closer With Standard arm silverfinish ASSA ABLOY Make
08	Vision Window 200x300 With fire Rated Glass
09	Fire Rating - 120 Minutes
10	Surface Finish - As per Client Requirement

SIZE:(RH Opening)

Sr.	Clear Width	Clear Height	Qty
01	1000	2400	03

This Drawing & Design is the property of NIHVA TECHNOLOGIES. Not to be sold or copied to any other concern.

TITLE :- FIRE DOOR

NIHVA TECHNOLOGIES PVT. LTD.
NIHVA TECHNOLOGIES PVT. LTD. PUNE
Tel : 020 66304033
Email:- info@nihva.com
Website:- www.nihva.com

NAME	DATE	SIGN	
S.J	16/05/2024		
A.K	16/05/2024		LOCATION -
V.T	16/05/2024		PRODUCT - FIRE DOOR / QTY-05 No's
If any queries contact : design1@nihva.com			DWG NO - NIHVA/24-25/00XX / REV- 01
All dimensions are in MM			SCALE : NTS / SHEET : 01 OF 01