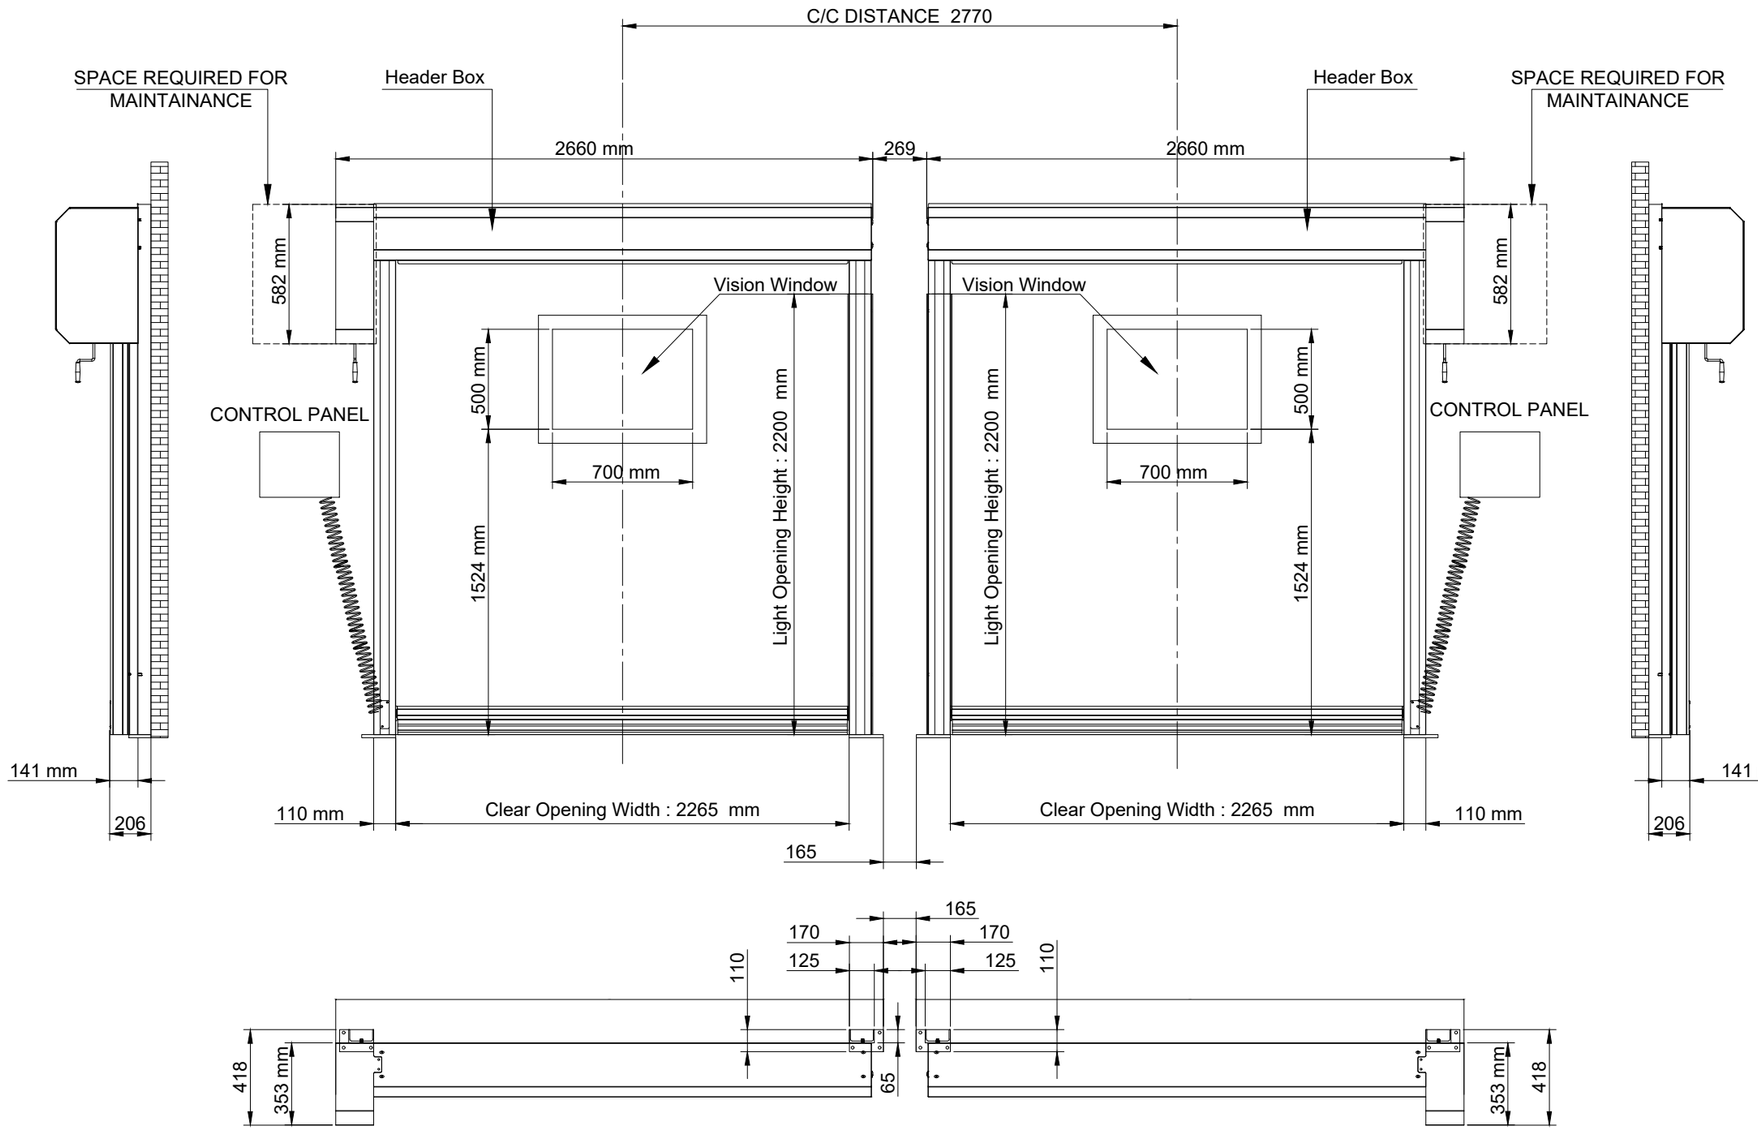


CLEAR WIDTH	CLEAR HEIGHT	QTY
2265 mm	2200mm	2 NOS

Note:-

1.All dimension are in MM

2.All civil work is in client scope

3.Given GA drawing is only for the client unerstanding purpose

4.In strucuture instead of (ISMC 125X65) Box 120*120*5 will be used, the door will be floor mounted

Rev No.	Revision	Date	Revised By

This drawing & design is the property of NIHVA TECHNOLOGIES. Not to be sold or copied to any other concern.

TITLE:-MACHINE PROTECTION DOOR

NIHVA TECHNOLOGIES PVT. LTD. PUNE
Tel : 020 66304033
Email:- info@nihva.com
Website:- www.nihva.com

	NAME	DATE	SIGN
DRAWN	NIRMALA	20/10/2023	
CHECK	A.K.	20/10/2023	
APPRD.	V.T.	20/10/2023	

If any queries contact :-design@nihva.com

ALL DIMENSION ARE IN mm

CLIENT - HIROTEC

LOCATION -

PRODUCT - Machine Protection Door

DWG NO:-NIHVA/23-24/CLT/085 | REV- 1

SCALE: NTS | SCALE:-- 1:1 | SHEET: 01 OF 01