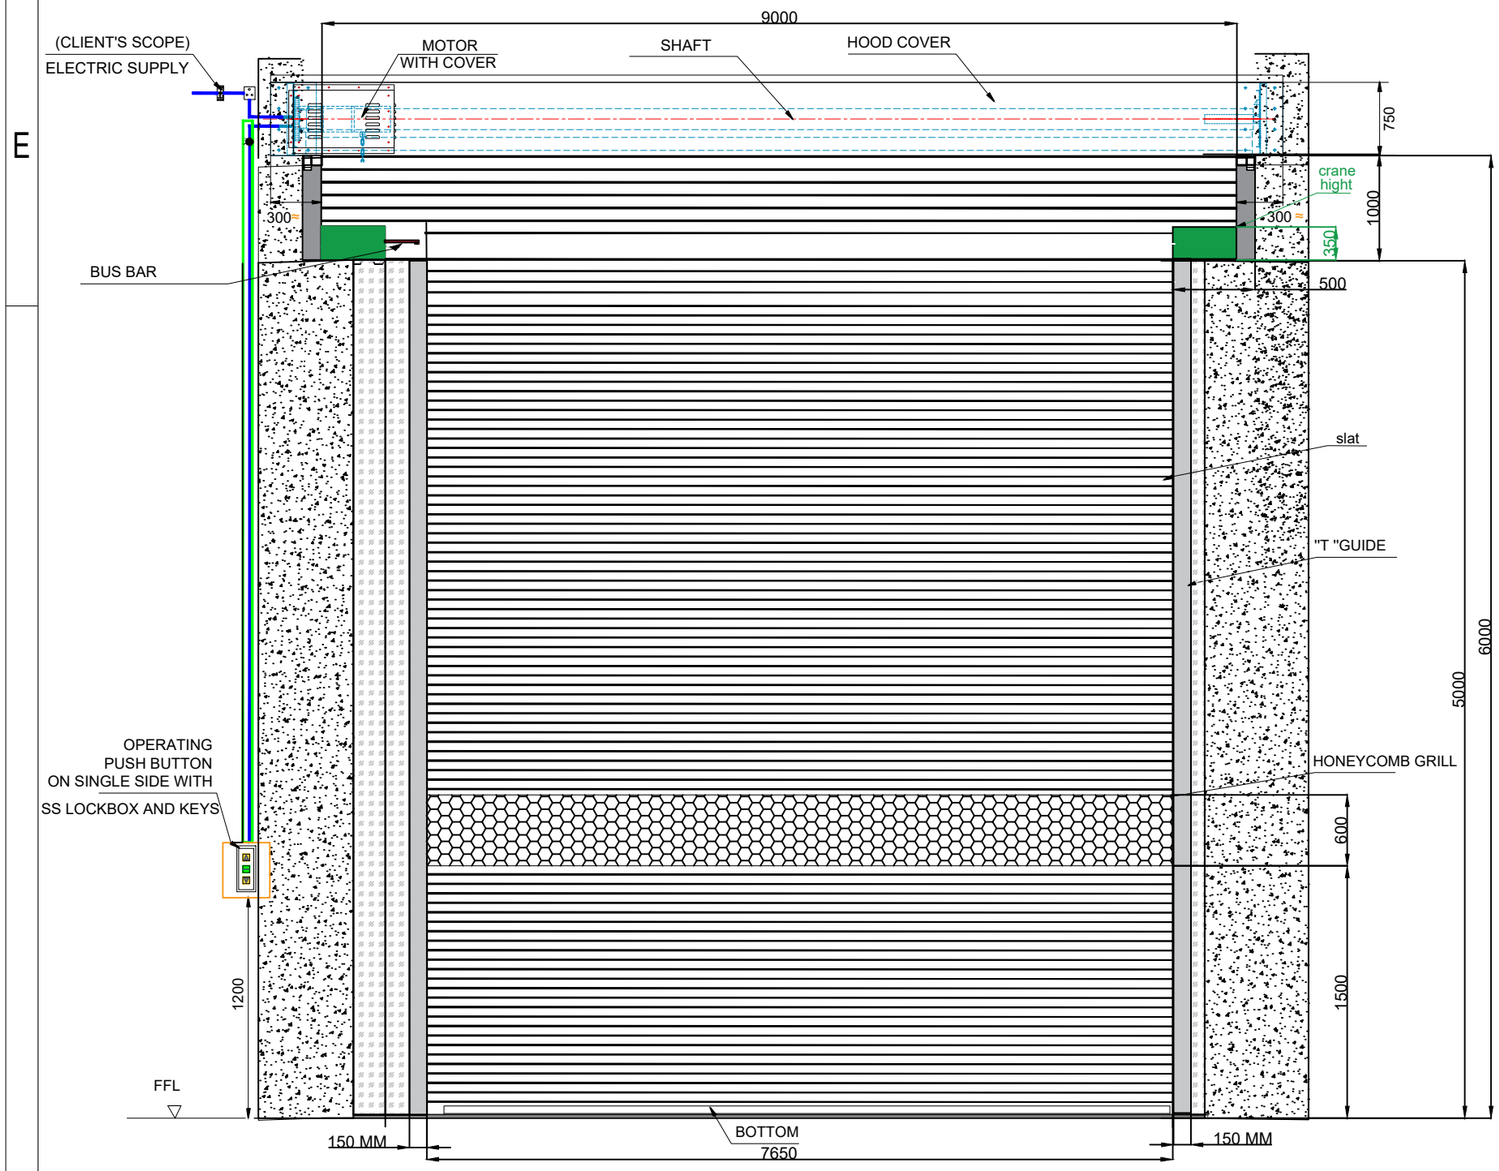


Note:-
1. All Dimensions are in mm
2. shutter mounting position is outside.

R01:- CRANE HEIGHT IS NOT MENTION PREVIOUS GA DWG -06-08-2025
R02:- HONEYCOMB GRILL IS NOT MENTION IN PREVIOUS DWG-14-08-2025
R03:- BUS BAR ADD SO SLAT SIZE IS DECREASE -26-08-2025

This drawing & design is the property of NIHVA TECHNOLOGIES. Not to be sold or copied to any other concern.

TITLE:- CRANE DOOR INPUT DRG.

	NAME	SIGN	DATE
DRAWN	B.S.		28-08-2025
CHECK & APPRD	V.T.		28-08-2025

NIHVA TECHNOLOGIES PVT. LTD. PUNE
Tel : 020 66304033
Email:- info@nihva.com
Website:- www.nihva.com

CLIENT - SAKSHI MEDTECH
PROJECT - CRANE DOOR INPUT DRG.
FORMAT NO - NIHVA-DD-F-03
If any queries contact :
DWG. NO. : NTPL-292-PM
REV- 03
ALL DIMENSION ARE IN mm
SCALE: NTS
WT:
SHEET:
A

4 3 2 1