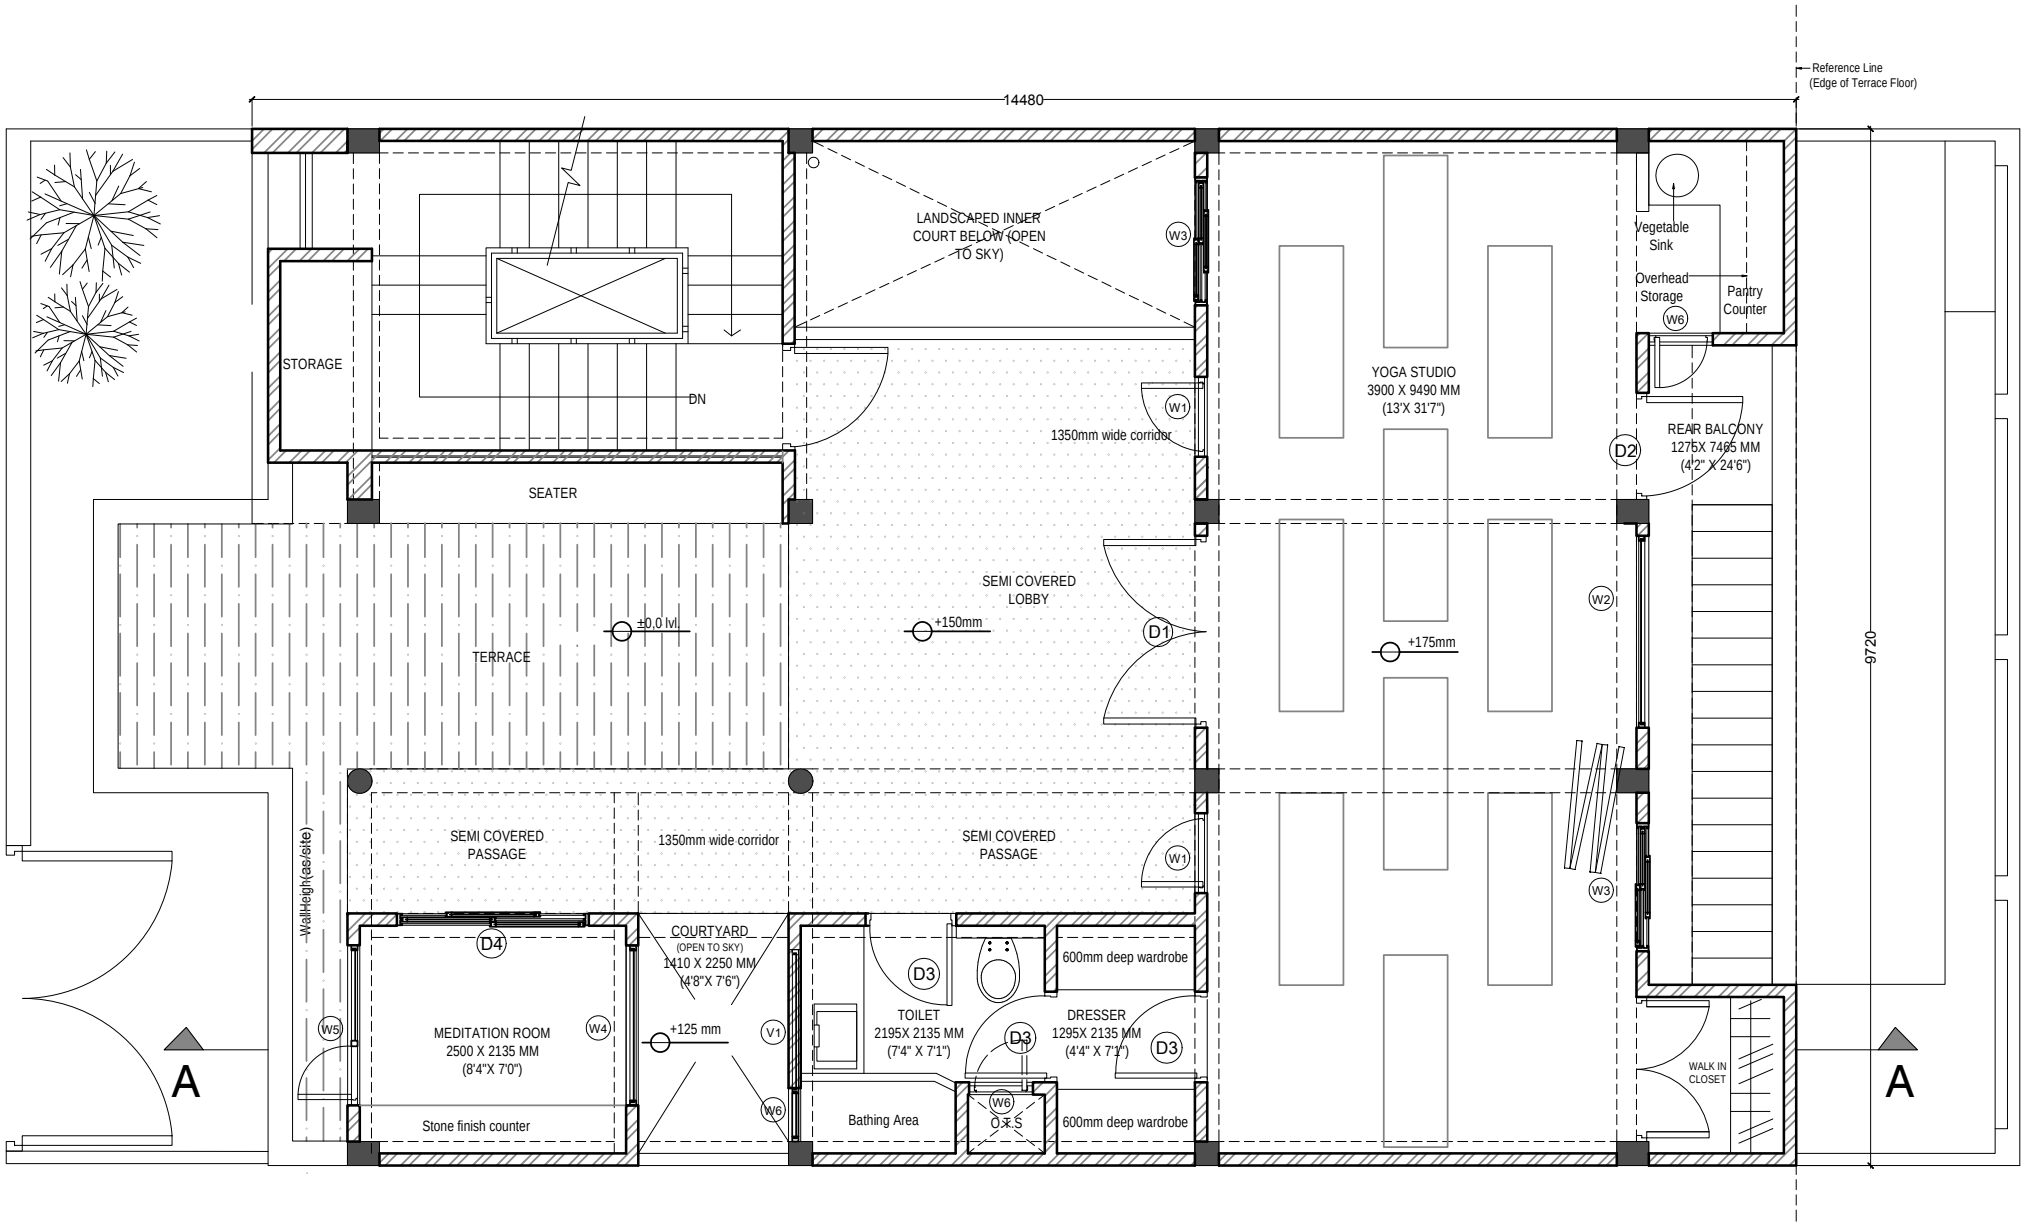


NOTES & INFORMATION

#1 THIS DRAWING IS THE PROPERTY OF **FORUM ARCHITECTURE** AND CANNOT BE USED FOR ANY PURPOSE THAN SPECIFIED WITHOUT THEIR WRITTEN PERMISSION.
#2 ALL DIMENSIONS ARE IN MM
#3 READ, DO NOT MEASURE.
#4 ANY DISCREPANCY IN THE DRAWING WILL BE BROUGHT TO THE NOTICE OF THE ARCHITECTS / CONSULTANTS IMMEDIATELY.

PROJECT :

RESIDENCE INTERIORS

CLIENT:
Ms. VANDANA & SHEFALI SHARMA

SITE:
F67, SEC 41, NOIDA

VERSION	DATE
1	01.07.2019
2	
3	
4	
5	

DRAWING TITLE

First Floor Layout

DRAWN BY:

SCALE: 1:50

DRAWING NO.: 1


N

ARCHITECTS:

FORUM ARCHITECTURE

892/A-2, ward no.8, khasra no. 1151/3,
Kalka Das Marg,
next to Andheria mode, Mehrauli,
New Delhi - 110030

web - www.forumarch.com
mail - studio@forumarch.com
Ph - (+91) 99104 90404 , 98116 00754

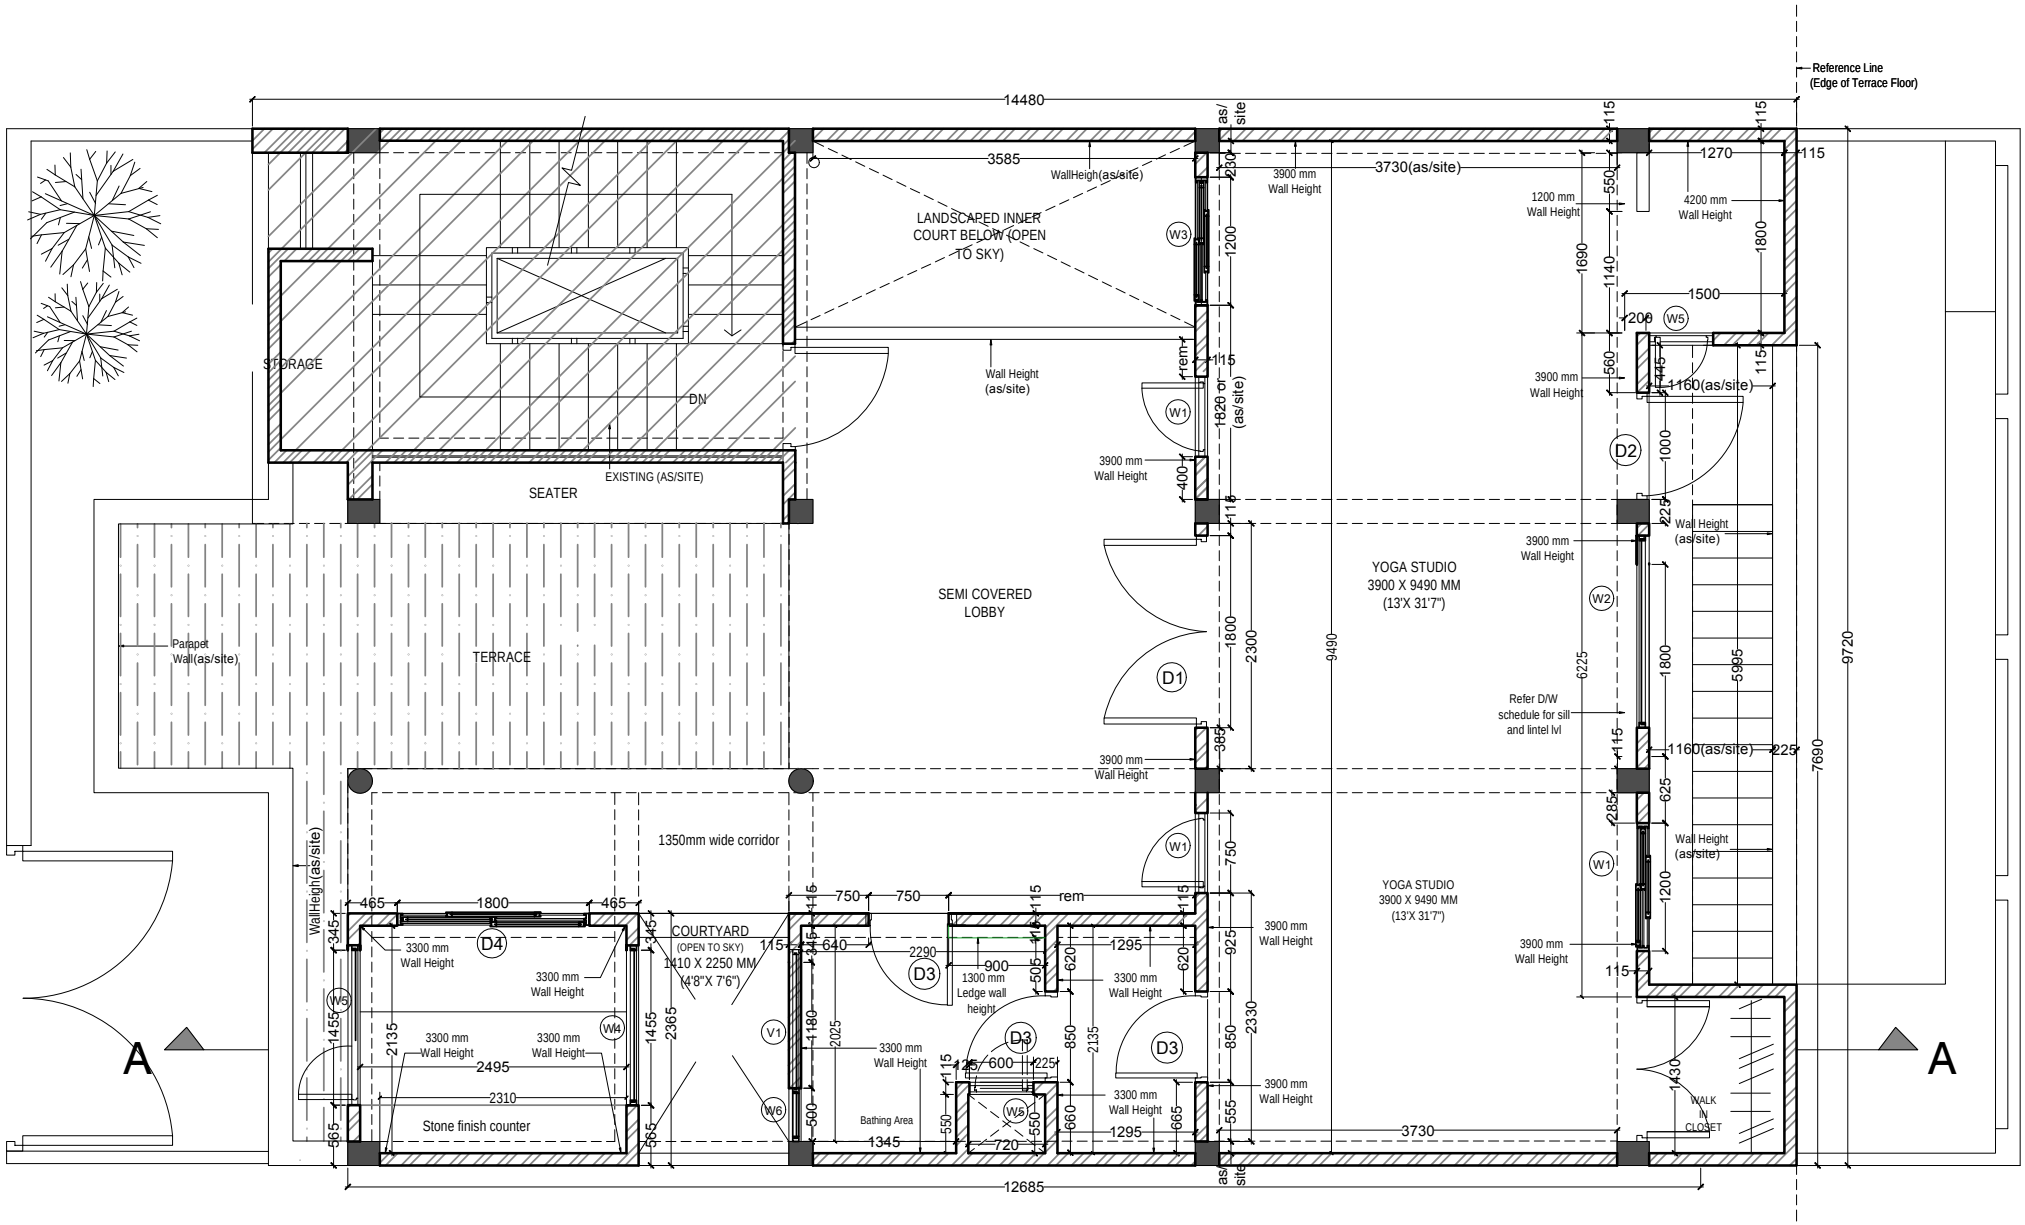

NOTES & INFORMATION

#1 THIS DRAWING IS THE PROPERTY OF **FORUM ARCHITECTURE** AND CANNOT BE USED FOR ANY PURPOSE THAN SPECIFIED WITHOUT THEIR WRITTEN PERMISSION.
#2 ALL DIMENSIONS ARE IN MM
#3 READ, DO NOT MEASURE.
#4 ANY DISCREPANCY IN THE DRAWING WILL BE BROUGHT TO THE NOTICE OF THE ARCHITECTS / CONSULTANTS IMMEDIATELY.

PROJECT :

RESIDENCE INTERIORS

CLIENT:
Ms. VANDANA & SHEFALI SHARMA

SITE:
F67, SEC 41, NOIDA

VERSION	DATE
1	01.07.2019
2	
3	
4	
5	

DRAWING TITLE
New Construction

DRAWN BY:

SCALE
1:50

DRAWING NO.
2


N

ARCHITECTS:

FORUM ARCHITECTURE

892/A-2, ward no.8, khasra no. 1151/3,
Kalka Das Marg,
next to Andheria mode, Mehrauli,
New Delhi - 110030

web - www.forumarch.com
mail - studio@forumarch.com
Ph - (+91) 99104 90404 , 98116 00754

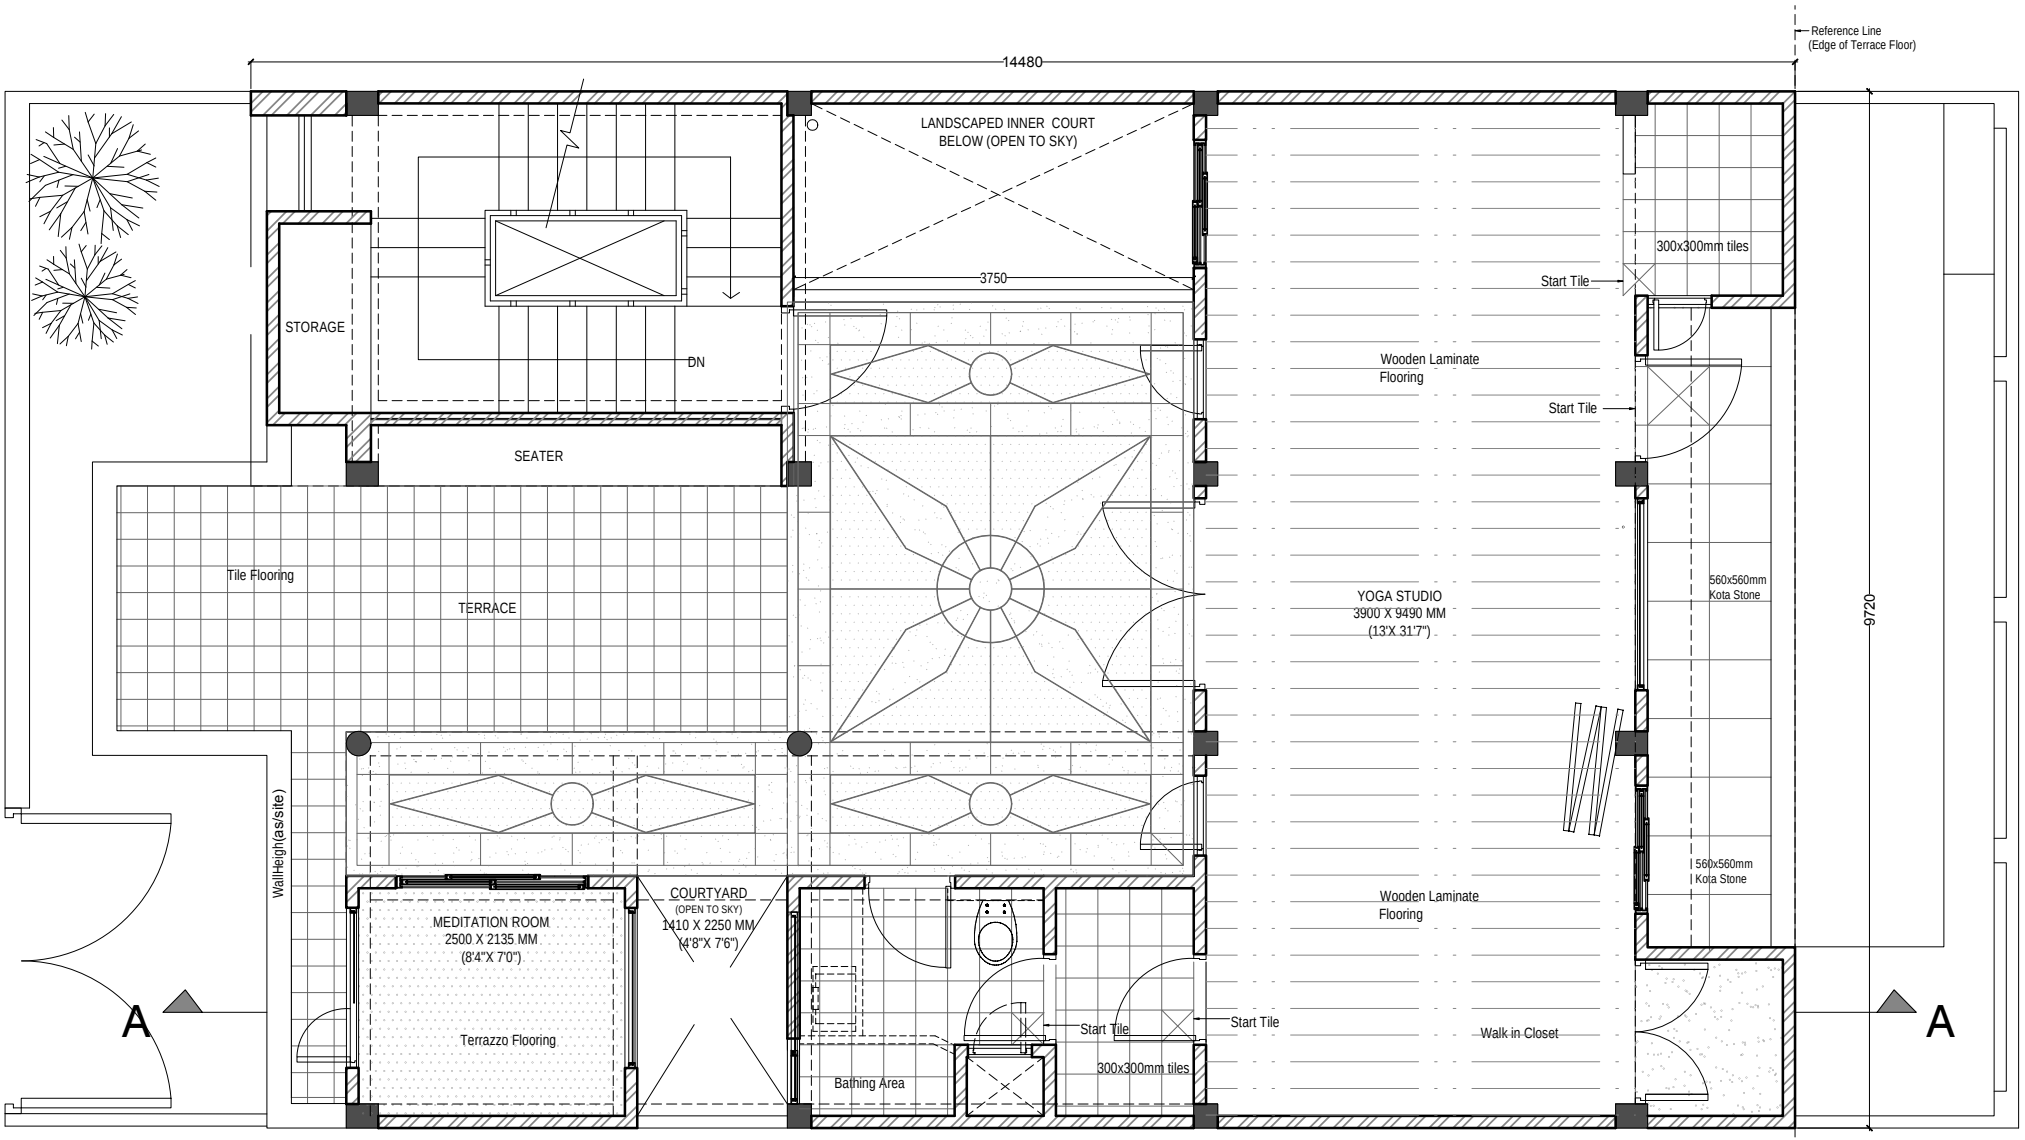

FLOORING LEGEND

S.NO.	FLOORING TYPE	HATCH PATTERN
1.	Wooden Laminate Flooring	
2.	Terrazzo Flooring	
3.	Jaisalmar Stone	

NOTES & INFORMATION

#1 THIS DRAWING IS THE PROPERTY OF **FORUM ARCHITECTURE** AND CANNOT BE USED FOR ANY PURPOSE THAN SPECIFIED WITHOUT THEIR WRITTEN PERMISSION.
#2 ALL DIMENSIONS ARE IN MM
#3 READ, DO NOT MEASURE.
#4 ANY DISCREPANCY IN THE DRAWING WILL BE BROUGHT TO THE NOTICE OF THE ARCHITECTS / CONSULTANTS IMMEDIATELY.

PROJECT :

RESIDENCE INTERIORS

CLIENT:
Ms. VANDANA & SHEFALI SHARMA

SITE:
F67, SEC 41, NOIDA

VERSION	DATE
1	01.07.2019
2	
3	
4	
5	

DRAWING TITLE
Flooring (O.P. - 1)

DRAWN BY:

SCALE
1:50

DRAWING NO.
3


N

ARCHITECTS:

FORUM ARCHITECTURE

892/A-2, ward no.8, khasra no. 1151/3,
Kalka Das Marg,
next to Andheria mode, Mehrauli,
New Delhi - 110030

web - www.forumarch.com
mail - studio@forumarch.com
Ph - (+91) 99104 90404 , 98116 00754

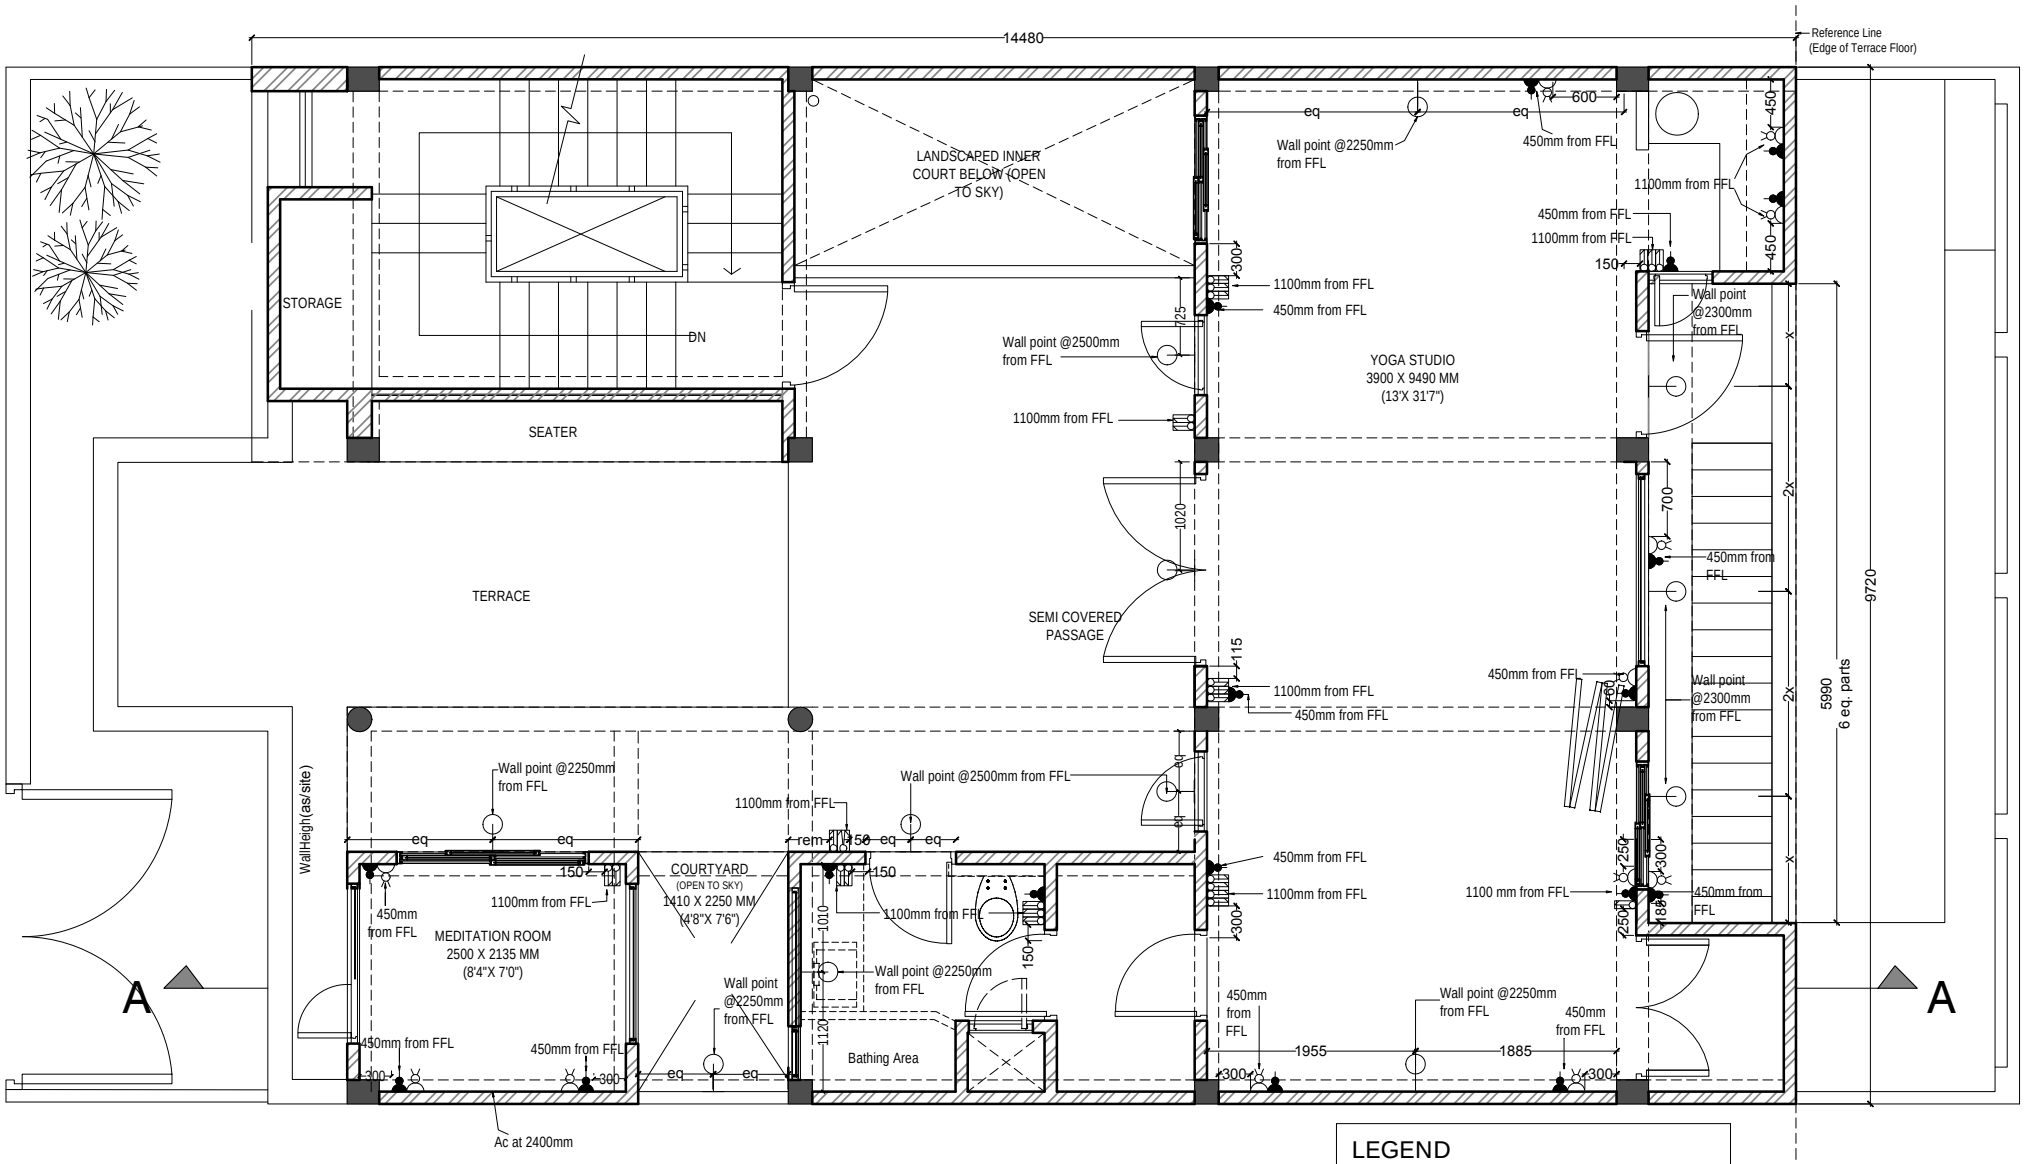

LEGEND			
6 Amp (3 module)		Ceiling Light point	
Wall point		Two Way Switch	
16 Amp (3 module)		Switch	
Exhaust		Fan	

NOTES & INFORMATION

#1 THIS DRAWING IS THE PROPERTY OF **FORUM ARCHITECTURE** AND CANNOT BE USED FOR ANY PURPOSE THAN SPECIFIED WITHOUT THEIR WRITTEN PERMISSION.
#2 ALL DIMENSIONS ARE IN MM
#3 READ, DO NOT MEASURE.
#4 ANY DISCREPANCY IN THE DRAWING WILL BE BROUGHT TO THE NOTICE OF THE ARCHITECTS / CONSULTANTS IMMEDIATELY.

PROJECT :

RESIDENCE INTERIORS

CLIENT:
Ms. VANDANA & SHEFALI SHARMA

SITE:
F67, SEC 41, NOIDA

VERSION	DATE
1	01.07.2019
2	
3	
4	
5	

DRAWING TITLE

Electric Wall Points

DRAWN BY:

SCALE: 1:50

DRAWING NO.: 4.1


N

ARCHITECTS:

FORUM ARCHITECTURE

892/A-2, ward no.8, khasra no. 1151/3,
Kalka Das Marg,
next to Andheria mode, Mehrauli,
New Delhi - 110030

web - www.forumarch.com
mail - studio@forumarch.com
Ph - (+91) 99104 90404 , 98116 00754

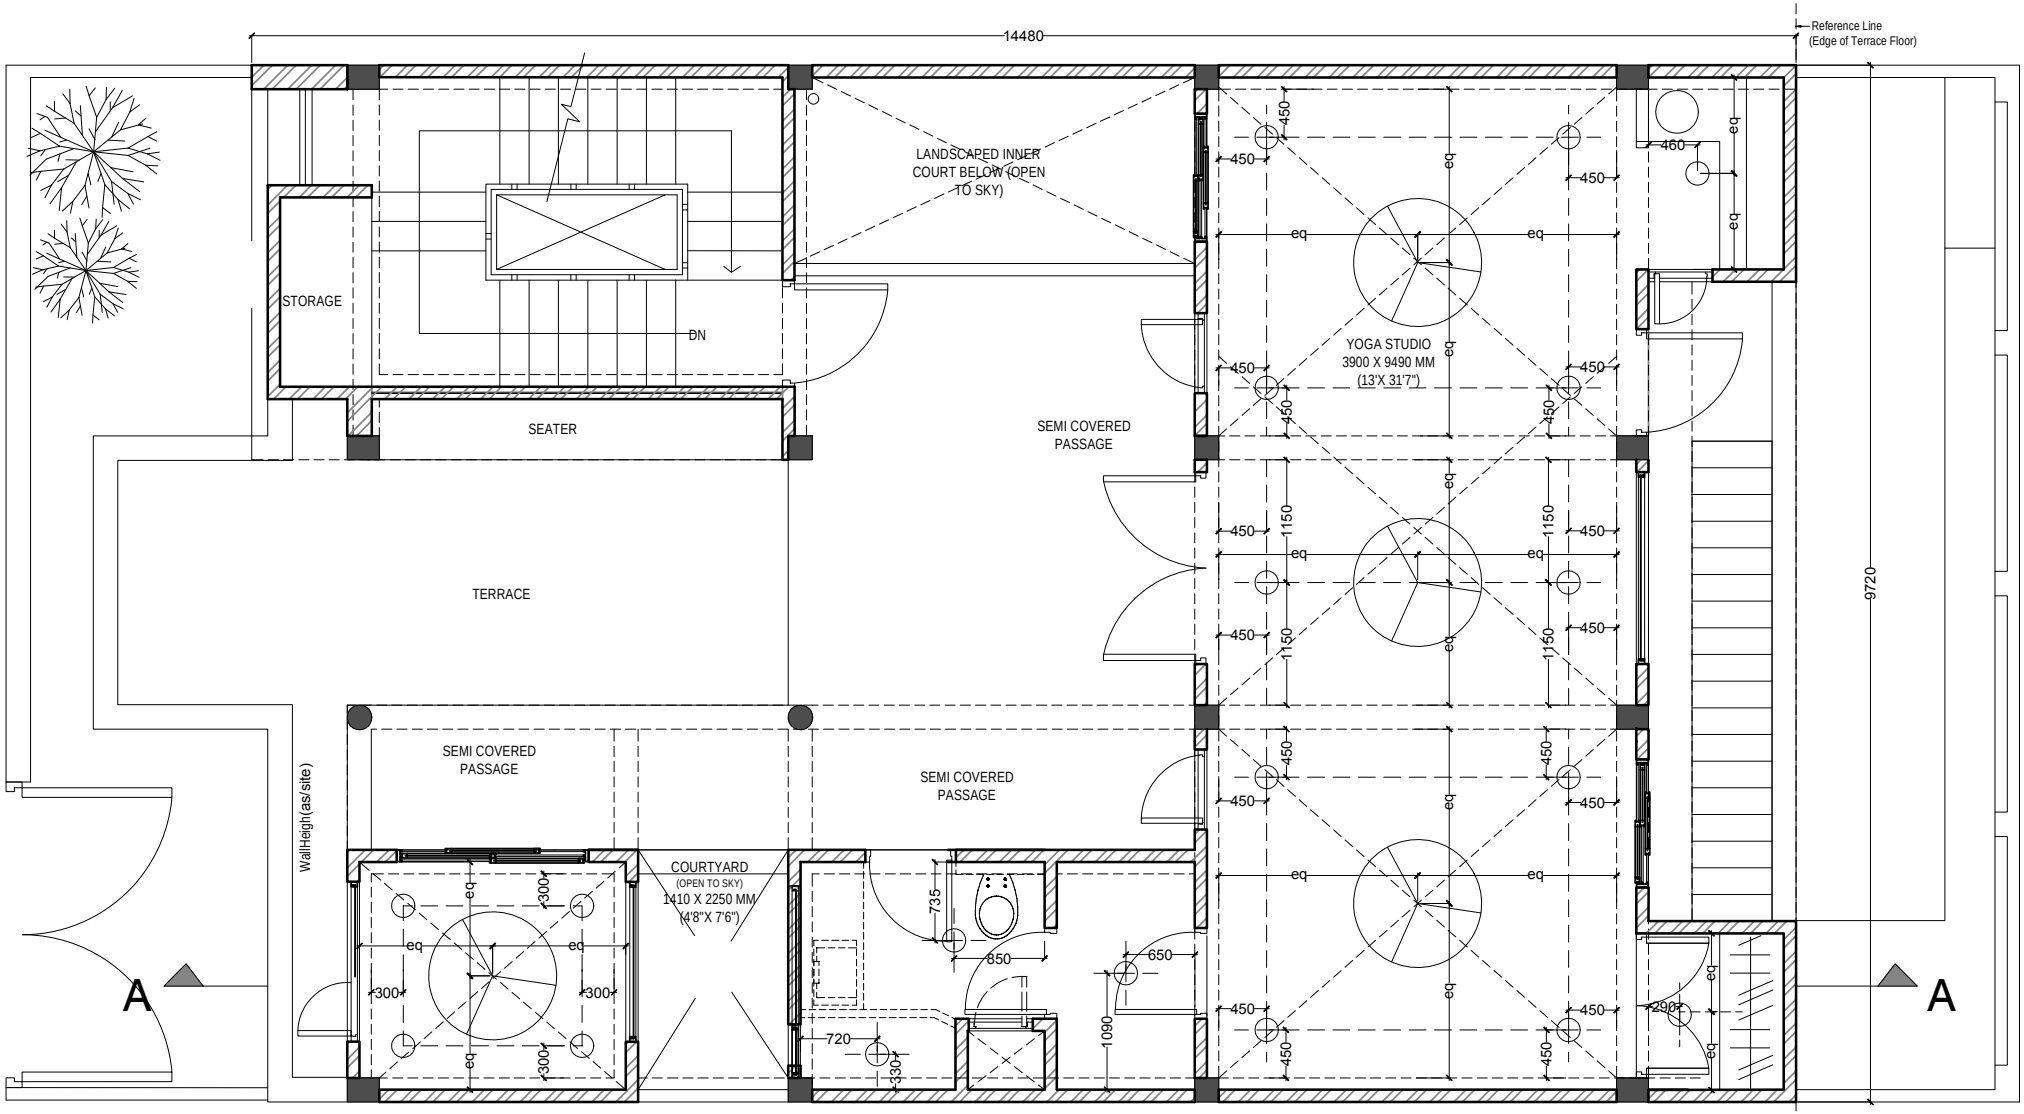

LEGEND

6 Amp (3 module)		Ceiling Light point	
Wall point		Two Way Switch	
16 Amp (3 module)		Switch	
Exhaust		Fan	

NOTES & INFORMATION

#1 THIS DRAWING IS THE PROPERTY OF **FORUM ARCHITECTURE** AND CANNOT BE USED FOR ANY PURPOSE THAN SPECIFIED WITHOUT THEIR WRITTEN PERMISSION.
#2 ALL DIMENSIONS ARE IN MM
#3 READ, DO NOT MEASURE.
#4 ANY DISCREPANCY IN THE DRAWING WILL BE BROUGHT TO THE NOTICE OF THE ARCHITECTS / CONSULTANTS IMMEDIATELY.

PROJECT :

RESIDENCE INTERIORS

CLIENT:
Ms. VANDANA & SHEFALI SHARMA

SITE:
F67, SEC 41, NOIDA

VERSION	DATE
1	01.07.2019
2	
3	
4	
5	

DRAWING TITLE

Electric Ceiling Points

DRAWN BY:

SCALE: 1:50

DRAWING NO.: 4.2

N

ARCHITECTS:

FORUM ARCHITECTURE

892/A-2, ward no.8, khasra no. 1151/3,
Kalka Das Marg,
next to Andheria mode, Mehrauli,
New Delhi - 110030

web - www.forumarch.com
mail - studio@forumarch.com
Ph - (+91) 99104 90404 , 98116 00754