




NOTE : ~ PLEASE MAINTAIN 8 MM GAP BETWEEN TWO LIP BUSHES.

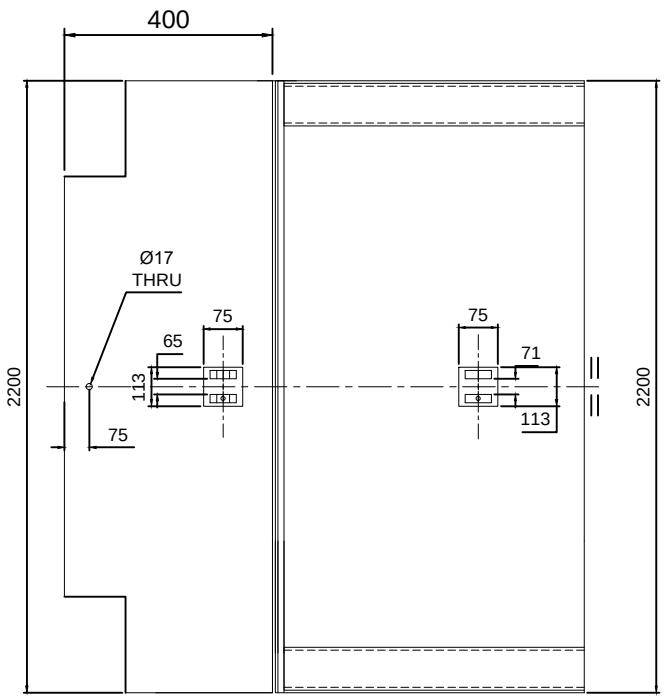

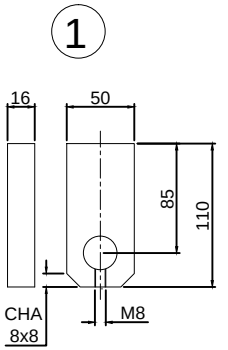

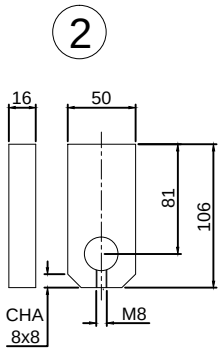

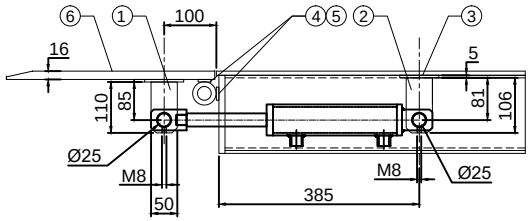

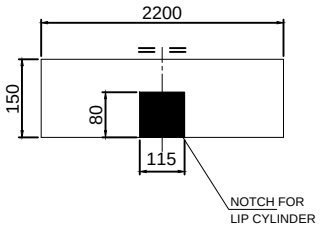

NOTE:~ MTL : MS

PART NO.	PART NAME	DESCRIPTION	QTY
1.	FLAT	50 X 16 X 113L	2 NOS
2.	FLAT	50 X 16 X 110L	2 NOS
3.	FLAT	75 X 5 X 113L	2 NOS
4.	FLAT	25 X 5 X 80L	16 NOS
5.	FLAT	25 X 5 X 50L	10 NOS
6.	PROFILE	400 X 16 X 2200L	1 NO

TOLERANCE - ±5mm

This drawing & design is the property of NIHVA TECHNOLOGIES. Not to be sold or copied to any other concern.

TITLE

LIP CYL MOUNTING

NIHVA TECHNOLOGIES PVT. LTD.
NIHVA TECHNOLOGIES PVT. LTD. PUNE
Tel : 020 66304033
Email:- info@nihva.com
Website:- www.nihva.com

	NAME	SIGN	DATE
DRAWN	PRADEEP		02.05.2018
CHECK	PRADEEP		02.05.2018
APPRD.	PRADEEP		02.05.2018

CLIENT -

PROJECT - DLIK1006

SITE LOCATION -

If any queries contact : design@nihva.com

DWG. NO. : NIHVA/18-19/DLIK1006_003

ALL DIMENSION ARE IN mm

SCALE: NTS | WT: | REV- 0