



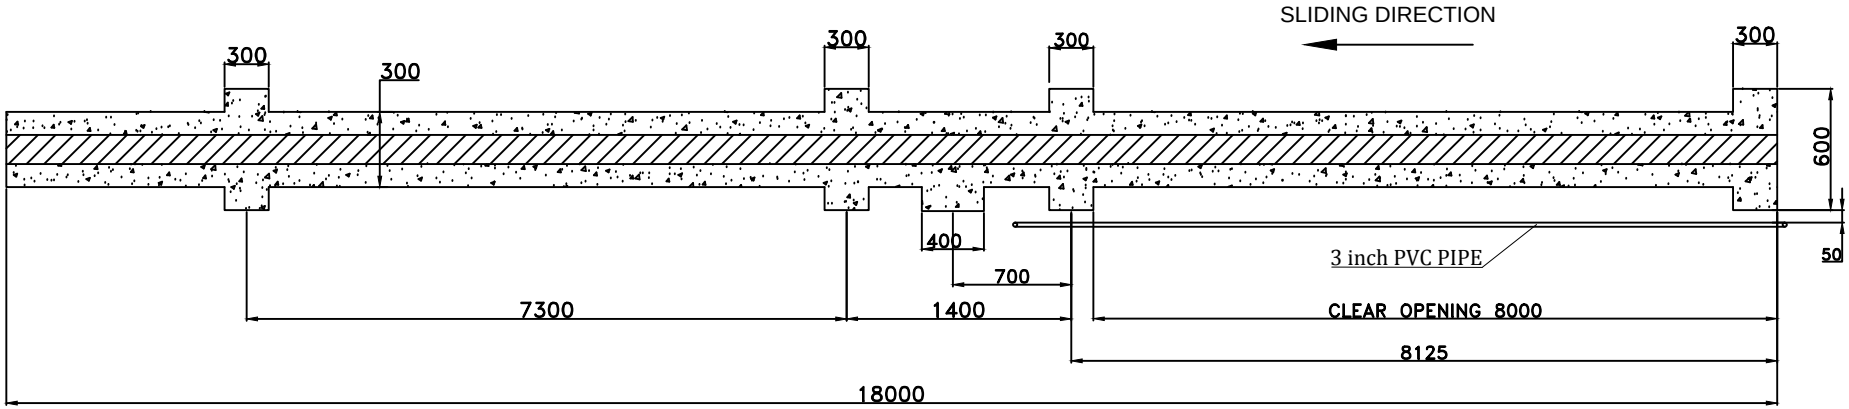

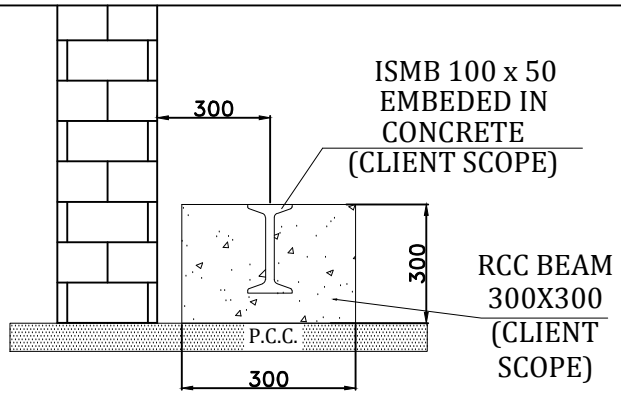

08 METER SLIDING GATE FOUNDATION

This drawing & designing is the property of NIHVA TECHNOLOGIES. Not be sold or copy to any other concern.

TITLE

SLIDING GATE FOUNDATION

CLIENT APPROVAL

ALL DIMENSION ARE IN mm

	SIGN	DATE
DRAWN	ABHIJIT	24/09/15
CHECK	ANIL	24/09/15
REV.	00	
APPRD.		
MFG		
Ref. No.		

NIHVA TECHNOLOGIES PVT. LTD.

NIHVA TECHNOLOGY PVT. LTD. PUNE
Tel : 020 66304033
Email:- info@nihva.com
Website:- www.nihva.com

CLIENT - MUKUND CONSTRUCTION

PROJECT -

SITE -BHOSARI MIDC

DWG. NO. - NIHVA/15-16/152

SCALE: 01 | WT: | SHEET: 01 OF 01

If any queries contact : projects@nihva.com