

OUTSIDE FTO PLOT
(MADC LAND)

SLIDING DIRECTION

LAND SIDE (OUTSIDE)

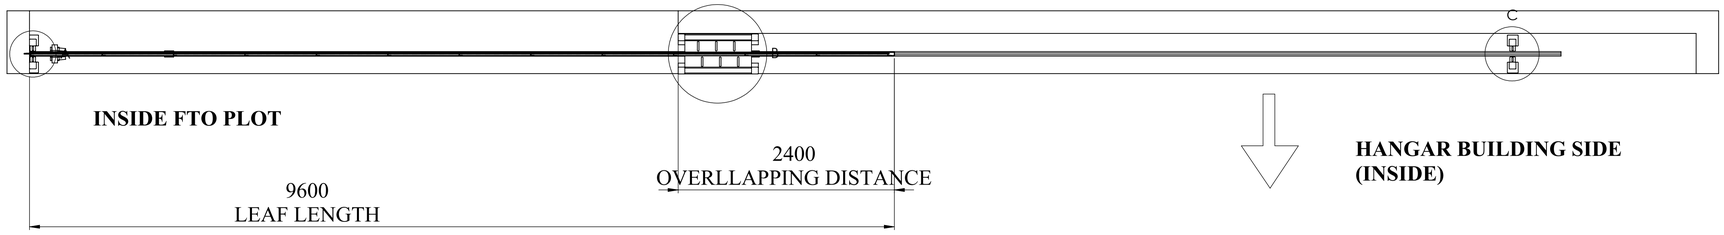



HANGAR BUILDING SIDE
(INSIDE)

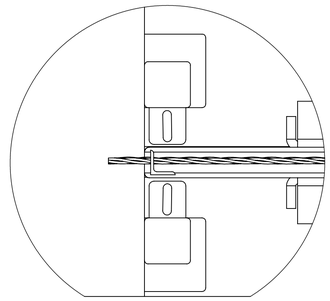

POST 1 & NYLON
ROLLER ASM


DETAIL A
SCALE 1 : 5

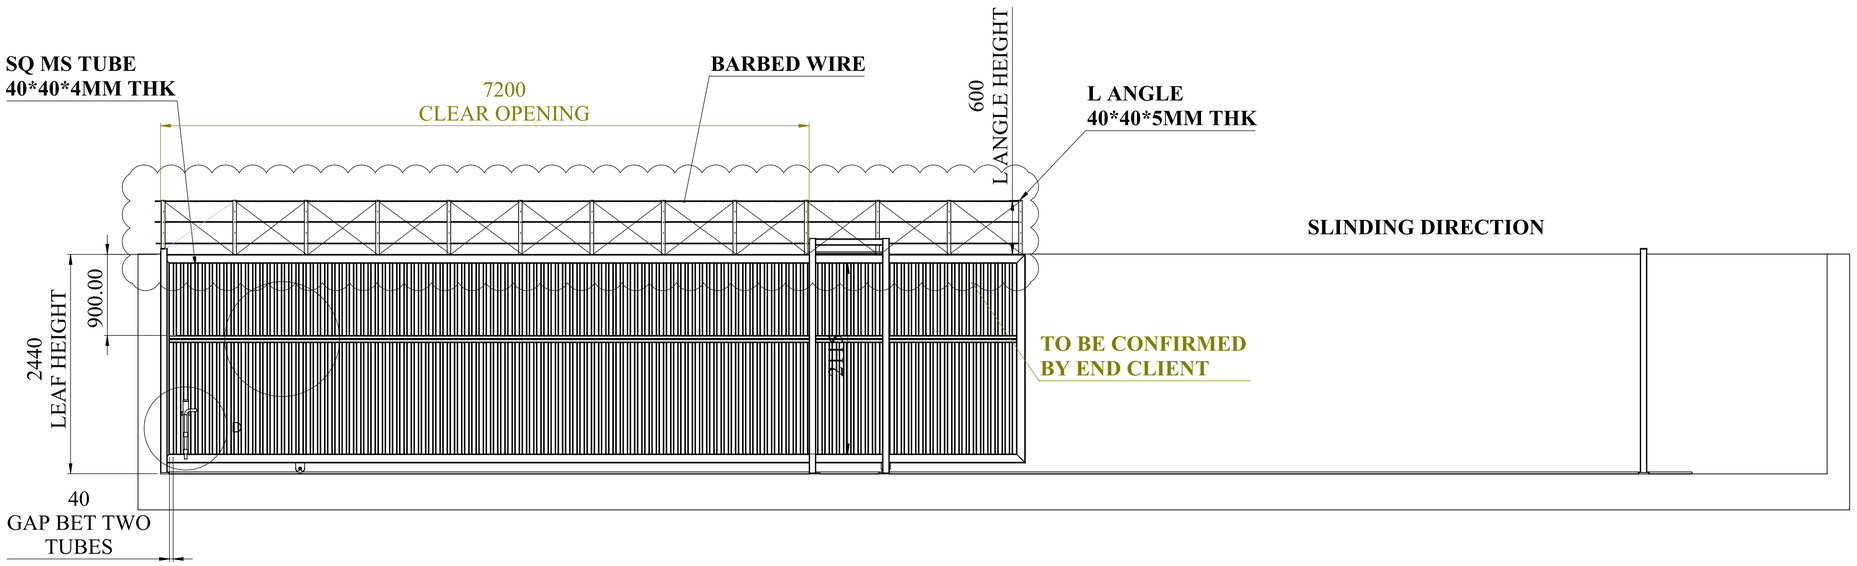

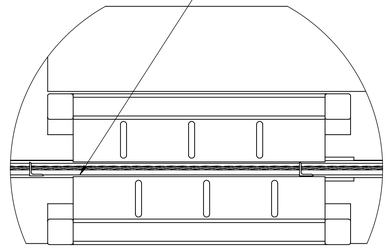


POST 2 & NYLON
ROLLER ASM

DETAIL B
SCALE 1 : 9

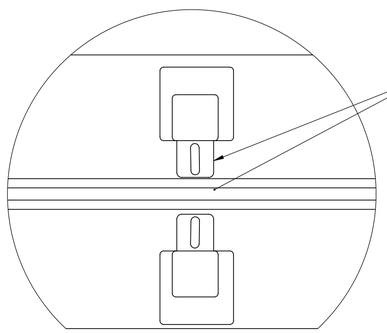


POST 3 & NYLON
ROLLER ASM

DETAIL C
SCALE 1 : 5

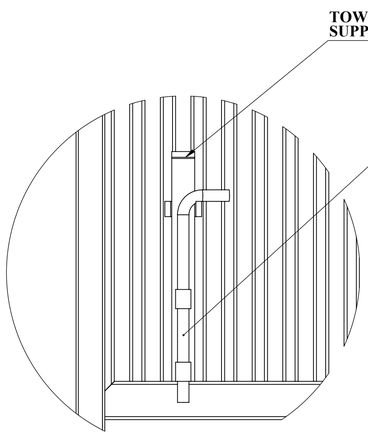

TOWER BOLT LOCKING
ARRANGEMENT

DETAIL D
SCALE 1 : 8

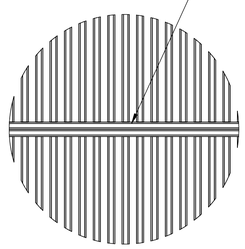

DETAIL I
SCALE 1 : 17

NOTE :

1)GA DRAWING SINGLE SLIDING GATE TYPE NO 05.
2)03 column posts when the gates is in the closed position.
3)03 column posts when the gates is in the fully open position.
4) barbed wire design is zigzag pattern.

UNLESS OTHERWISE SPECIFIED: DIMENSIONS ARE IN MILLIMETERS SURFACE FINISH: TOLERANCES: LINEAR: ANGULAR:	FINISH:		DEBURR AND BREAK SHARP EDGES	DO NOT SCALE DRAWING	REVISION
	NAME	SIGNATURE	DATE	TITLE:	
DRAWN					
CHK'D					
APPV'D					
MFG					
Q.A					
MATERIAL:				DWG NO.	
WEIGHT:				SCALE:1:100	SHEET 1 OF 1

GA DRAWING TYPE 05