


Revision		Date	By
A	Clear width was 82000	2019-03-28	KTL
B	Clear width was 80000	2019-03-29	KTL

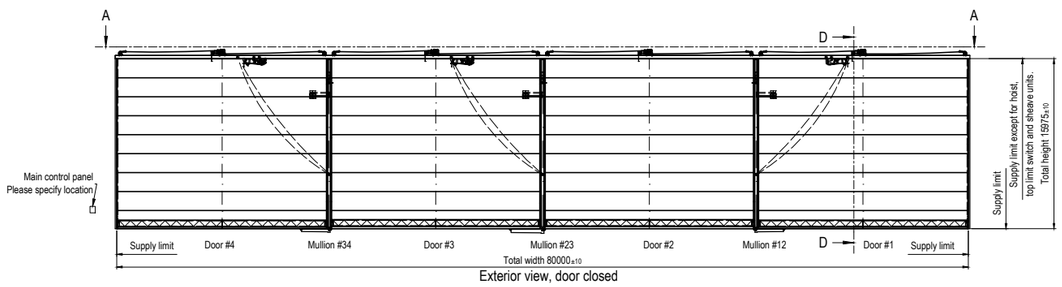


Exterior view, door closed

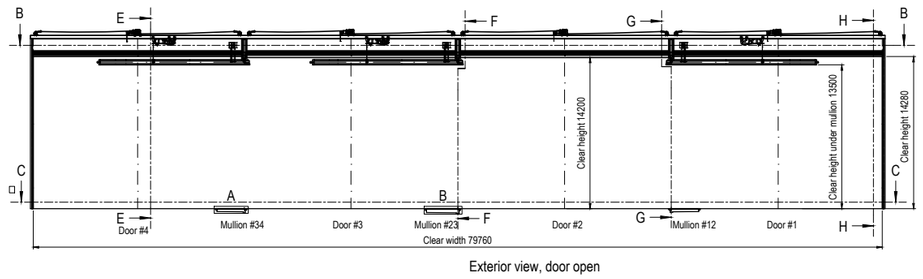


Exterior view, door open

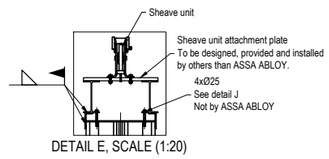


DETAIL E, SCALE (1:20)

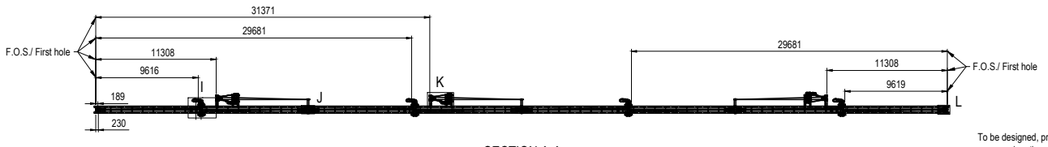


SECTION A-A

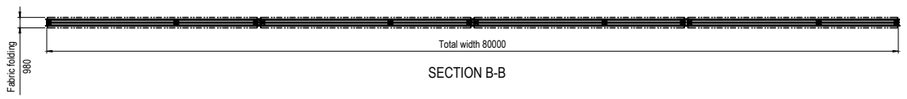


SECTION B-B

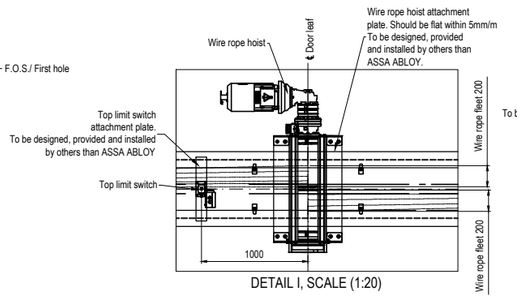


DETAIL I, SCALE (1:20)

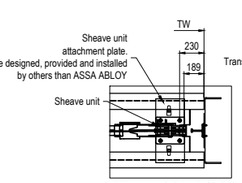

DETAIL L, SCALE (1:20)

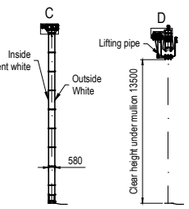


SECTION D-D

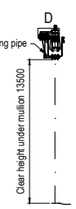


SECTION E-E




SECTION F-F

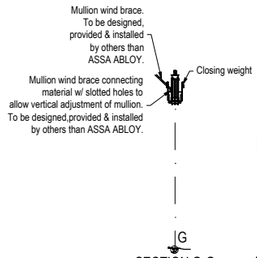


SECTION G-G

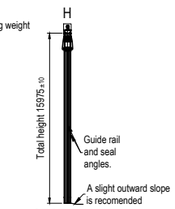


SECTION H-H

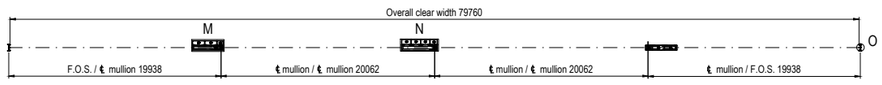


SECTION C-C

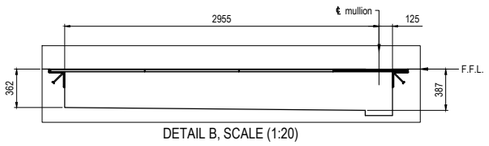


DETAIL B, SCALE (1:20)

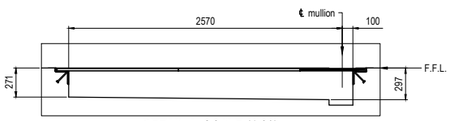


DETAIL A, SCALE (1:20)
Floor pit #12 mirrored

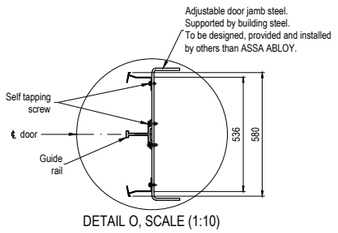


DETAIL O, SCALE (1:10)

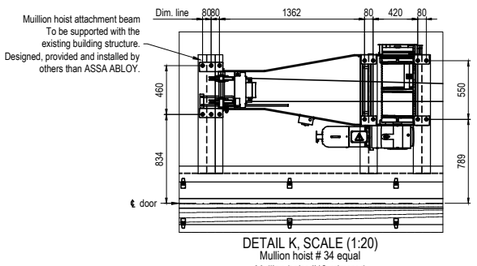


DETAIL K, SCALE (1:20)
Mullion hoist # 34 equal
Mullion hoist #12 mirrored

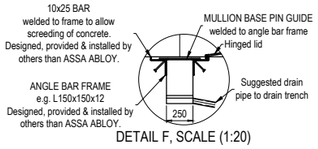


DETAIL F, SCALE (1:20)

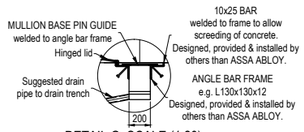


DETAIL G, SCALE (1:20)

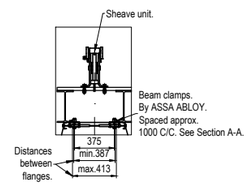


DETAIL H, SCALE (1:20)
@ all doors

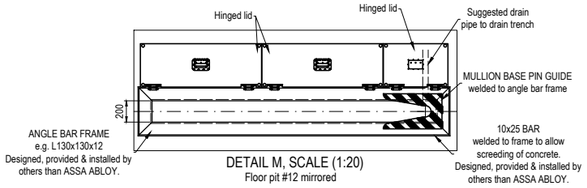


DETAIL M, SCALE (1:20)
Floor pit #12 mirrored

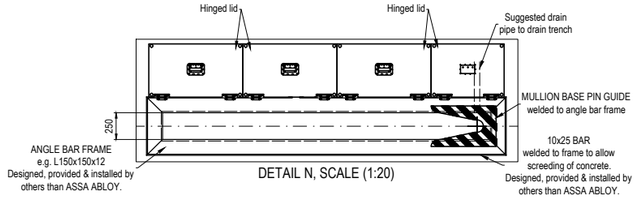

DETAIL N, SCALE (1:20)

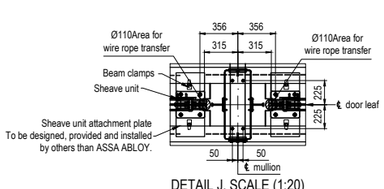


DETAIL J, SCALE (1:20)
@ all mullions

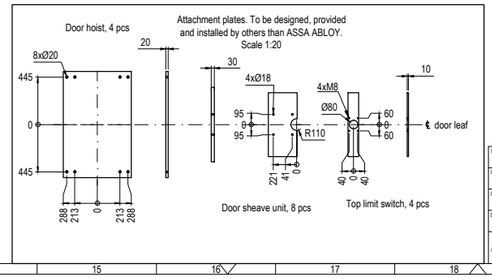



DETAIL D, SCALE (1:20)

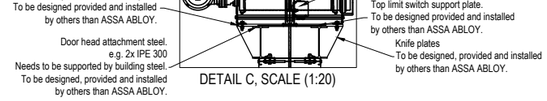

DETAIL C, SCALE (1:20)

DOOR IDENTITY NUMBER: 84247001

LOAD DIAGRAM & NOTES, ref. to drwng. no. 65846

DESIGNED: PL	SIZE: A1F	SCALE: 1:200	
CODE: 84247	If not otherwise stated: Tolerances ISO 2768-m EN ISO 13920-B Cutting class ISO 9013-442 Weld class ISO 5817-C Surface finish Smooth raw surface		
ITEM NO			
DATE: 2018-02-21			

Indamer
India
Megadoor 79760 x 14200/13500
Interface

ASSA ABLOY

DRAWING NO: 65845

REVISION: B

PLOT DATE

The concept, the content of ASSA ABLOY Entrance Systems AB and shall not be disclosed or wholly permitted to copied, imported in a third party or used for any other unauthorized purpose.