
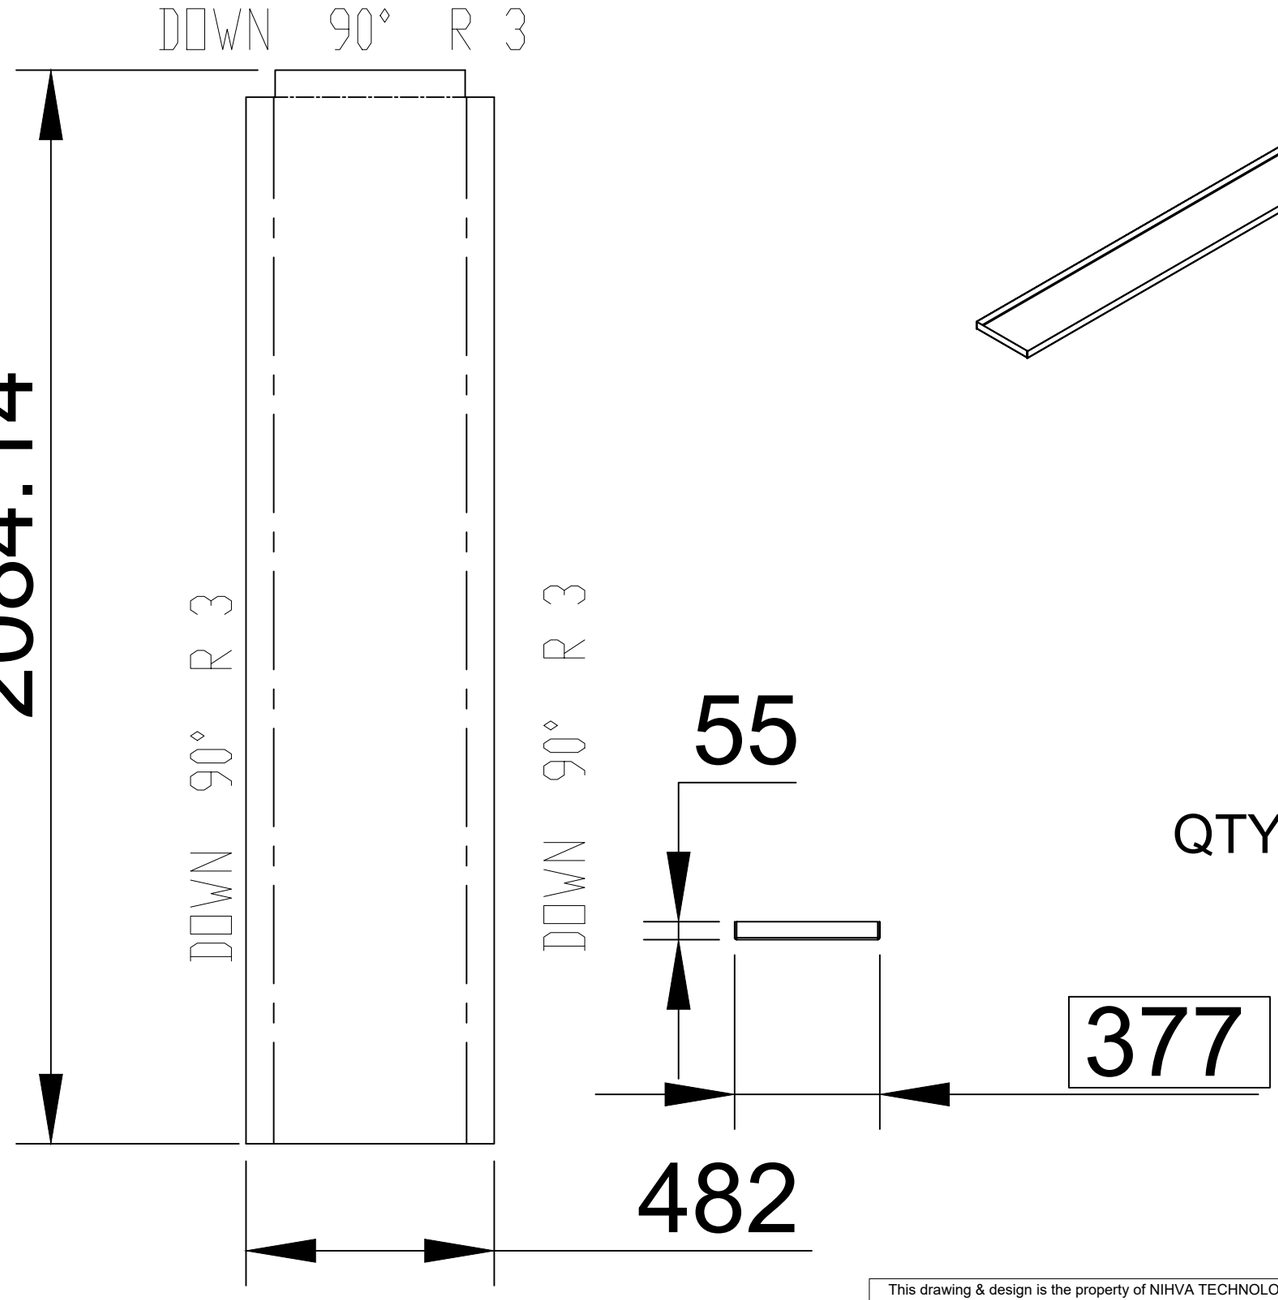


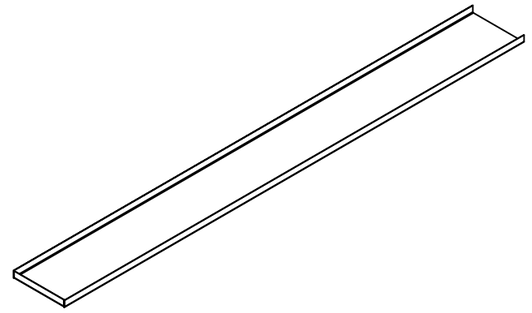

QTY:02 NOS

This drawing & design is the property of NIHVA TECHNOLOGIES. Not to be sold or copied to any other concern.

3 LEAF RIGHT SIDE CRM DOOR 03			NIHVA TECHNOLOGIES PVT. LTD.
	NAME	DATE	
DRAWN	M.SUTAR	16/06/2022	CLIENT - NIHVA TECHNOLOGIES PVT LTD
CHECK	M.SUTAR	16/06/2022	LOCATION -
APPRD.	V.TARAK	16/06/2022	PRODUCT - SLIDING DOOR
If any queries contact : design@nihva.com			DWG NO:-NIHVA/22-23/CLT/
ALL DIMENSION ARE IN mm			SCALE: NTS / SCALE:-- 1:1 / SHEET:

NIHVA TECHNOLOGIES PVT. LTD. PUNE
Tel : 020 66304033
Email:- info@nihva.com
Website:- www.nihva.com

Rev No.	Revision	Date	Revised By

