

PRODUCED BY AN AUTODESK EDUCATIONAL PRODUCT

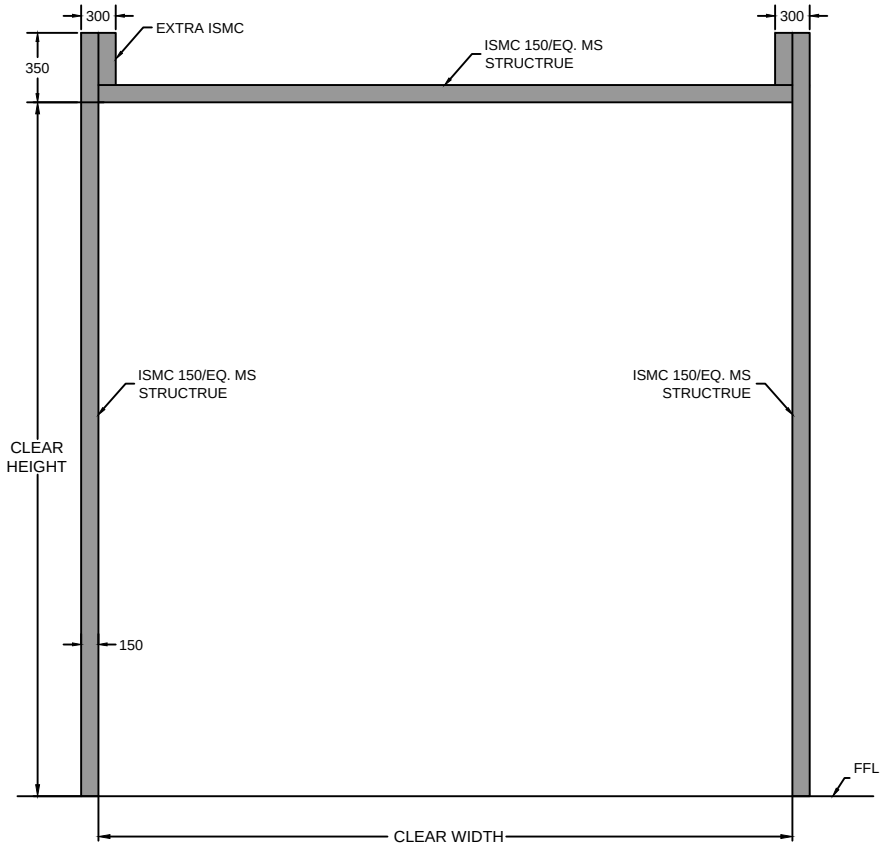

INSIDE ELEVATION

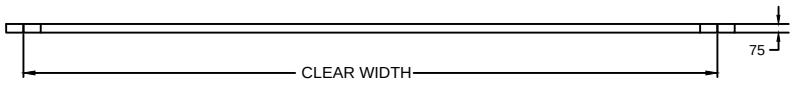

PLAN

SR NO.	CLEAR WIDTH	CLEAR HEIGHT	QUANTITY
1	2420 mm	2300 mm	01

TOLERANCE - ±10mm

This drawing & design is the property of NIHVA TECHNOLOGIES. Not to be sold or copied to any other concern.

TITLE: MS STRUCTURE FOR SECTIONAL DOOR LL

NIHVA TECHNOLOGIES PVT. LTD.
NIHVA TECHNOLOGIES PVT. LTD. PUNE
Tel : 020 66304033
Email:- info@nihva.com
Website:- www.nihva.com

	NAME	SIGN	DATE
DRAWN	P.A		10.02.2020
CHECK	G.J		10.02.2020
APPRD.			

CLIENT - R.P TECH

PROJECT -

SITE LOCATION - PUNE

If any queries contact : design@nihva.com

DWG. NO. : NIHVA/19-20/ REV- 0

ALL DIMENSION ARE IN mm

SCALE: NTS WT: SHEET: 01 OF 01