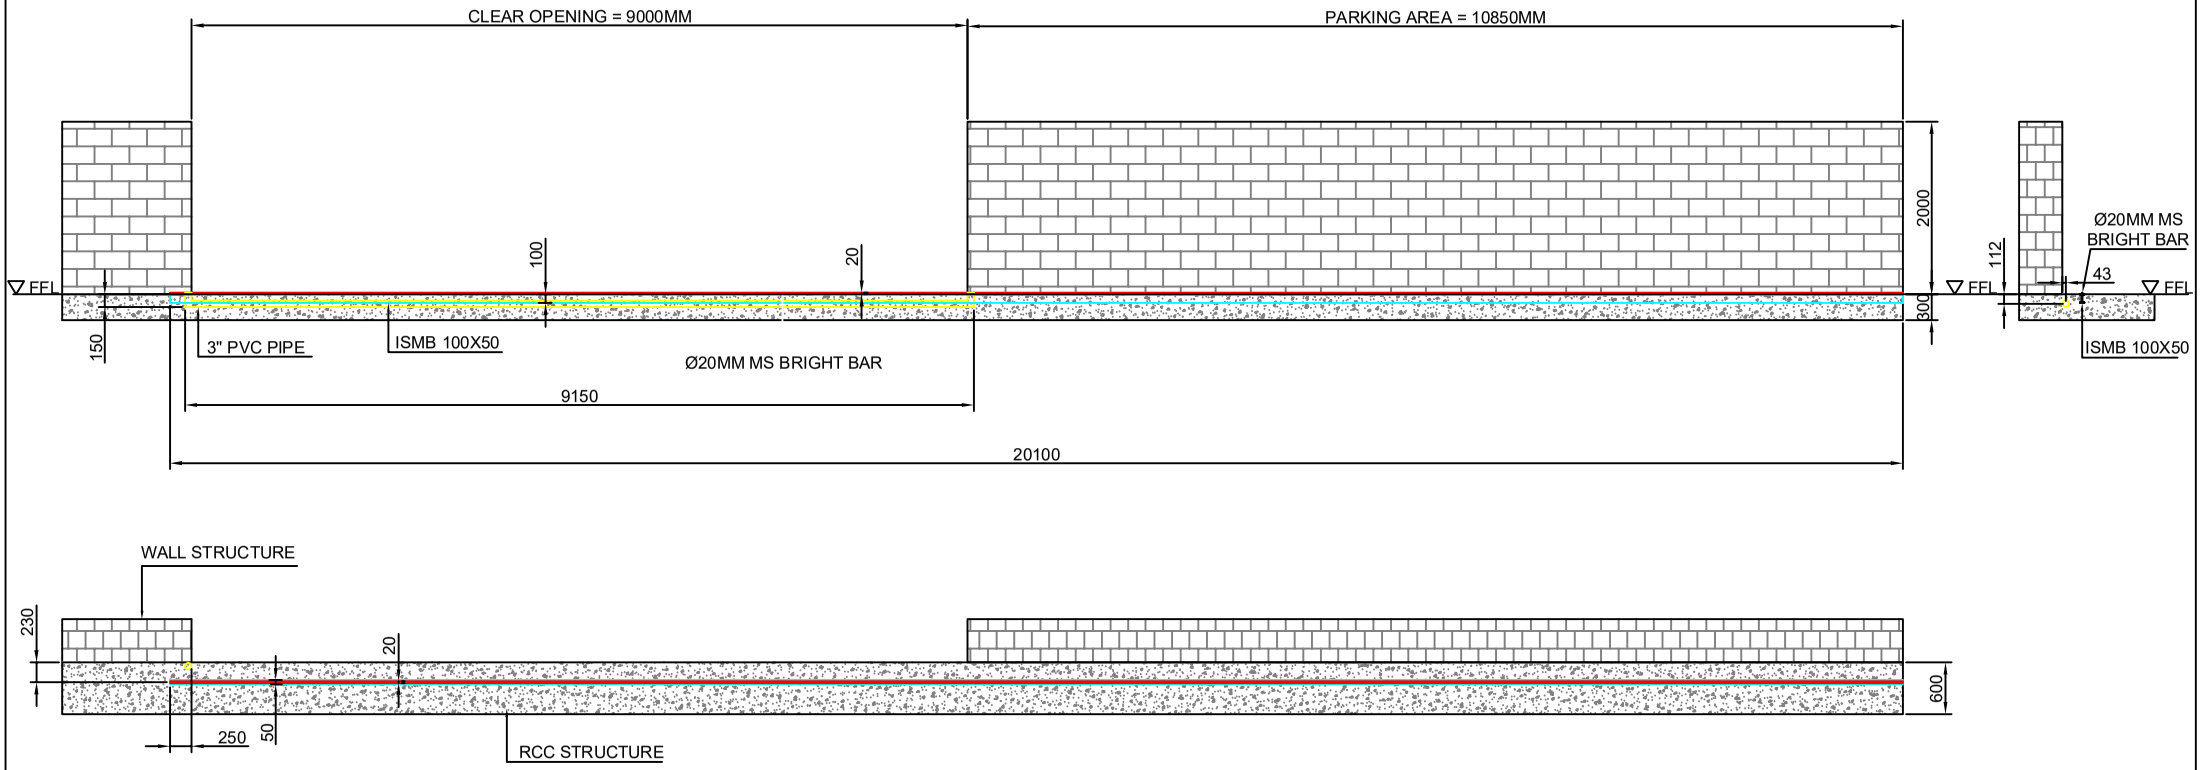


Technical Specs of Motorized Sliding Gate

1. Parking length required -10750+100mm
2. Bottom Rail - Bright bar Ø20mm
3. Total leaf weight ≈ Approx.1134kg
4. ISMB 100 X 50 positioned in the foundation.

Note-

1. All dimension are in mm.
2. All civil work is under client scope.
3. 3" PVC pipe in the foundation to be provided by client.
4. Power supply single phase 230v, 50hz. is in client scope.
5. Cable for power supply 2.5 sqmm 3 core
6. Cable for photocell - 1.5 sqmm 4 core

This drawing & design is the property of NIHVA TECHNOLOGIES. Not to be sold or copied to any other concern.

TITLE:- Foundation Drawing for Sliding Gate				NIHVA TECHNOLOGIES PVT. LTD. PUNE Tel : 020 66304033 Email:- info@nihva.com Website:- www.nihva.com
	NAME	DATE	SIGN	
DRAWN	SUJATA.B	22/10/2021		CLIENT - SCON PROJECTS
CHECK	G.PATIL	22/10/2021		LOCATION -
APPRD.	A.KURHADE	22/10/2021		PRODUCT - SLIDING GATE QTY:-
If any queries contact : design@nihva.com				DWG NO:-NIHVA\21-22\0250 REV- 0
ALL DIMENSION ARE IN mm				SCALE: NTS SCALE:-- 1:1 SHEET: 01 OF 01

Rev No.	Revision	Date	Revised By