
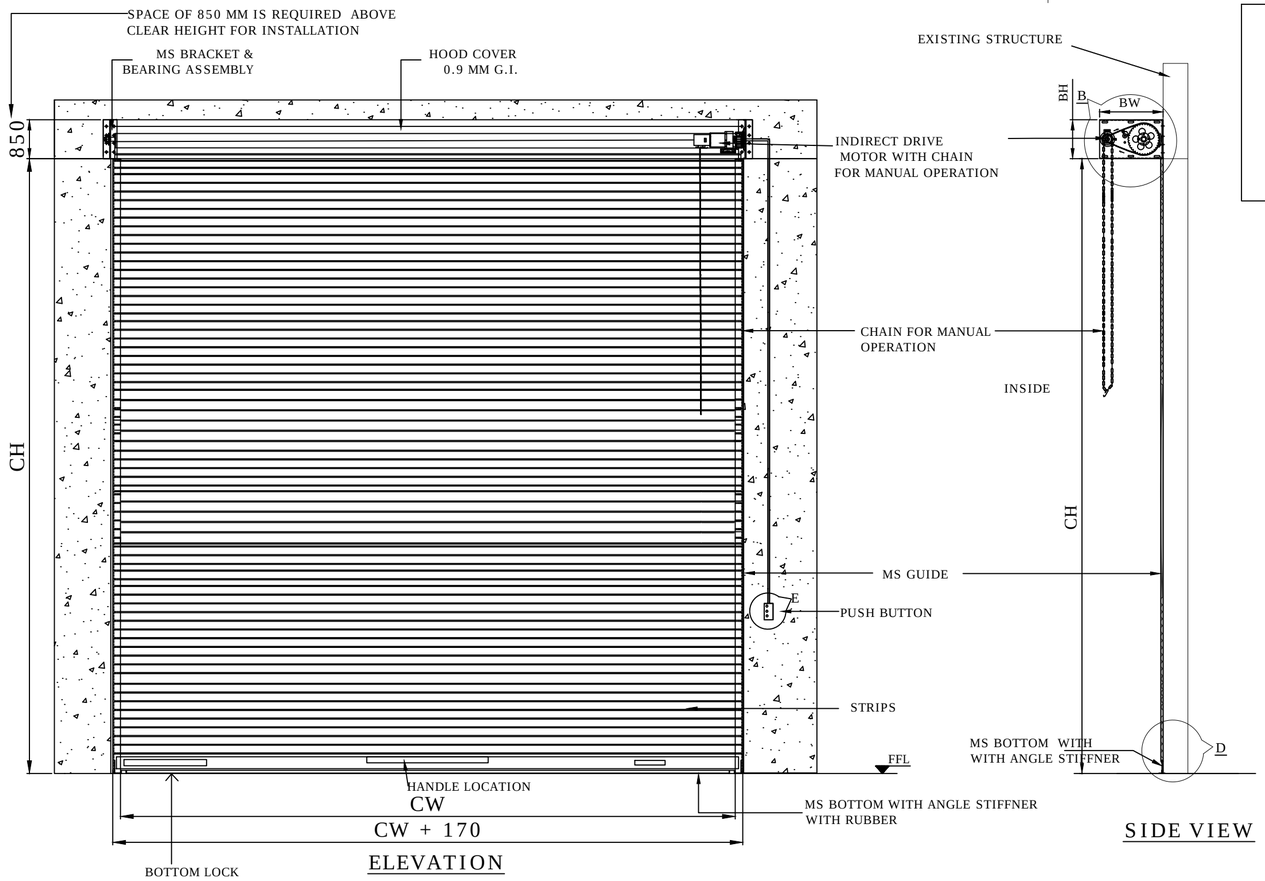



NOTE:

1. REQUIRED MS STRUCTURE , FITTING & ALL CIVIL WORK IS IN CLIENT SCOPE.
2. SPACE OF 850 MM IS REQUIRED ABOVE CLEAR HEIGHT FOR ROLLING SHUTTER INSTALLATION .
3. KINDLY CONFIRM RAL SHADE , MOUNTING SURFACE & INSTALLATION LOCATION (INSIDE/OUTSIDE).

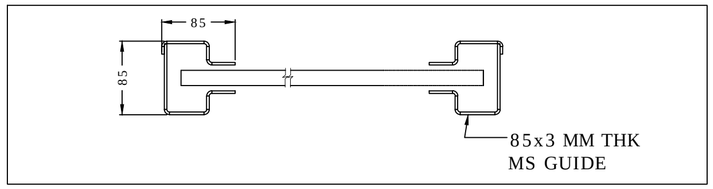


SR NO	PARAMETER	DESCRIPTION	CUSTOMER REMARK
1	SHUTTER MOUNTING	ON STRUCTURE / ON CONCRETE	
2	SURFACE FINISH	RAL CODE FOR POWDER COATING	
3	INSTALLATION LOCATION	INSIDE / OUTSIDE	


RAL CODE	SHADE	COLOUR
RAL 9001	CREAM	
RAL 9002	GREY WHITE	
RAL 9010	PURE WHITE	
RAL 5002	ULTRAMARINE BLUE	
RAL 7035	LIGHT GREY	
RAL 7001	SILVER GREY	

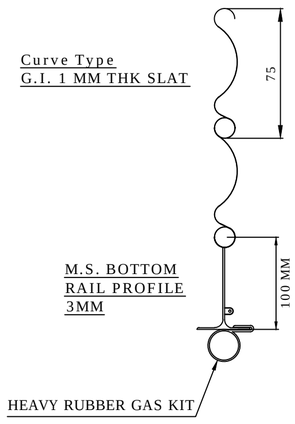

DETAILS : D

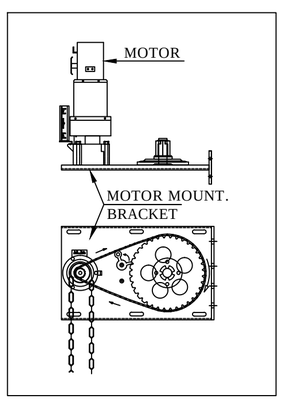

DETAILS : A & B

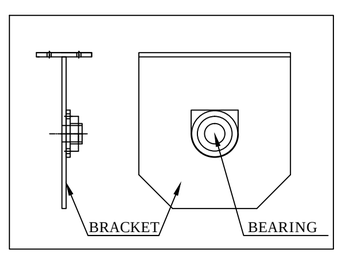

DETAILS : C

4000	5000		
4000	4000		
3700	4000		
CLEAR WIDTH (CW)	CLEAR HEIGHT (CH)	QUANTITY	RAL COLOR POWDER COATED

This drawing & design is the property of NIHVA TECHNOLOGIES. Not to be sold or copied to any other concern.

TITLE GI MOTORIZED INDIRECT DRIVE ROLLING SHUTTER

	NAME	SIGN	DATE
DRAWN	S.M.S.		16.3.2021
CHECK	S.M.S.		16.3.2021
APPRD.			

NIHVA TECHNOLOGIES PVT. LTD.
NIHVA TECHNOLOGIES PVT. PUNE
Tel : 020 66304033
Email:- info@nihva.com
Website:- www.nihva.com

CLIENT - ARP CONSTRUCTION

PROJECT - ARP CONSTRUCTION

SITE LOCATION -

If any queries contact : projectsupport@nihva.com

DWG. NO. : NIHVA/20-21/0082 REV- R00

ALL DIMENSION ARE IN mm

SCALE: NTS WT: SHEET: