

Abbrevation's:
WOW-Wall Opening Width
WOH-Wall Opening Height
UC-Under Cut
FFL-Finished Floor Level

ASSESORIES DETALES

(a) HINGES: SS Ball bearing butt hinges size 100x75x3mm

(b) LOCK : Mortise Dead lock,Cylinder(Both side key) with Escutcheon (ALTOS make) with 3 keys.

(c) DOOR CLOSER : TS 68 Dorma make

(d) HANDLE : D Handle one side & push plate(125x325x1.2mm) on other side


(e) CONCEALED FLUSH BOLT

(f) SS Kick plate from push side.

(g) Auto drop seal.

Shutter thickness : 47 mm
Frame Sheet thick : 1.2mm
Shutter sheet thick :0.8mm
Fixing : On Solid Brick plastered wall with Anchors
Electrostatic powder coated


NOTE:- *All Dimensions are in mm.
*Tolerance:-All Linear Dimensions ±3mm,Others ±0.5mm.
*The Drawing Is For Location of Hardware only. Drawing Does Not Represent The Hardware For More Clarity, Please Go Through Hardware Broucher.

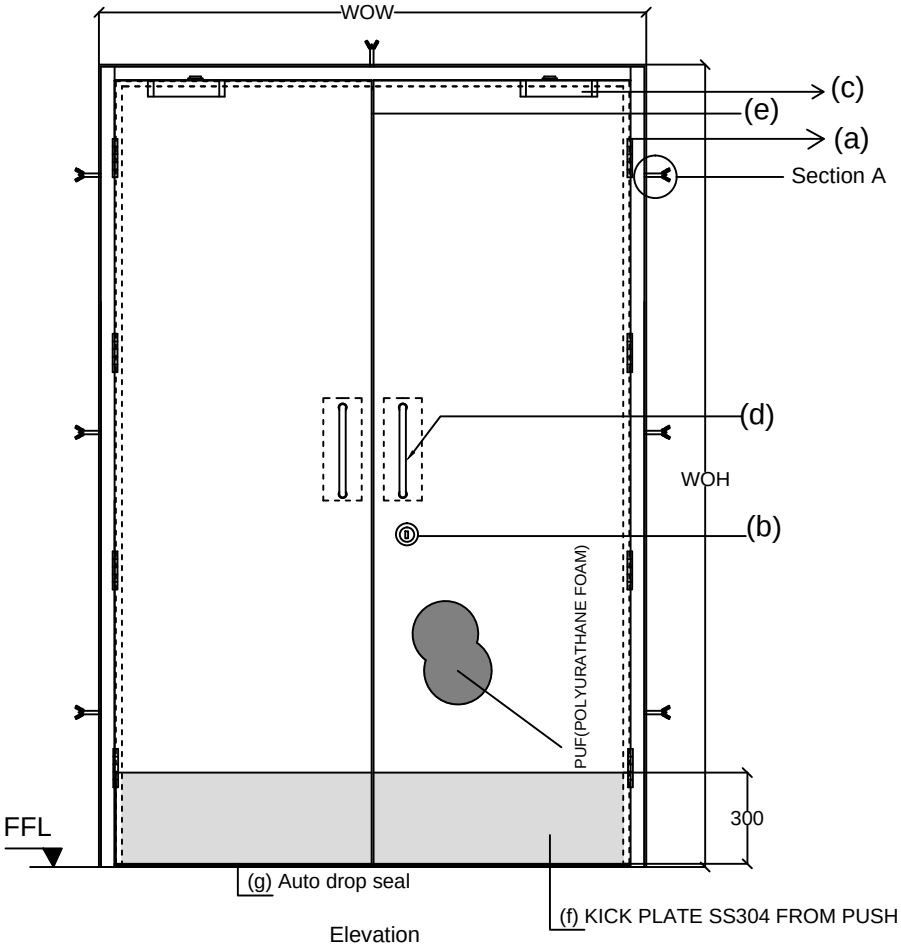

Elevation



Top View

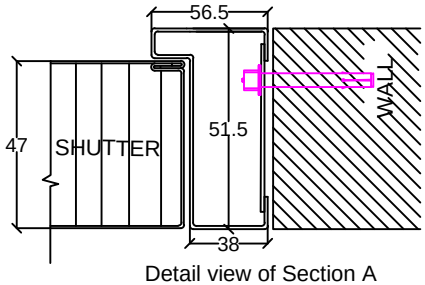

Detail view of Section A

Steel door size

WOW	WOH	TYPE 5	TYPE 6	TYPE 7	TYPE 8	QUANTITY
1500	2200					22
2400	2200					1

NOTE- CLIENT SHOULD SELECT DOOR TYPE FROM DOOR HANDLING SHEET.

COLOR- RAL 5015

This drawing & designing is the property of NIHVA TECHNOLOGIES. Not be sold or copy to any other concern.

STEEL DOOR (DOUBLE LEAF)

CLIENT APPROVAL

ALL DIMENSION ARE IN mm

	NAME	DATE	SIGN.
DRAWN	OMKAR	09/02/17	
CHECK	SAGAR P.	09/02/17	
REV.	1		
APPRD.	R.K.	09/02/17	
MFG			

NIHVA TECHNOLOGIES PVT. LTD.
NIHVA TECHNOLOGY PVT. LTD. PUNE
Tel : 020 66304033
Email:- info@nihva.com
Website:-www.nihva.com

CLIENT - ZAMIL STEEL BUILDINGS INDIA PVT.LTD.
PROJECT -
SITE -
DWG. NO. - NIHVA/16-17/0119/R01
SCALE:NTS | WT: | SHEET: 01 OF 01
If any queries contact : projects@nihva.com