
NOTE:

1) FINISHED FLOOR TO RCC SLAB CEILING HEIGHT IS 111 " (2820 mm)
2) FINISHED FLOOR TO DOOR & WINDOWS LINTEL HEIGHT IS 7'2" (2150 mm)
3) FINISHED FLOOR TO WINDOWS SILL HEIGHT IS 30" (750 mm)
4) FINAL DIMENSIONS SHOULD BE CROSS CHECKED AT SITE BEFORE MANUFACTURING MODULAR FURNITURE

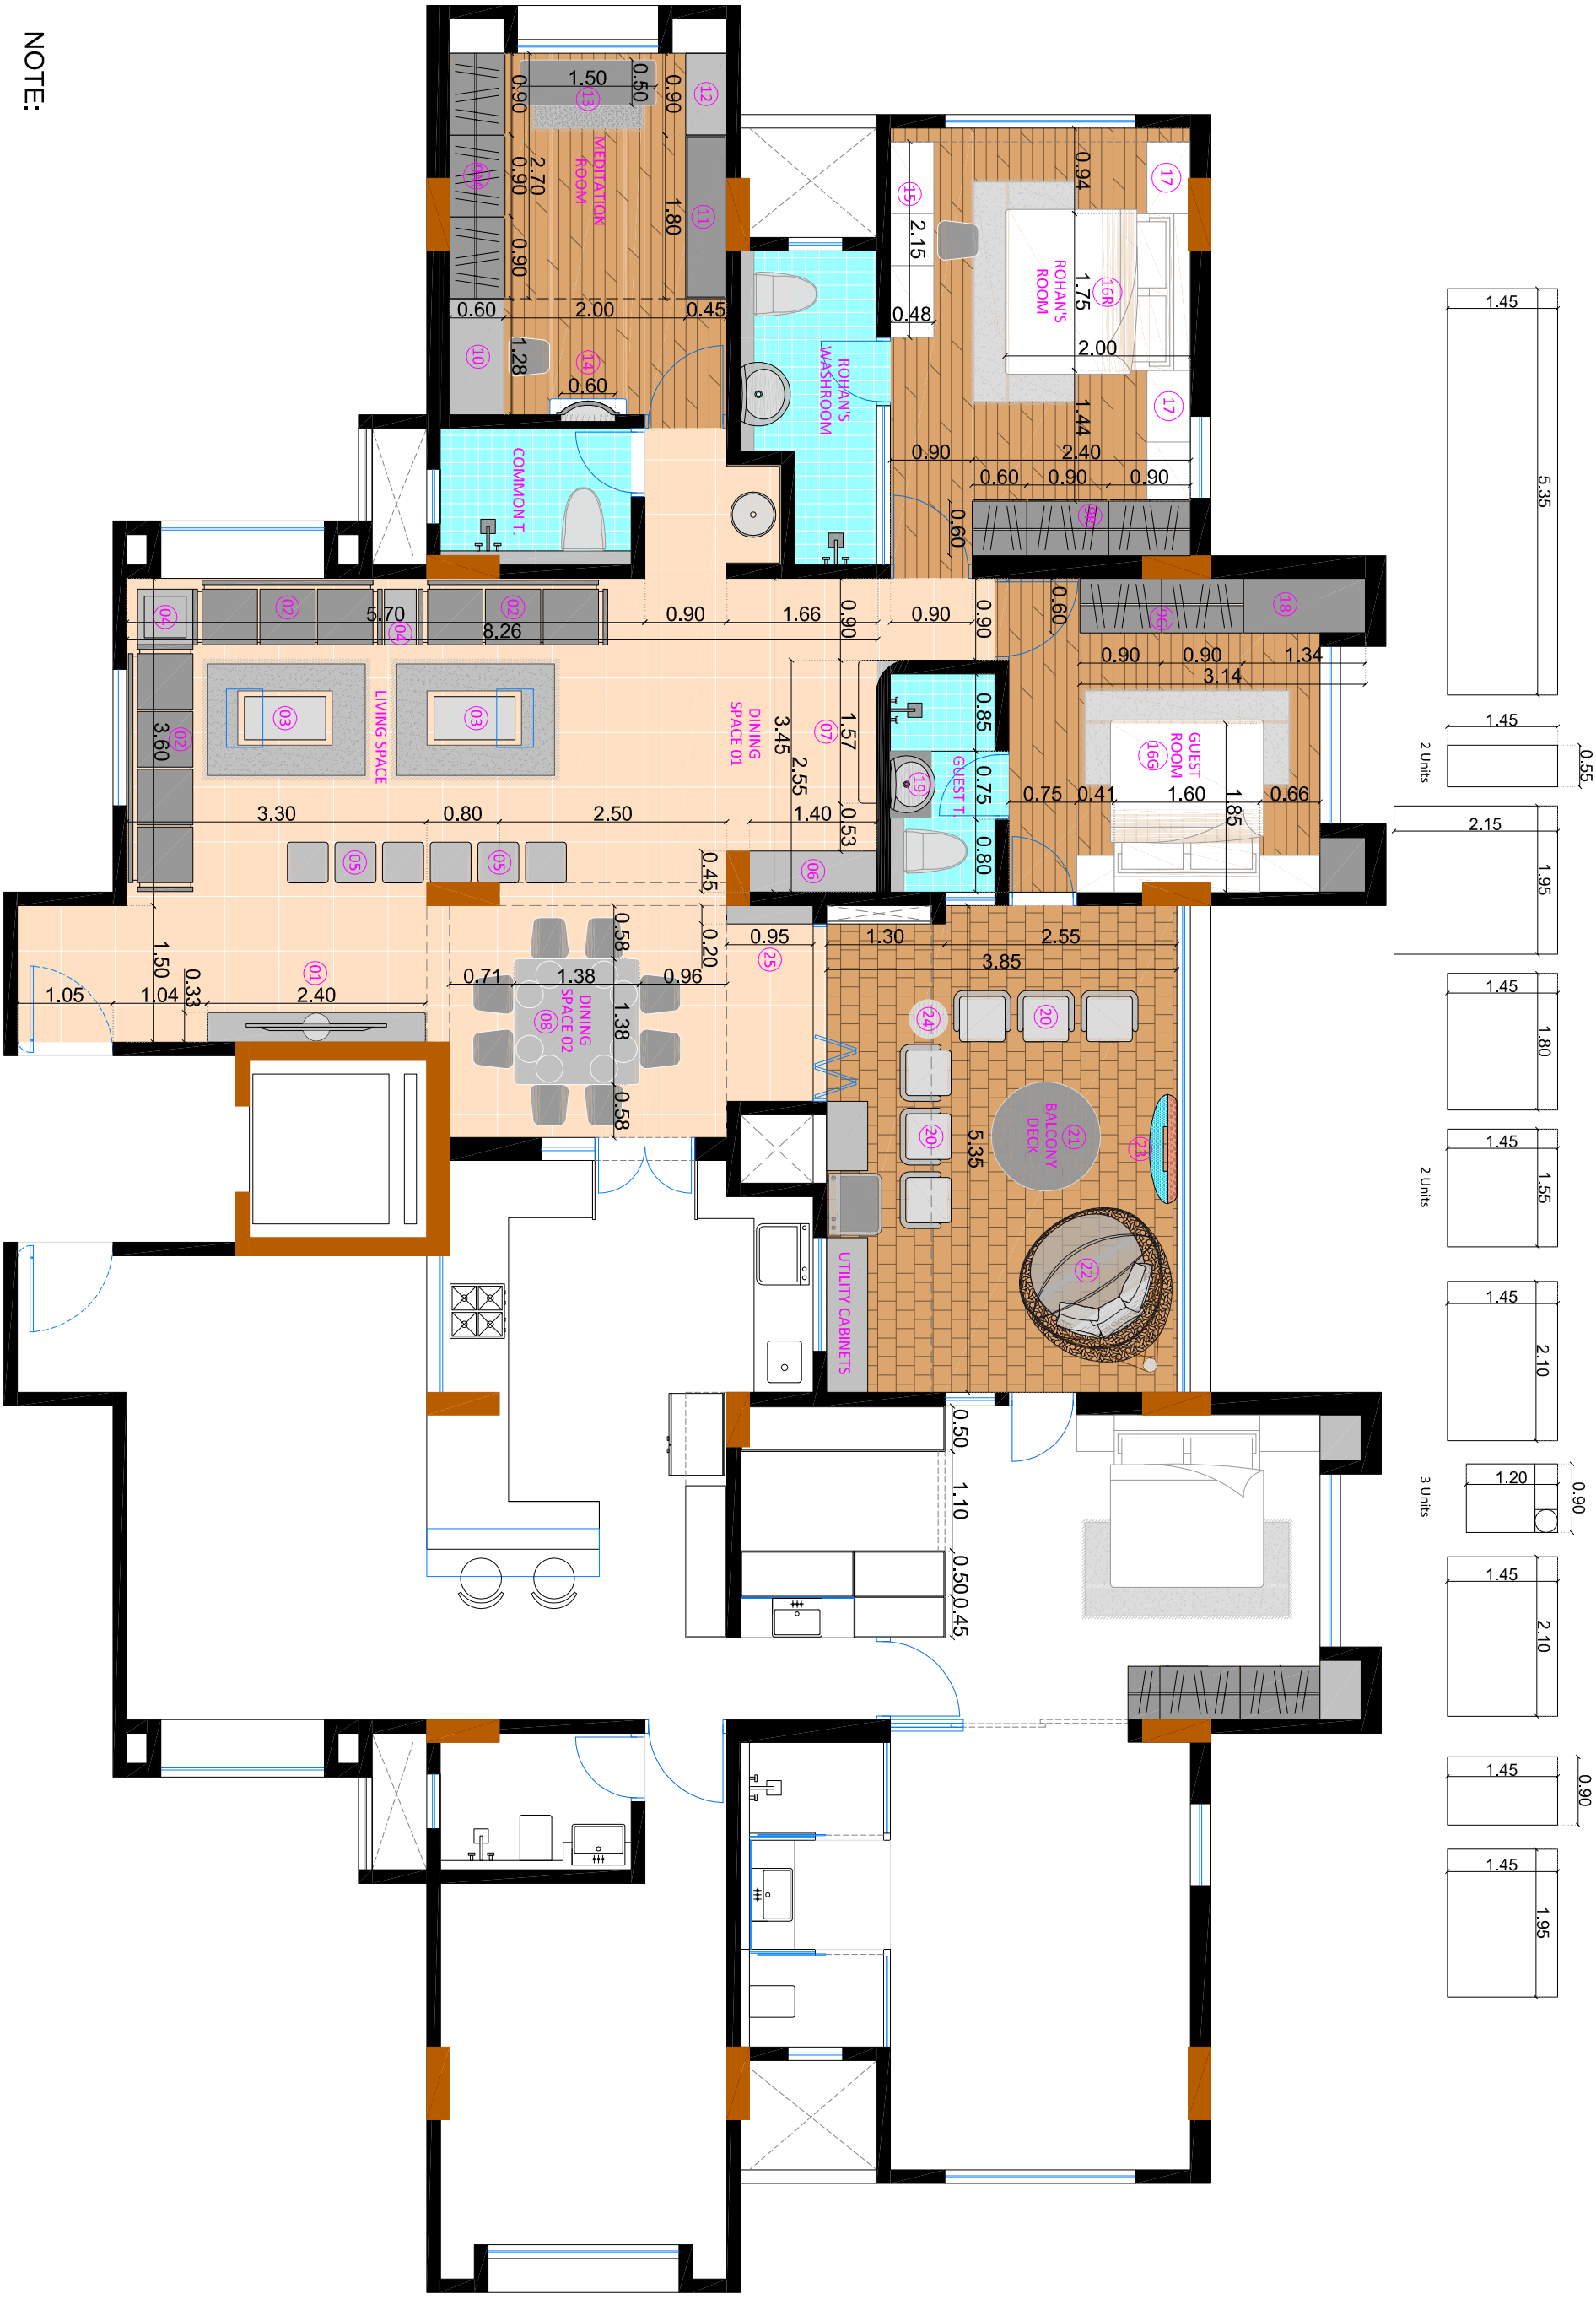

R15_01

FLOOR LAYOUT PLAN - R15

RENOVATION DESIGN PROPOSAL OF C23 & C24 APARTMENT AT BANNER, PUNE.

NORTH

design studio
Architecture | Interior Design
Ar. Piyush Parekh
7, 4th Floor, Smruti Arcade, Gangadham - Bibwewadi Road, Pune-37
zdesignstudio09@gmail.com | +91-9325851004