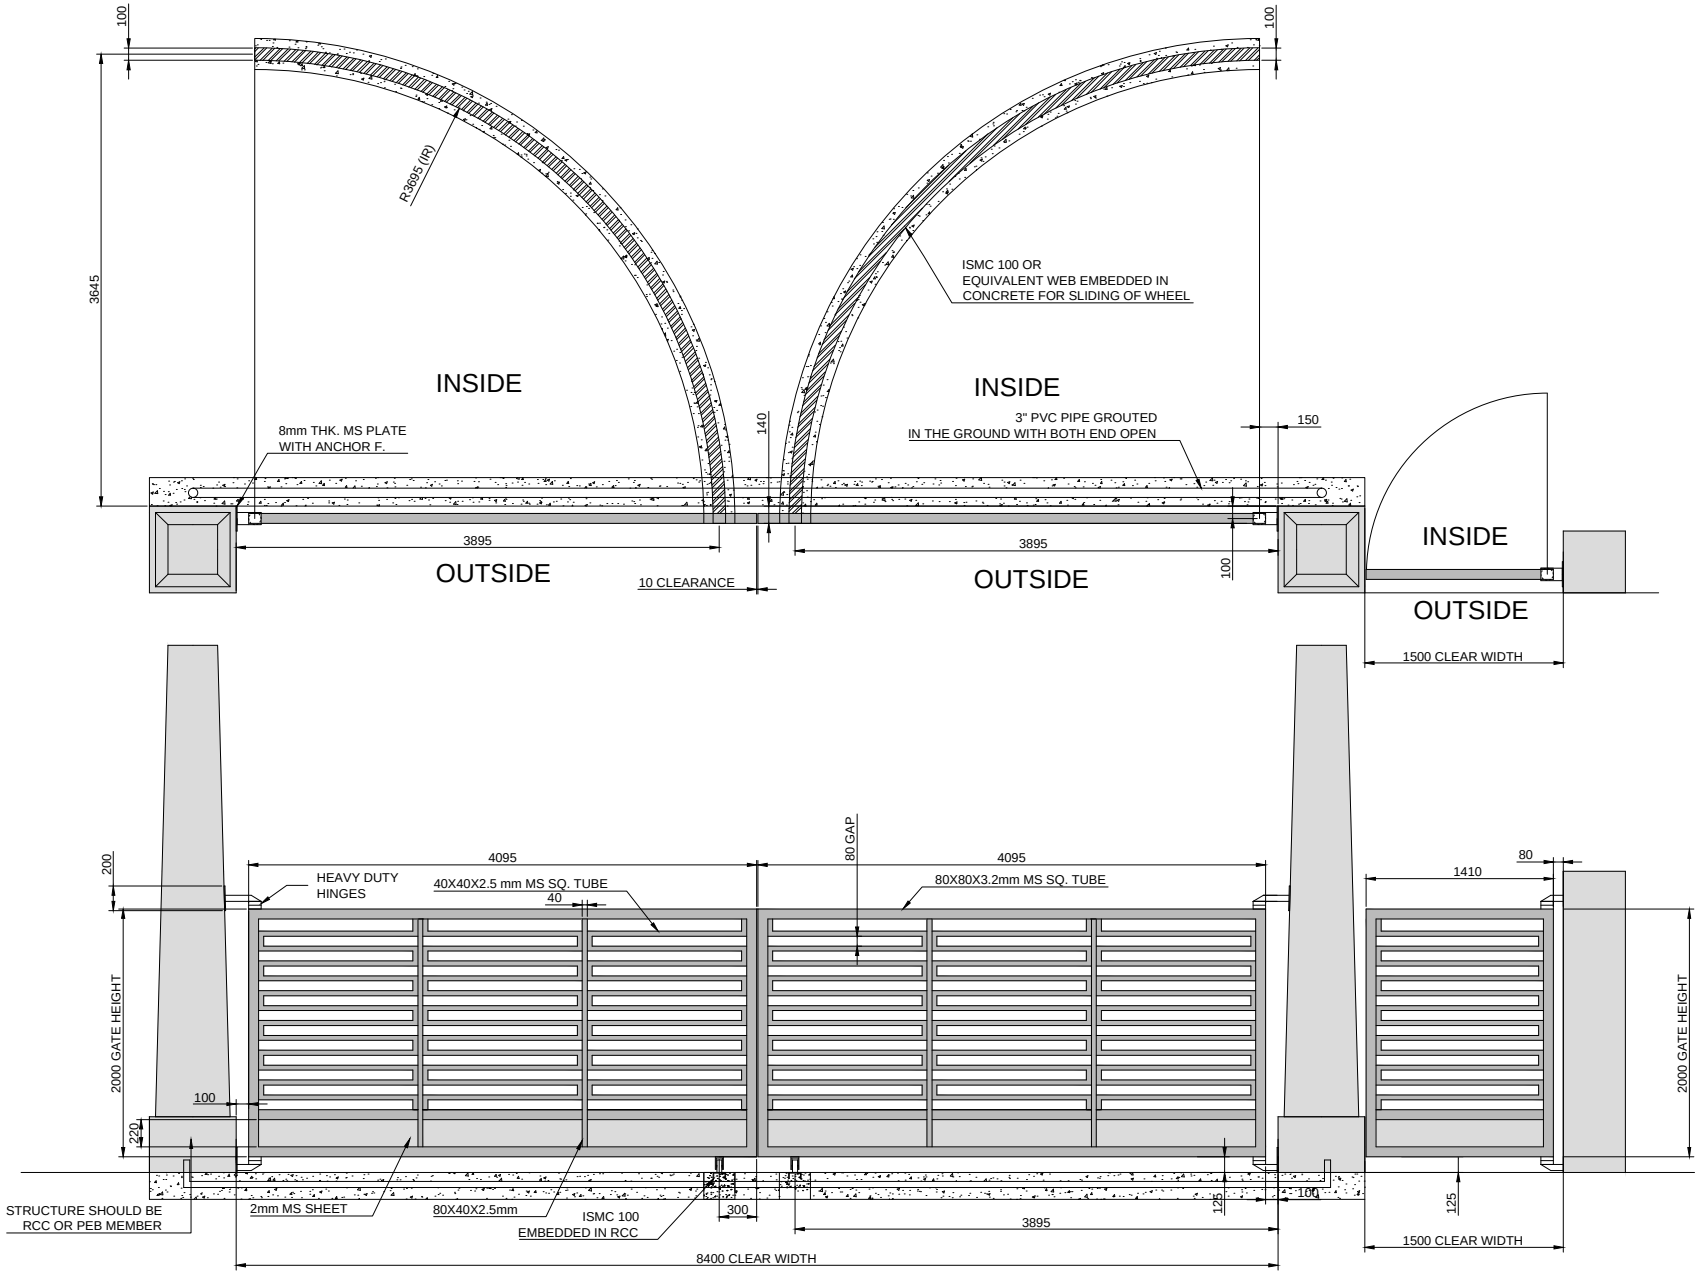

OUTSIDE ELEVATION

DIMENSION :

CLEAR WIDTH	CLEAR HEIGHT	QUANTITY
8400 mm	2000 mm	01 NOS.
1500 mm	2000 mm	01 NOS.

MATERIAL :

THICKNESS :

MODIFICATIONS DONE:-

1.GATE SHIFTED TOWARD INSIDE FOR UPGRADE TO AUTOMATIC SWING DOOR IN FUTURE.

2. 3 INCH PVC PIPE SHOULD BE PROVIDED IN GROUND FOR INTEGRATION OF SWING DOOR.

NIHVA TECHNOLOGIES PVT. LTD.

NIHVA TECHNOLOGY
PVT. LTD. PUNE
Email:- info@nihva.com
Website:- www.nihva.com

TITLE:

MANUAL SWING GATE & WICKET GATE

CLIENT'S APPROVAL :

CLIENT - LUPIN LIMITED

PROJECT -

SITE LOCATION - SIKKIM

DWG. NO. : NIHVA/16-17/0098/R02

SCALE: 1:1	WT:	SHEET:1 OF 1

DRAWN BY: OMKAR	DATE: 08-11-2016
CHECK : ANIL	DATE: 08-11-2016

If any queries contact : projects@nihva.com

NOTE: ALL DIMENSION ARE IN mm

THIS DRAWING & DESIGNING IS THE PROPERTY OF NIHVA TECHNOLOGIES. NOT BE SOLD OR COPY TO ANY OTHER CONCERN.