


DRAWING



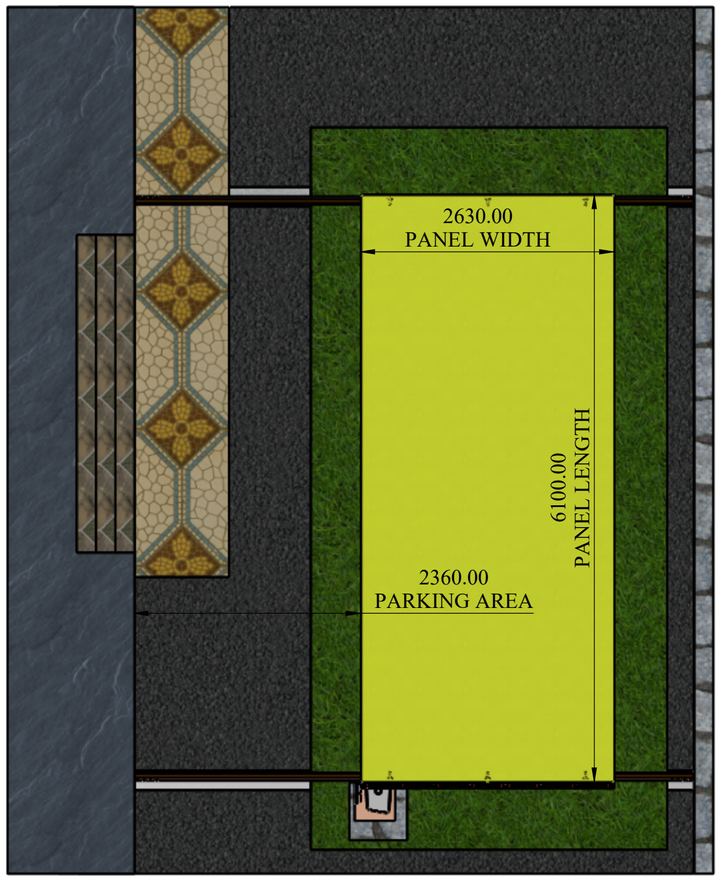


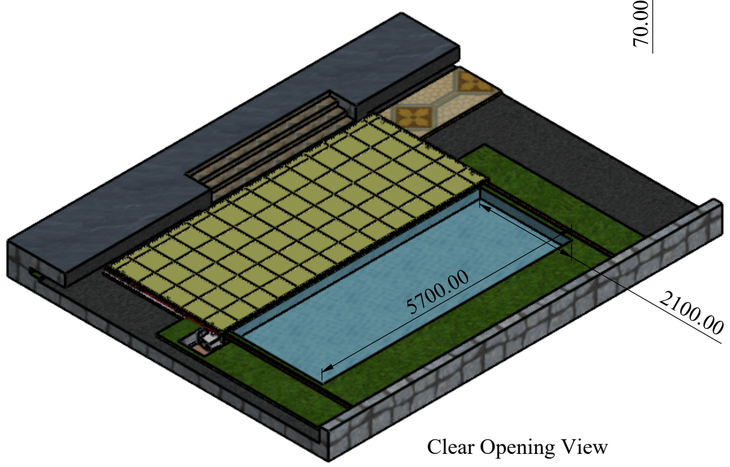


Clear Opening View

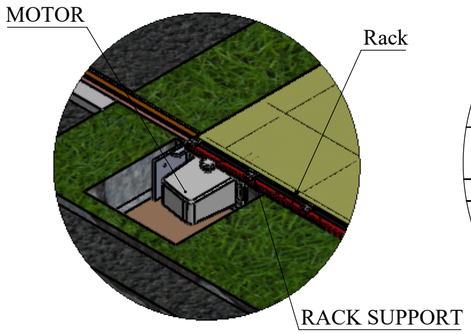


DETAIL A
SCALE 1 : 20

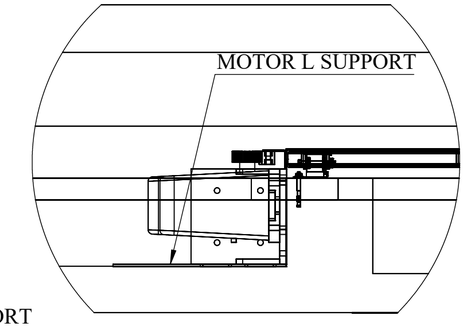

DETAIL B
SCALE 1 : 10

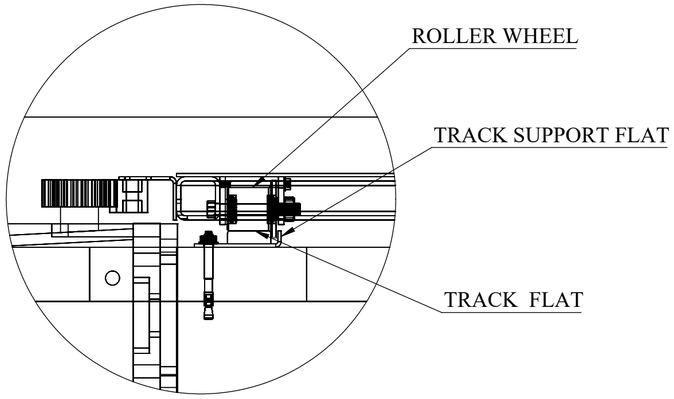

DETAIL C
SCALE 1 : 4

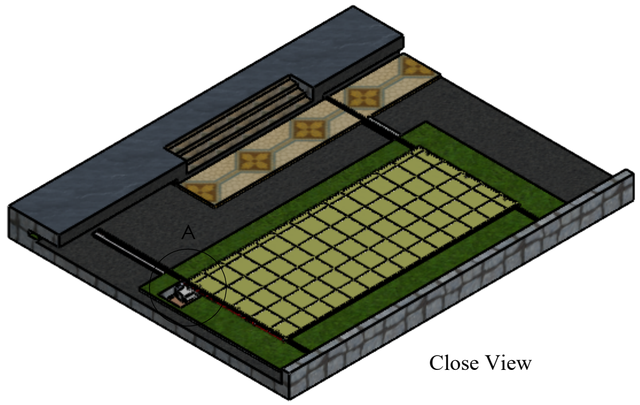

Close View

REV DESCRIPTION	DATE	REV NO
		REV 00
1.		REV 01

NOTE :

GA Drawing
Keep track clean before the panel movement.

SPECIAL INSTRUCTION'S :

TITLE - SWIMMING POOL ENCLOSER				NIHVA Technologies Pvt. Ltd.	NIHVA TECHNOLOGIES PVT.LTD.PUNE Website - www.nihva.com
DWG NO - NTPL-000-PM-001					
	NAME	SIGNATURE	DATE	PRODUCT - SWIMMING POOL DECK	
DRAWN	V.W.		22-08-2025	PROJECT NO - NTPL-000-PM	REVISION - 0
CHK'D	P.M.		23-08-2025	SITE LOCATION - PUNE	WEIGHT -
APPV'D	V.T.		23-08-2025	MATRIAL -	QTY - 1
If any queries contact - design@nihva.com				PROJECTION METHOD:	SCALE :
ALL DIMENSION ARE IN mm			A2		SHEET 1 OF 2