


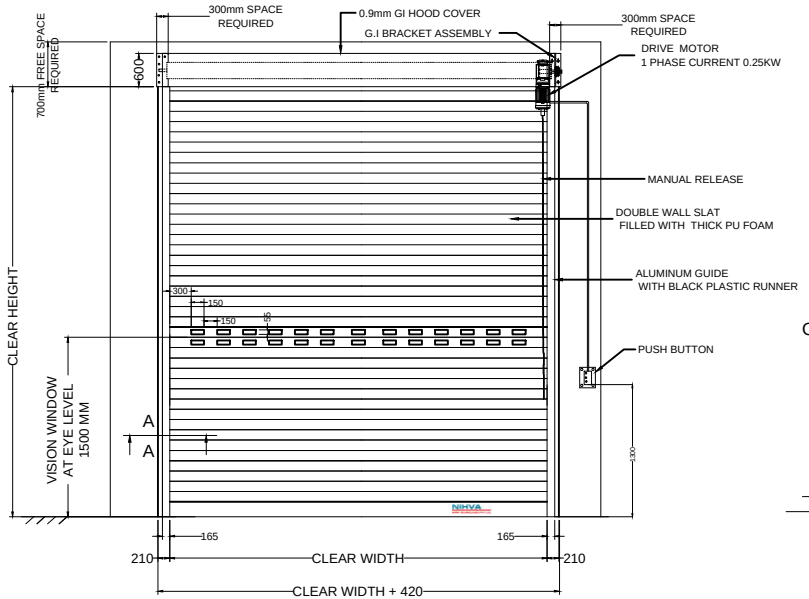


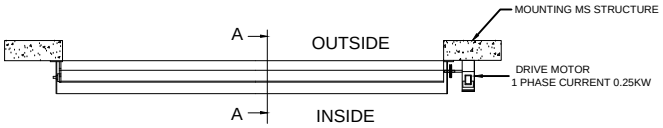


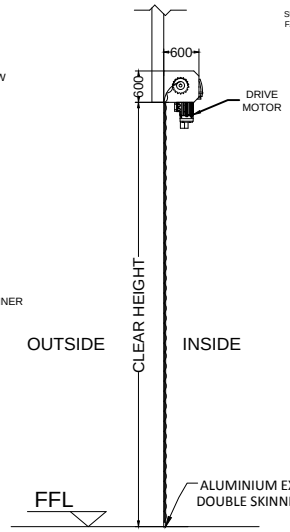

Section A-A

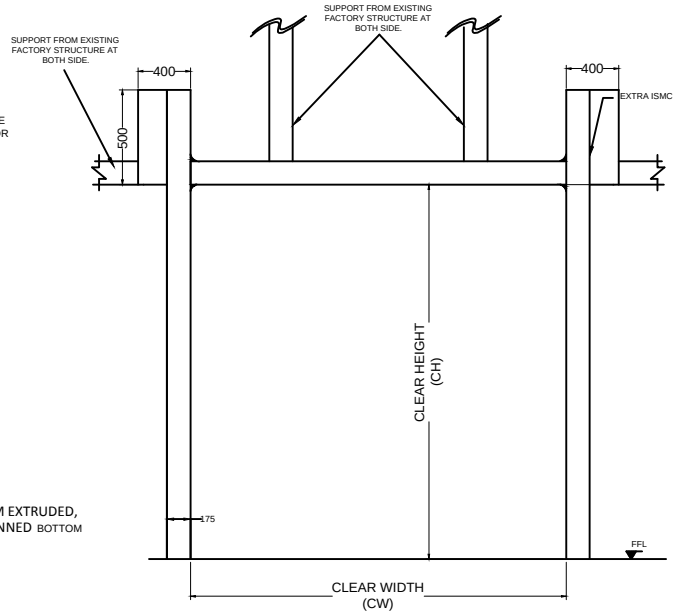


STRUCTURE

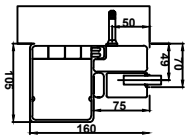

SECTION DETAIL

MAIN SLATS
DOUBLE WALL ROLLING SHUTTER



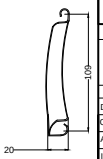

CLIENT SCOPE

1) 16A 3 PIN INDUSTRIAL TYPE FEMALE SOCKET 230V, 50HZ, WITH EARTH AROUND 1/2 METER FROM CONTROLLER/OPERATOR.
2) ALL CIVIL WORK WILL BE CLIENT'S SCOPE.
3) TECHNICAL MS STRUCTURE REQUIRED FOR SHUTTER IS IN CLIENT'S SCOPE.

STANDARD COLOR OF SLATS & SHUTTER -RAL9002 (GRAY WHITE)

CLEAR WIDTH	CLEAR HEIGHT	QUANTITY
5000 mm	3560mm	1 NO

REV NO	DATE	DRAWN	REMARK
R01	09.10.2020	P.A	1. CLEAR HEIGHT CHANGE.

NOTE : DOOR TO BE FIXED FROM INSIDE ONLY

This drawing & design is the property of NIHVA TECHNOLOGIES. Not to be sold or copied to any other concern.

TITLE: DOUBLE WALL ROLLING SHUTTER

NIHVA TECHNOLOGIES PVT. LTD.
NIHVA TECHNOLOGIES PVT. LTD. PUNE
Tel : 020 66304033
Email:- info@nihva.com
Website:- www.nihva.com

	NAME	SIGN	DATE
DRAWN	S.S.		6.10.2020
CHECK	P.A		6.10.2020
APPRD.			

CLIENT - M A ENGINEERING
PROJECT - JOHN DEERE INDIA PVT LTD
SITE LOCATION - PUNE
If any queries contact : projectsupport @nihva.com
DWG. NO. : NIHVA/20-21/0058/R01 REV- R01
ALL DIMENSION ARE IN mm
SCALE: NTS WT: SHEET: