


DRAWING

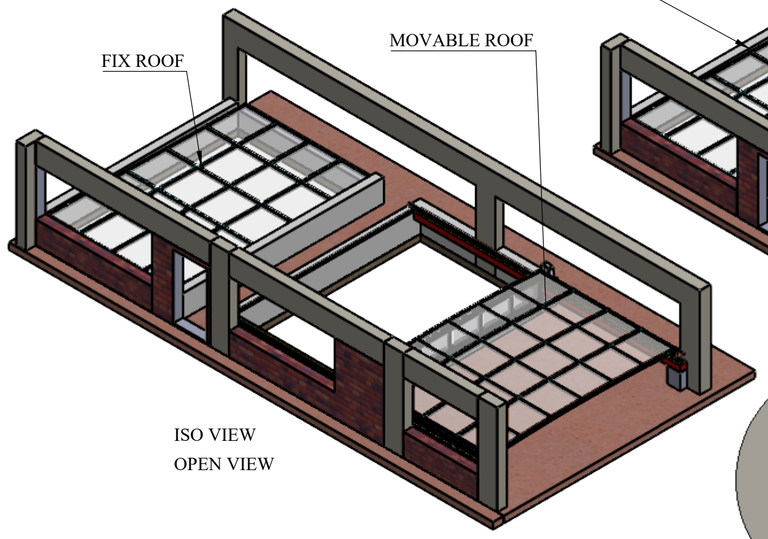


ISO VIEW
OPEN VIEW

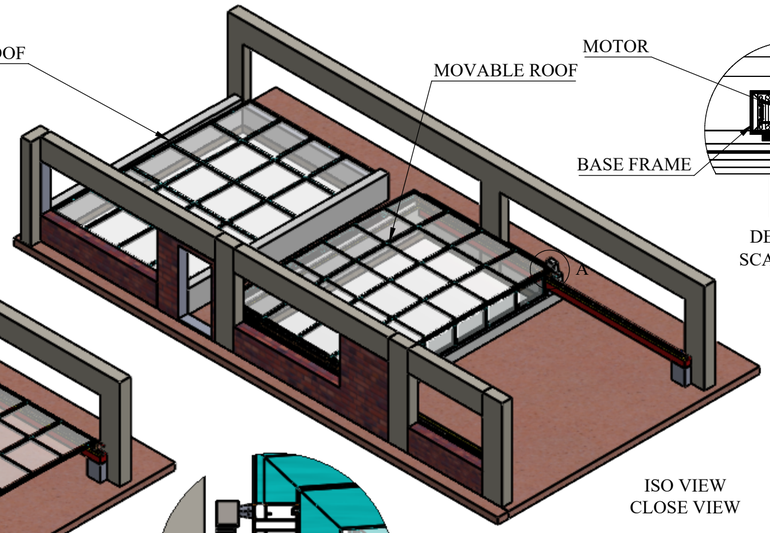


ISO VIEW
CLOSE VIEW

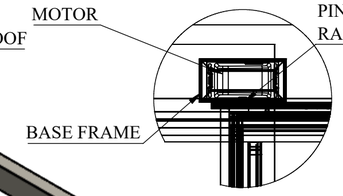


DETAIL B
SCALE 1 : 20

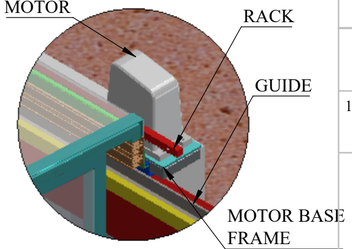

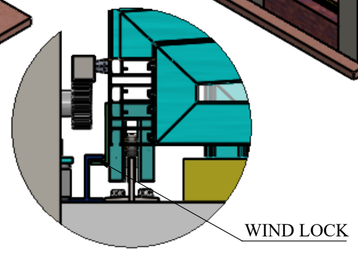


DETAIL D
SCALE 1 : 6

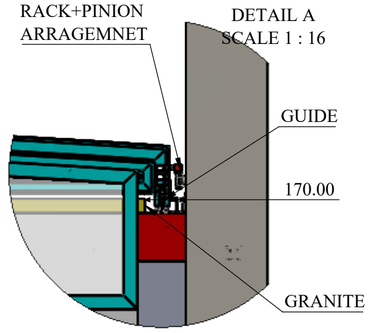


DETAIL A
SCALE 1 : 16

DETAIL C
SCALE 1 : 18

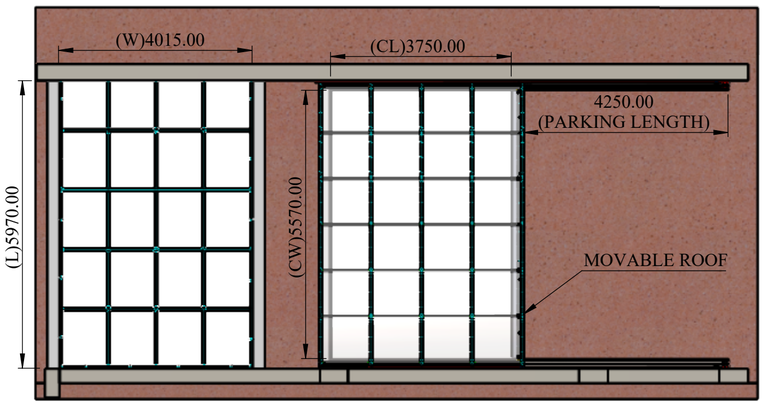


FIX ROOF


T.V.

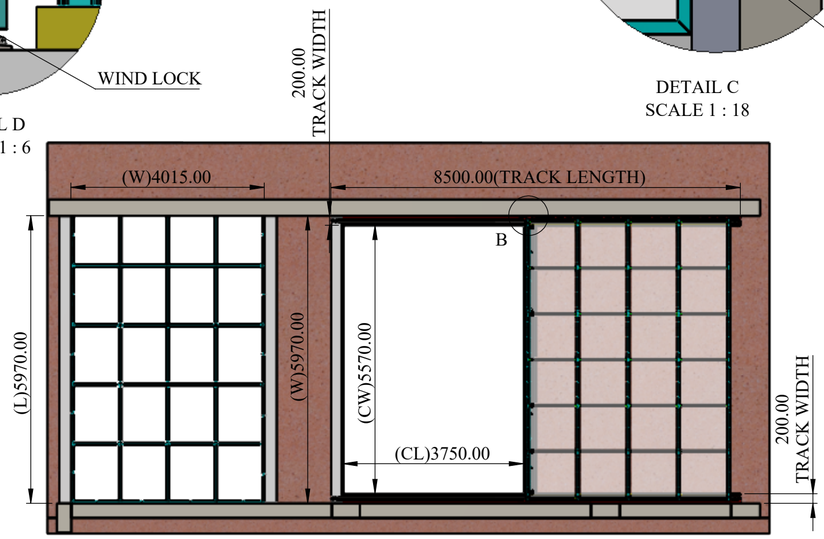

T.V.

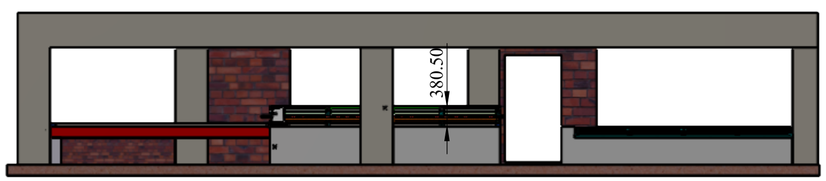

S.V.

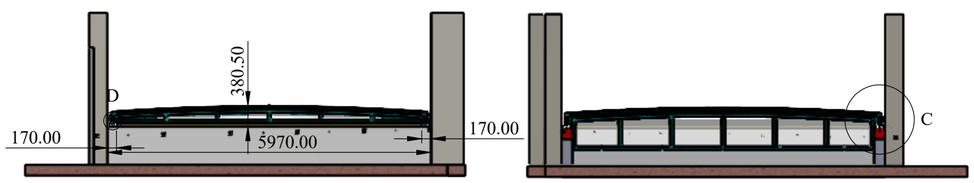

F.V.

B.V.

REV DESCRIPTION	DATE	REV NO
	24-09-2026	REV 00
1.		

NOTE :

GA DRAWING:
THIS DRAWING IS ONLY FOR CLIENT APPROVAL.
FIX ROOF WEIGHT - 600 KG.
RECTRACTABLE ROOF SYSTEM WEIGHT - 800KG.

SPECIAL INSTRUCTION'S :

This drawing & design is the property of NIHVA TECHONOLOGIES PVT. LTD. Not to be sold or copied to any other concern

TITLE - ROOF AUTOMATION

DWG NO - NTPL-

NIHVA Technologies Pvt. Ltd.


NIHVA TECHNOLOGIES PVT.LTD.PUNE
Website - www.nihva.com


	NAME	SIGNATURE	DATE
DRAWN	V.W.		24-09-2026
CHK'D	S.P.		25-09-2026
APPV'D	V.T.		25-09-2026

PRODUCT - RECTRACTABLE ROOF
CLIENT NAME - DR.NIKAM.
SITE LOCATION - KARAD.
MATRIAL -
QTY - 1


If any queries contact - info@nihva.com
ALL DIMENSION ARE IN mm
A2
PROJECTION METHOD:
SCALE :
SHEET 1 OF 2


DRAWING

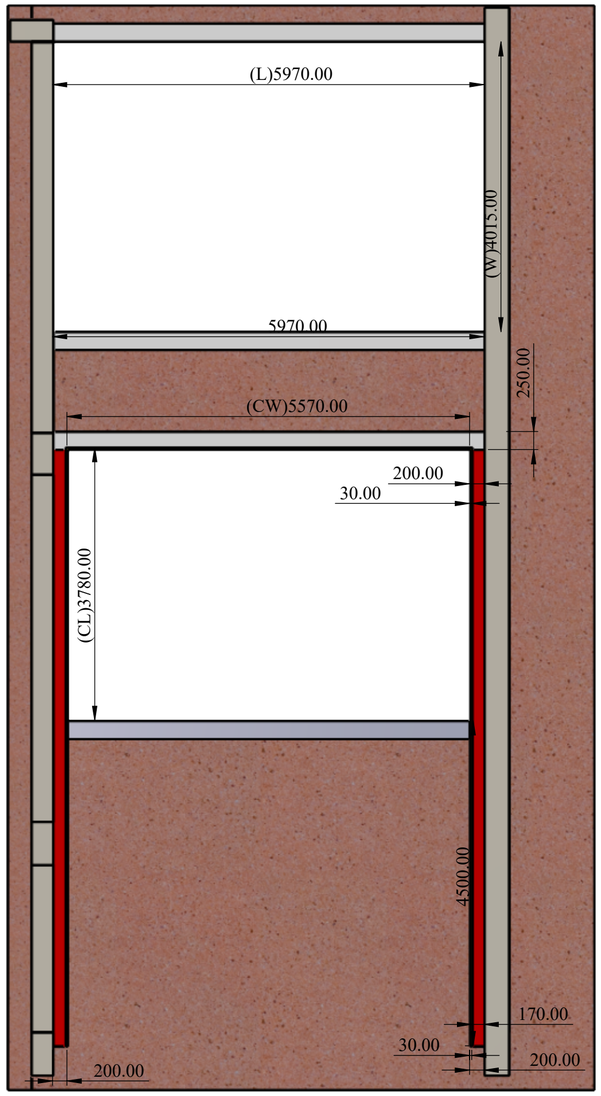

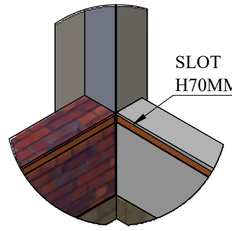


DETAIL G
SCALE 1 : 30

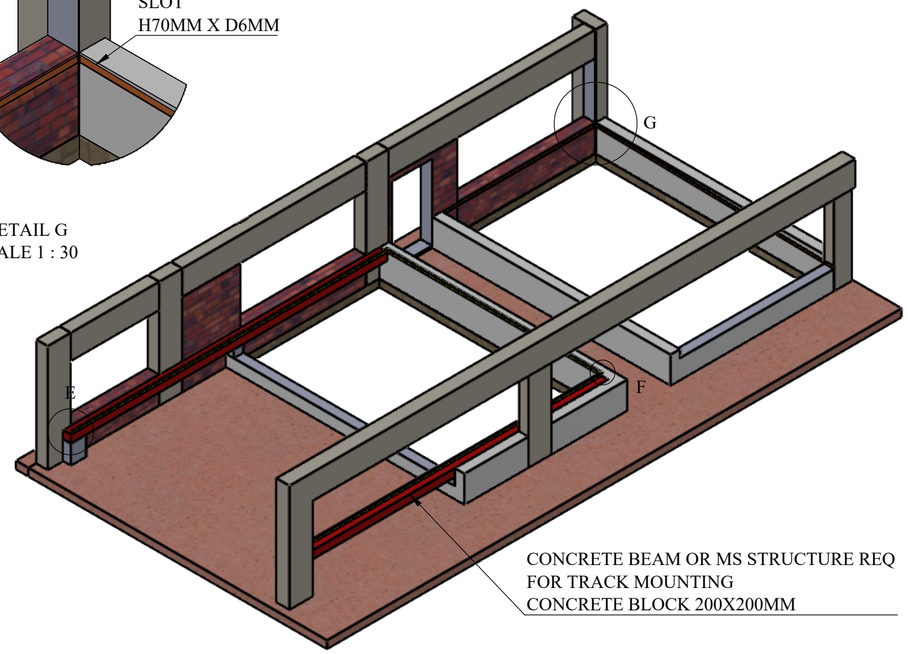


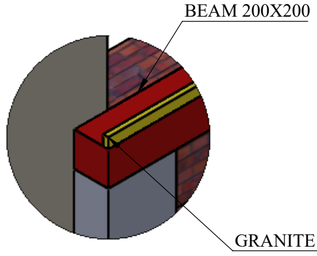


DETAIL E
SCALE 1 : 18

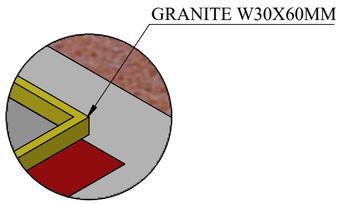

DETAIL F
SCALE 1 : 12

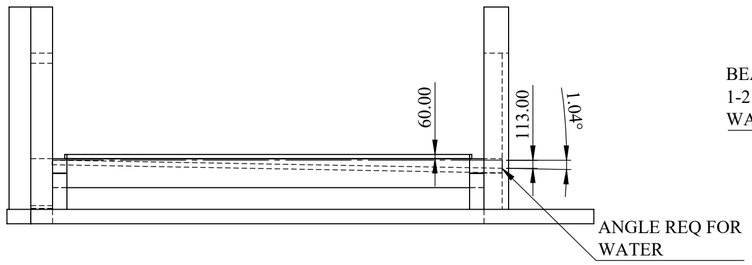

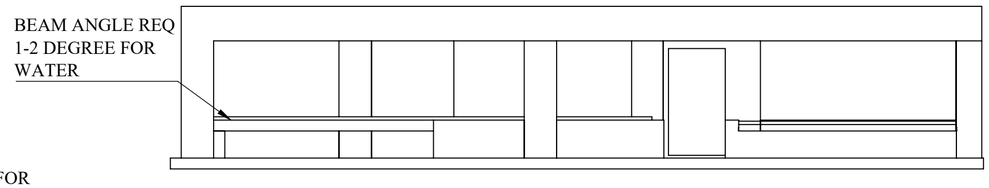

REV DESCRIPTION	DATE	REV NO
	24-09-2026	REV 00
1.		

NOTE :

CIVIL DRAWING:
BASE STRUCTURE IN CLIENT SCOPE.
CONCRETE BEAM 200X200 REQ BOTH SIDE FOR TRACK MOUNTING.
GRANITE STRIP 30X60 REQUIRED FOR WATER RESTRICATION ALL SIDES

SPECIAL INSTRUCTION'S :

This drawing & design is the property of NIHVA TECHONOLOGIES PVT. LTD. Not to be sold or copied to any other concern

TITLE - ROOF AUTOMATION

DWG NO - NTPL-

NIHVA Technologies Pvt. Ltd.

NIHVA TECHNOLOGIES PVT.LTD.PUNE
Website - www.nihva.com

	NAME	SIGNATURE	DATE
DRAWN	V.W.		24-09-2026
CHK'D	S.P.		25-09-2026
APPV'D	V.T.		25-09-2026

PRODUCT - RECTRACTABLE ROOF
CLIENT NAME - DR.NIKAM.
SITE LOCATION - KARAD.
MATRIAL -
QTY - 1
If any queries contact - info@nihva.com
ALL DIMENSION ARE IN mm
A2
PROJECTION METHOD:
SCALE :
SHEET 2 OF 2