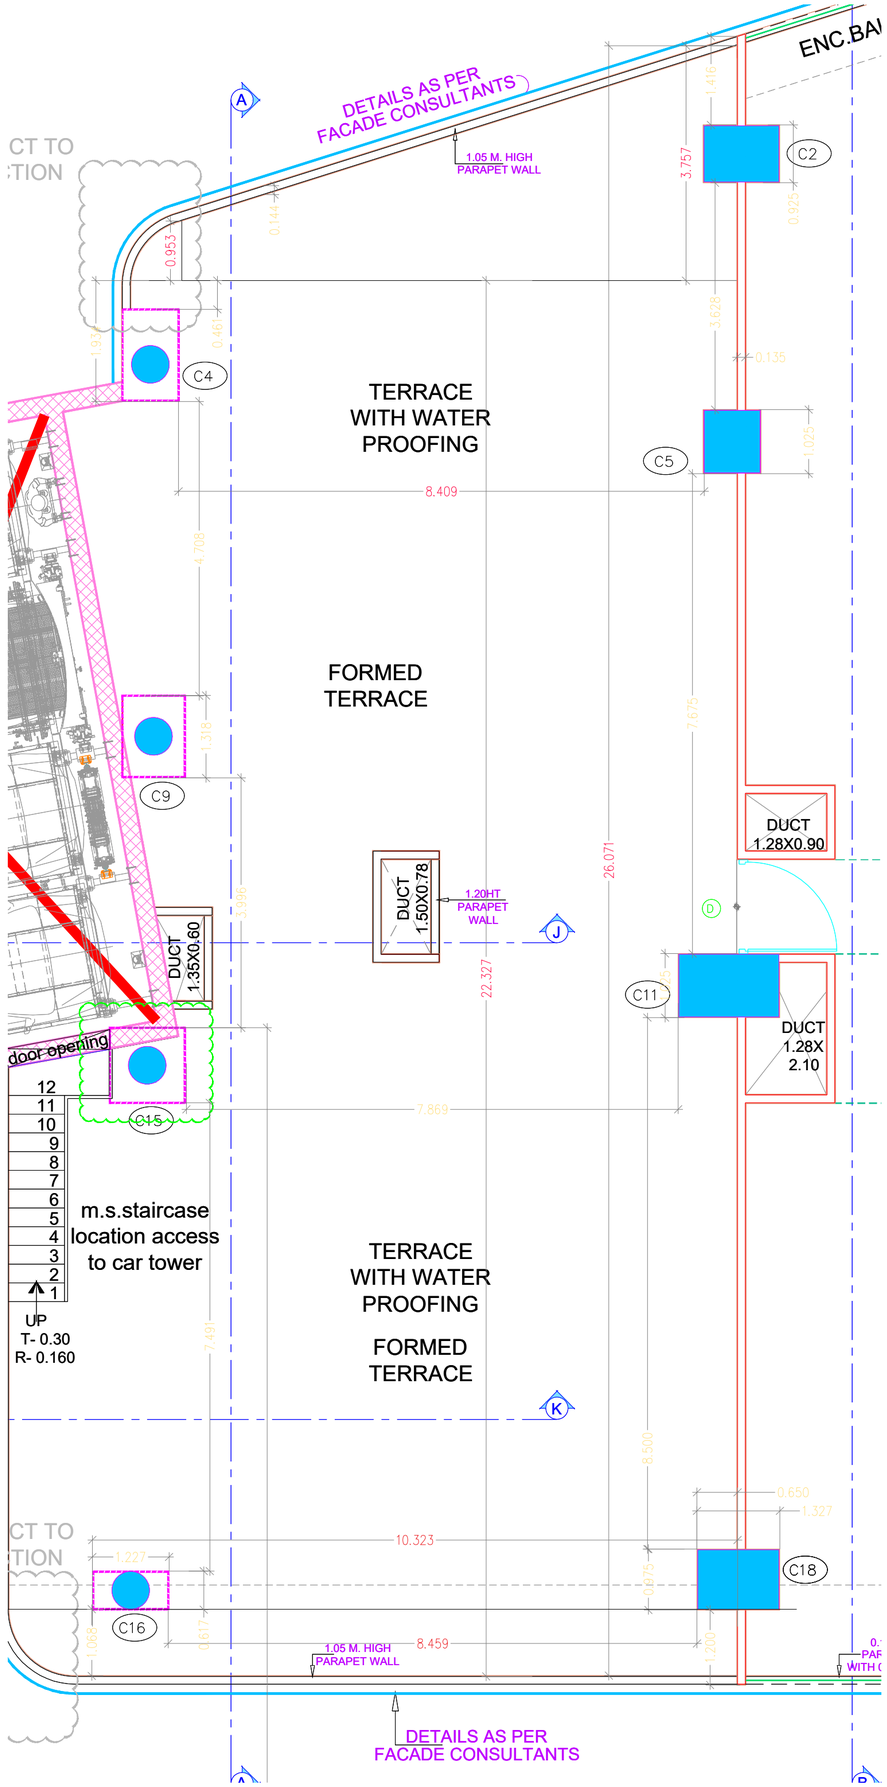

ENC.BA
DETAILS AS PER
FACADE CONSULTANTS
1.05 M. HIGH
PARAPET WALL
A
C2
C4
C5
C9
C15
C16
C18
C11
TERRACE
WITH WATER
PROOFING
FORMED
TERRACE
DUCT
1.28X0.90
DUCT
1.50X0.78
1.20HT
PARAPET
WALL
DUCT
1.35X0.60
DUCT
1.28X
2.10
door opening
m.s.staircase
location access
to car tower
UP
T- 0.30
R- 0.160
J
K
D
8.409
7.869
10.323
8.459
26.071
22.327
7.491
7.675
8.500
3.757
3.628
1.416
0.953
0.144
0.461
0.135
1.025
0.925
4.708
1.318
3.996
0.650
1.327
1.227
0.617
1.068
1.200
DETAILS AS PER
FACADE CONSULTANTS