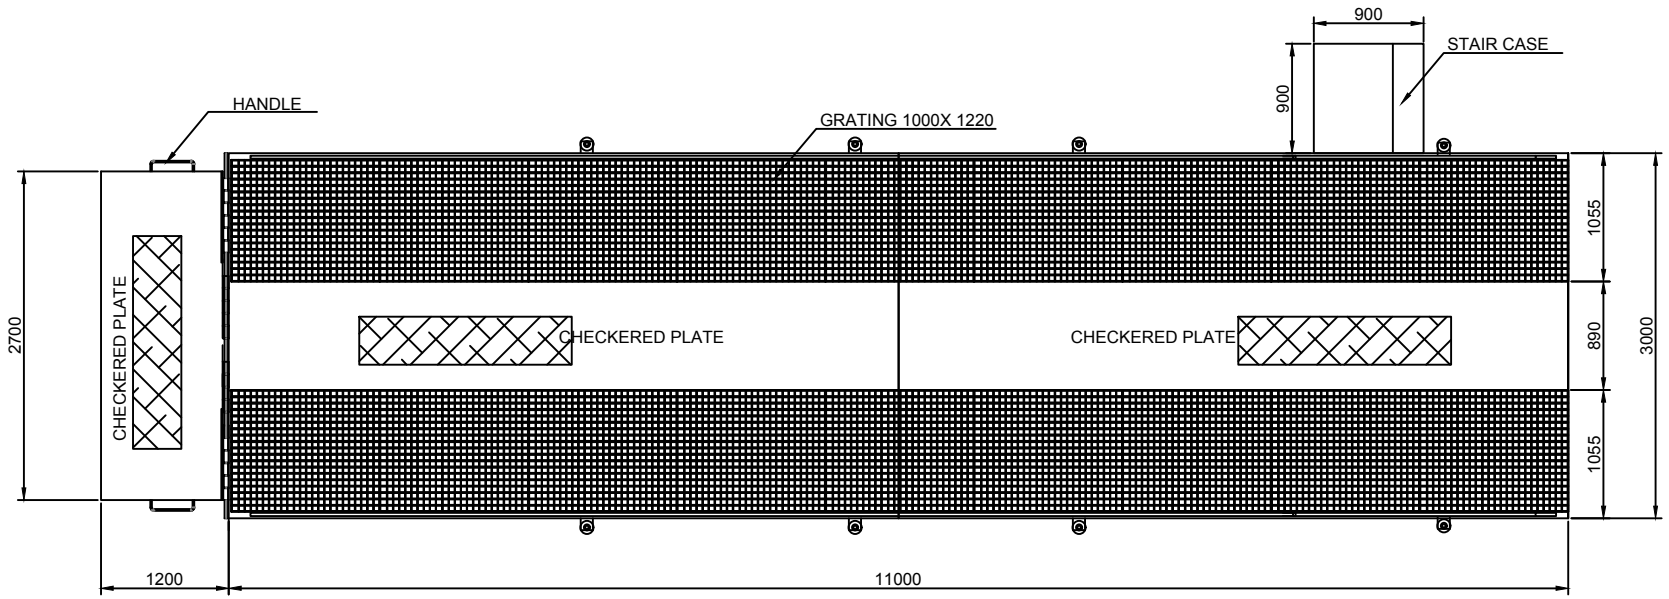
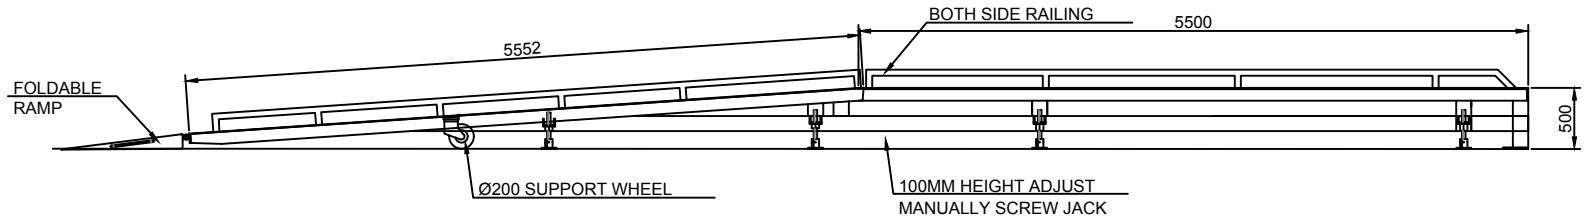



| SR.NO | WIDTH (W) | LENGTH ( L) | HEIGHT (H) | CAPACITY |
|---|---|---|---|---|
| 1 | 3000 | 11000 | 500 | 10 Ton |
| 2 | | | | |
| 3 | | | | |
| 4 | | | | |
| 5 | | | | |

NOTE:-

1. ALL DIMENSIONS ARE IN MM
2. THES DRAWING IS FOR UNDERSTANDING PURPOSE
3. WHEEL ONLY MOVEMENT PURPOSE
4. ALL LOAD ON SCREW JACK

This drawing & design is the property of NIHVA TECHNOLOGIES. Not to be sold or copied to any other concern.

TITLE:- GA DRAWING
MANUALLY DOCK RAMP

NIHVA
NIHVA TECHNOLOGIES PVT. LTD.

NIHVA TECHNOLOGIES
PVT. LTD. PUNE
Tel : 020 66304033
Email:- info@nihva.com
Website:- www.nihva.com

| | NAME | DATE | SIGN |
|---|---|---|---|
| DRAWN | BB | 29.08.24 | |
| CHECK | BB | 29.08.24 | |
| APPRD. | VT | 29.08.24 | |

If any queries contact : design@nihva.com

ALL DIMENSION ARE IN mm

CLIENT - FERRERO INDIA PVT LTD
LOCATION - BARAMATI
PRODUCT - MANUALLY DOCK RAMP
DWG NO:-NIHVA/24-25/00XX | REV- 0
SCALE: NTS | SCALE:-- 1:1 | SHEET: 01 OF 01