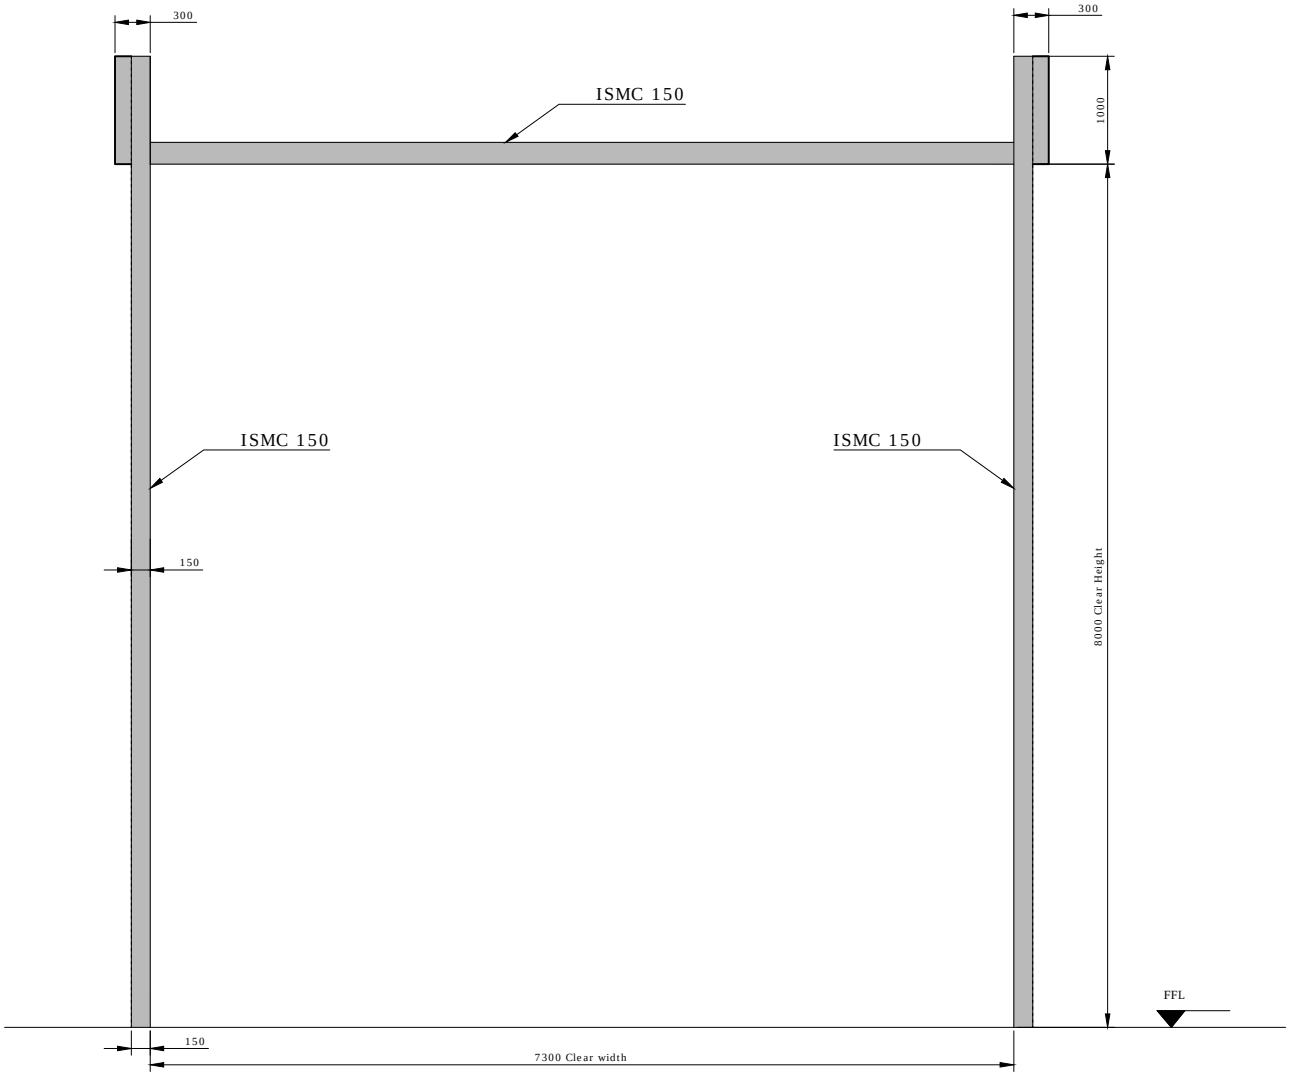


INSIDE ELEVATION

NOTE-
1. IF RCC LINTEL FOR MS BRACKET & WALL FOR MS GUIDE IS AVAILABLE AT SITE THEN NO NEED OF MS STRUCTURE.
2. REQUIRED STRUCTURE FOR ROLLING SHUTTER WILL BE CLIENT'S SCOPE.

CLEAR WIDTH (CW)	CLEAR HEIGHT (CH)	QUANTITY
7300	8000	1

This drawing & designing is the property of NIHVA TECHNOLOGIES. Not to be sold or copied to any other concern.

TITLE
MOTORIZED ROLLING SHUTTER STRUCTURE.

	SIGN	DATE
DRAWN	SURAJ	14/09/17
CHECK	SAGAR	14/09/17
APPROVAL	SHEKHAR	14/09/17
REV.		

If any queries contact : projects@nihva.com

ALL DIMENSION ARE IN mm

NIHVA TECHNOLOGIES PVT. LTD.
NIHVA TECHNOLOGIES PVT. LTD. PUNE
Tel : 020 66304033
Email:- info@nihva.com
Website:- www.nihva.com

CLIENT -S.S.GHORPADE
PROJECT -ROSS PROCESS EQUIPMENT PVT. LTD.
SITE -CHAKAN
DWG. NO. : NIHVA/17-18/0204
SCALE: NTS | WT: | SHEET: 01 OF 01