


PRODUCED BY AN AUTODESK EDUCATIONAL PRODUCT


THIS DRAWING & DESIGNING IS THE PROPERTY OF TECHNOCRATS SECURITY SYSTEMS PVT. LTD. AND MUST NOT BE COPIED OR LENT WITHOUT THEIR PERMISSION IN WRITING.

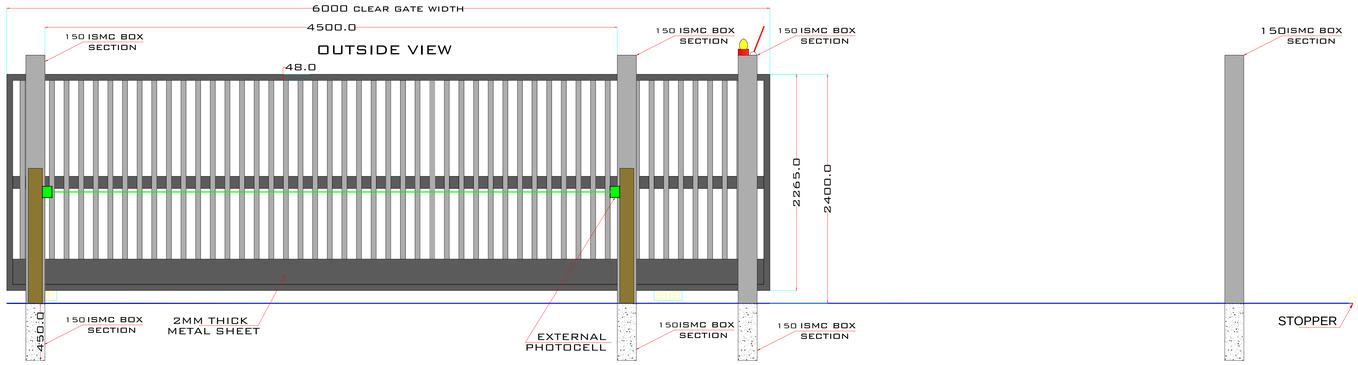


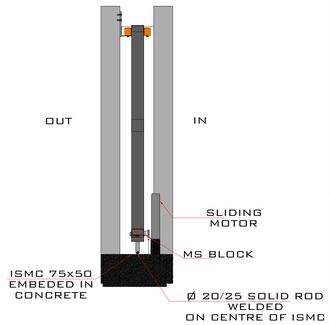

CROSS SECTION

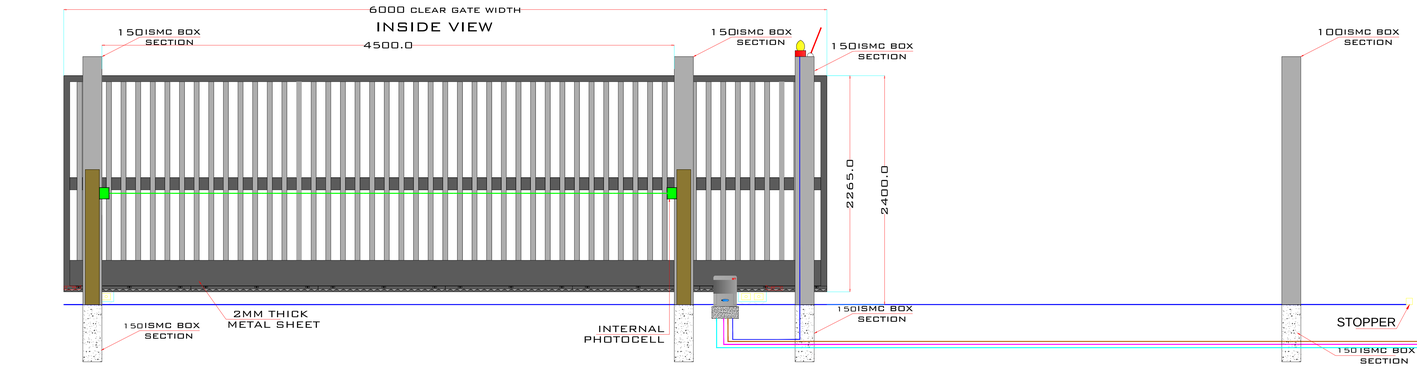

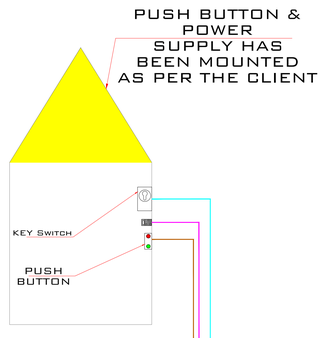

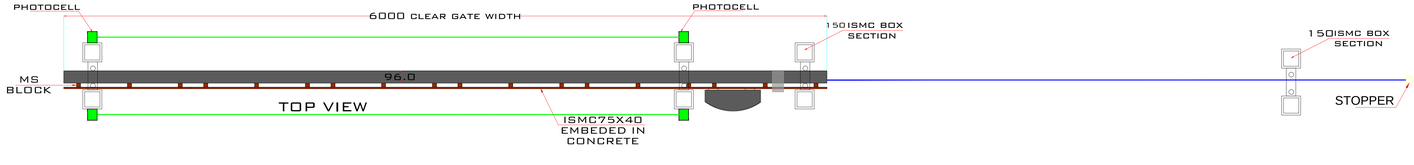

NOTE:-

LEGEND:-

WIRES	DESCRIPTION	SUPPLY
	MOTOR TO SUPPLY	3 C x 1.5 SQ.MM(UN-ARMOURED, NON-SHIELDED, ISI APPROVED FLEXIBLE CABLE THROUGH GI CONDUIT.
	PHOTOCELL TO MOTOR	4 C x 1 SQ.MM (UN-ARMOURED, NON-SHIELDED, ISI APPROVED FLEXIBLE CABLE THROUGH GI CONDUIT.
	KEYSWITCH TO MOTOR	
	MOTOR TO PUSH BUTTON	
	FLASHING LIGHT TO MOTOR	

PRODUCT DETAILS :-

SR.NO	DESCRIPTIONS	QTY
	SLIDING MOTOR	01
	230V/5AMP	01
	PUSH BUTTON	01
	KEY SWITCH	01

R 0	1. ATTENDANCE PURPOSE READER SHIFTED TO TS4 -P-D01	17.12.09

Released For :

Tender ☐ Approval ☐ Construction ☐ As built ☐

OWNERS :

PROJECT MANAGEMENT CONSULTANT :

SERVICE CONSULTANT :

ARCHITECTS :

TECHNOCRATS SECURITY SYSTEM PVT.LTD
Unit C-2, Modal Industrial Colony, Vishweshwar Nagar , Road No.2,
Off. Aarey Road, Goregaon (E), Mumbai 63. E mail : design@technocrat.asia

PROJECT : THE TATA POWER COMPANY
OFFICE BUILDING
B-12,13,SECTOR 4
NOIDA 201301

DRAWING TITLE :

SLIDING GATE WIRING DWGS

JOB No.	DRG.NO.	REV.
------	------	0.1

SCALE:	DATE:	DRAWN:	CHKD :	APPVD:
NTS	28/05/2014	JACOB	SANJAY	------


D:\AUTOMATION PROJECT 2013\SLIDING GATES\TATA\New folder\SLIDING AND SWING GATE rev 6.dwg, Layout1, 23-Jul-14 12:49:48 PM, Siva, DWG To PDF.pc3, Previous paper size (1189.00 x 841.00 MM), 1:263.612


PRODUCED BY AN AUTODESK EDUCATIONAL PRODUCT


PRODUCED BY AN AUTODESK EDUCATIONAL PRODUCT

THIS DRAWING & DESIGNING IS THE PROPERTY OF TECHNOCRATS SECURITY SYSTEMS PVT. LTD. AND MUST NOT BE COPIED OR LENT WITHOUT THEIR PERMISSION IN WRITING.

SLIDING GATE DETAILS

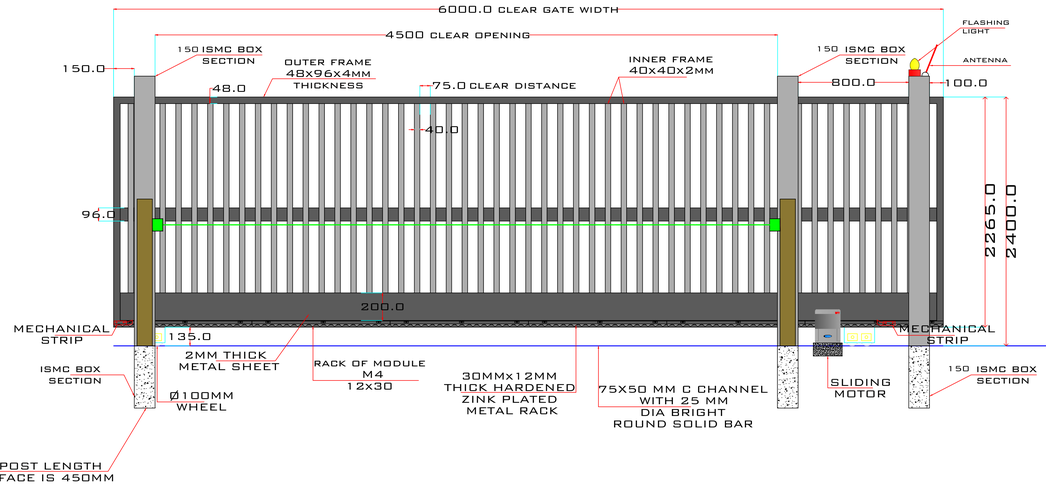


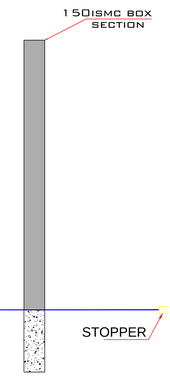


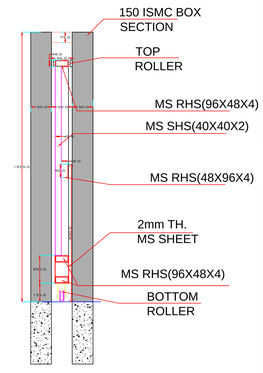

SLIDING TOP RAIL DETAIL

SLIDING ROLLER DETAIL `A'

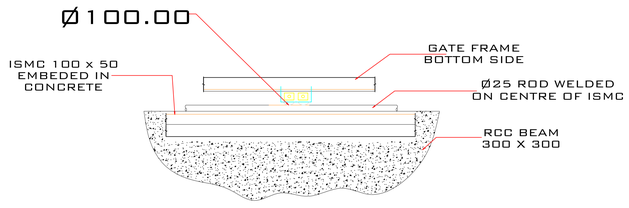


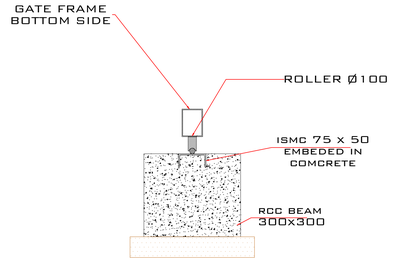

OPENING AND CLOSING GATE OF SPEED (9M/MIN)

MOTOR DETAIL

MOTOR CAN PULL 1500KG GATE

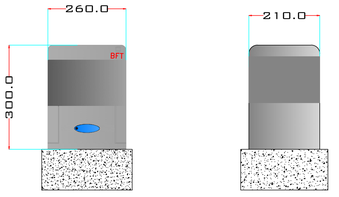

FRONT VIEW

CROSS SECTION

NOTE:-

PRODUCT DETAILS :-

SR.NO	DESCRIPTIONS	DATE
R 0	1. ATTENDANCE PURPOSE READER SHIFTED TO TS4 -P-D01	17.12.09

Released For :

Tender ☐	Approval ☐	Construction ☐	As built ☐

OWNERS :

PROJECT MANAGEMENT CONSULTANT :

SERVICE CONSULTANT :

ARCHITECTS :

TECHNOCRATS SECURITY SYSTEM PVT.LTD
Unit C-2, Modal Industrial Colony, Vishweshwar Nagar , Road No.2, Off. Aarey Road, Goregaon (E), Mumbai 63. E mail : design@technocrat.asia

PROJECT : THE TATA POWER COMPANY
OFFICE BUILDING
B-12,13,SECTOR 4
NOIDA 201301

DRAWING TITLE :
SLIDING GATE DETAILS


JOB No.	DRG.NO.	REV.
------	------	

SCALE:	DATE:	DRAWN:	CHKD :	APPVD:
NTS	28/05/2014	JACOB	SANJAY	------


D:\AUTOMATION PROJECT 2013\SLIDING GATES\TATA\New folder\SLIDING AND SWING GATE rev 6.dwg, Layout2, 23-Jul-14 12:49:57 PM, Siva, DWG To PDF.pc3, Previous paper size (1189.00 x 841.00 MM), 1:263.612

PRODUCED BY AN AUTODESK EDUCATIONAL PRODUCT

SWING GATE

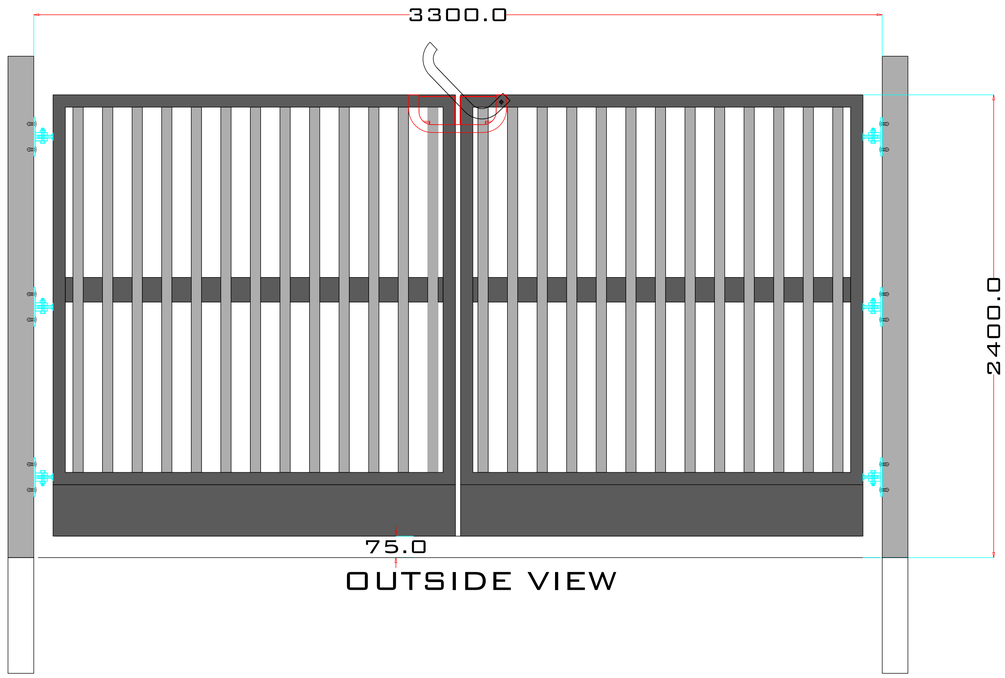

OUTSIDE VIEW

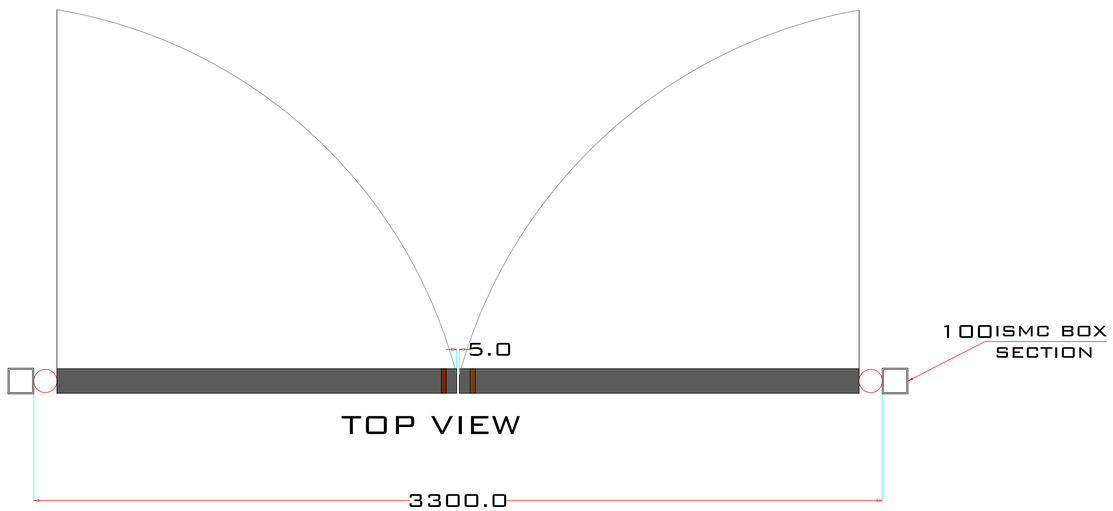

TOP VIEW

NOTE:-

PRODUCT DETAILS :-

SR.NO	DESCRIPTIONS	DATE
R 0	1. ATTENDANCE PURPOSE READER SHIFTED TO TS4 -P-D01	17.12.09

Released For :

Tender ☐	Approval ☐	Construction ☐	As built ☐

OWNERS :

PROJECT MANAGEMENT CONSULTANT :

SERVICE CONSULTANT :

ARCHITECTS :

TECHNOCRATS SECURITY SYSTEM PVT.LTD
Unit C-2, Modal Industrial Colony, Vishweshwar Nagar , Road No.2,
Off. Aarey Road, Goregaon (E), Mumbai 63. E mail : design@technocrat.asia

PROJECT : THE TATA POWER COMPANY
OFFICE BUILDING
B-12,13,SECTOR 4
NOIDA 201301

DRAWING TITLE :
SWING GATE

JOB No.	DRG.NO.	REV.
------	------	

SCALE:	DATE:	DRAWN:	CHKD :	APPVD:
NTS	28/05/2014	JACOB	SANJAY	------

THIS DRAWING & DESIGNING IS THE PROPERTY OF TECHNOCRATS SECURITY SYSTEMS PVT. LTD. AND MUST NOT BE COPIED OR LENT WITHOUT THEIR PERMISSION IN WRITING.

D:\AUTOMATION PROJECT 2013\SLIDING GATES\TATA\New folder\SLIDING AND SWING GATE rev 6.dwg, Layout3, 23-Jul-14 12:50:02 PM, Siva, DWG To PDF.pc3, Previous paper size (1189.00 x 841.00 MM), 1:263.612

PRODUCED BY AN AUTODESK EDUCATIONAL PRODUCT

THIS DRAWING & DESIGNING IS THE PROPERTY OF TECHNOCRATS SECURITY SYSTEMS PVT. LTD. AND MUST NOT BE COPIED OR LENT WITHOUT THEIR PERMISSION IN WRITING.

SWING GATE DETAILS

DETAIL 4

3300.0CLEAR OPENING

INSIDE VIEW

OUTER FRAME
48x96x4MM
THICKNESS

75.0CLEAR DISTANCE

INNER FRAME
40x40x2MM

ISMC BOX
SECTION

DETAIL 3

50.0

75MM
HINGE'S

100ISMC BOX
SECTION

2400.0

200.0

75.0

2MM THICK
METAL SHEET

LOCK

DETAIL 1A

DETAIL 2

ISMC BOX
SECTION

100ISMC BOX
SECTION

DETAIL 1

VERTICAL POST LENGTH
BELOW SURFACE IS 450MM

NOTE:-

SR.NO	DESCRIPTIONS	DATE
R 0	1. ATTENDANCE PURPOSE READER SHIFTED TO TS4 -P-D01	17.12.09

PRODUCT DETAILS :-

Released For :

Tender ☐	Approval ☐	Construction ☐	As built ☐

OWNERS :

PROJECT MANAGEMENT CONSULTANT :

SERVICE CONSULTANT :

ARCHITECTS :

TECHNOCRATS SECURITY SYSTEM PVT.LTD
Unit C-2, Modal Industrial Colony, Vishweshwar Nagar , Road No.2,
Off. Aarey Road, Goregaon (E), Mumbai 63. E mail : design@technocrat.asia

PROJECT :
THE TATA POWER COMPANY
OFFICE BUILDING
B-12,13,SECTOR 4
NOIDA 201301


DRAWING TITLE :
SWING GATE DETAILS

JOB No.	DRG.NO.	REV.
------	------	


SCALE:	DATE:	DRAWN:	CHKD :	APPVD:
NTS	28/05/2014	JACOB	SANJAY	------

D:\AUTOMATION PROJECT 2013\SLIDING GATES\TATA\New folder\SLIDING AND SWING GATE rev 6.dwg, Layout4, 23-Jul-14 12:50:07 PM, Siva, DWG To PDF.pc3, Previous paper size (1189.00 x 841.00 MM), 1:263.612


PRODUCED BY AN AUTODESK EDUCATIONAL PRODUCT

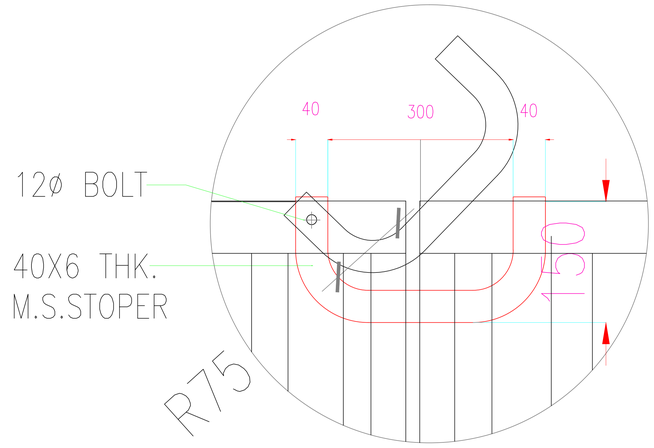


DETAIL - 4

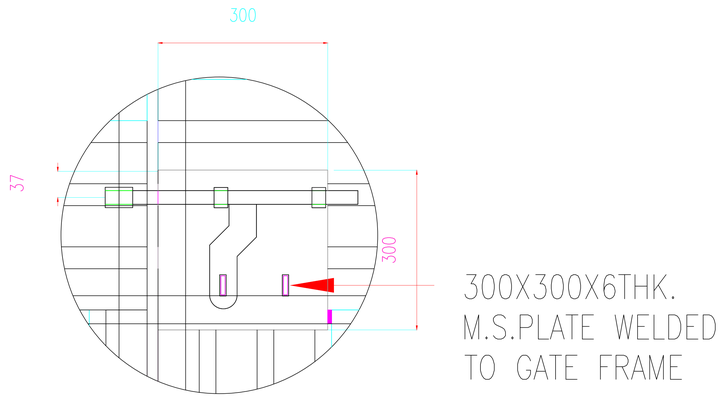


DETAIL - 3

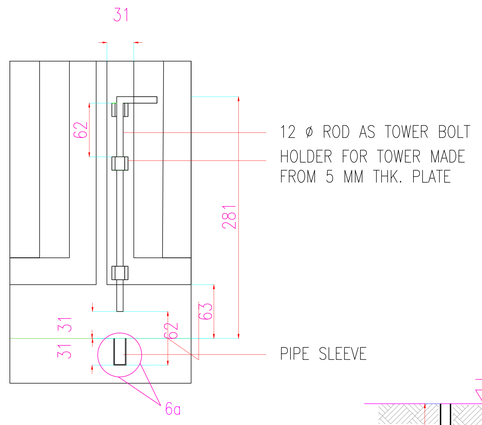

DETAIL - 1

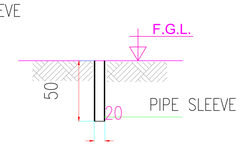

DETAIL - 1a

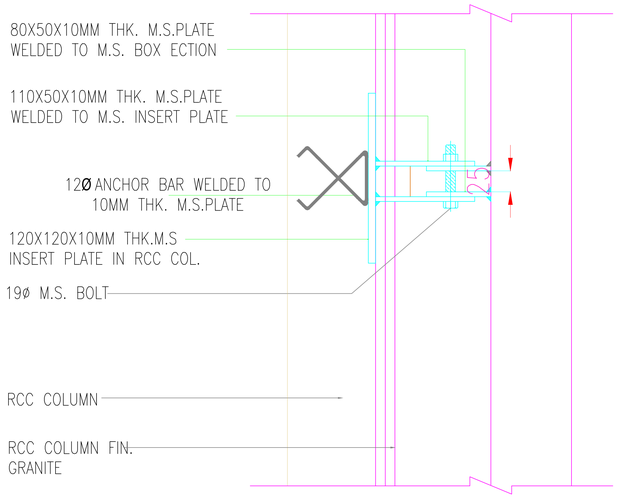

DETAIL - 2

NOTE:-

PRODUCT DETAILS :-

SR.NO	DESCRIPTIONS	DATE
R 0	1. ATTENDANCE PURPOSE READER SHIFTED TO TS4 -P-D01	17.12.09

Released For :

Tender ☐	Approval ☐	Construction ☐	As built ☐

OWNERS :

PROJECT MANAGEMENT CONSULTANT :

SERVICE CONSULTANT :

ARCHITECTS :

TECHNOCRATS SECURITY SYSTEM PVT.LTD
Unit C-2, Modal Industrial Colony, Vishweshwar Nagar , Road No.2,
Off. Aarey Road, Goregaon (E), Mumbai 63. E mail : design@technocrat.asia

PROJECT : THE TATA POWER COMPANY
OFFICE BUILDING
B-12,13,SECTOR 4
NOIDA 201301

DRAWING TITLE :

SWING GATE HINGE'S & LOCK DETAILS.1

JOB No.	DRG.NO.	REV.
------	------	

SCALE:	DATE:	DRAWN:	CHKD :	APPVD:
NTS	10/03/2014	JACOB	SANJAY	------

THIS DRAWING & DESIGNING IS THE PROPERTY OF TECHNOCRATS SECURITY SYSTEMS PVT. LTD. AND MUST NOT BE COPIED OR LENT WITHOUT THEIR PERMISSION IN WRITING.

D:\AUTOMATION PROJECT 2013\SLIDING GATES\TATA\New folder\SLIDING AND SWING GATE rev 6.dwg, Layout5, 23-Jul-14 12:50:12 PM, Siva, DWG To PDF.pc3, Previous paper size (1189.00 x 841.00 MM), 1:263.612