



Material Specifications on
Front Elevation of Entrance Gate

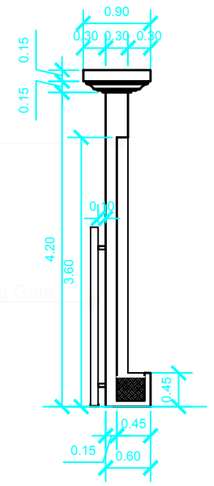

Section of
Entrance Gate

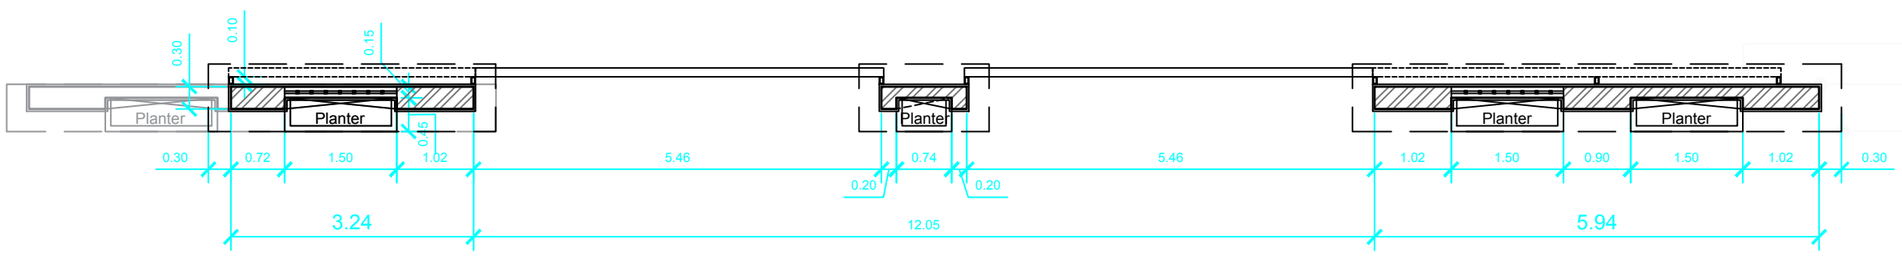

Material Specifications on
Plan of Entrance Gate

NOTES :

1. Do not scale the drawing.Work to figured dimensions only.
2. All dimensions are in metres(m) unless noted otherwise.
3. This drawing to be read in conjunction with all relevant contract drawings and documentation.
4. This drawing is to be carefully checked by contractor against architects drawings,and any discrepancy reported to the engineer before construction commences.

REVISIONS :

DATE	REVISIONS	DRAWN BY	UPDATE
29.02.24	R1	Ar. Amisha	Length reduced as per site conditions

ARCHITECT :
Epic designs pvt. ltd.

CLIENT : Highyield Fortune Pvt. Ltd.

DATE	Drawn By	Checked By	SCALE	Status
29.02.24	Ar. Amisha	Ar. Akshat		For Study

Drawing Name :
Entrance Wall Design

Drawing No. :

Project :
Foresta, Mulshi