


NOTE :- 1)All dimensions are in mm
2)Mat:-

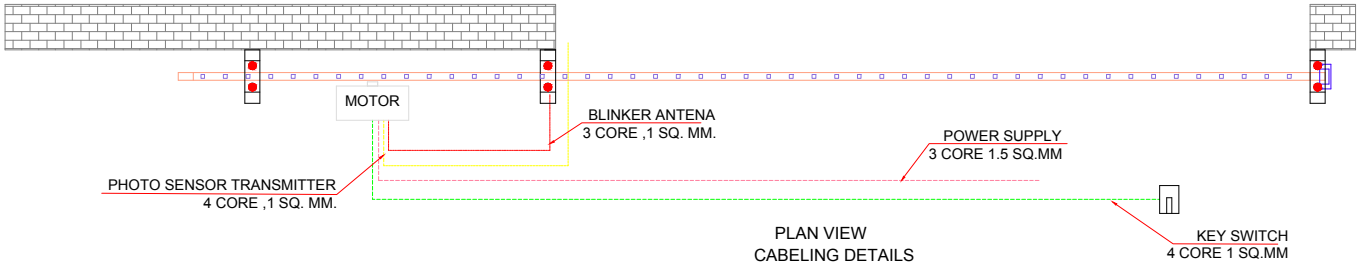


PLAN VIEW
CABELING DETAILS

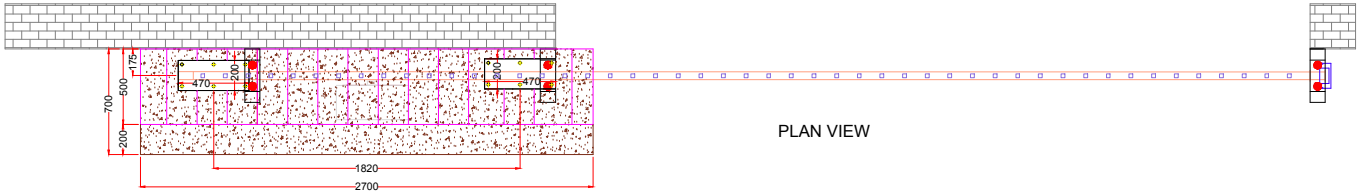

PLAN VIEW

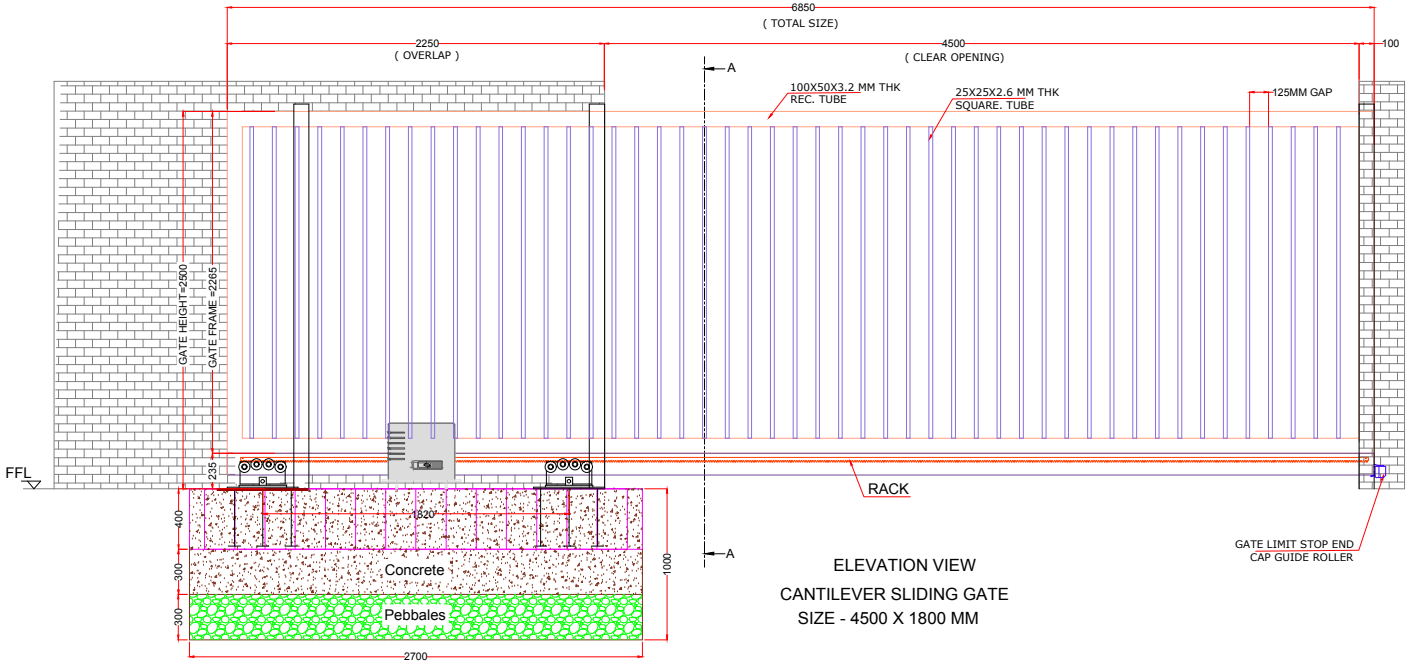

ELEVATION VIEW
CANTILEVER SLIDING GATE
SIZE - 4500 X 1800 MM

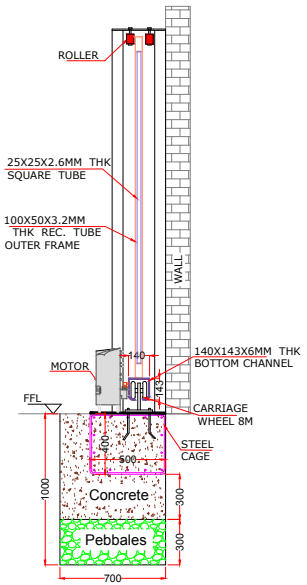

SECTION A-A

NOTE-:
1) All dimensions are in mm
2) Mat -MS
3) Cable details -

- 4 CORE , 0.5 SQ. MM. CABLE FOR PHOTOSENSOR
- 4 CORE , 1 SQ. MM. CABLE FOR KEY SWITCH
- 3 CORE , 1 SQ. MM. CABLE FOR POWER SUPPLY
- 3 CORE , 0.5 SQ. MM. CABLE FOR BLINKER & ANTENA

DRAWN	AKASH
CHECKED	
DATE	05/02/2020
QTY	

Nirmal Automation Pvt. Ltd.,
Pune-411038
www.nirmalautomation.com
nirmalautomation@gmail.com
020-65271490

DESCRIPTION:- CANTILEVER SLIDING GATE			
CLIENT:- NIHVA TECHNOLOGIES PVT LTD .			
DRAWING NO	NAPL-425-01-01	REVISION	01
WEIGHT		SCALE	